A2	PROSOIL	BOREHOLE NO: BH-1	
		LOCATION : Plot #53, Road #13, Block D, Banani, Dhaka.	
PROJECT : Proposed 10 (Ten) Storied Building.		DEPTH OF BORING: 18.0m	R. L.: On Road Level.
CLIENT : Building Technology & Ideas Ltd.		DATE OF BORING: 29-08-2010.	G. W. T : 2.43m below from E.G.L.

THICKNESS	SOIL STRATA	BORELOG	UNDISTURBED SAMPLE	DISTURBED SAMPLE	DEPTH (m) SPT VALUES (BLOWS / 300mm)	Grain Size Distribution, % Clay %, Silt %, Sand %	Max^{m} Penetration

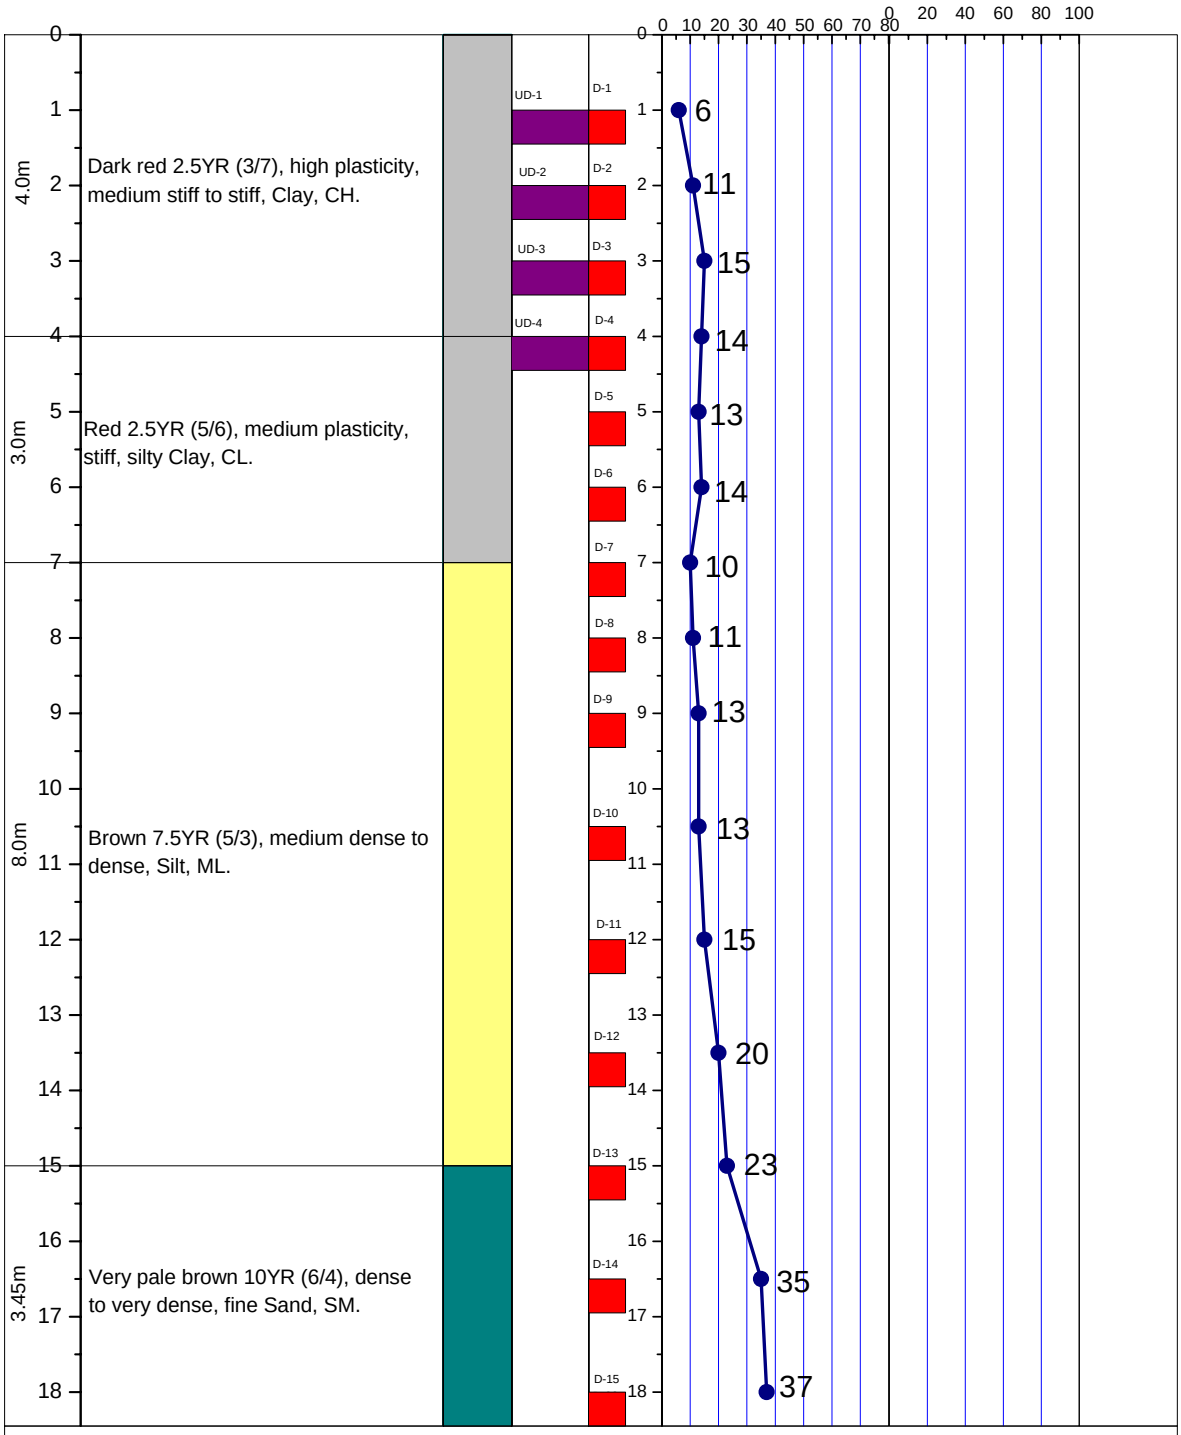

LEGEND FOR BORELOG AND GRAIN SIZE DISTRIBUTION (BASED ON 'ASTM CLASSIFICATION D-2487')

PLASTIC CLAY | SAND | SILT | SHALE

PEAT/HIGHLY ORGANIC SOIL | MICACEOUS FINE SAND/SILT | UNDISTURBED SAMPLE | DISTURBED SAMPLE

N- BLOWS DELIVERED PER FOOT BY A 140 LB HAMMER FALLING 30 INCHES

MAX^{m} PENETRATION= 50 BLOWS

AFTER 50 BLOWS PENETRATION DEPTH WERE MEASURED