A2	PROSOIL	BOREHOLE NO: BH-2	
		LOCATION : Gosaierhat,Damuday Thana, Shariatpur.	
PROJECT : CIRCLE ASP OFFICE cum RESIDENCE.		DEPTH OF BORING : 19.5m	R. L.: 2.44m below from Road Level.
CLIENT : PWD.		DATE OF BORING: 30-08-2014.	B. W. T : 2.64m below from E.G.L.

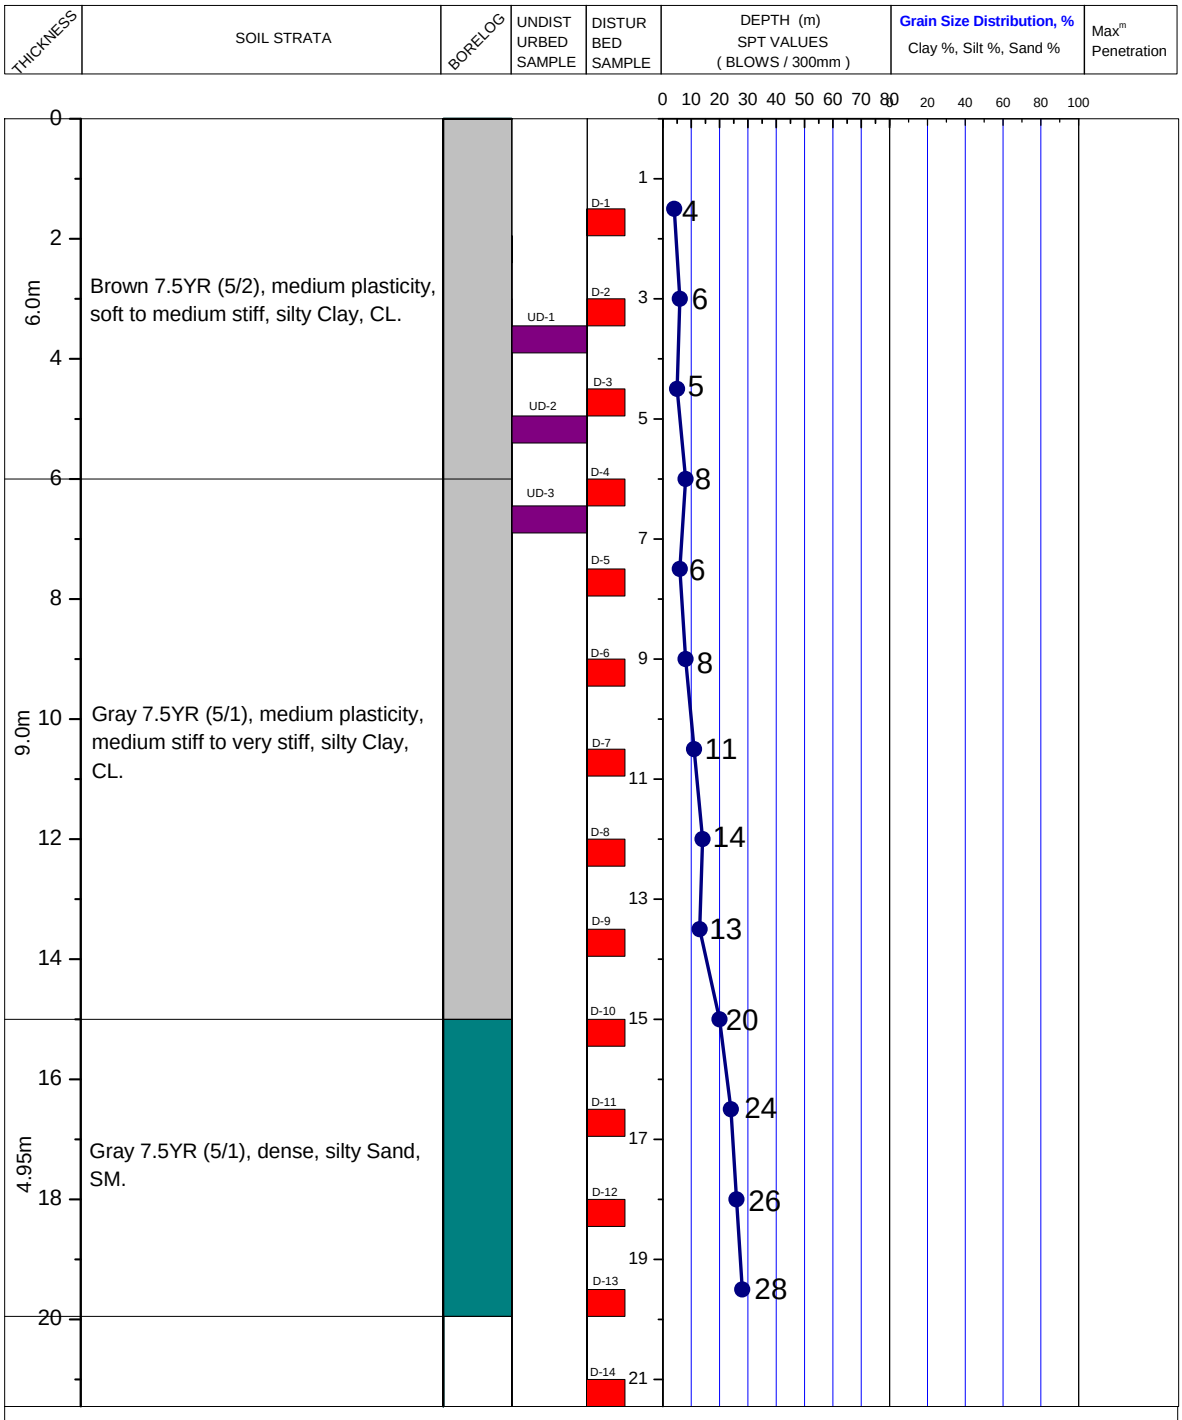

LEGEND FOR BORELOG AND GRAIN SIZE DISTRIBUTION (BASED ON 'ASTM CLASSIFICATION D-2487')

PLASTIC CLAY | SAND | SHALE | UNDISTURBED SAMPLE

MICACEOUS FINE SAND/SILT | SILT | PEAT/HIGHLY ORGANIC SOIL | DISTURBED SAMPLE

N- BLOWS DELIVERED PER FOOT BY A 140 LB HAMMER FALLING 30 INCHES

MAX^{m} PENETRATION= 50 BLOWS

AFTER 50 BLOWS PENETRATION DEPTH WERE MEASURED