A2	Tarique Hasan & Associates Ltd.	BOREHOLE NO: 06	Easting: 222938.00	Northing: 2524186.00
		LOCATION : Barisal Airport, Barisal.		
PROJECT : Consultant Services for Development of Saidpur, Barisal and Osmani International Airport Projects (Design Phase)		DEPTH OF BORING : 15.0m		R. L. : 2.430m
CLIENT : Civil Aviation Authority of Bangladesh.		DATE OF BORING : 06-10-2018		B. W. T :1.4 m below from E. G. L.

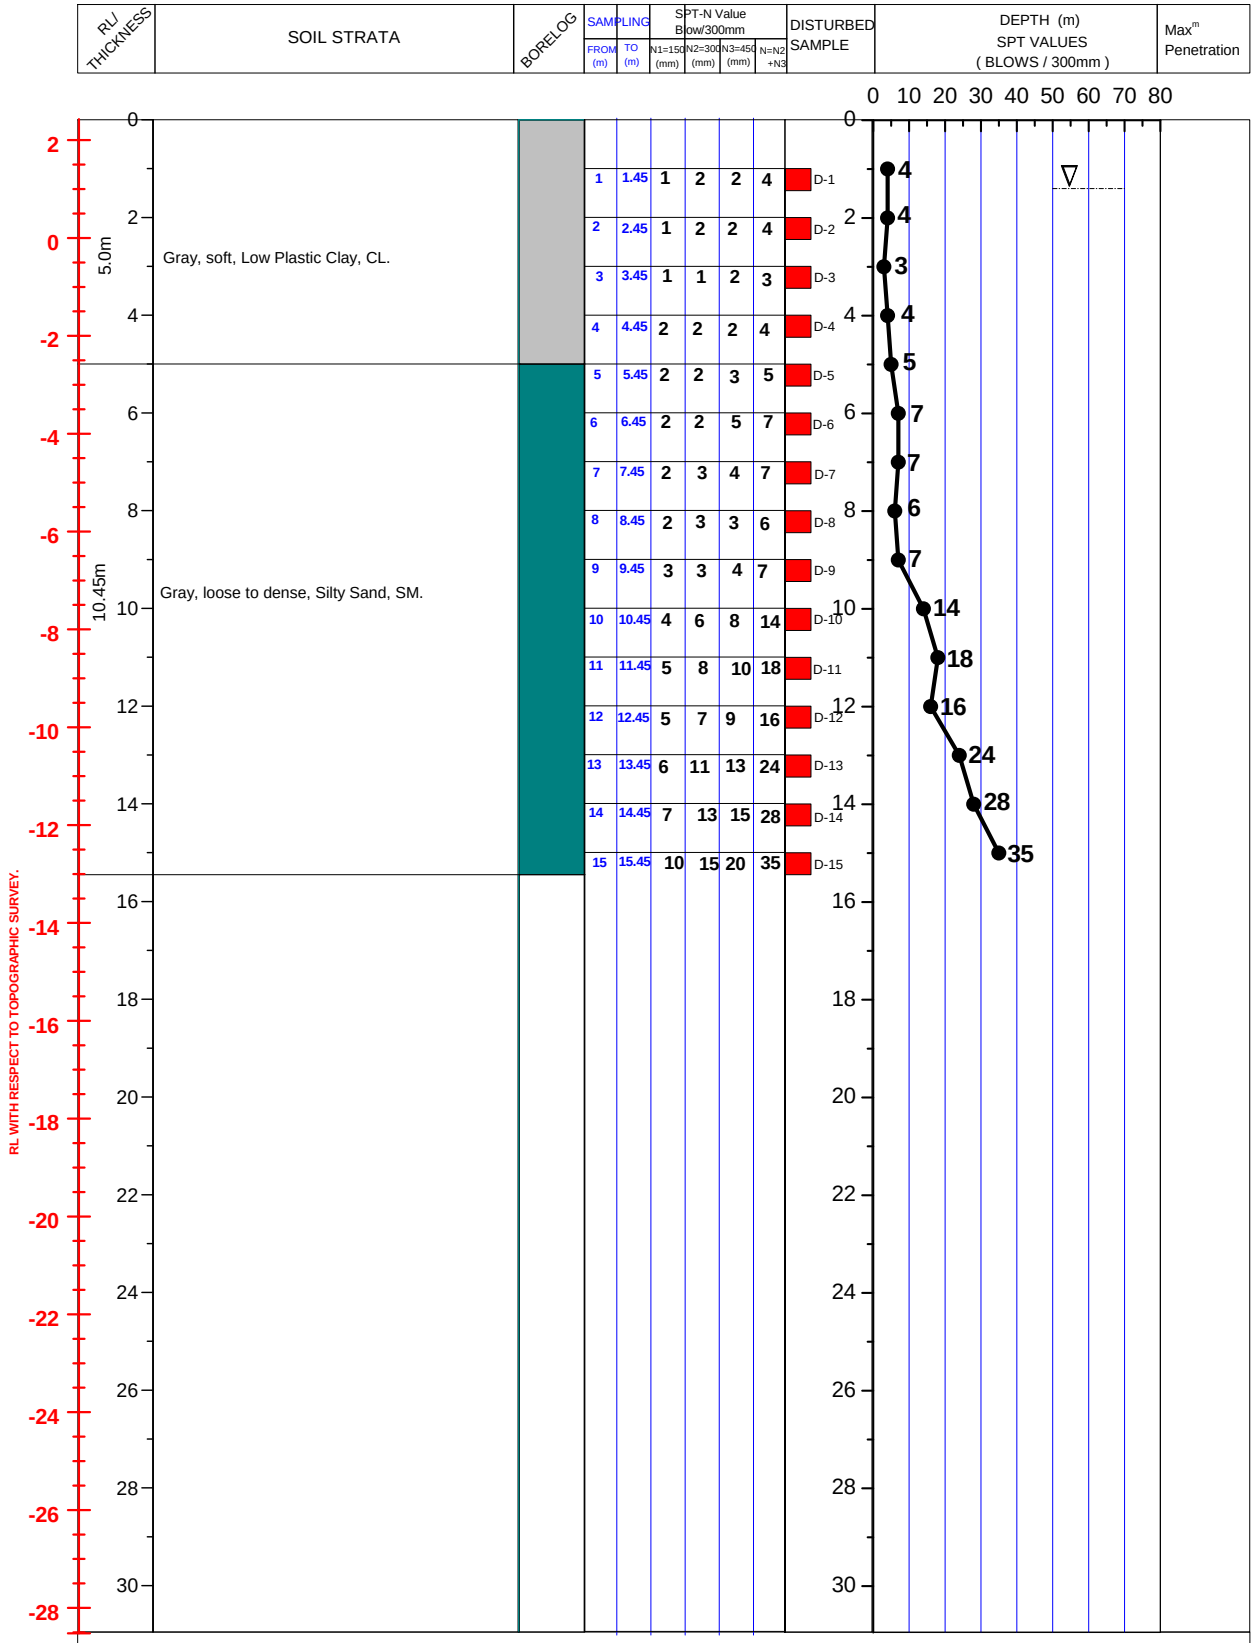

LEGEND FOR BOREHOLE AND GRAIN SIZE DISTRIBUTION (BASED ON 'ASTM CLASSIFICATION D-2487')

PLASTIC CLAY	SILT	PEAT/HIGHLY ORGANIC SOIL	UNDISTURBED SAMPLE
MICACEOUS FINE SAND/SILT	SAND	SHALE	DISTURBED SAMPLE

N- BLOWS DELIVERED PER FOOT BY A 140 LB HAMMER FALLING 30 INCHES

MAX^m PENETRATION= 50 BLOWS. AFTER 50 BLOWS PENETRATION DEPTH WERE MEASURED