A2	PROSOIL	BOREHOLE NO: BH-1	
		LOCATION : House #231, Road #04, CDA R/A, Agrabad, Chittagong.	
PROJECT : METROPOLE.		DEPTH OF BORING : 39.0m	R. L. : On Road Level.
CLIENT : Building Technology & Ideas Ltd.		DATE OF BORING : 12-09-2011.	G. W. T : Tidal Water.

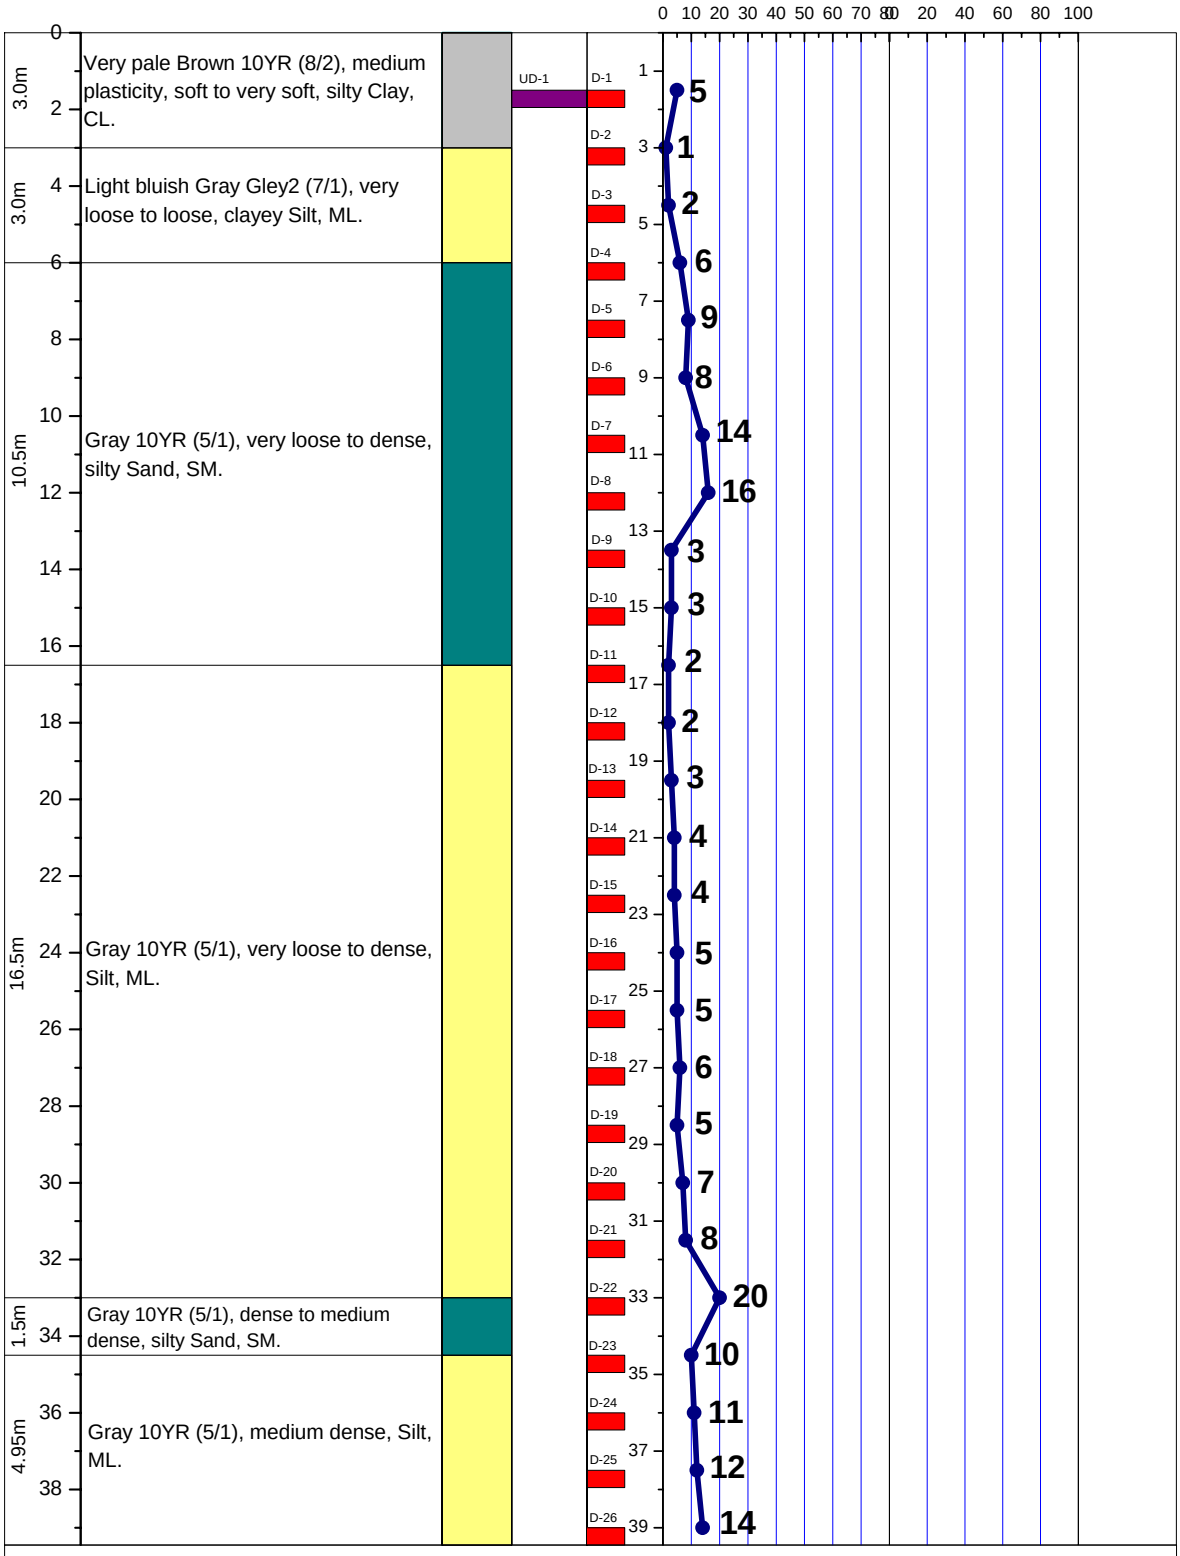

LEGEND FOR BORELOG AND GRAIN SIZE DISTRIBUTION (BASED ON 'ASTM CLASSIFICATION D-2487')

PLASTIC CLAY	SILT	PEAT/HIGHLY ORGANIC SOIL	UNDISTURBED SAMPLE
MICACEOUS FINE SAND/SILT	SAND	SHALE	DISTURBED SAMPLE

N- BLOWS DELIVERED PER FOOT BY A 140 LB HAMMER FALLING 30 INCHES

MAX^{m} PENETRATION= 50 BLOWS. AFTER 50 BLOWS PENETRATION DEPTH WERE MEASURED