A2	PROSOIL	BOREHOLE NO: BH-1	
		LOCATION : Chainage 7+760 to 7+920m On Feni sadar-Elahigonj -Rajapur-Kurashimunshi-Tulatali Road, Feni.	
PROJECT : Proposed Kata Khal Steel Bridge At Gap No 8/2.		DEPTH OF BORING : 33.0m	Chainage: 7+761 R. L. : 5.02
CLIENT : Road Division, Feni.		DATE OF BORING: 14-11-2012.	G. W. T : 1.83m below from E.G.L.

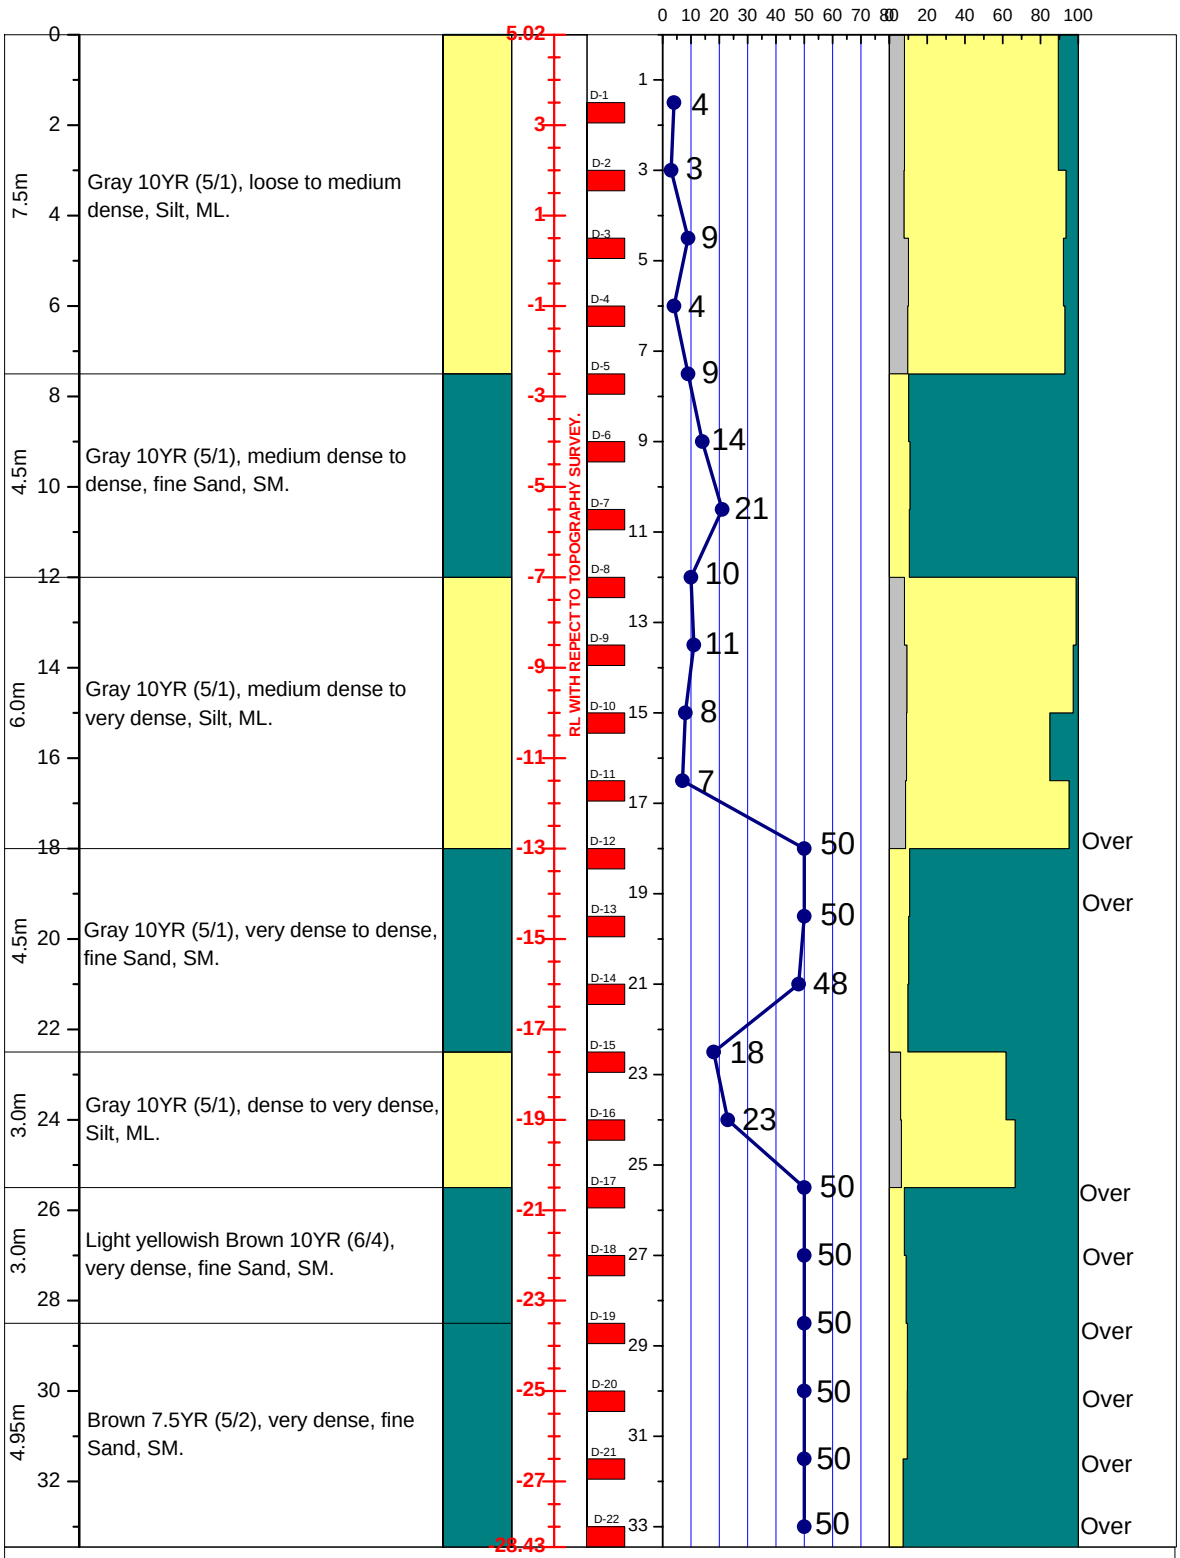

LEGEND FOR BORELOG AND GRAIN SIZE DISTRIBUTION (BASED ON 'ASTM CLASSIFICATION D-2487')

PLASTIC CLAY	SILT	PEAT/HIGHLY ORGANIC SOIL	UNDISTURBED SAMPLE
MICACEOUS FINE SAND/SILT	SAND	SHALE	DISTURBED SAMPLE

N- BLOWS DELIVERED PER FOOT BY A 140 LB HAMMER FALLING 30 INCHES

MAX^m PENETRATION= 50 BLOWS. AFTER 50 BLOWS PENETRATION DEPTH WERE MEASURED