A2	PROSOIL	BOREHOLE NO: BH-1	
		LOCATION : Jangalhata, Golabganj, Sylhet. (24°59'16.9243"N, 91°58'50.3784"E).	
PROJECT : Jangalhata GPS, (Multi-purpose Cyclone Shelter/Govt. Primary School)		DEPTH OF BORING : 21.0m	R. L.: 0.76m above from Road Level.
CLIENT : US Army Corps of Engr, Alaska District. THROUGH : AUSPICIOUS, QA Contractor.		DATE OF BORING : 15-04-2013.	G. W. T : 7.62m below from E.G.L.

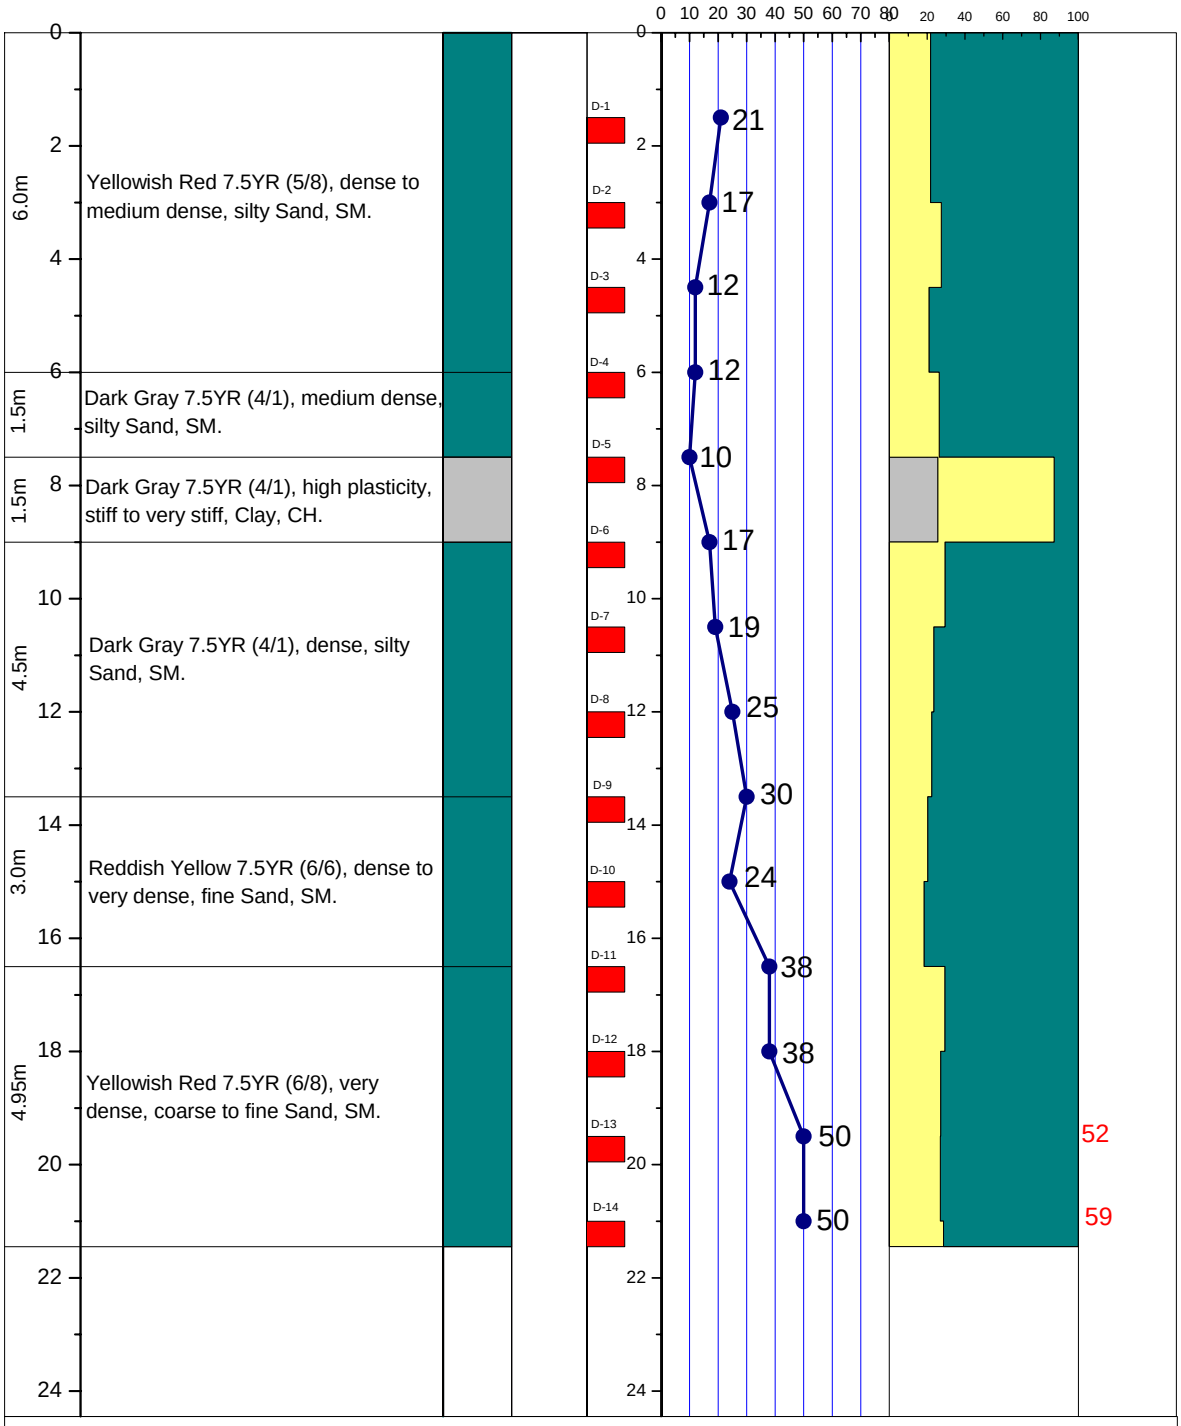

LEGEND FOR BORELOG AND GRAIN SIZE DISTRIBUTION (BASED ON 'ASTM CLASSIFICATION D-2487')

PLASTIC CLAY	SILT	SHALE	UNDISTURBED SAMPLE
MICACEOUS FINE SAND/SILT	SAND	PEAT/HIGHLY ORGANIC SOIL	DISTURBED SAMPLE

N- BLOWS DELIVERED PER FOOT BY A 140 LB HAMMER FALLING 30 INCHES

MAX^{m} PENETRATION= 50 BLOWS
AFTER 50 BLOWS PENETRATION DEPTH WERE MEASURED

A6	PROSOIL	BOREHOLE NO: BH-1 (SETTLEMENT CALCULATION)
		LOCATION : Jangalhata, Golabganj, Sylhet. (24°59'16.9243"N, 91°58'50.3784"E).
PROJECT : Jangalhata GPS, (Multi-purpose Cyclone Shelter/Govt. Primary School).		**SHALLOW FOOTING:** B: 0.6m, L=0.9m, P=100kpa
CLIENT : US Army Corps of Engr, Alaska District. THROUGH : AUSPICIOUS, QA Contractor.		**Shear failure Safety Factor=0.3**

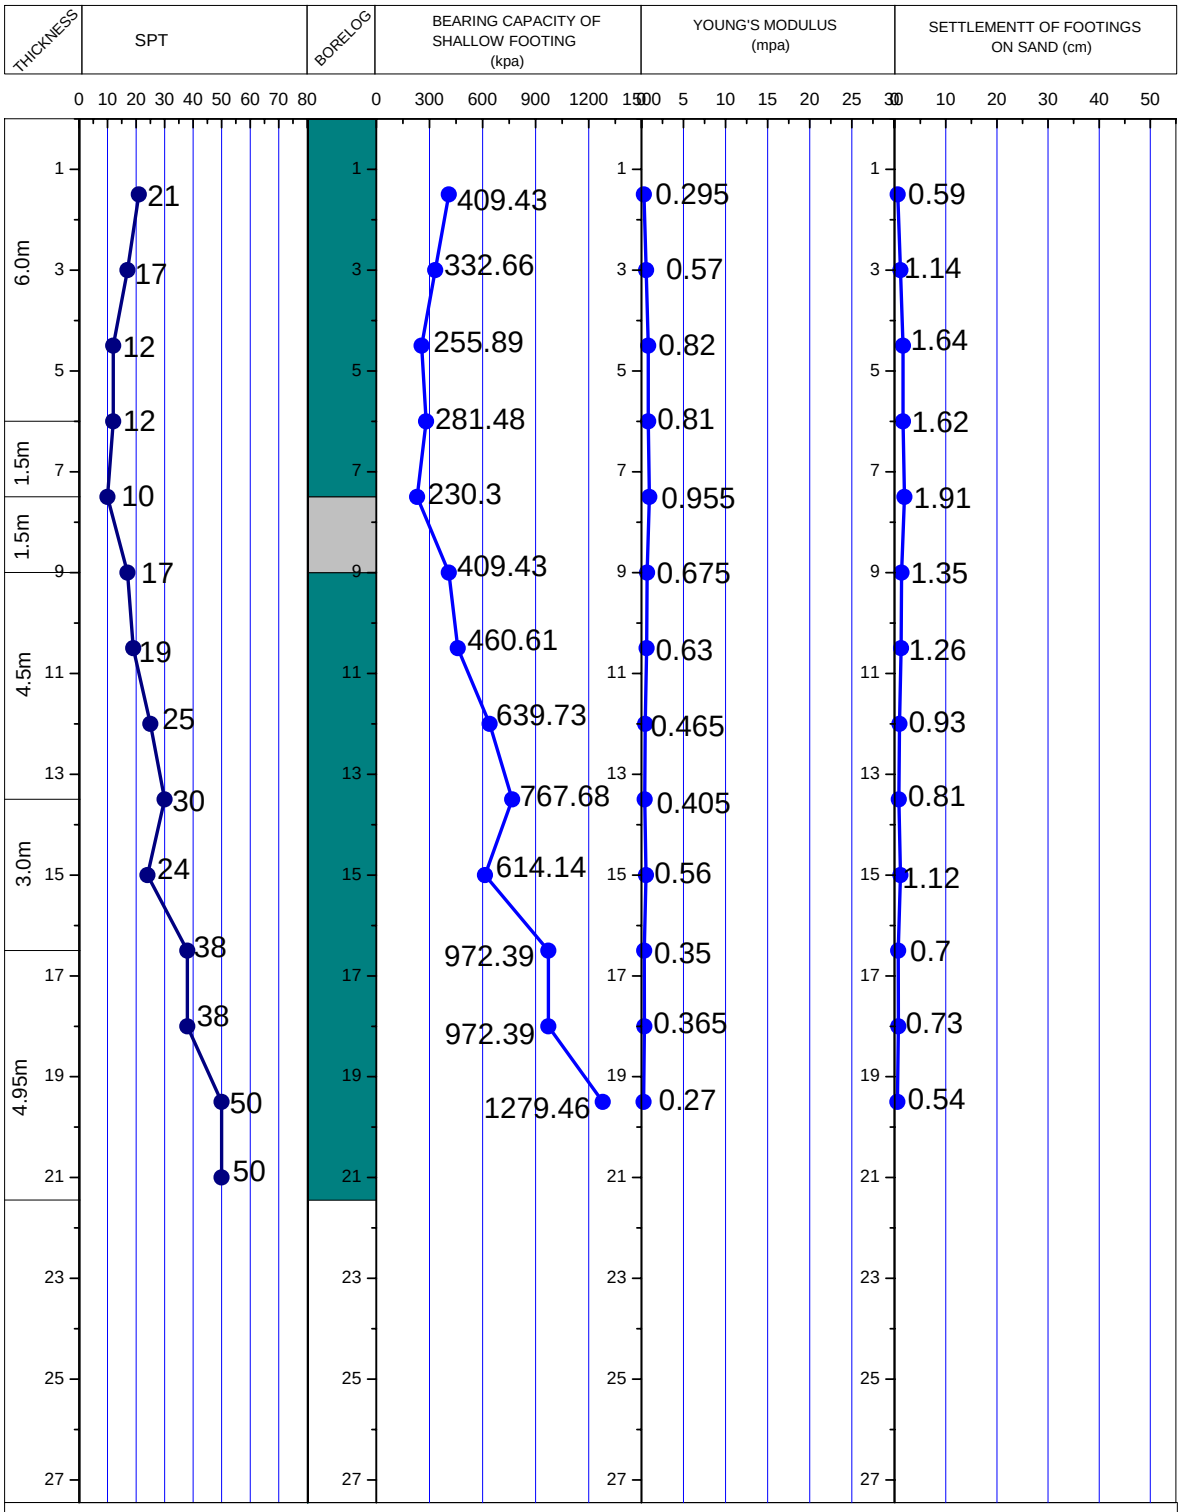

LEGEND FOR BORELOG AND GRAIN SIZE DISTRIBUTION (BASED ON 'ASTM CLASSIFICATION D-2487')

PLASTIC CLAY	SILT	SHALE	UNDISTURBED SAMPLE
MICACEOUS FINE SAND/SILT	SAND	PEAT/HIGHLY ORGANIC SOIL	

SETTLEMENT CALCULATION BY SOFTWARE: **NOVO SPT CORRELATION PROGRAM.**