A2	PROSOIL	BOREHOLE NO: BH-1	
		LOCATION : Dakmara Gorosthan, Sadar, Natore.	
PROJECT : Telecommunication Tower.		DEPTH OF BORING : 21.0m	R. L.: 1.12m below from Road Level.
CLIENT : AXIATA (Bangladesh) Ltd.		DATE OF BORING : 07-08-2009.	G. W. T : 0.15m above (Rain water) from E. G. L.

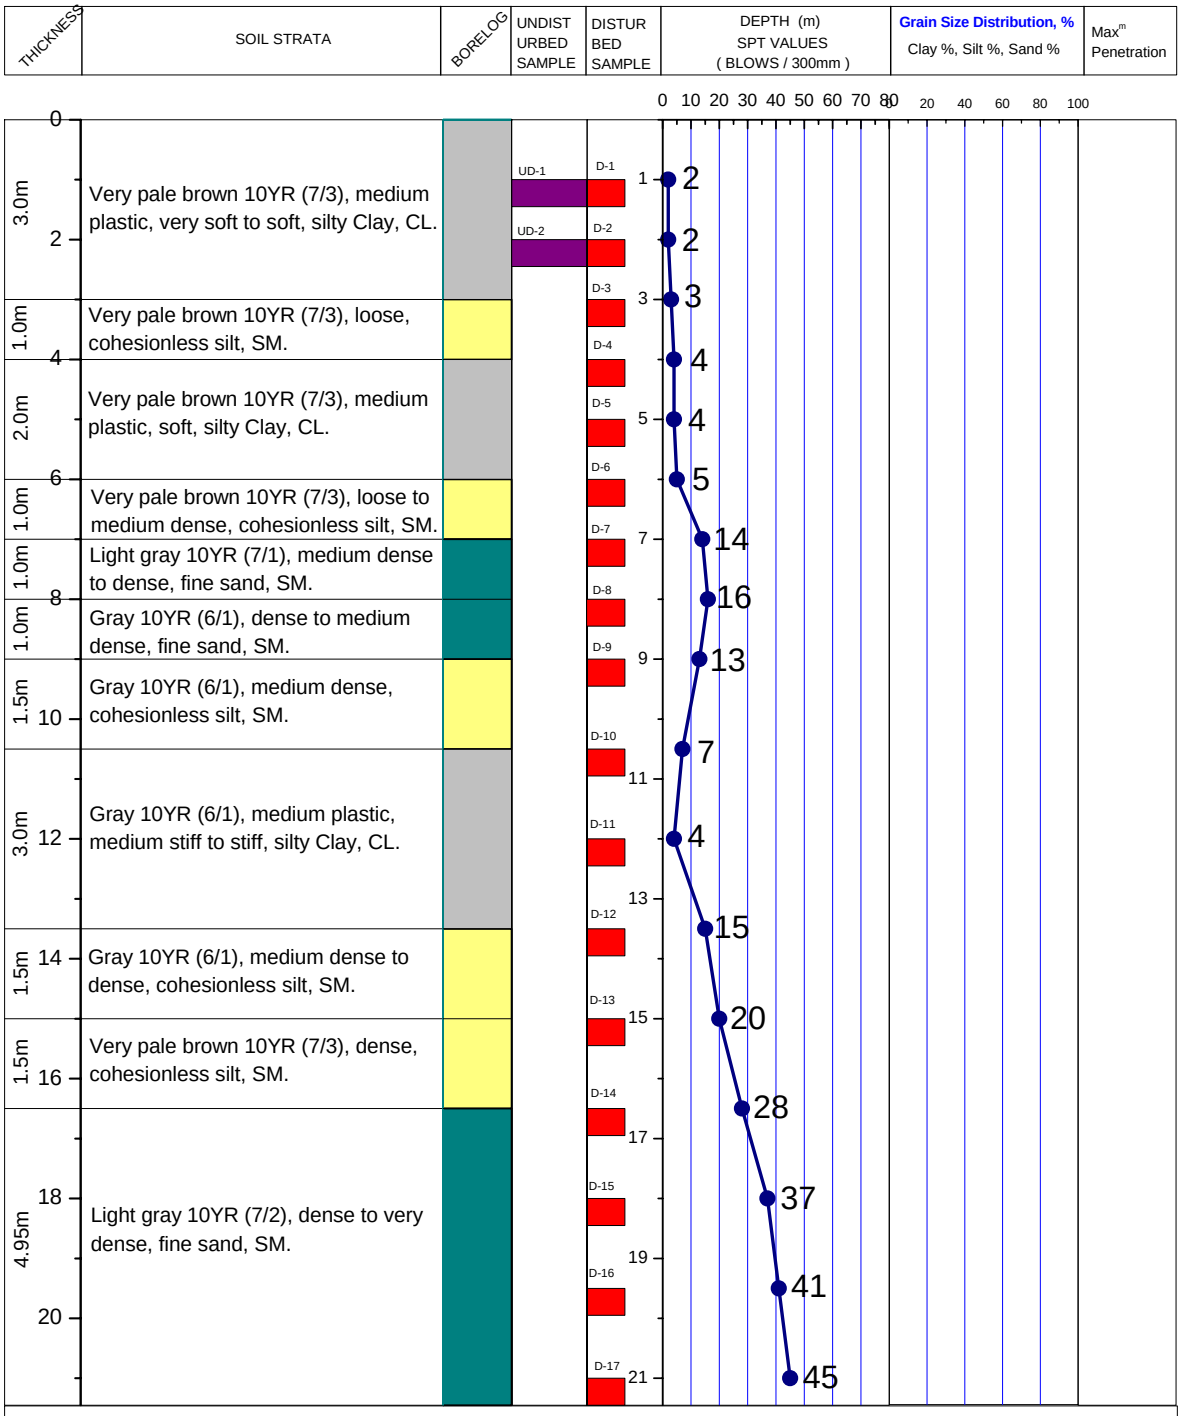

LEGEND FOR BORELOG AND GRAIN SIZE DISTRIBUTION

PLASTIC SILTY CLAY

LOW PLASTIC CLAYEY SILT

NON PLASTIC SILT

SAND

ORGANIC

UNDISTURBED SAMPLE

DISTURBED SAMPLE

SHALE

N- BLOWS DELIVERED PER FOOT BY A 140 LB HAMMER FALLING 30 INCHES

MAX^{m} PENETRATION= 50 BLOWS

AFTER 50 BLOWS PENETRATION DEPTH WERE MEASURED