
A2 PROSOIL	BOREHOLE NO: BH-1	
	LOCATION : Chainage 13+657 km on Darbost-Kanaight-Shahbag Road, Sylhet.	
PROJECT : Proposed Bridge at 14th km (14/1) from Chainage 13+657km to 13+677km.	DEPTH OF BORING : 30.0m	Chainage: 13+657 R. L. : 9.1
CLIENT : Road Division, Sylhet.	DATE OF BORING : 20-02-2010.	G. W. T : 0.30m below from E.G.L.

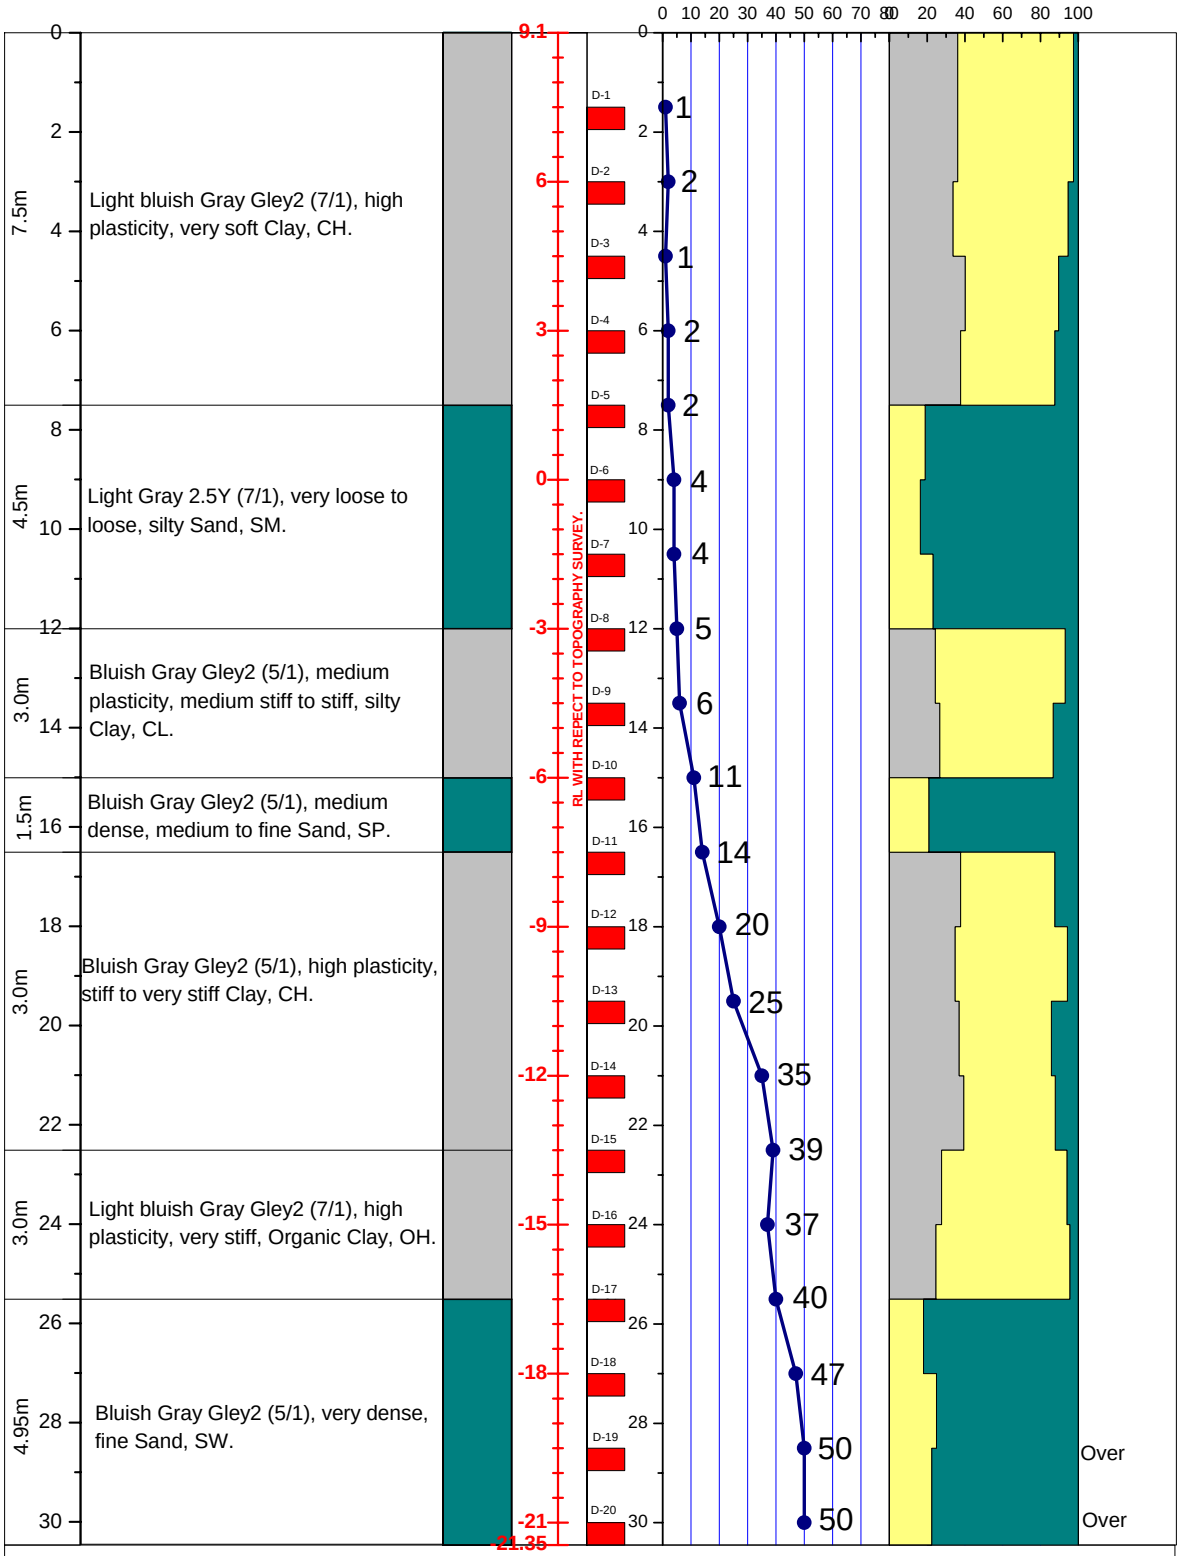

LEGEND FOR BORELOG AND GRAIN SIZE DISTRIBUTION (BASED ON 'ASTM CLASSIFICATION D-2487')

PLASTIC CLAY	SILT	PEAT/HIGHLY ORGANIC SOIL	UNDISTURBED SAMPLE
MICACEOUS FINE SAND/SILT	SAND	SHALE	DISTURBED SAMPLE

N- BLOWS DELIVERED PER FOOT BY A 140 LB HAMMER FALLING 30 INCHES

MAX^m PENETRATION= 50 BLOWS. AFTER 50 BLOWS PENETRATION DEPTH WERE MEASURED