
A2 PROSOIL	BOREHOLE NO: BH-01	
	LOCATION : BGB Rajshahi.	
PROJECT : Proposed 15 Storied Regimental Ors Family Accommodation at Rajshahi Sector Head Quarter, Border Guard Bangladesh.	DEPTH OF BORING : 30.0m	R. L. : on Road Level.
CLIENT : Sheltech Engineering Ltd.	DATE OF BORING : 28-01-2019	B. W. T : 4.7m below from E. G. L.

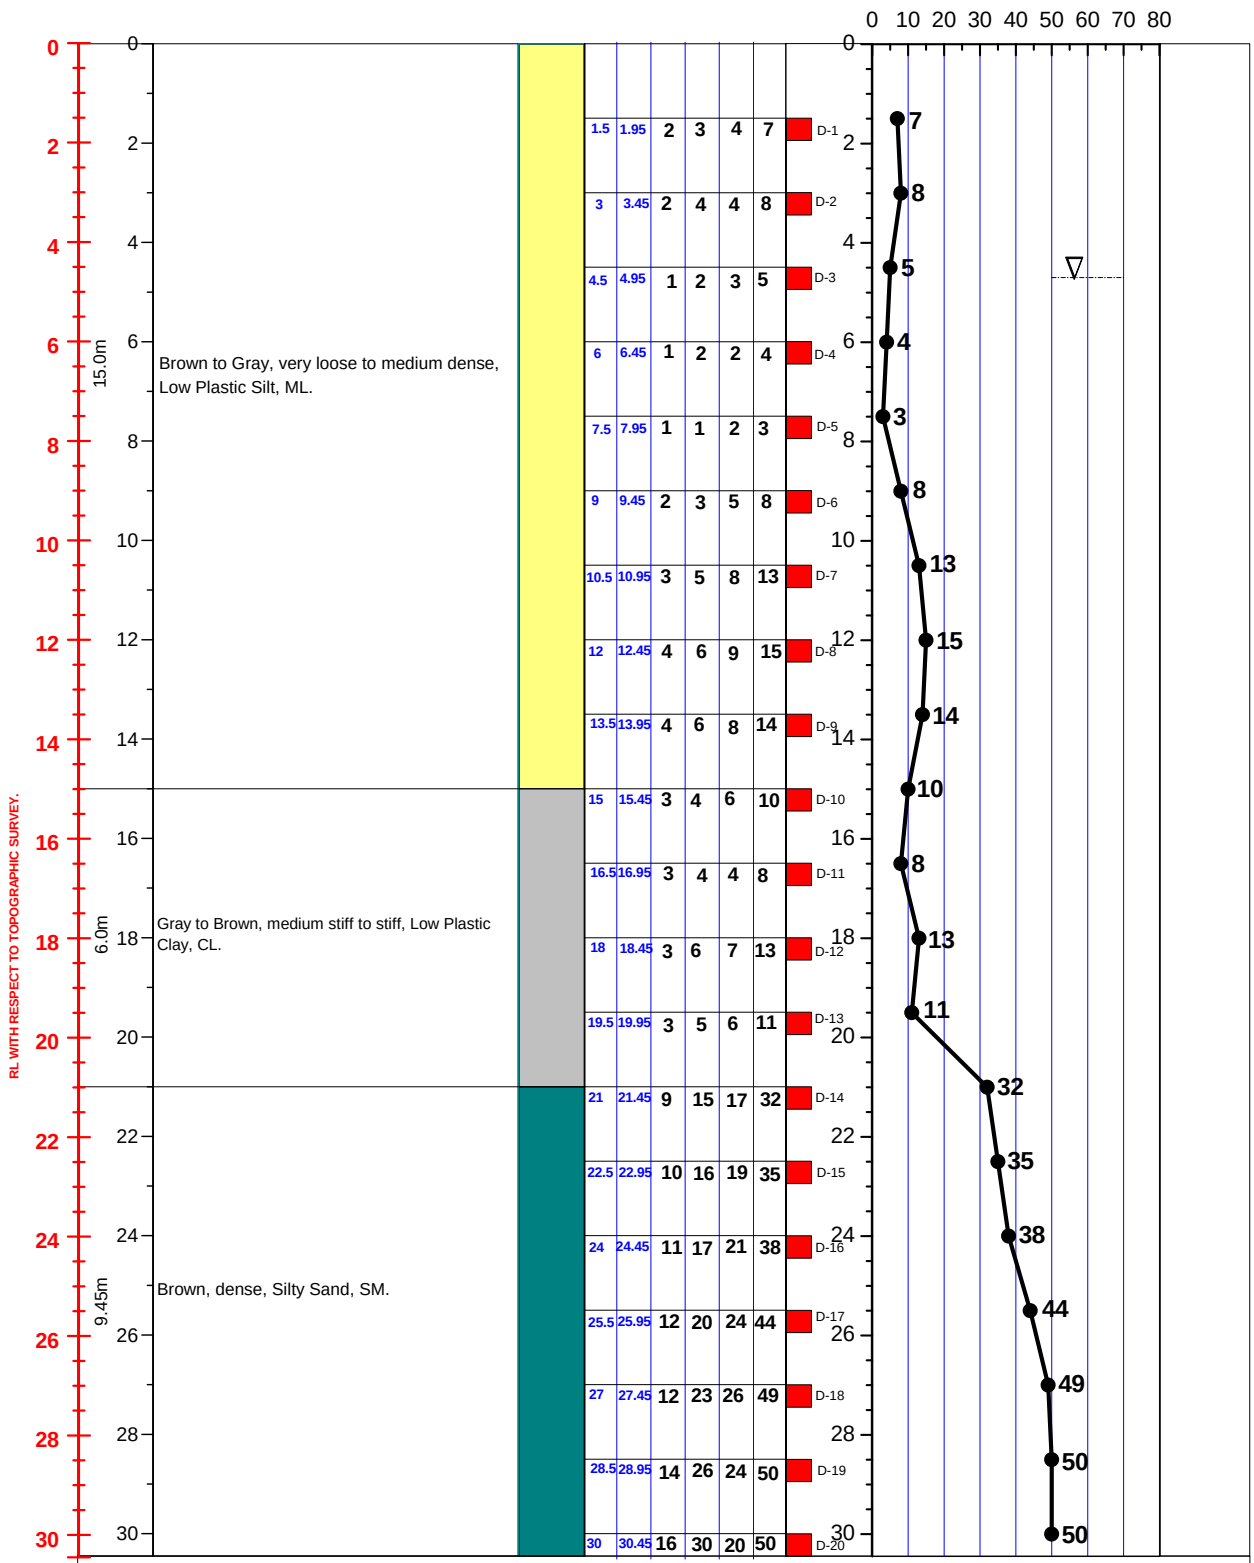

LEGEND FOR BORELOG AND GRAIN SIZE DISTRIBUTION (BASED ON 'ASTM CLASSIFICATION D-2487')

PLASTIC CLAY	SILT	PEAT/HIGHLY ORGANIC SOIL	UNDISTURBED SAMPLE
MICACEOUS FINE SAND/SILT	SAND	SHALE	DISTURBED SAMPLE

N- BLOWS DELIVERED PER FOOT BY A 140 LB HAMMER FALLING 30 INCHES

MAX^m PENETRATION= 50 BLOWS. AFTER 50 BLOWS PENETRATION DEPTH WERE MEASURED