
A2 PROSOIL	BOREHOLE NO: BH-1	
	LOCATION : Kushiara River, Azmiriganj, Habiganj.	
PROJECT : Proposed Bridge.	DEPTH OF BORING : 40.5m	Chainage: R. L. : -2.06
CLIENT : Road Division, Hobigonj.	DATE OF BORING : 23-07-2010.	G. W. T : 1.52m above from E.G.L.

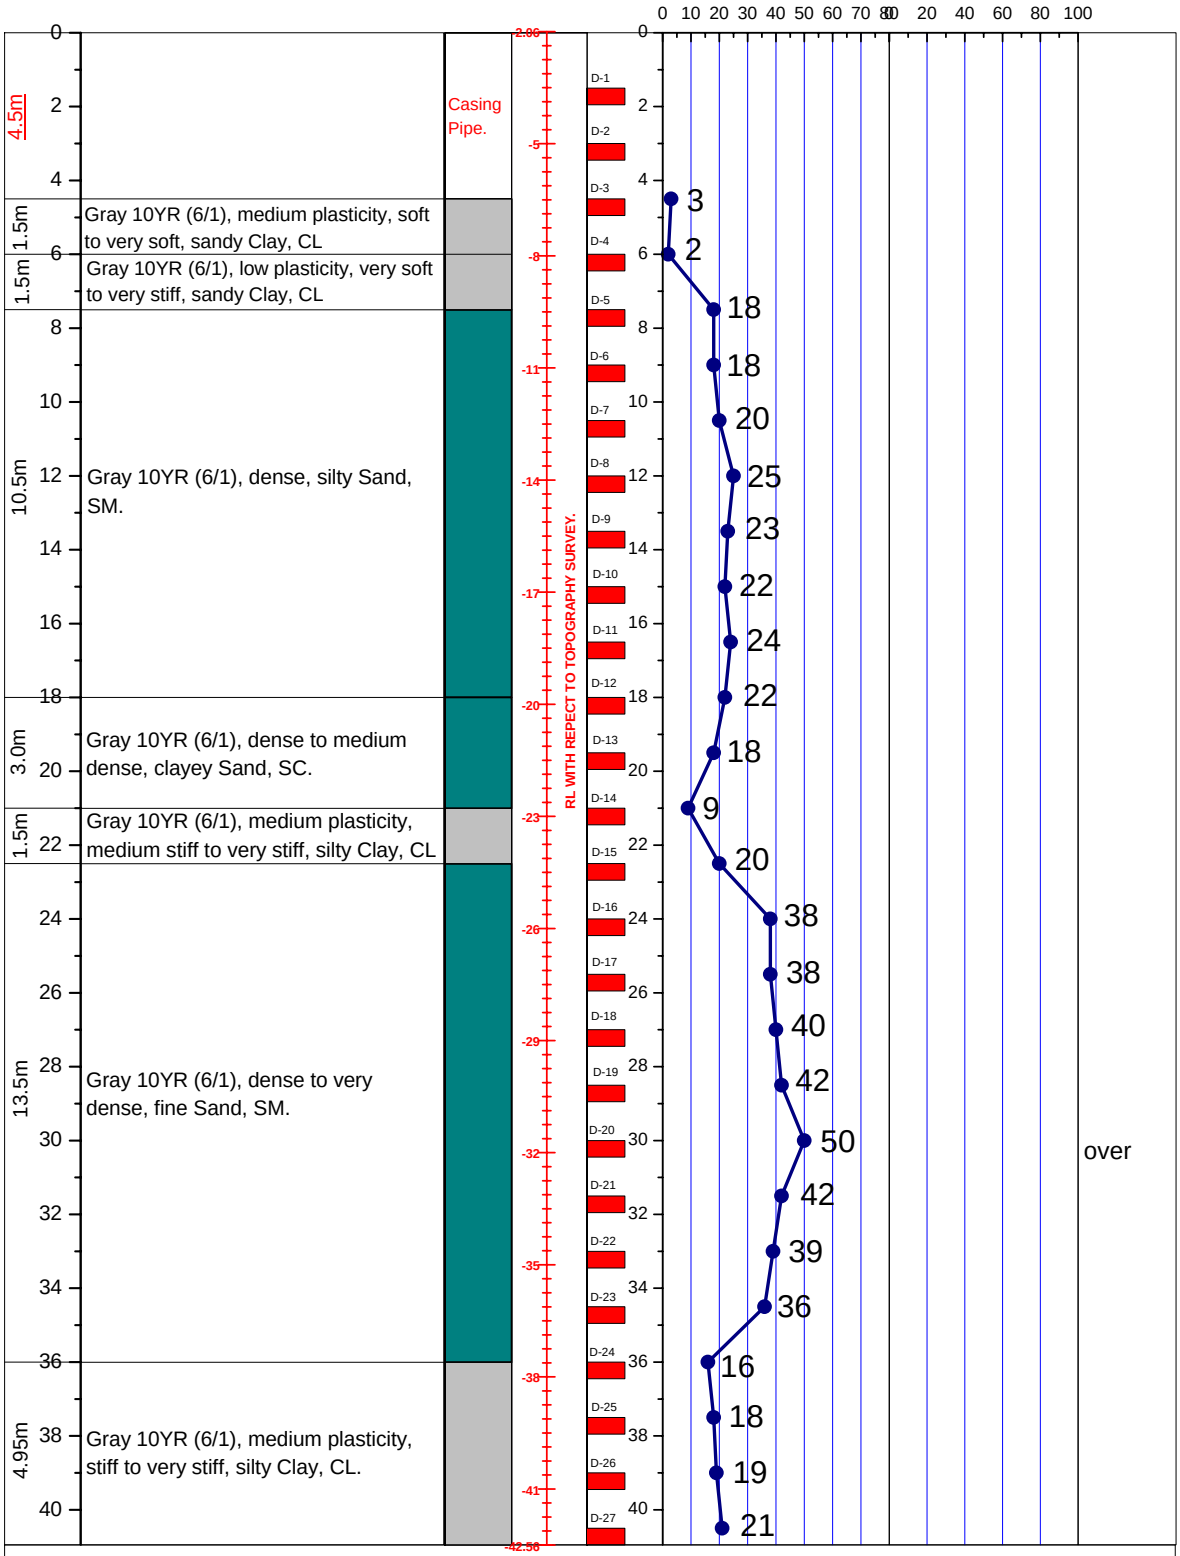


LEGEND FOR BORELOG AND GRAIN SIZE DISTRIBUTION (BASED ON 'ASTM CLASSIFICATION D-2487')

PLASTIC CLAY	SILT	PEAT/HIGHLY ORGANIC SOIL	DISTURBED SAMPLE
MICACEOUS FINE SAND/SILT	SAND	SHALE	UNDISTURBED SAMPLE

N- BLOWS DELIVERED PER FOOT BY A 140 LB HAMMER FALLING 30 INCHES

MAX^{m} PENETRATION= 50 BLOWS. AFTER 50 BLOWS PENETRATION DEPTH WERE MEASURED

A2	PROSOIL	BOREHOLE NO: BH-2	
		LOCATION : Kushiara River, Azmiriganj, Habiganj.	
PROJECT : Proposed Bridge.		DEPTH OF BORING : 42.0m	Chainage: R. L. : 4.14
CLIENT : Road Division, Hobigonj.		DATE OF BORING : 26-07-2010.	G. W. T : 1.52m above from E.G.L.

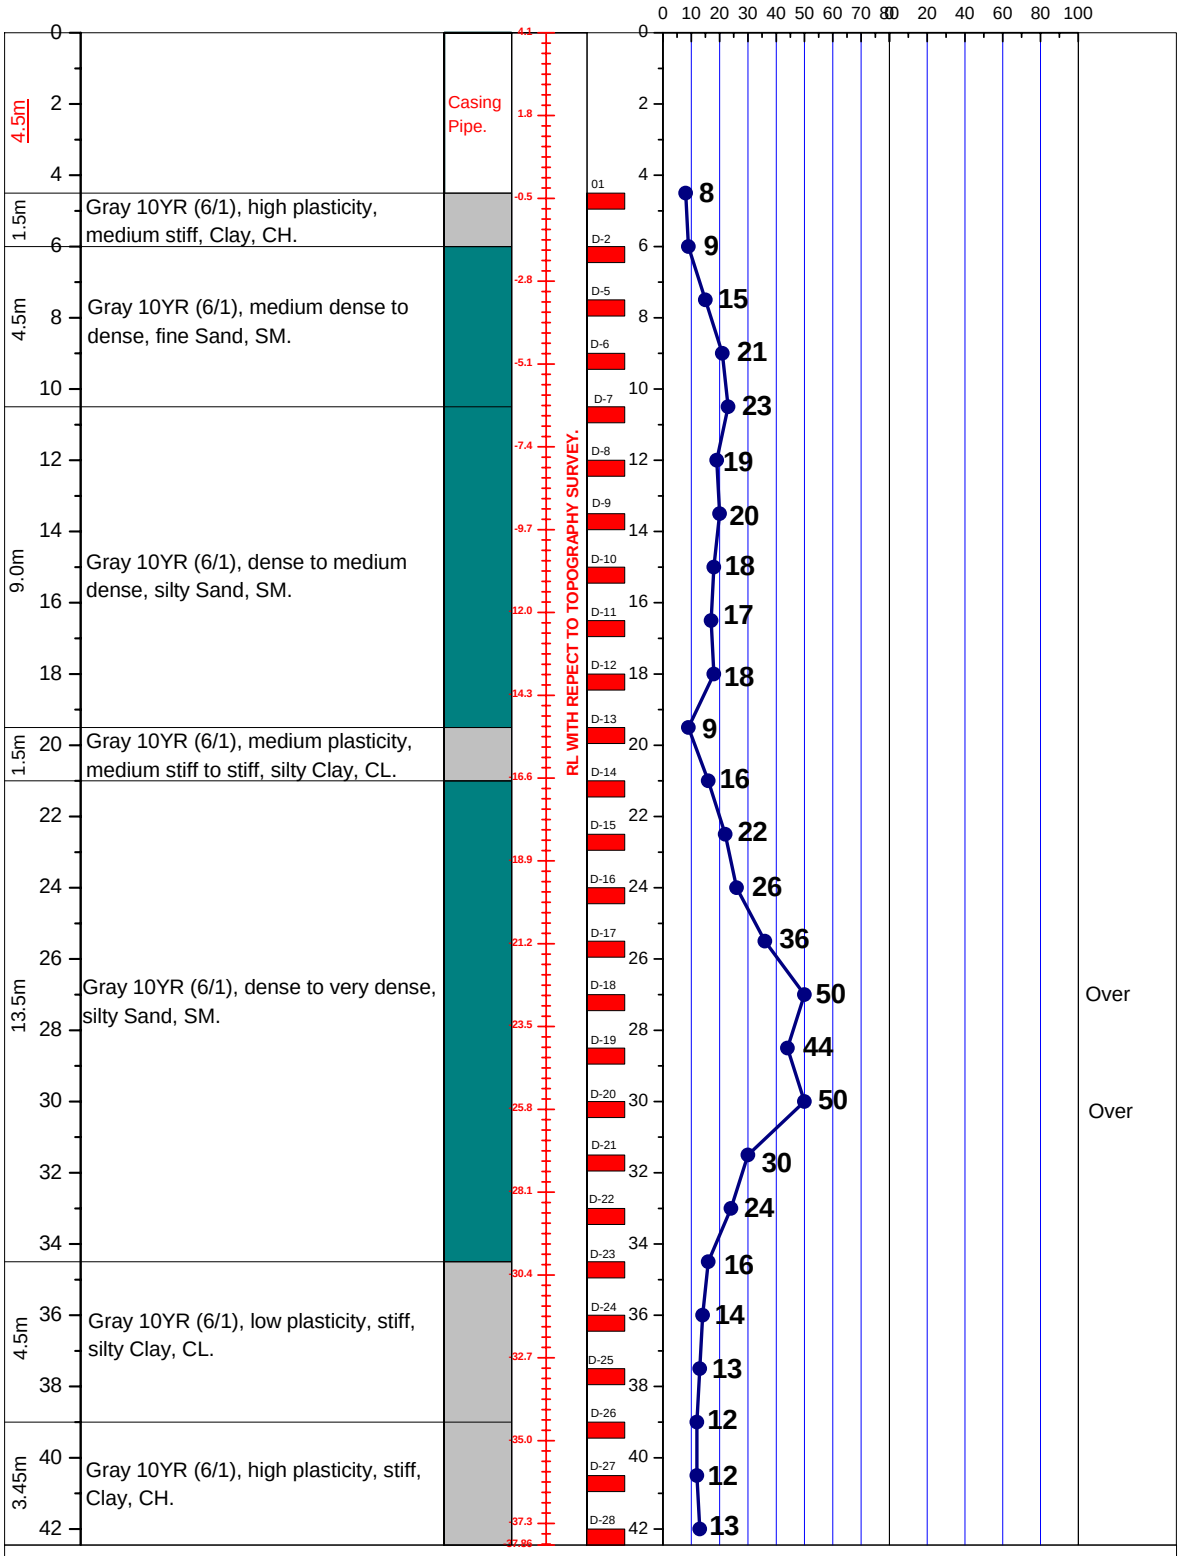

LEGEND FOR BORELOG AND GRAIN SIZE DISTRIBUTION (BASED ON 'ASTM CLASSIFICATION D-2487')


PLASTIC CLAY	SILT	PEAT/HIGHLY ORGANIC SOIL	UNDISTURBED SAMPLE
MICACEOUS FINE SAND/SILT	SAND	SHALE	DISTURBED SAMPLE

N- BLOWS DELIVERED PER FOOT BY A 140 LB HAMMER FALLING 30 INCHES

MAX^{m} PENETRATION= 50 BLOWS. AFTER 50 BLOWS PENETRATION DEPTH WERE MEASURED

A2	PROSOIL	BOREHOLE NO: BH-3	
		LOCATION : Kushiara River, Azmiriganj, Habiganj.	
PROJECT : Proposed Bridge.		DEPTH OF BORING : 30.0m	Chainage: R. L. : -4.04
CLIENT : Road Division, Hobigonj.		DATE OF BORING : 13-02-2010.	G. W. T : 10.37m above from E.G.L.

THICKNESS	SOIL STRATA	BORELOG	RL	DISTURBED SAMPLE	DEPTH (m) SPT VALUES (BLOWS / 300mm)	Grain Size Distribution, % Clay %, Silt %, Sand %	Max^{m} Penetration

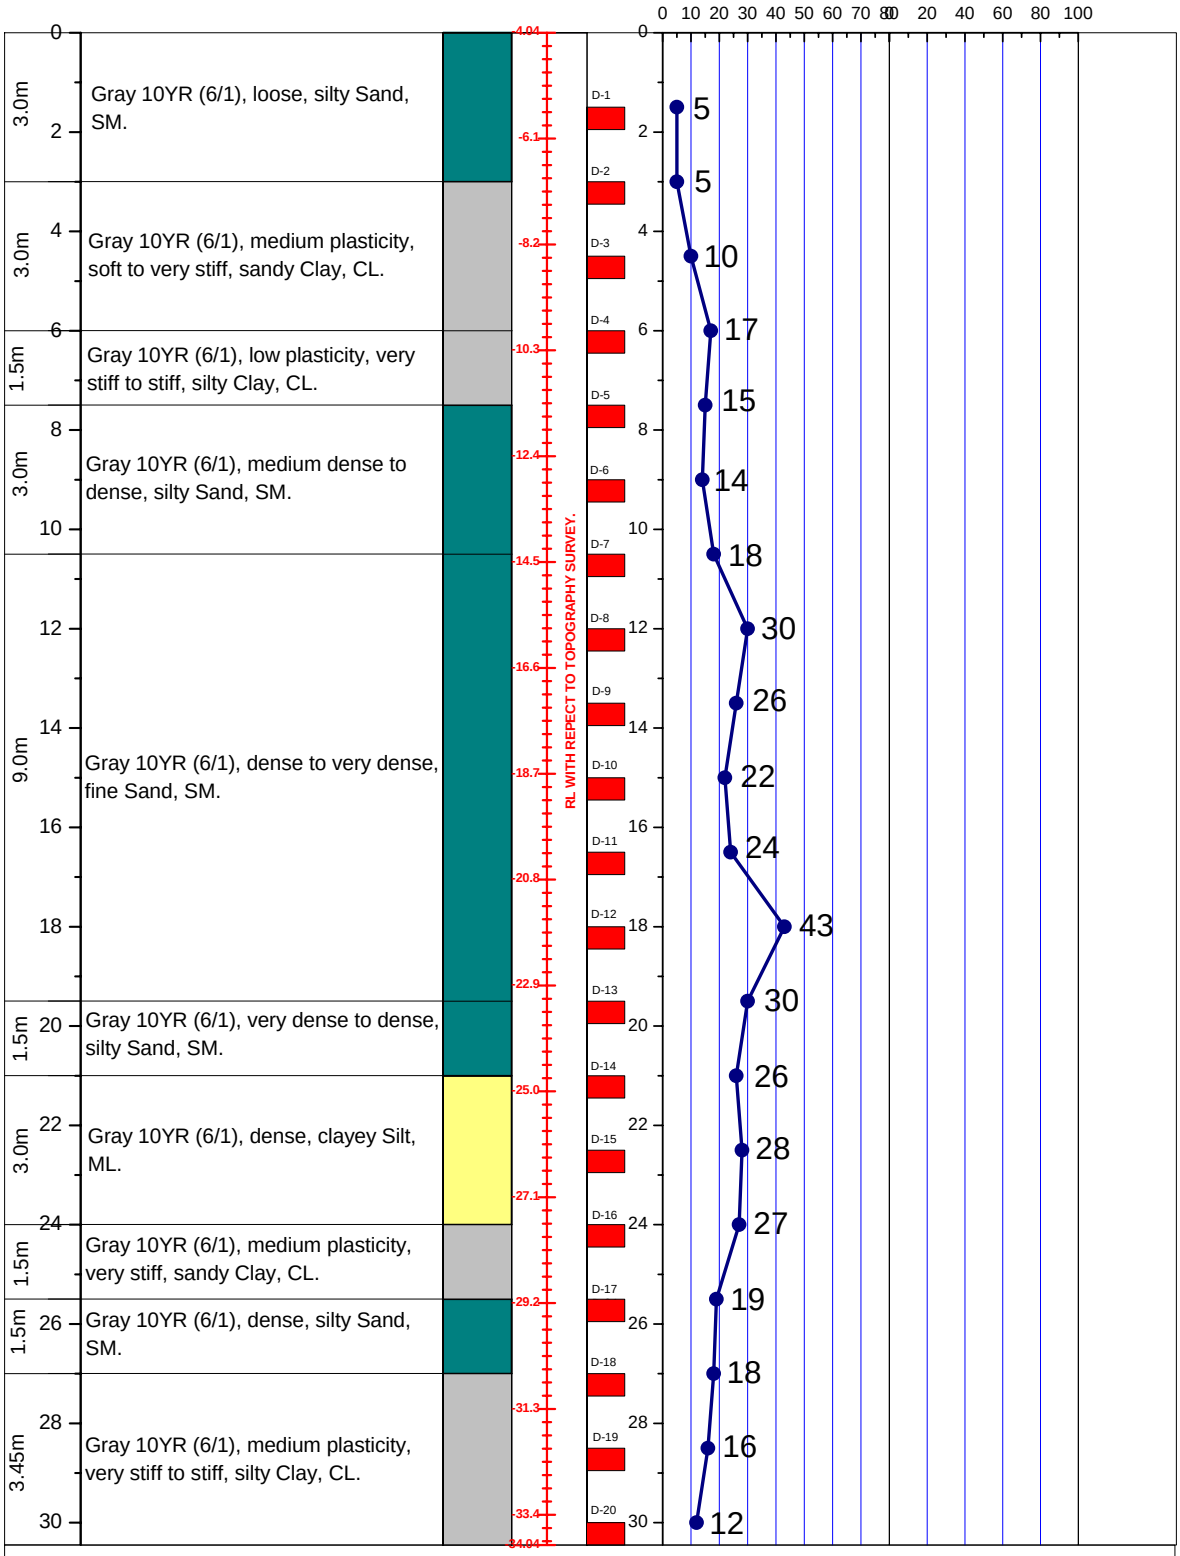


LEGEND FOR BORELOG AND GRAIN SIZE DISTRIBUTION (BASED ON 'ASTM CLASSIFICATION D-2487')

PLASTIC CLAY	SILT	PEAT/HIGHLY ORGANIC SOIL	UNDISTURBED SAMPLE
MICACEOUS FINE SAND/SILT	SAND	SHALE	DISTURBED SAMPLE

N- BLOWS DELIVERED PER FOOT BY A 140 LB HAMMER FALLING 30 INCHES

MAX^{m} PENETRATION= 50 BLOWS. AFTER 50 BLOWS PENETRATION DEPTH WERE MEASURED

A2 PROSOIL	BOREHOLE NO: BH-4	
	LOCATION : Kushiara River, Azmiriganj, Habiganj.	
PROJECT : Proposed Bridge.	DEPTH OF BORING : 40.5m	Chainage: R. L. : -0.20
CLIENT : Road Division, Hobigonj.	DATE OF BORING : 31-07-2010.	G. W. T : 9.76m above from E.G.L.

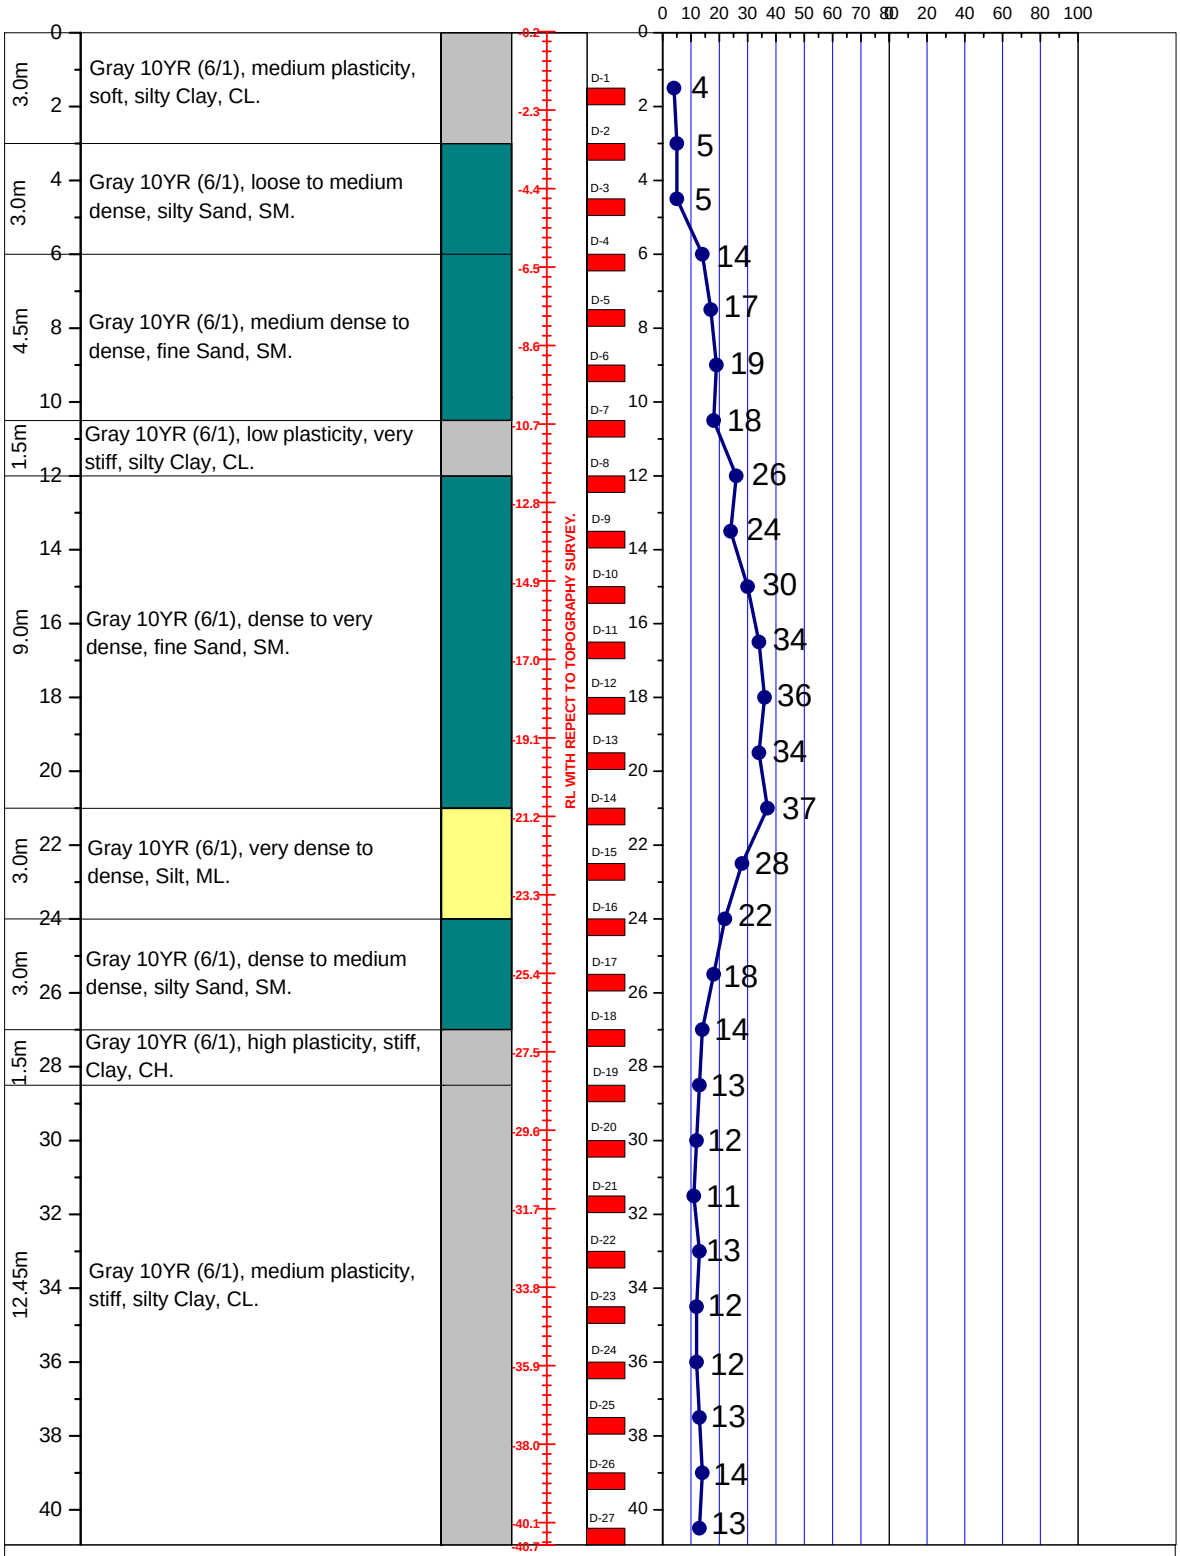


LEGEND FOR BORELOG AND GRAIN SIZE DISTRIBUTION (BASED ON 'ASTM CLASSIFICATION D-2487')

PLASTIC CLAY	SILT	PEAT/HIGHLY ORGANIC SOIL	DISTURBED SAMPLE
MICACEOUS FINE SAND/SILT	SAND	SHALE	UNDISTURBED SAMPLE

N- BLOWS DELIVERED PER FOOT BY A 140 LB HAMMER FALLING 30 INCHES

MAX^{m} PENETRATION= 50 BLOWS. AFTER 50 BLOWS PENETRATION DEPTH WERE MEASURED

A2	PROSOIL	BOREHOLE NO: BH-5	
		LOCATION : Kushiara River, Azmiriganj, Habiganj.	
PROJECT : Proposed Bridge.		DEPTH OF BORING : 42.0m	Chainage: R. L. : 5.63
CLIENT : Road Division, Hobigonj.		DATE OF BORING : 03-08-2010.	G. W. T : On E.G.L.

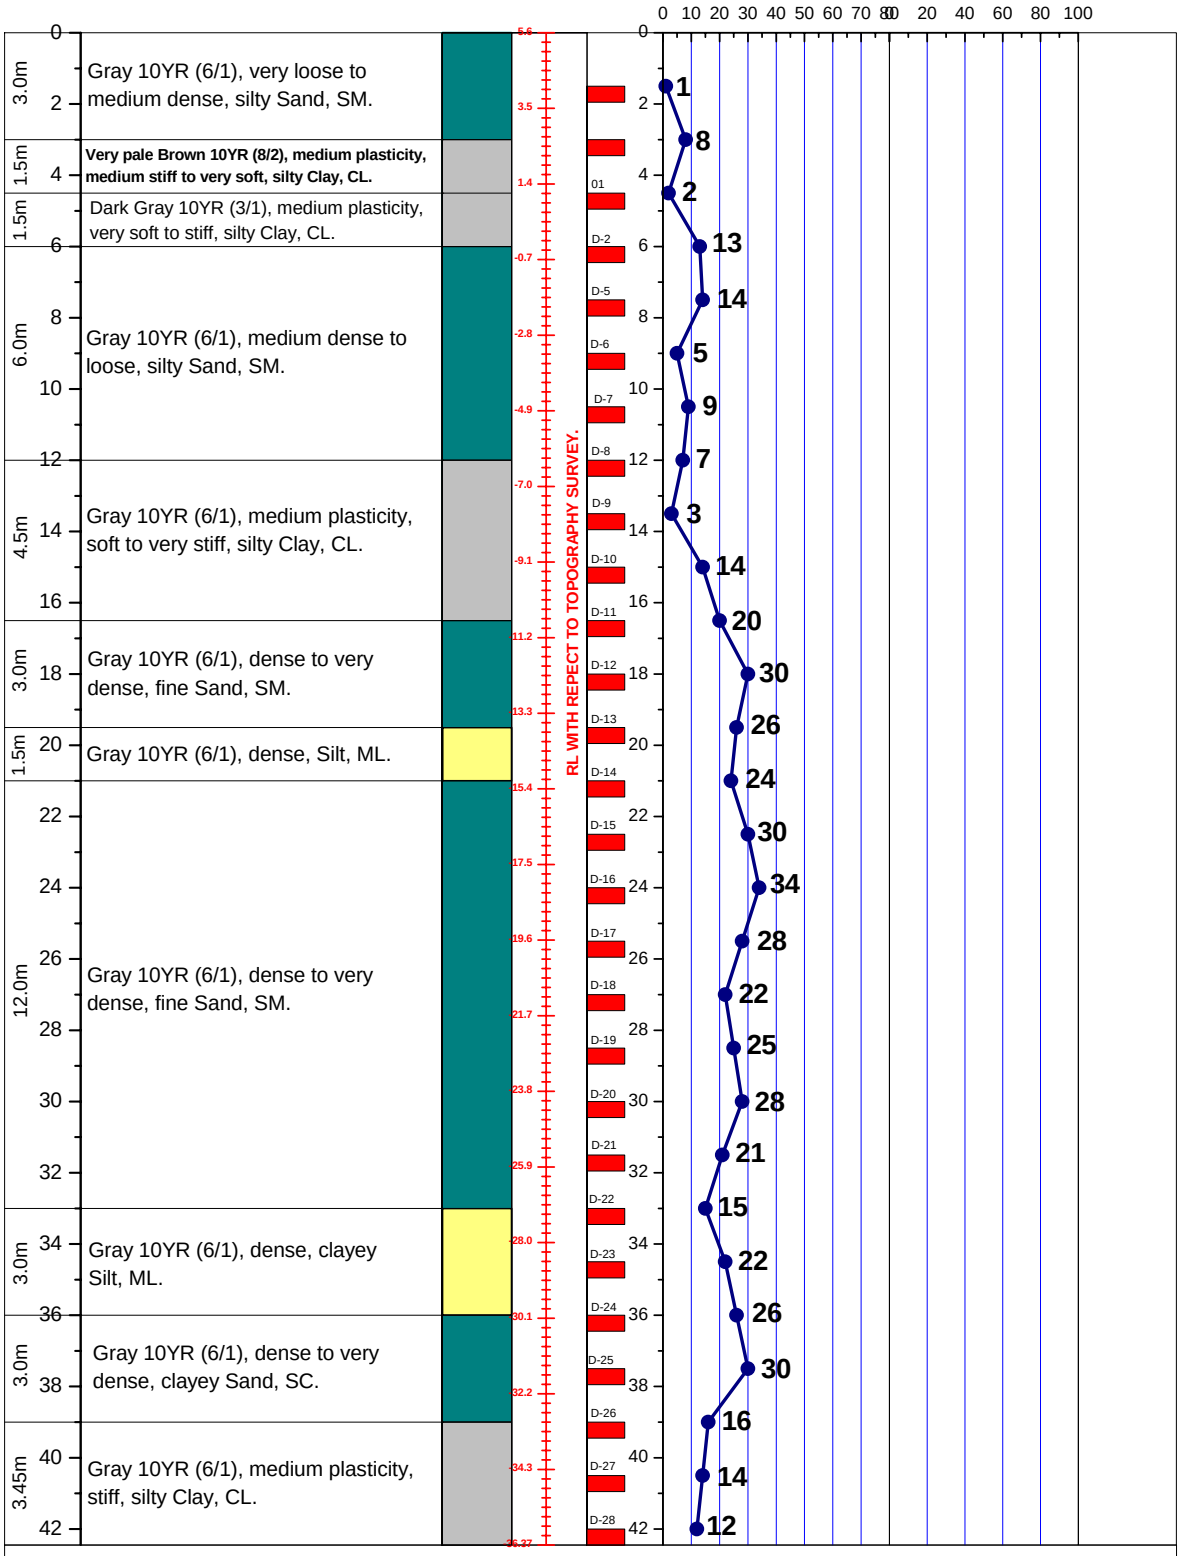

LEGEND FOR BORELOG AND GRAIN SIZE DISTRIBUTION (BASED ON 'ASTM CLASSIFICATION D-2487')

PLASTIC CLAY	SILT	PEAT/HIGHLY ORGANIC SOIL	UNDISTURBED SAMPLE
MICACEOUS FINE SAND/SILT	SAND	SHALE	DISTURBED SAMPLE

N- BLOWS DELIVERED PER FOOT BY A 140 LB HAMMER FALLING 30 INCHES

MAX^m PENETRATION= 50 BLOWS. AFTER 50 BLOWS PENETRATION DEPTH WERE MEASURED