A2 PROSOIL	BOREHOLE NO: BH-1	
	LOCATION : Gap No. (8/1) of Kuti-Kasba Road, B.Baria.	
PROJECT : Proposed PC Girder Bridge at Gap No.(9/1).	DEPTH OF BORING : 45.0m	Chainage: 7+775.5 R. L. : 5.55
CLIENT : Road Division, B.Baria.	DATE OF BORING : 28-02-2012.	G. W. T : 2.44m below from E.G.L.

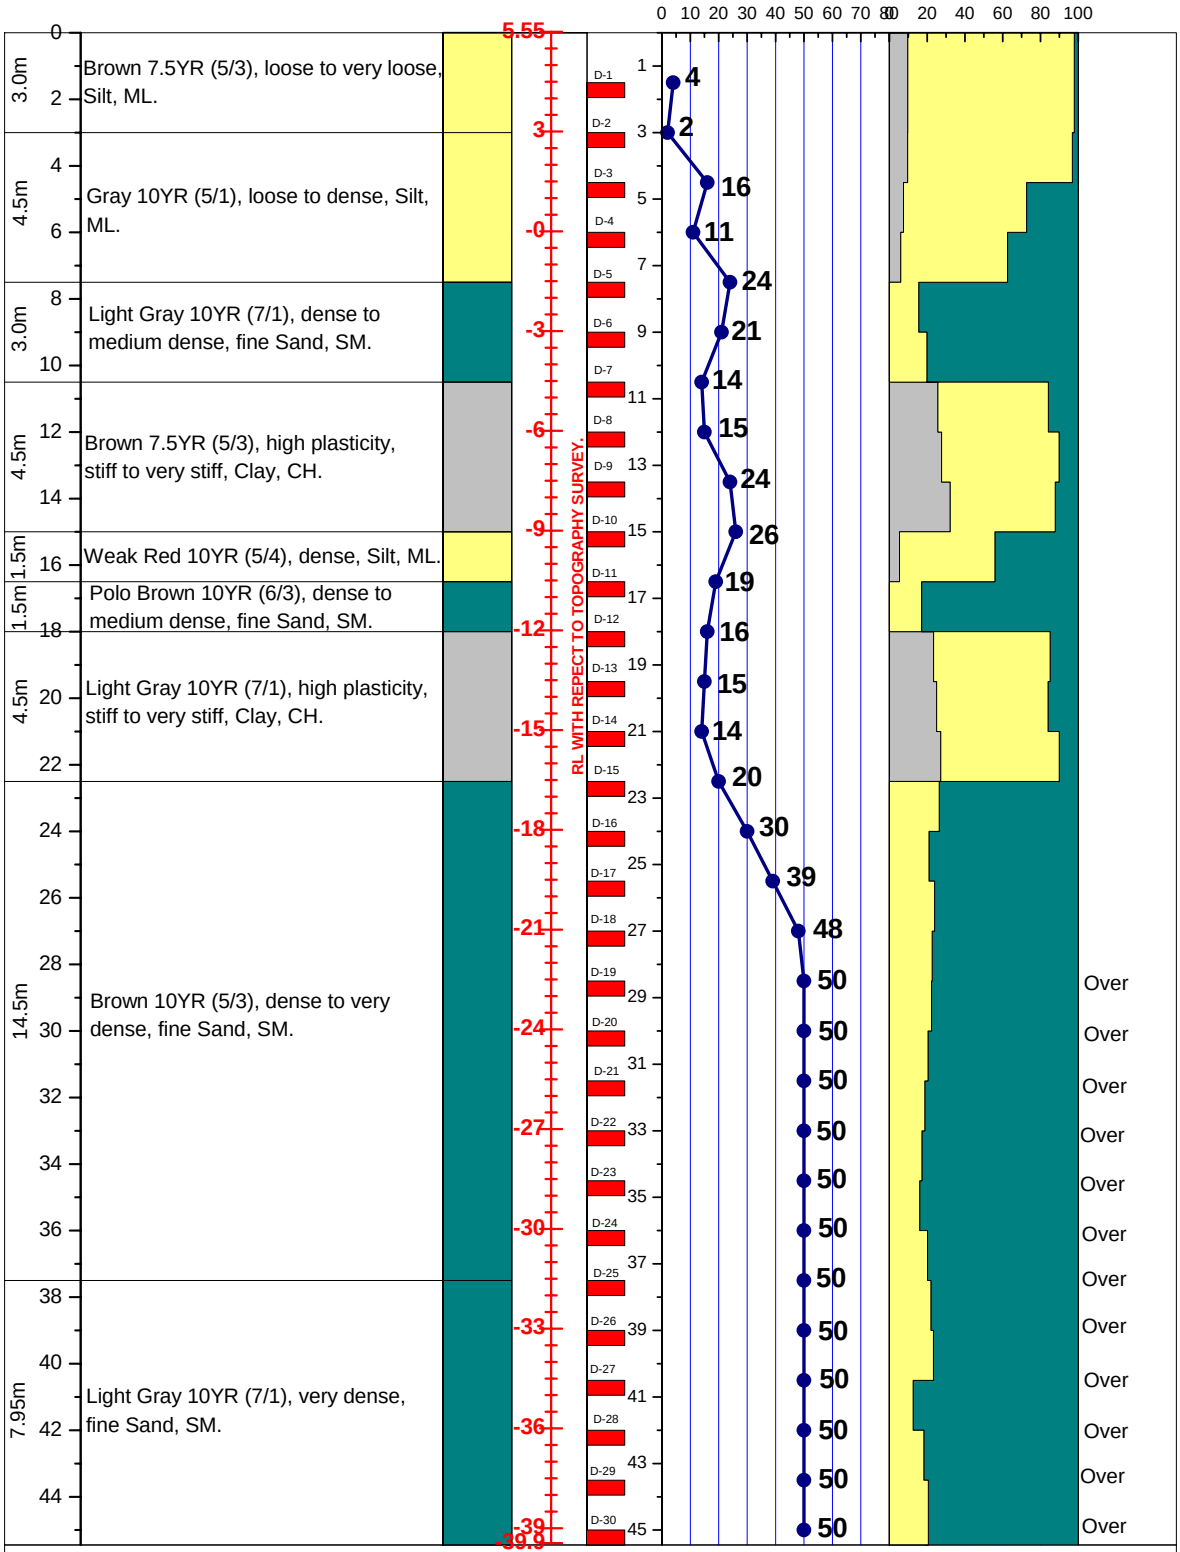

LEGEND FOR BORELOG AND GRAIN SIZE DISTRIBUTION (BASED ON 'ASTM CLASSIFICATION D-2487')

PLASTIC CLAY	SILT	PEAT/HIGHLY ORGANIC SOIL	UNDISTURBED SAMPLE
MICACEOUS FINE SAND/SILT	SAND	SHALE	DISTURBED SAMPLE

N- BLOWS DELIVERED PER FOOT BY A 140 LB HAMMER FALLING 30 INCHES

MAX^{m} PENETRATION= 50 BLOWS. AFTER 50 BLOWS PENETRATION DEPTH WERE MEASURED