A2	PROSOIL	BOREHOLE NO: BH-1	
		LOCATION : 2nd km for the Chainage 2+268 km on Raipura-Narsingdi-Madongonj Road (Raipura-Narsingdi-Portion), Narsingdi.	
PROJECT : Proposed Bridge.		DEPTH OF BORING : 30.0m	Chainage: 2+257 R. L. : 5.13
CLIENT : Road Division, Narsingdi.		DATE OF BORING : 26-07-2010.	G. W. T : 1.21m below from E.G.L.

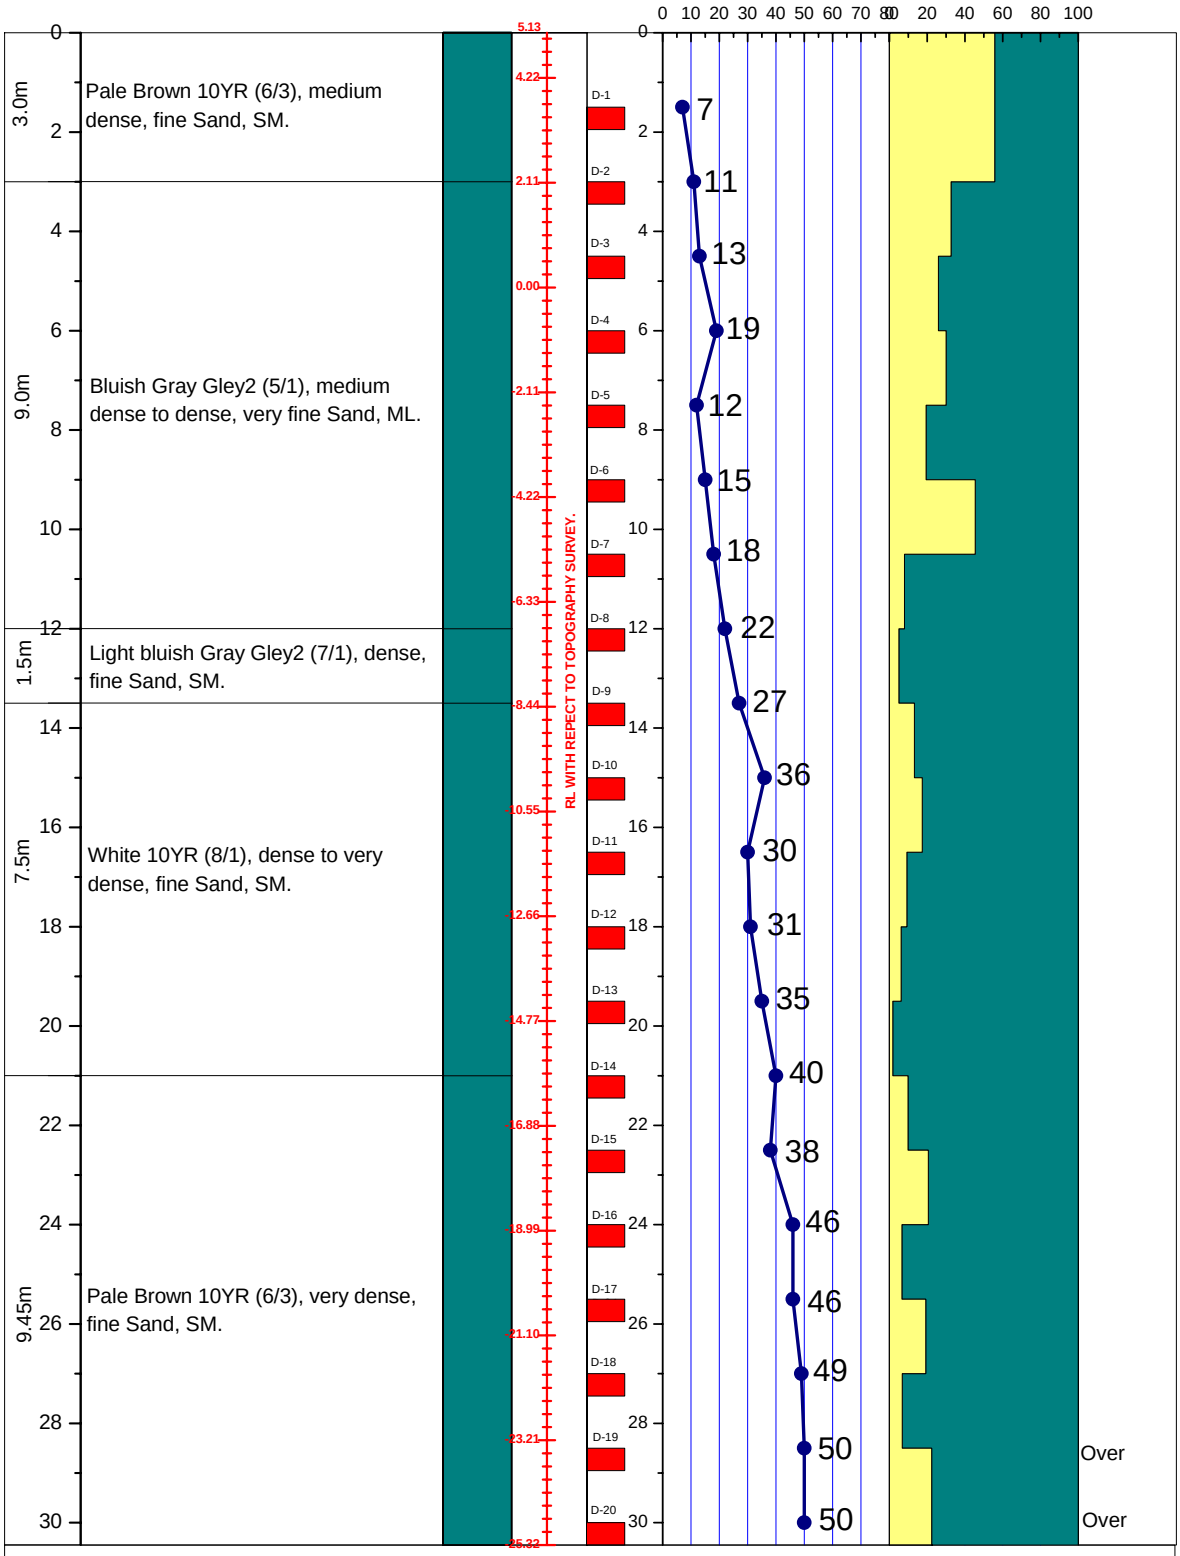

LEGEND FOR BORELOG AND GRAIN SIZE DISTRIBUTION (BASED ON 'ASTM CLASSIFICATION D-2487')

PLASTIC CLAY	SILT	PEAT/HIGHLY ORGANIC SOIL	UNDISTURBED SAMPLE
MICACEOUS FINE SAND/SILT	SAND	SHALE	DISTURBED SAMPLE

N- BLOWS DELIVERED PER FOOT BY A 140 LB HAMMER FALLING 30 INCHES

MAX^m PENETRATION= 50 BLOWS. AFTER 50 BLOWS PENETRATION DEPTH WERE MEASURED