A2 PROSOIL	BOREHOLE NO: BH-1	
	LOCATION : Naria Thana, Shariotpur.	
PROJECT : CIRCLE ASP OFFICE cum RESIDENCE.	DEPTH OF BORING : 30.0m	R. L.: 0.33m below from Road Level.
CLIENT : PWD.	DATE OF BORING: 1-09-2014.	B. W. T : 0.66m below from E.G.L.

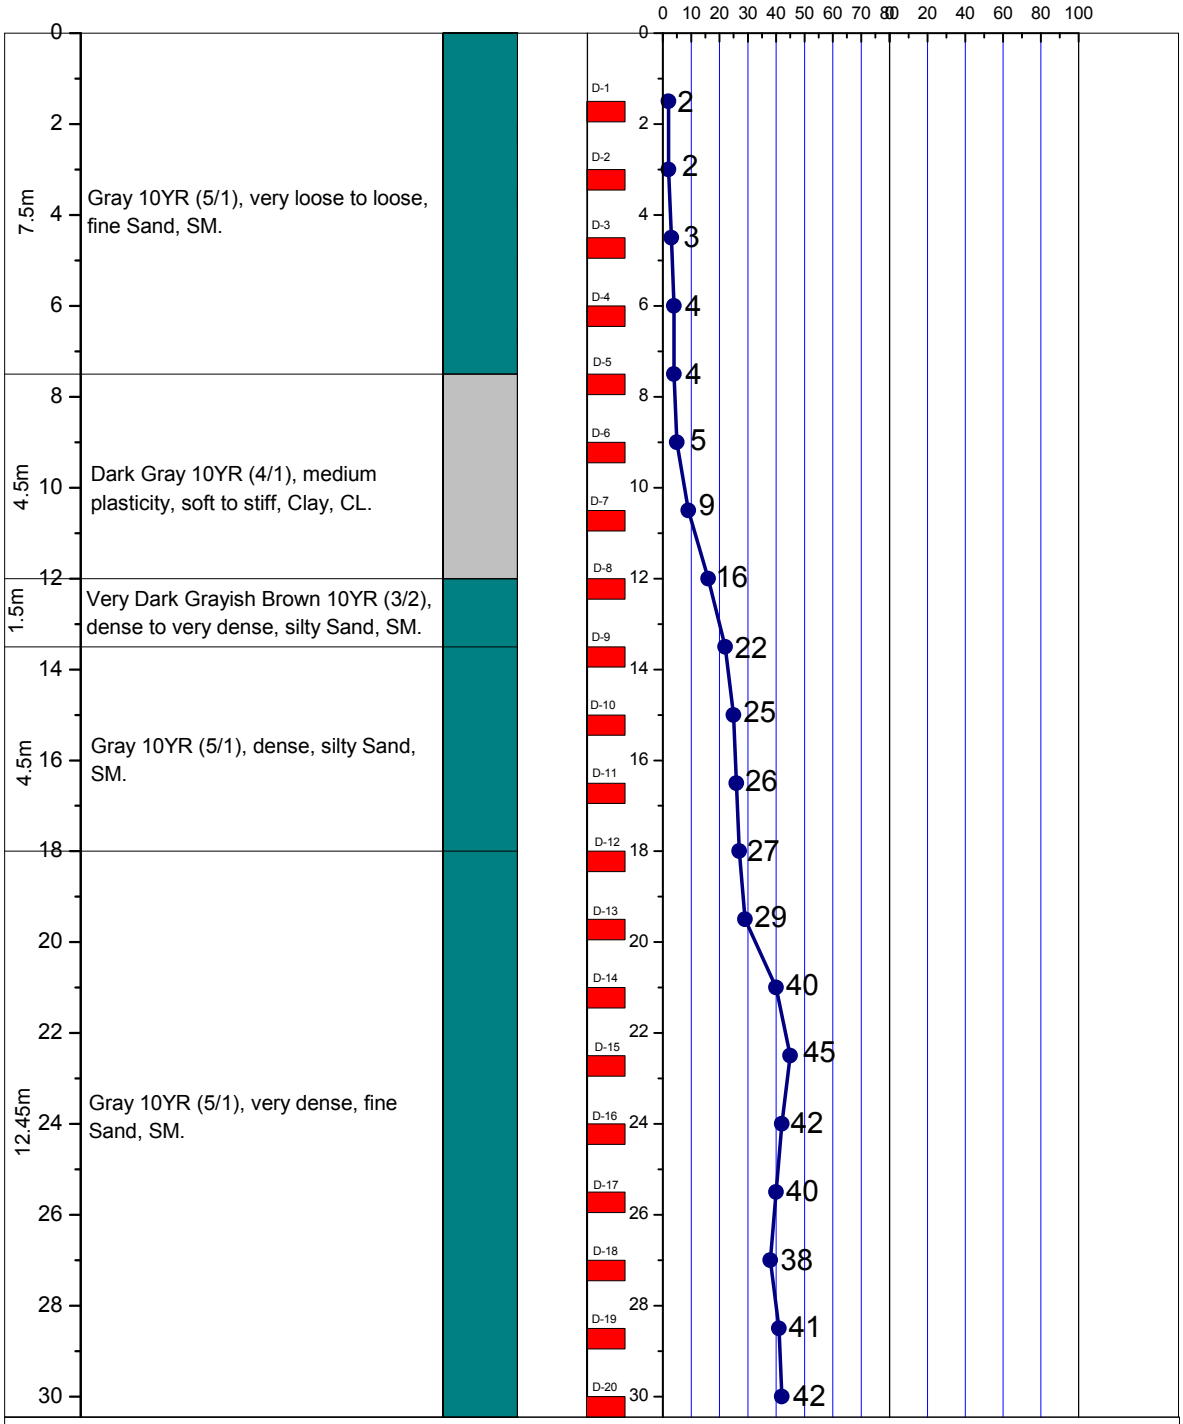

LEGEND FOR BORELOG AND GRAIN SIZE DISTRIBUTION (BASED ON 'ASTM CLASSIFICATION D-2487')

PLASTIC CLAY	SILT	SHALE	UNDISTURBED SAMPLE
MICACEOUS FINE SAND/SILT	SAND	PEAT/HIGHLY ORGANIC SOIL	DISTURBED SAMPLE

N- BLOWS DELIVERED PER FOOT BY A 140 LB HAMMER FALLING 30 INCHES

MAX^m PENETRATION= 50 BLOWS

AFTER 50 BLOWS PENETRATION DEPTH WERE MEASURED