
BORE LOGS FOR B.H. # 02

Co-ordinate:- E: 0756585
N: 2555256

Client : Bangladesh Road Research Laboratory (BRRL)
Project : Engineering Soil Mapping by Sub-Soil investigation
Location : At Borakhula (Narail-Mirjapur Road), Narail.

Method of boring : Mechanical Percussion Wash boring (water mixed with bentonite)
Diameter of the borehole : 100mm
Date : 03-05-2015 & 04-05-2015

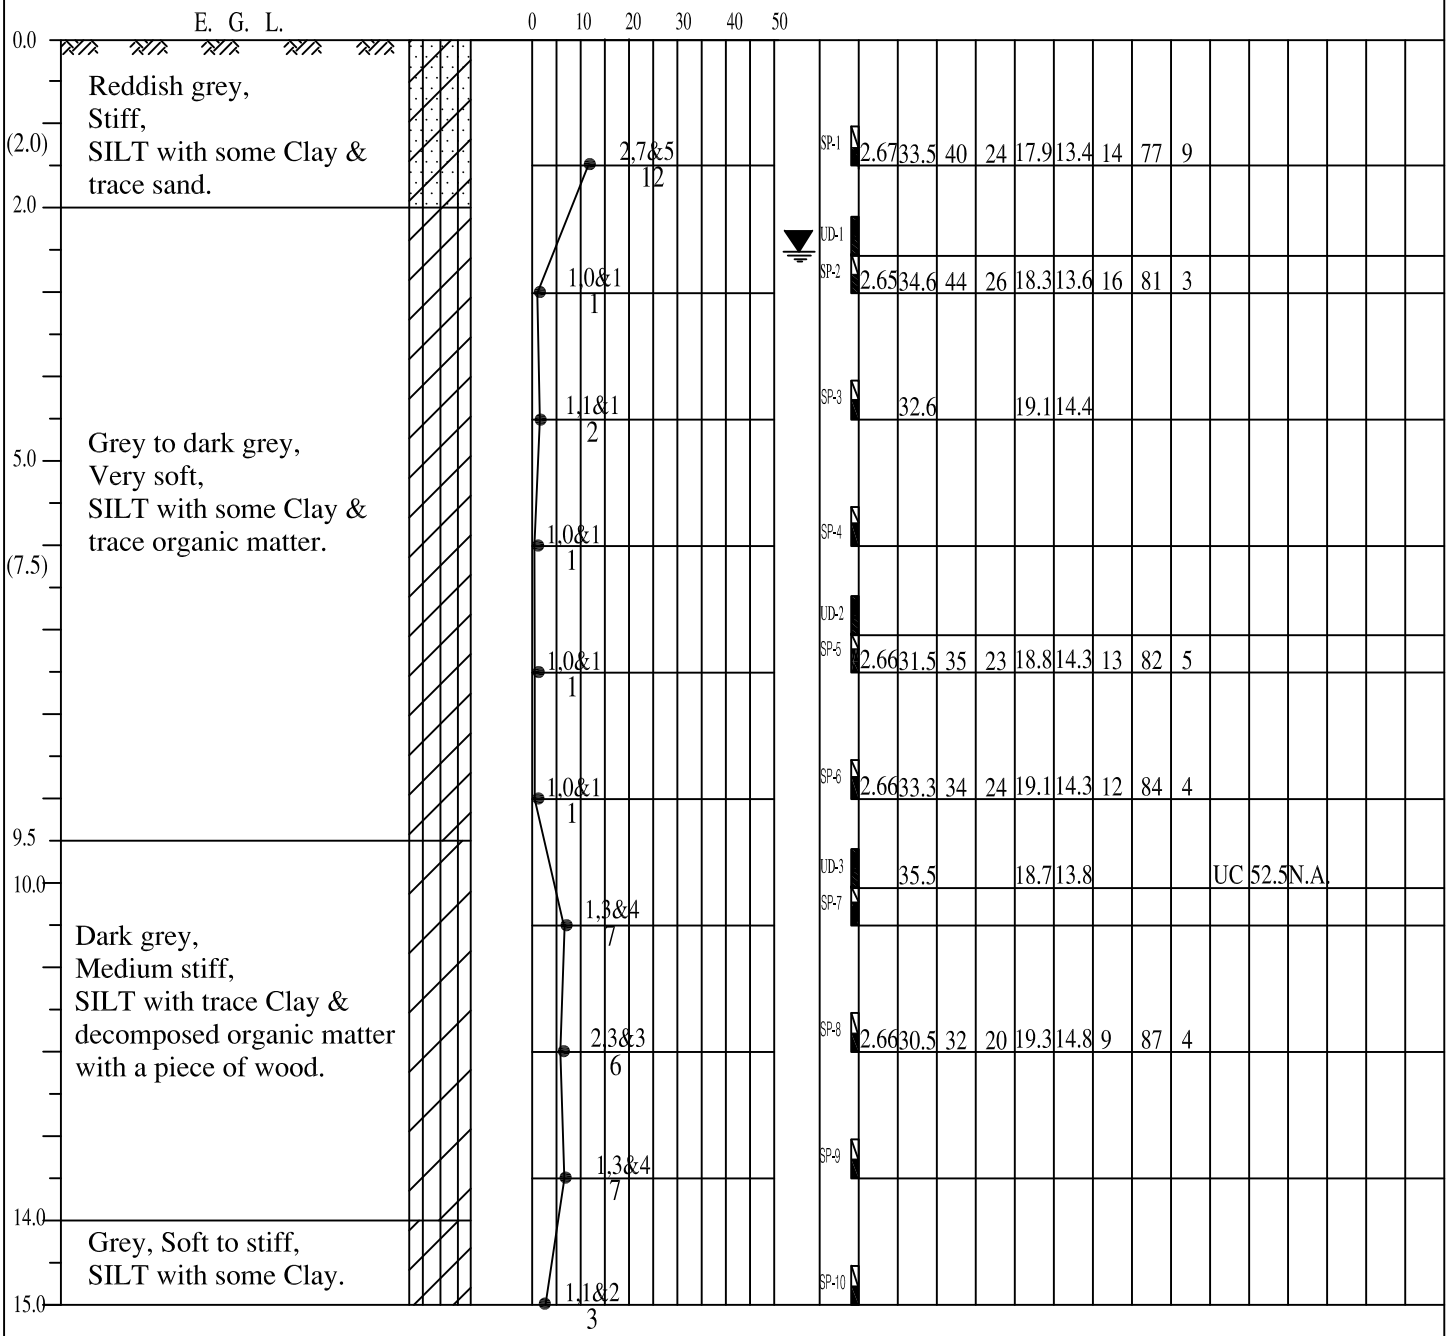

Depth (m) Thickness (m)	VISUAL CLASSIFICATION OF SOIL (Available soil samples)	LOG	R.L. (-) 0.65 (m)	STANDARD PENETRATION TEST RESULTS (N - VALUES)	G.W.T. 2.50 m (b) on 05-05	SAMPLING	G_s	W (%)	ATT. LIMITS L_w	ATT. LIMITS P_w	DENSITIES γ_w (kN/m³)	DENSITIES γ_d (kN/m³)	G.S.DISTRIBUTION CLAY (%)	G.S.DISTRIBUTION SILT (%)	G.S.DISTRIBUTION SAND (%)	SHEAR CHARACTERISTICS TYPE OF TEST	SHEAR CHARACTERISTICS C (kPa)	SHEAR CHARACTERISTICS ø (°)	CONSOLIDATION CHARACTERISTICS e_0	CONSOLIDATION CHARACTERISTICS C_c	CONSOLIDATION CHARACTERISTICS P_c (kPa)
0.0	Reddish grey, Stiff, SILT with some Clay & trace sand.			2,7&5 12		SP-1	2.67	33.5	40	24	17.9	13.4	14	77	9						
						UD-1															
(2.0)						SP-2	2.65	34.6	44	26	18.3	13.6	16	81	3						
2.0				1,0&1 1																	
				1,1&1 2		SP-3		32.6			19.1	14.4									
5.0	Grey to dark grey, Very soft, SILT with some Clay & trace organic matter.					SP-4															
				1,0&1 1																	
(7.5)						UD-2															
				1,0&1 1		SP-5	2.66	31.5	35	23	18.8	14.3	13	82	5						
				1,0&1 1		SP-6	2.66	33.3	34	24	19.1	14.3	12	84	4						
9.5						UD-3		35.5			18.7	13.8				UC	52.5	N.A.			
10.0	Dark grey, Medium stiff, SILT with trace Clay & decomposed organic matter with a piece of wood.			1,3&4 7		SP-7															
				2,3&3 6		SP-8	2.66	30.5	32	20	19.3	14.8	9	87	4						
				1,3&4 7		SP-9															
14.0	Grey, Soft to stiff, SILT with some Clay.																				
15.0				1,1&2 3		SP-10															

Cont'd...P/2

Note(s) :

1) G.W.T. is not dependable.
2) R.L. was taken from C/L of Narail-Mirjapur Road.
3) UD-01 collected from 2.10-2.55m, UD-02 collected from 16.60-7.05m & UD-03 collected from 9.60-10.05m, UD-04 collected from 23.10-23.55m & UD-05 collected from 35.10-35.55m depth.

M. AHMED & ASSOCIATES LTD., DHAKA.


Prepared by : H. Rahman	Checked. by : I. Ahmed	Date : 17-05-2015	Drg. No. :

BORE LOGS FOR B.H. # 02

Co-ordinate:- E: 0756585
N: 2555256

Client : Bangladesh Road Research Laboratory (BRRL)
Project : Engineering Soil Mapping by Sub-Soil investigation
Location : At Borakhula (Narail-Mirjapur Road), Narail.

Method of boring : Mechanical Percussion Wash boring (water mixed with bentonite)
Diameter of the borehole : 100mm
Date : 03-05-2015 & 04-05-2015

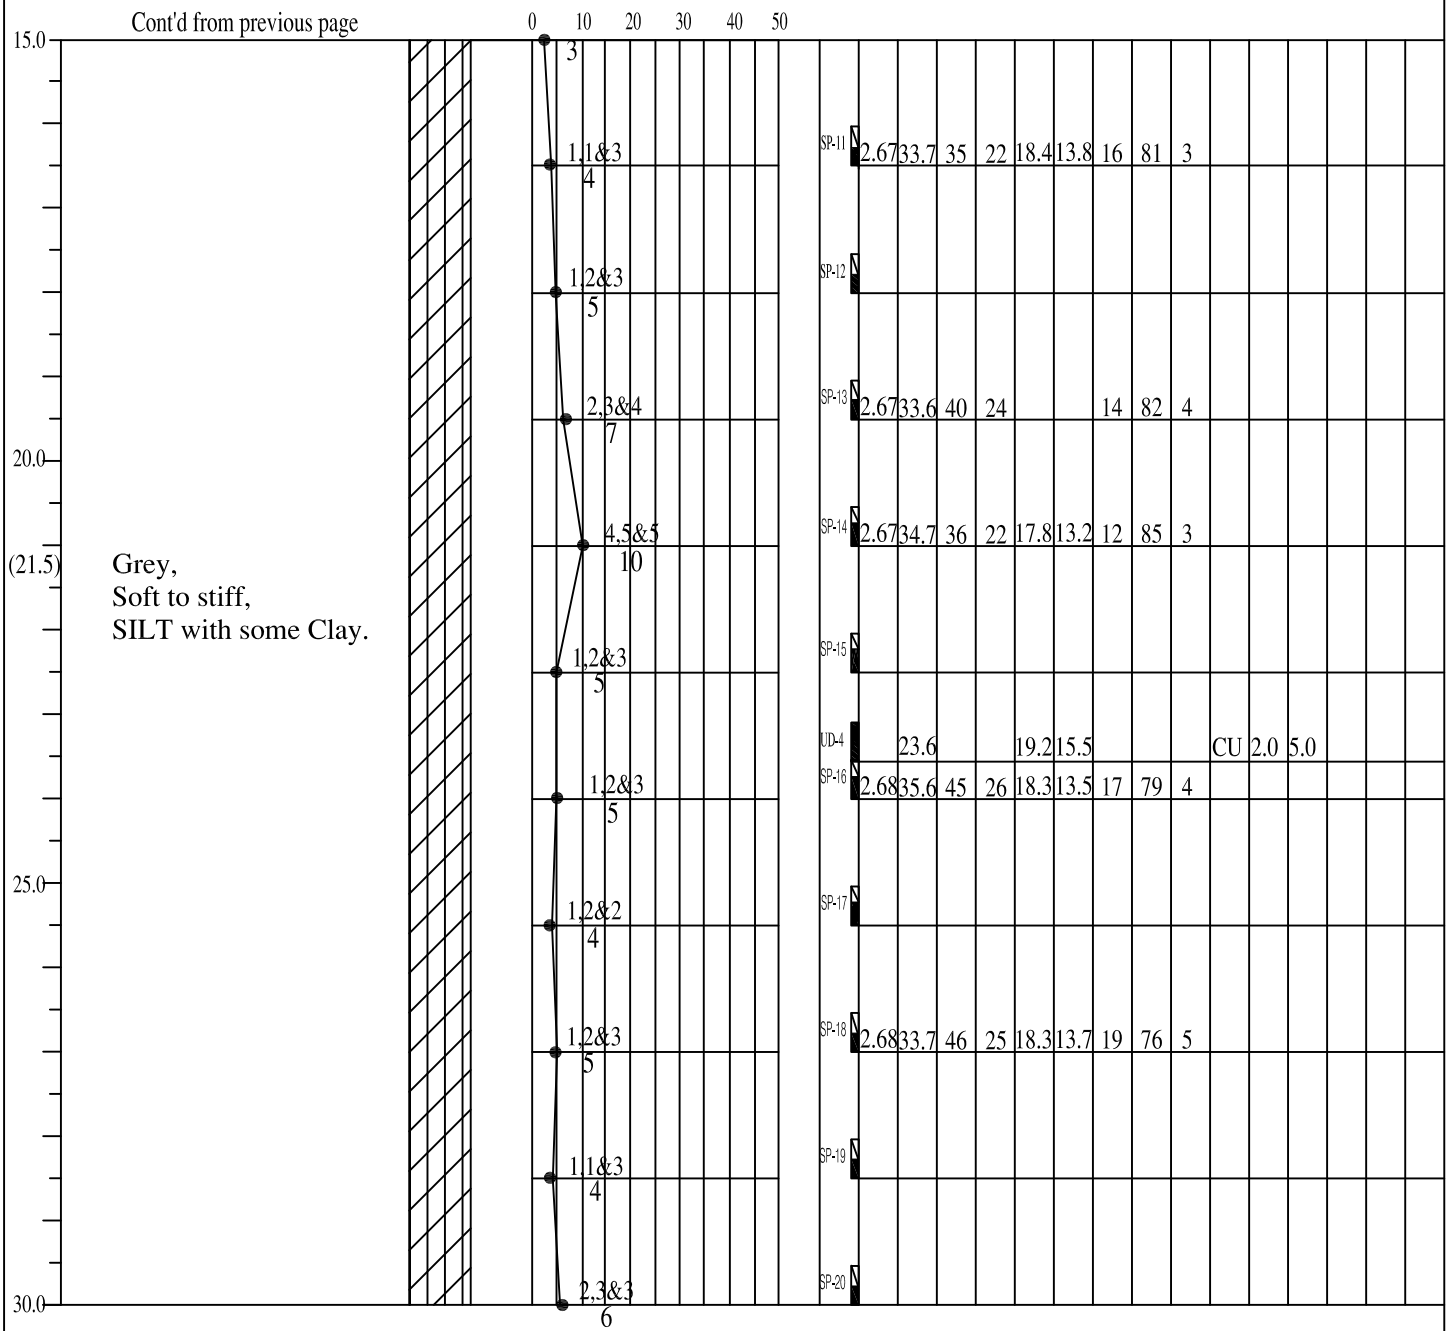

SUMMARY OF LABORATORY TEST RESULTS

Depth (m) / Thickness (m)	VISUAL CLASSIFICATION OF SOIL (Available soil samples)	LOG	STANDARD PENETRATION TEST RESULTS (N - VALUES)	SAMPLING	G_s	W (%)	ATT. LIMITS L_w	ATT. LIMITS P_w	DENSITIES γ_w (kN/m³)	DENSITIES γ_d (kN/m³)	G.S.DISTRIBUTION CLAY (%)	G.S.DISTRIBUTION SILT (%)	G.S.DISTRIBUTION SAND (%)	SHEAR CHARACTERISTICS TYPE OF TEST	SHEAR CHARACTERISTICS C (kPa)	SHEAR CHARACTERISTICS ø (°)	CONSOLIDATION CHARACTERISTICS e_0	CONSOLIDATION CHARACTERISTICS C_c	CONSOLIDATION CHARACTERISTICS P_c (kPa)
15.0	Cont'd from previous page		3																
			1,1&3 4	SP-11	2.67	33.7	35	22	18.4	13.8	16	81	3						
			1,2&3 5	SP-12															
			2,3&4 7	SP-13	2.67	33.6	40	24			14	82	4						
20.0			4,5&5 10	SP-14	2.67	34.7	36	22	17.8	13.2	12	85	3						
(21.5)	Grey, Soft to stiff, SILT with some Clay.		1,2&3 5	SP-15															
				UD-4		23.6			19.2	15.5				CU	2.0	5.0			
			1,2&3 5	SP-16	2.68	35.6	45	26	18.3	13.5	17	79	4						
25.0			1,2&2 4	SP-17															
			1,2&3 5	SP-18	2.68	33.7	46	25	18.3	13.7	19	76	5						
			1,1&3 4	SP-19															
30.0			2,3&3 6	SP-20															

Cont'd...P/3

M. AHMED & ASSOCIATES LTD., DHAKA.


Prepared by : H. Rahman	Checked. by : I. Ahmed	Date : 17-05-2015	Drg. No. :

BORE LOGS FOR B.H. # 02

Co-ordinate:- E: 0756585
N: 2555256

Client : Bangladesh Road Research Laboratory (BRRL)
Project : Engineering Soil Mapping by Sub-Soil investigation
Location : At Borakhula (Narail-Mirjapur Road), Narail.

Method of boring : Mechanical Percussion Wash boring (water mixed with bentonite)
Diameter of the borehole : 100mm
Date : 03-05-2015 & 04-05-2015

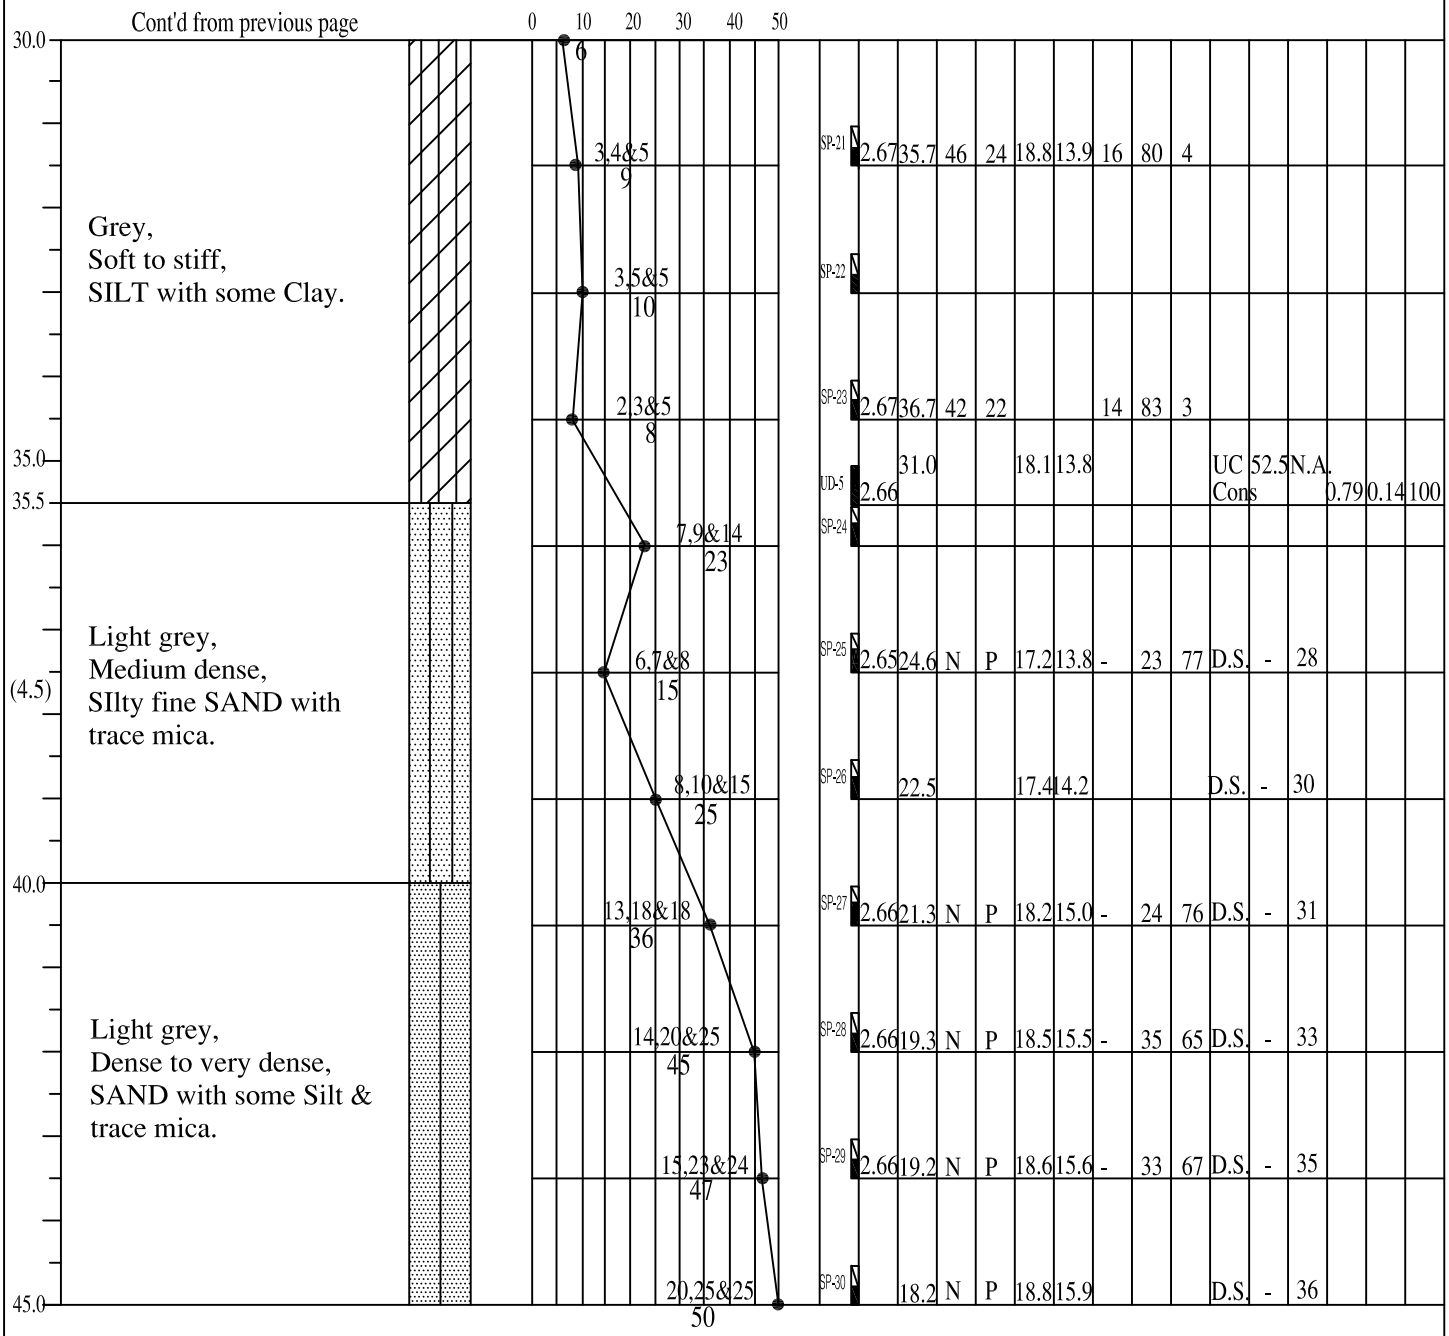

Depth (m) Thickness (m)	SAMPLING	G_s	W (%)	ATT. LIMITS L_w	ATT. LIMITS P_w	DENSITIES γ_w (kN/m³)	DENSITIES γ_d (kN/m³)	G.S.DISTRIBUTION CLAY (%)	G.S.DISTRIBUTION SILT (%)	G.S.DISTRIBUTION SAND (%)	SHEAR CHARACTERISTICS TYPE OF TEST	SHEAR CHARACTERISTICS C (kPa)	SHEAR CHARACTERISTICS ø (°)	CONSOLIDATION CHARACTERISTICS e_0	CONSOLIDATION CHARACTERISTICS C_c	CONSOLIDATION CHARACTERISTICS P_c (kPa)
	SP-21	2.67	35.7	46	24	18.8	13.9	16	80	4						
	SP-22															
	SP-23	2.67	36.7	42	22			14	83	3						
	UD-5	2.66	31.0			18.1	13.8				UC Cons	52.5	N.A.	0.79	0.14	100
	SP-24															
	SP-25	2.65	24.6	N	P	17.2	13.8	-	23	77	D.S.	-	28			
	SP-26		22.5			17.4	14.2				D.S.	-	30			
	SP-27	2.66	21.3	N	P	18.2	15.0	-	24	76	D.S.	-	31			
	SP-28	2.66	19.3	N	P	18.5	15.5	-	35	65	D.S.	-	33			
	SP-29	2.66	19.2	N	P	18.6	15.6	-	33	67	D.S.	-	35			
	SP-30		18.2	N	P	18.8	15.9				D.S.	-	36			

Cont'd...P/4

M. AHMED & ASSOCIATES LTD., DHAKA.

Prepared by : H. Rahman	Checked. by : I. Ahmed	Date : 17-05-2015	Drg. No. :

BORE LOGS FOR B.H. # 02

Co-ordinate:- E: 0756585
N: 2555256

Client : Bangladesh Road Research Laboratory (BRRL)
Project : Engineering Soil Mapping by Sub-Soil investigation
Location : At Borakhula (Narail-Mirjapur Road), Narail.

Method of boring : Mechanical Percussion Wash boring (water mixed with bentonite)
Diameter of the borehole : 100mm
Date : 03-05-2015 & 04-05-2015

Depth (m) Thickness (m)	VISUAL CLASSIFICATION OF SOIL (Available soil samples)	LOG	STANDARD PENETRATION TEST RESULTS (N - VALUES)	SAMPLING	SUMMARY OF LABORATORY TEST RESULTS																
					G_s	W	ATT. LIMITS		DENSITIES		G.S.DISTRIBUTION			SHEAR CHARACTERISTICS			CONSOLIDATION CHARACTERISTICS				
							L_w	P_w	γ_w	γ_d	CLAY	SILT	SAND	TYPE OF TEST	C	ø	e_0	C_c	P_c		
					–	(%)	–	–	(kN/m³)	(kN/m³)	(%)	(%)	(%)		(kPa)	(°)	–	–	(kPa)		
	Cont'd from previous page		0 10 20 30 40 50																		
45.0			50																		
	Light grey, Dense to very dense, SAND with some Silt & trace mica.		21,26&27	SP-31	2.66	18.0	N	P	19.0	16.1	-	30	70	D.S.	-	37					
			53																		
			20,26&26	SP-32	2.66	17.8	N	P	19.2	16.3	-	33	67	D.S.	-	39					
			52																		
			22,27&28	SP-33	2.65	19.5	N	P	19.0	15.9	-	28	72	D.S.	-	37					
			55																		
50.0			25,30&35	SP-34	2.65	19.2	N	P	19.2	16.1	-	25	75	D.S.	-	38					
51.0			65																		

END OF THE BOREHOLE

M. AHMED & ASSOCIATES LTD., DHAKA.

Prepared by : H. Rahman	Checked. by : I. Ahmed	Date : 17-05-2015	Drg. No. :