A2 PROSOIL	BOREHOLE NO: BH-1	
	LOCATION : Alladatpur, Narail.	
PROJECT : Proposed Five Storied Building.	DEPTH OF BORING : 15.0m	R. L.: On Road Level.
CLIENT : Faysal.	DATE OF BORING : 10-01-2012.	G. W. T : 2.74m below from E. G. L.

THICKNESS	SOIL STRATA	BORELOG	UNDISTURBED SAMPLE	DISTURBED SAMPLE	DEPTH (m) SPT VALUES (BLOWS / 300mm)	Grain Size Distribution, % Clay %, Silt %, Sand %	Max^{m} Penetration
2.0m	Brown 10YR (5/3), medium dense to loose, silty Sand, SM.			D-1, D-2	7, 3		
1.0m	Very pale Brown 10YR (8/3), loose to very loose, clayey Silt, ML.			D-3	1		
1.0m	Dark reddish Gray 10YR (4/1), loose to very loose, clayey Silt, ML.			D-4	5		
1.0m	Gray 10YR (5/1), loose to medium dense, silty Sand, SM.			D-5	9		
2.5m	Gray 10YR (5/1), medium dense to very dense, silty Sand (with mica), SM.			D-6, D-7	9, 39		
7.95m	Light gray 10YR (7/1), very dense, fine sand, SM.			D-8, D-9, D-10, D-11, D-12	40, 43, 41, 41, 42		

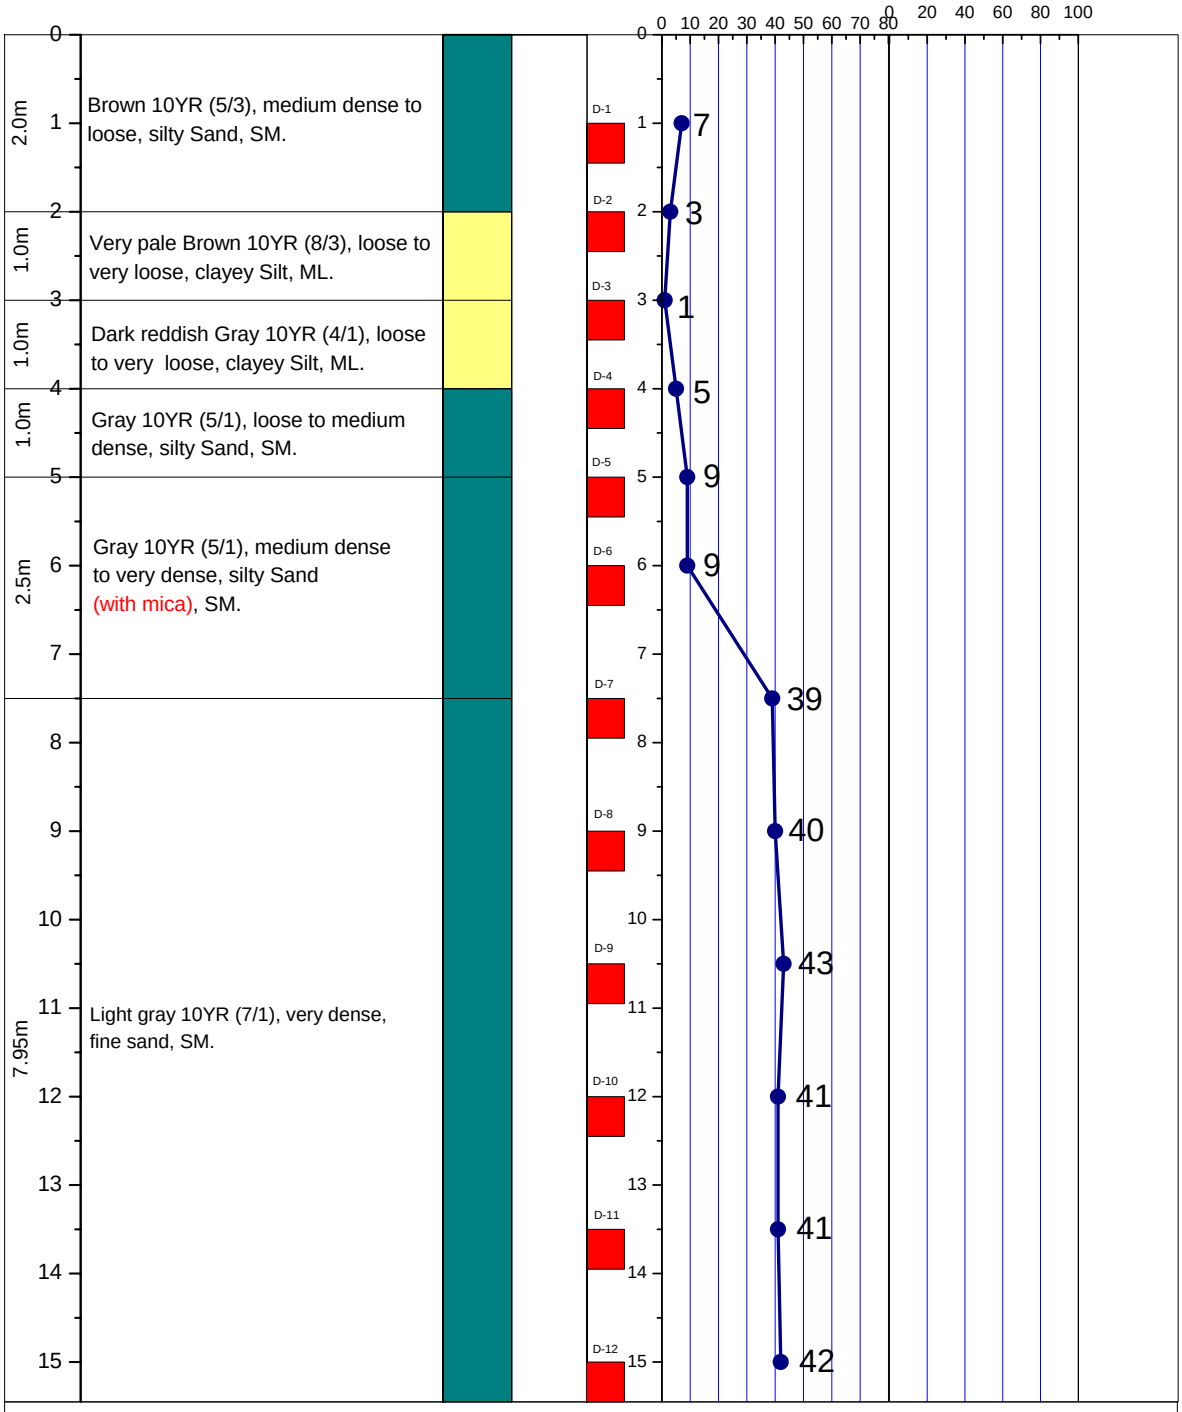

LEGEND FOR BORELOG AND GRAIN SIZE DISTRIBUTION (BASED ON 'ASTM CLASSIFICATION D-2487')

PLASTIC CLAY	SAND	SILT	SHALE
PEAT/HIGHLY ORGANIC SOIL	MICACEOUS FINE SAND/SILT	UNDISTURBED SAMPLE	DISTURBED SAMPLE

N- BLOWS DELIVERED PER FOOT BY A 140 LB HAMMER FALLING 30 INCHES

MAX^{m} PENETRATION= 50 BLOWS

AFTER 50 BLOWS PENETRATION DEPTH WERE MEASURED