
A2	PROSOIL	Borehole No: BH-01 (06N-03_A-1)	Easting: 402014.546	Northing: 858945.705
		Location: Abutment-A1 (Bahagili Bridge)		
Name of Project: Western Bangladesh Bridge Improvement Project.		Borehole Depth: 53.5m		R. L. : 35.53m
CLIENT: Roads and Highways Department.		Date of Boring: 10-12-2020 to 14-12-2020		B. W. T : 32.61m below from E. G. L.

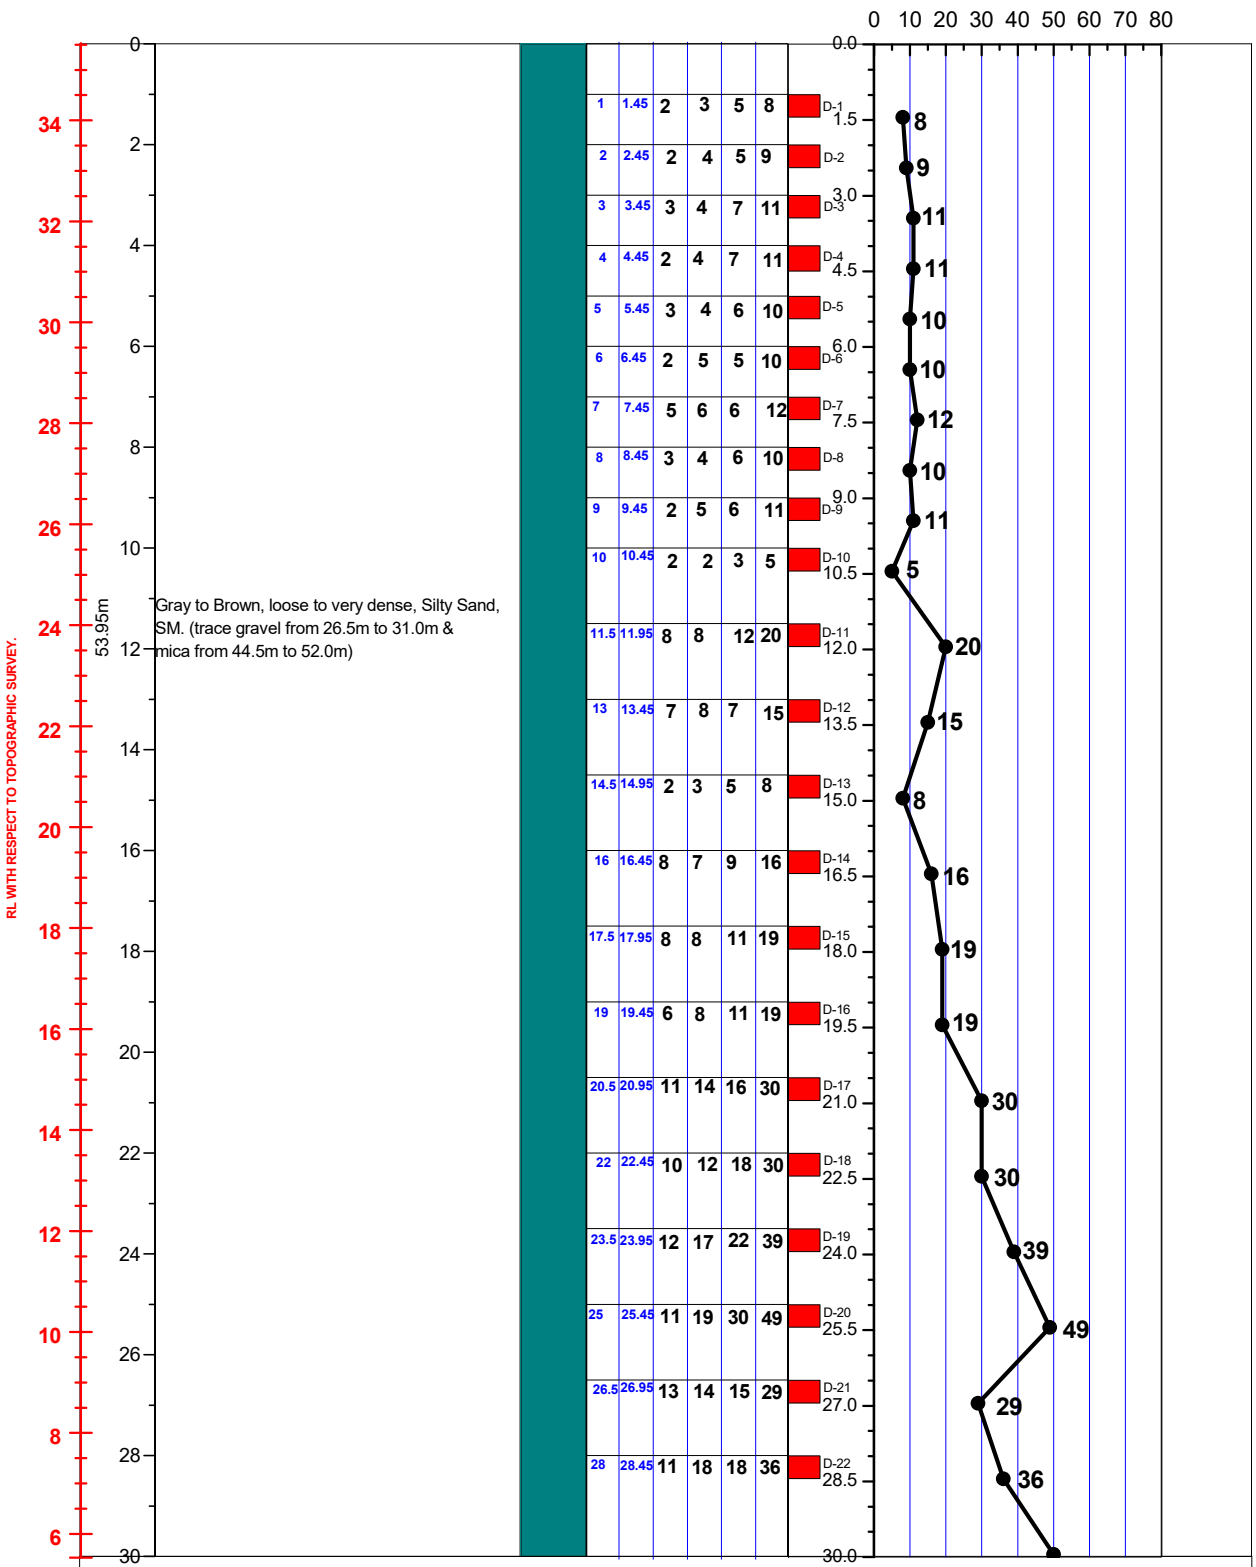


LEGEND FOR BORELOG AND GRAIN SIZE DISTRIBUTION (BASED ON 'ASTM CLASSIFICATION D-2487')

PLASTIC CLAY	SILT	PEAT/HIGHLY ORGANIC SOIL	UNDISTURBED SAMPLE
MICACEOUS FINE SAND/SILT	SAND	SHALE	DISTURBED SAMPLE

N- BLOWS DELIVERED PER FOOT BY A 140 LB HAMMER FALLING 30 INCHES

MAX^{m} PENETRATION= 50 BLOWS. AFTER 50 BLOWS PENETRATION DEPTH WERE MEASURED

A2	PROSOIL	Borehole No: BH-01 (06N-03_A-1)	Easting: 402014.546	Northing: 858945.705
		Location: Abutment-A1 (Bahagili Bridge)		
Name of Project: Western Bangladesh Bridge Improvement Project.		Borehole Depth: 53.5m		R. L. : 35.53m
CLIENT: Roads and Highways Department.		Date of Boring: 10-12-2020 to 14-12-2020		B. W. T : 32.61m below from E. G. L.

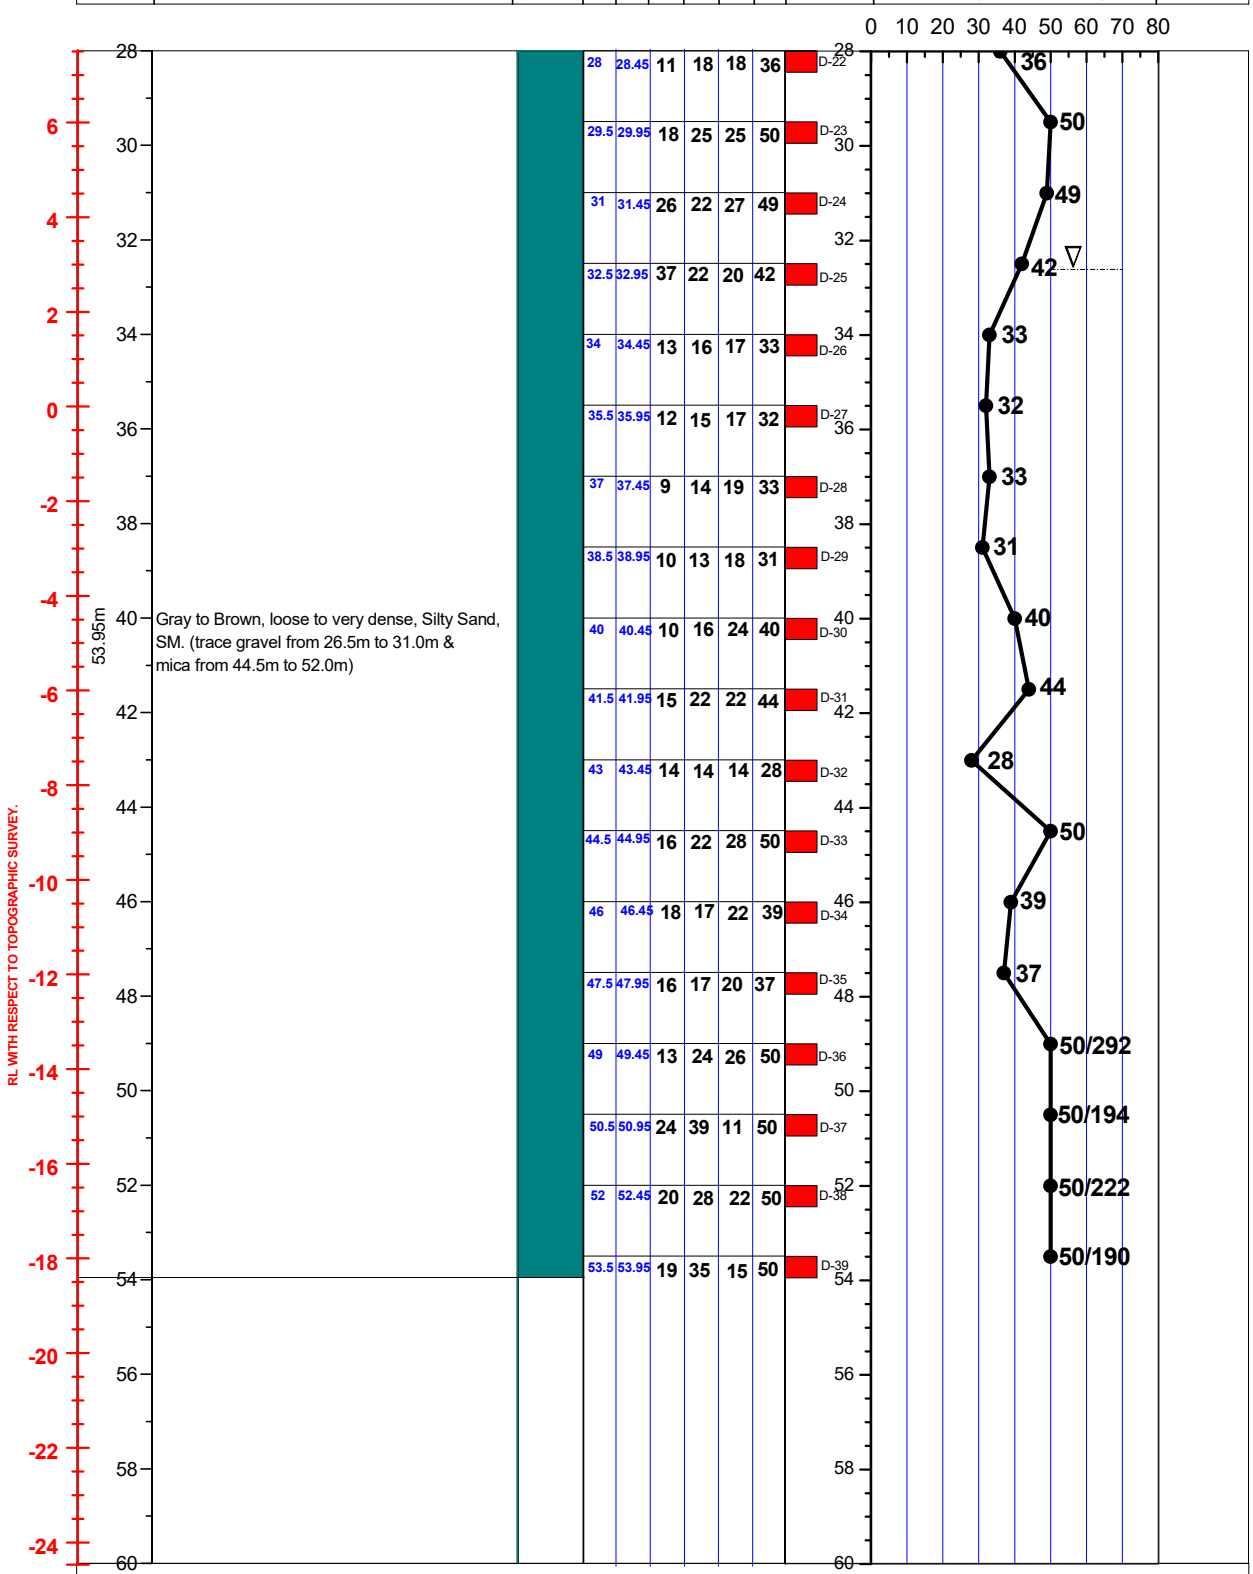

LEGEND FOR BORELOG AND GRAIN SIZE DISTRIBUTION (BASED ON 'ASTM CLASSIFICATION D-2487')

PLASTIC CLAY | SILT | PEAT/HIGHLY ORGANIC SOIL | UNDISTURBED SAMPLE

MICACEOUS FINE SAND/SILT | SAND | SHALE | DISTURBED SAMPLE

N- BLOWS DELIVERED PER FOOT BY A 140 LB HAMMER FALLING 30 INCHES

MAX^{m} PENETRATION= 50 BLOWS. AFTER 50 BLOWS PENETRATION DEPTH WERE MEASURED