B	PROSOIL	BOREHOLE NO: BH-1	
		LOCATION : 29th Km Of Assasuni-Paikgacha Road, Satkhira.	
PROJECT : Proposed Manikkhali Bridge Over Khulpetua River.		DEPTH OF BORING : 51.0m	Chainage: 28+282 R. L. : 2.23
CLIENT : Road Division, Satkhira.		DATE OF BORING : 26-05-2012.	G. W. T : 0.91m above from E.G.L.

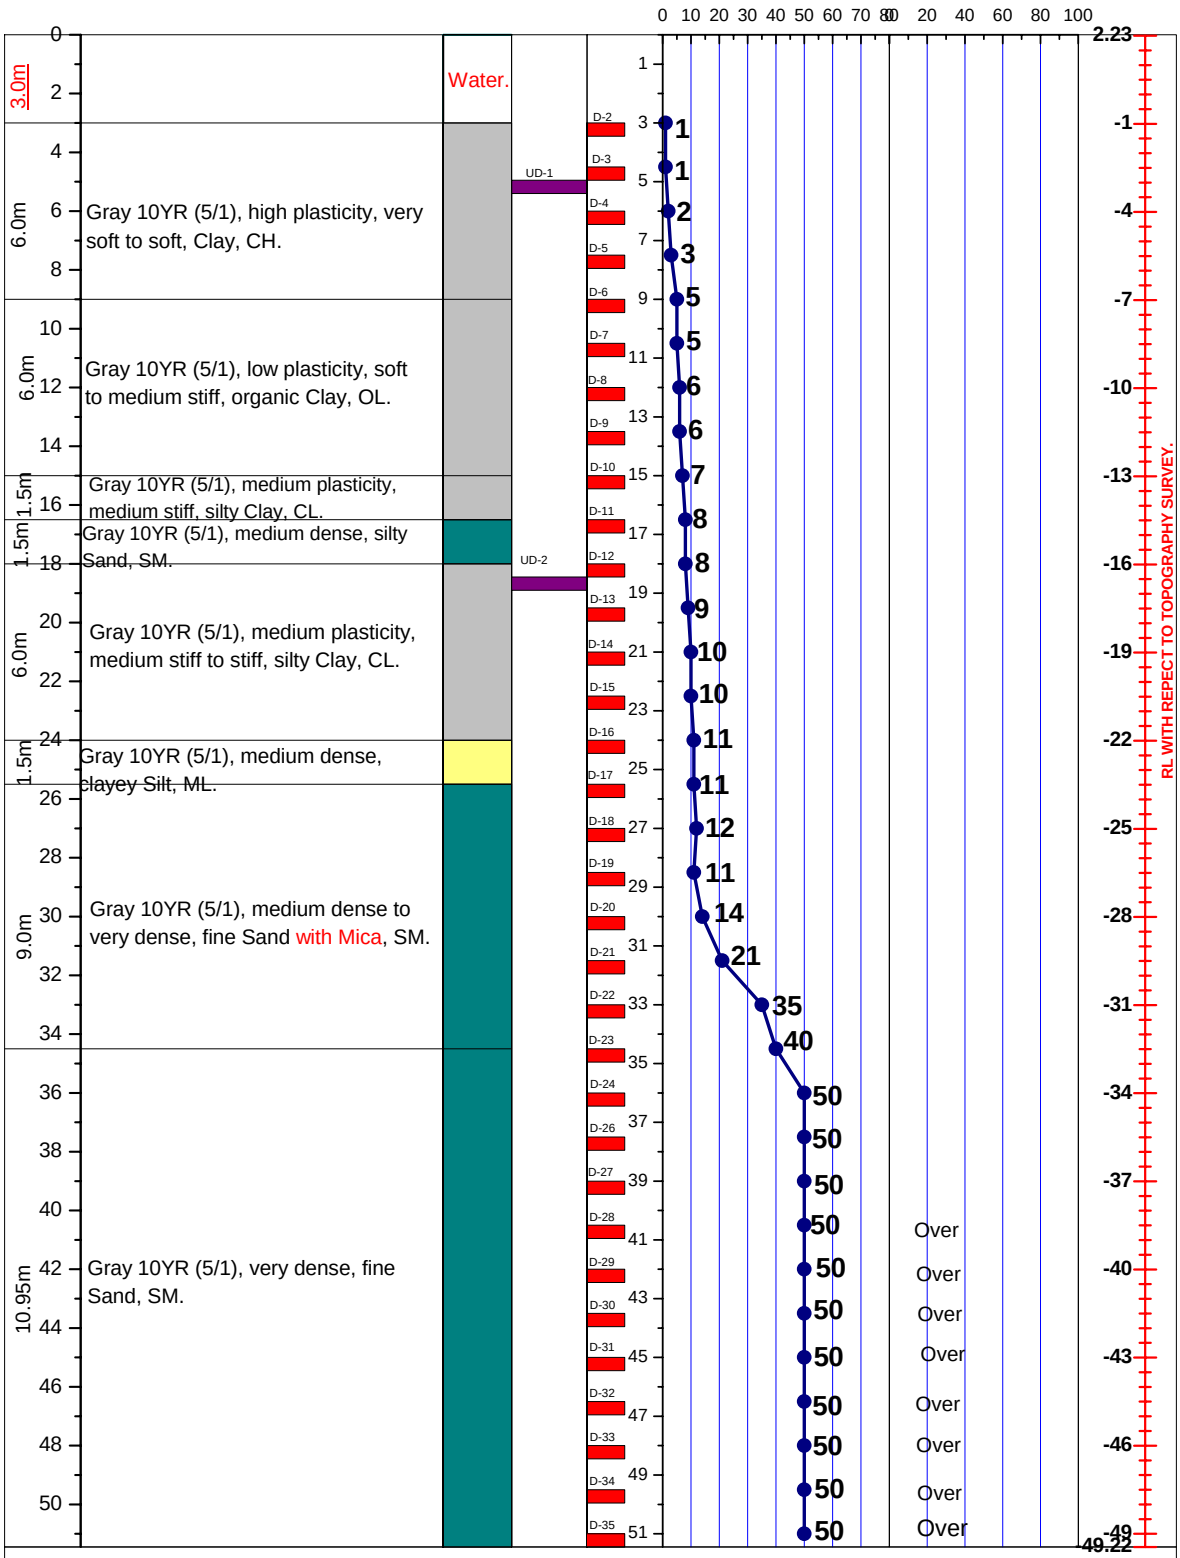

LEGEND FOR BORELOG AND GRAIN SIZE DISTRIBUTION (BASED ON 'ASTM CLASSIFICATION D-2487')

PLASTIC CLAY	SILT	PEAT/HIGHLY ORGANIC SOIL	UNDISTURBED SAMPLE
MICACEOUS FINE SAND/SILT	SAND	SHALE	DISTURBED SAMPLE

N- BLOWS DELIVERED PER FOOT BY A 140 LB HAMMER FALLING 30 INCHES

MAXm PENETRATION= 50 BLOWS. AFTER 50 BLOWS PENETRATION DEPTH WERE MEASURED