A2	SOIL & PILE TEST.COM	BOREHOLE NO: BH-1	
		LOCATION : Railway Overpass (from 1+025.18 to 1+570.56) on B.Baria-Comilla Road.	
PROJECT : Proposed Railway Overpass (1+025.18 to 1+570.56).		DEPTH OF BORING : 36.0m	Chainage: 1+570.56 R. L. : 7.242
CLIENT : Road Division, Brahmanbaria.		DATE OF BORING : 22-04-2011.	G. W. T : 2.44m below from E.G.L.

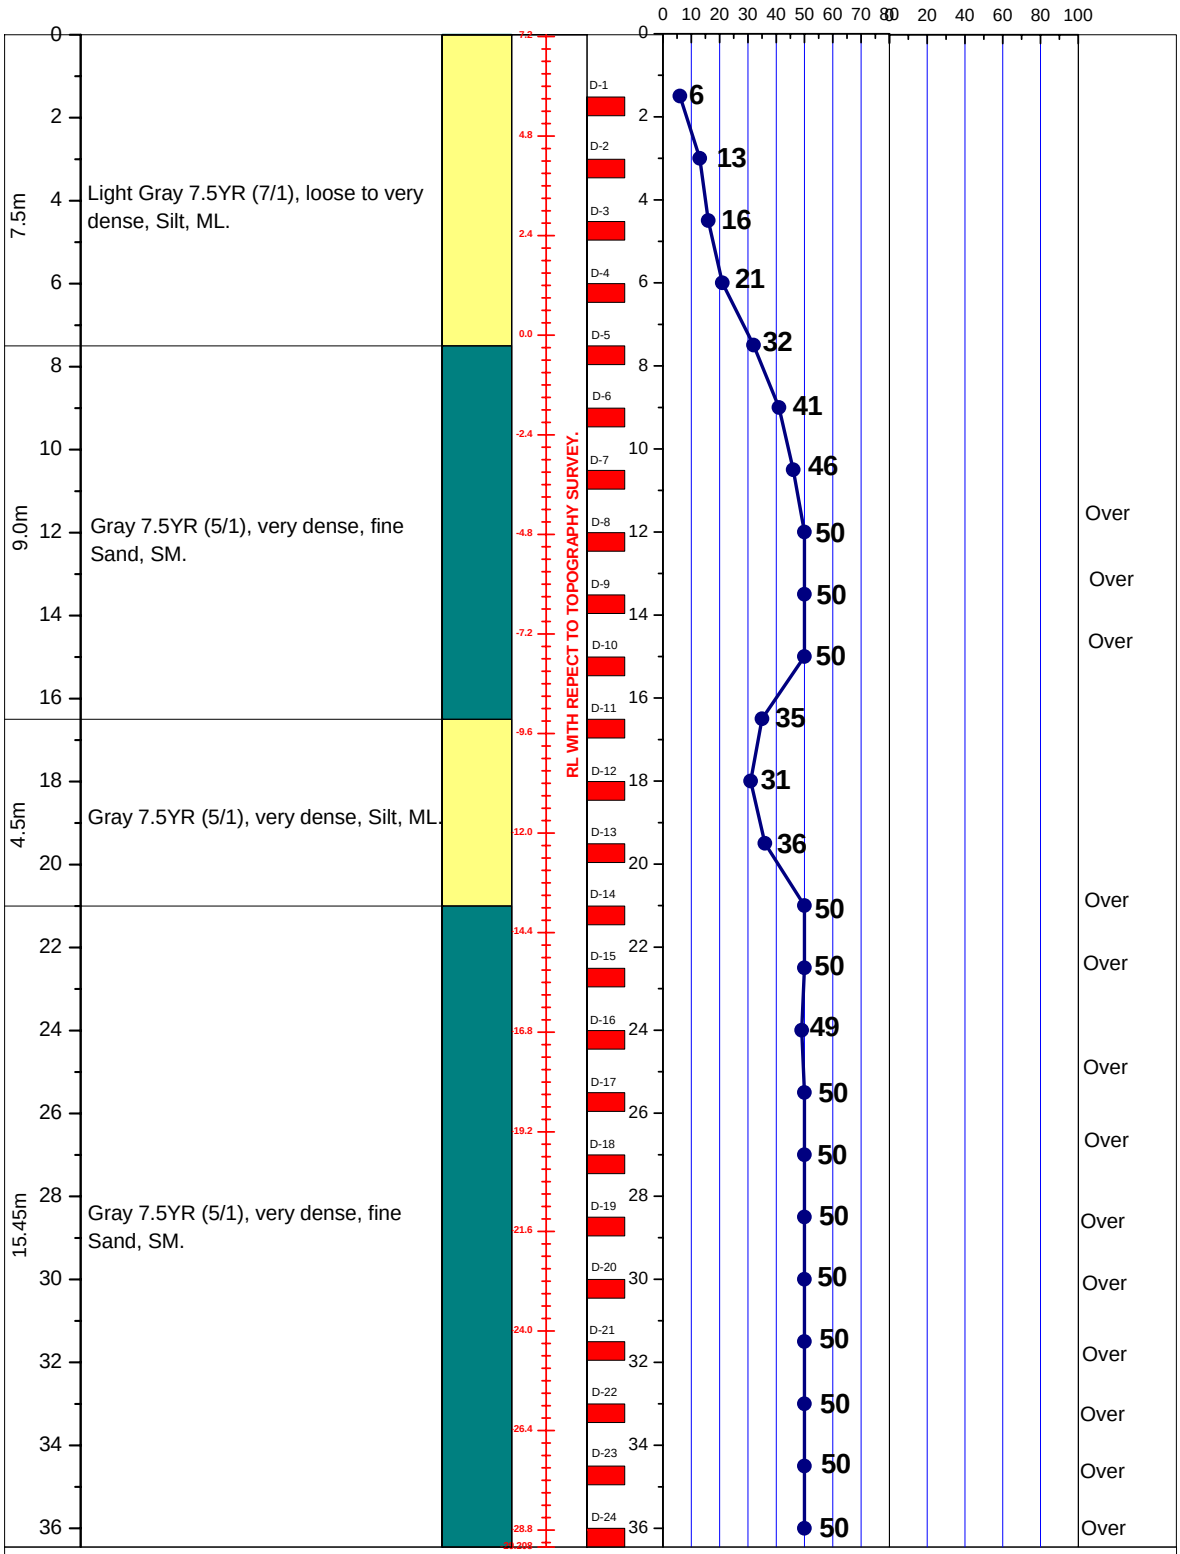

LEGEND FOR BORELOG AND GRAIN SIZE DISTRIBUTION (BASED ON 'ASTM CLASSIFICATION D-2487')

PLASTIC CLAY	SILT	PEAT/HIGHLY ORGANIC SOIL	UNDISTURBED SAMPLE
MICACEOUS FINE SAND/SILT	SAND	SHALE	DISTURBED SAMPLE

N- BLOWS DELIVERED PER FOOT BY A 140 LB HAMMER FALLING 30 INCHES

MAX^m PENETRATION= 50 BLOWS. AFTER 50 BLOWS PENETRATION DEPTH WERE MEASURED