
A2 PROSOIL	BOREHOLE NO: BH-1	
	LOCATION : Baitul Izzat, Shatkania, Chittagong.	
PROJECT : Telecommunication Tower.	DEPTH OF BORING : 51.0m	R. L.: 1.21m below from Road Level.
CLIENT : TM International, Bangladesh Ltd.	DATE OF BORING : 15-02-2009.	G. W. T : 0.91m below from E. G. L.

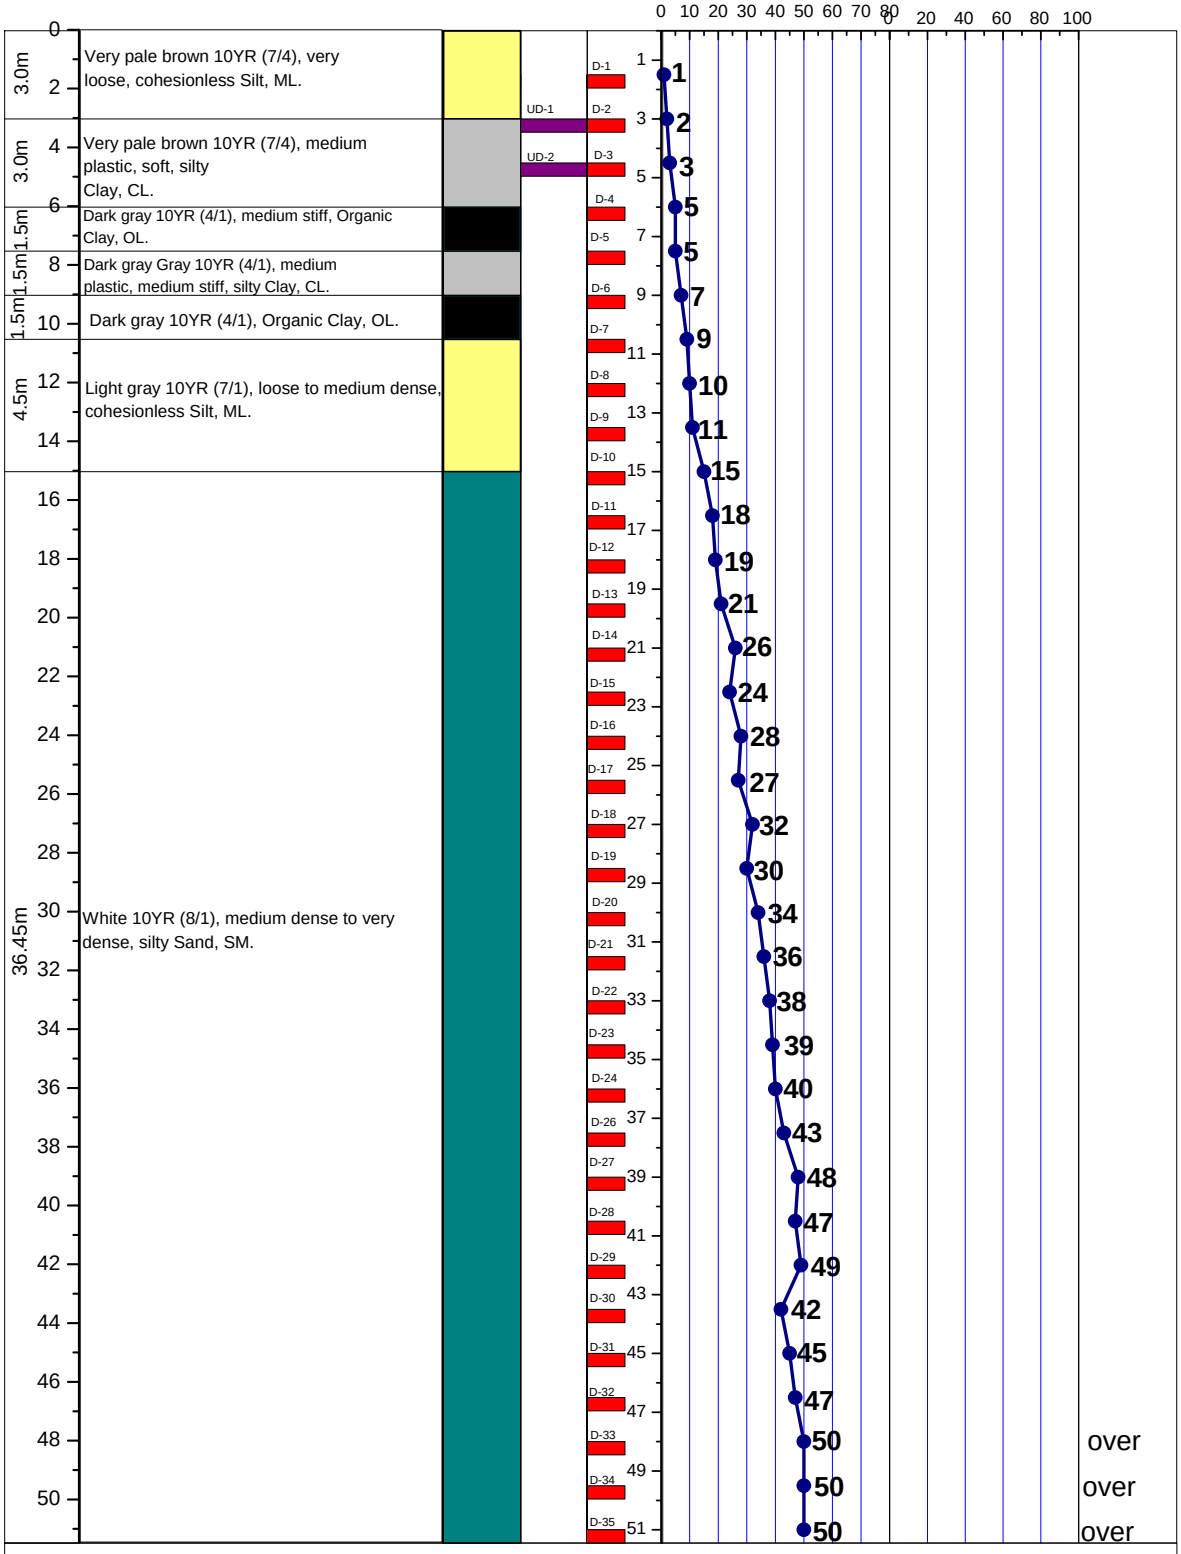


LEGEND FOR BORELOG AND GRAIN SIZE DISTRIBUTION (BASED ON 'ASTM CLASSIFICATION D-2487')

PLASTIC CLAY	SILT	PEAT/HIGHLY ORGANIC SOIL	UNDISTURBED SAMPLE
MICACEOUS FINE SAND/SILT	SAND	SHALE	DISTURBED SAMPLE

N- BLOWS DELIVERED PER FOOT BY A 140 LB HAMMER FALLING 30 INCHES

MAX^{m} PENETRATION= 50 BLOWS. AFTER 50 BLOWS PENETRATION DEPTH WERE MEASURED

A2	PROSOIL	BOREHOLE NO: BH-1	
		LOCATION : Boalkhali, Chittagong.	
PROJECT : Telecommunication Tower.		DEPTH OF BORING : 51.0m	R. L.: 0.45m below from Road Level.
CLIENT : Grameenphone Ltd.		DATE OF BORING : 18-04-2007.	G. W. T : 3.05m below from E. G. L.

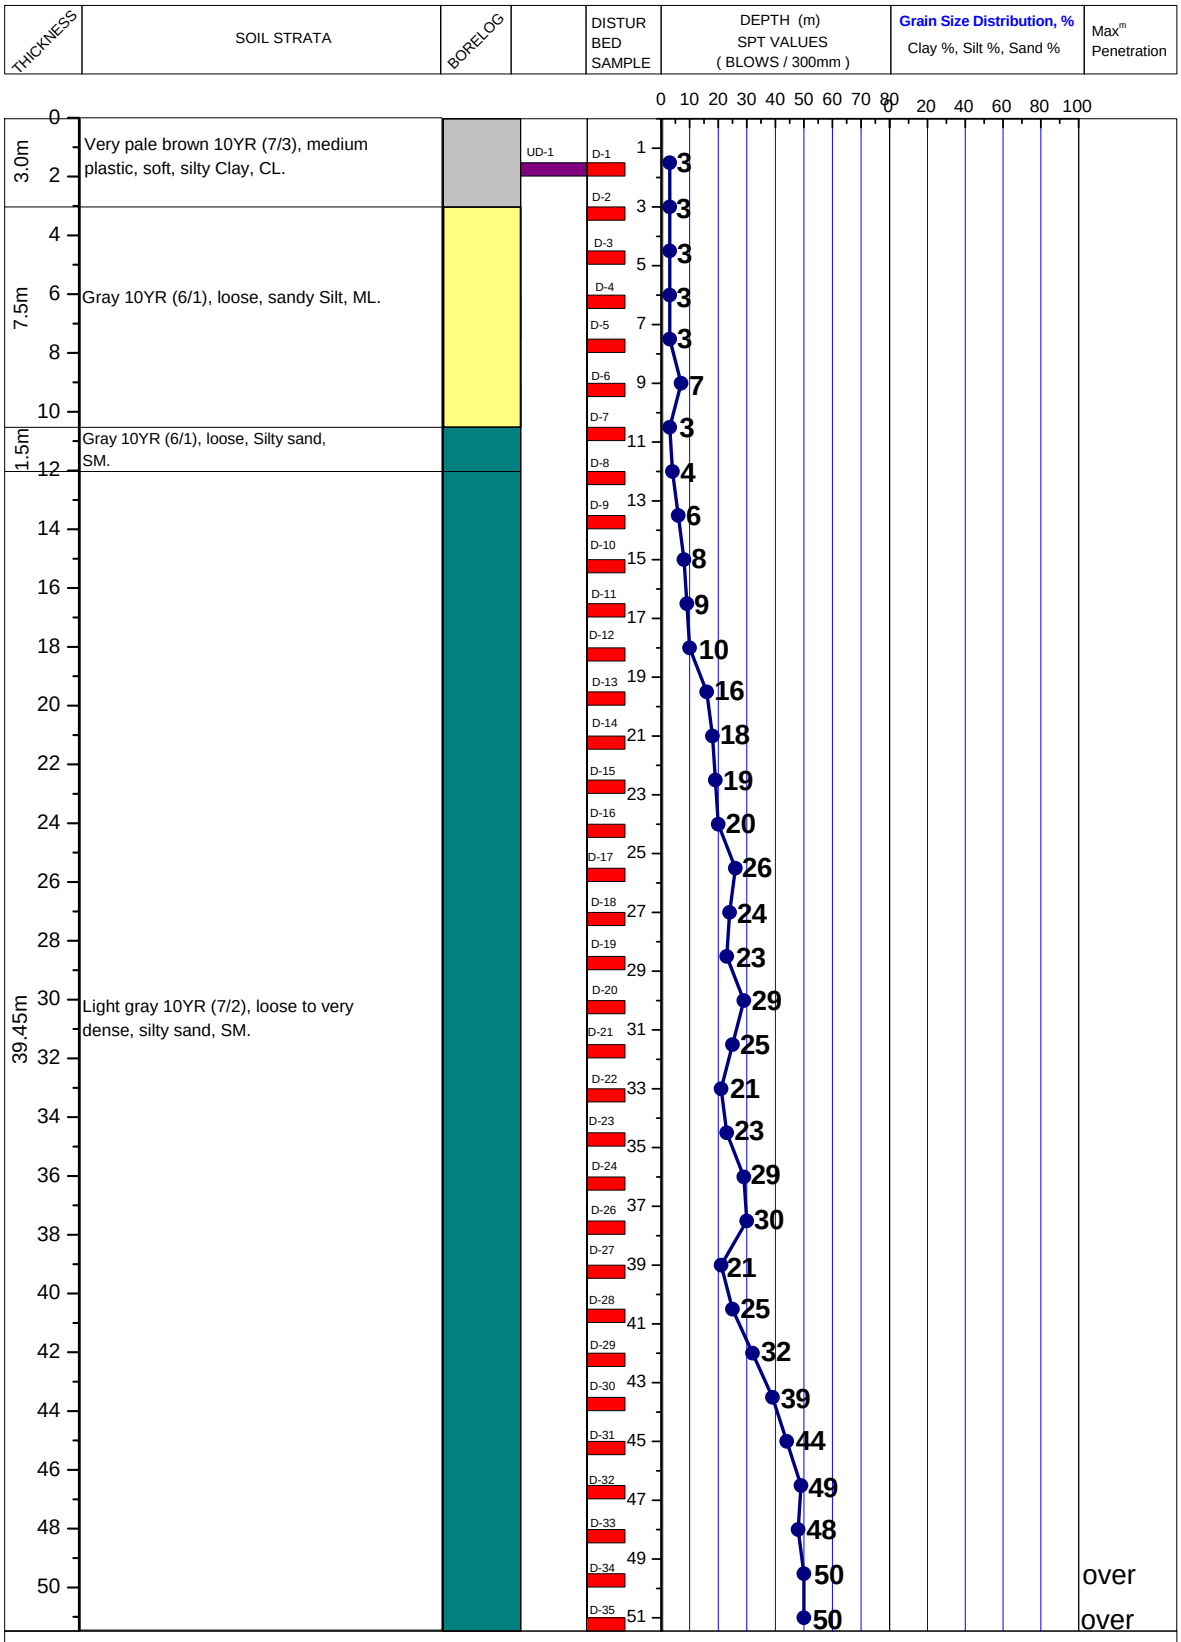


LEGEND FOR BORELOG AND GRAIN SIZE DISTRIBUTION (BASED ON 'ASTM CLASSIFICATION D-2487')

PLASTIC CLAY	SILT	PEAT/HIGHLY ORGANIC SOIL	UNDISTURBED SAMPLE
MICACEOUS FINE SAND/SILT	SAND	SHALE	DISTURBED SAMPLE

N- BLOWS DELIVERED PER FOOT BY A 140 LB HAMMER FALLING 30 INCHES

MAX^{m} PENETRATION= 50 BLOWS. AFTER 50 BLOWS PENETRATION DEPTH WERE MEASURED

A2 PROSOIL	BOREHOLE NO: BH-1	
	LOCATION : Chandanaish, Chittagong.	
PROJECT : Telecommunication Tower.	DEPTH OF BORING : 51.0m	R. L.: 1.07m below from Road Level.
CLIENT : Grameenphone Ltd.	DATE OF BORING : 17-04-2007.	G. W. T : Rain Water.

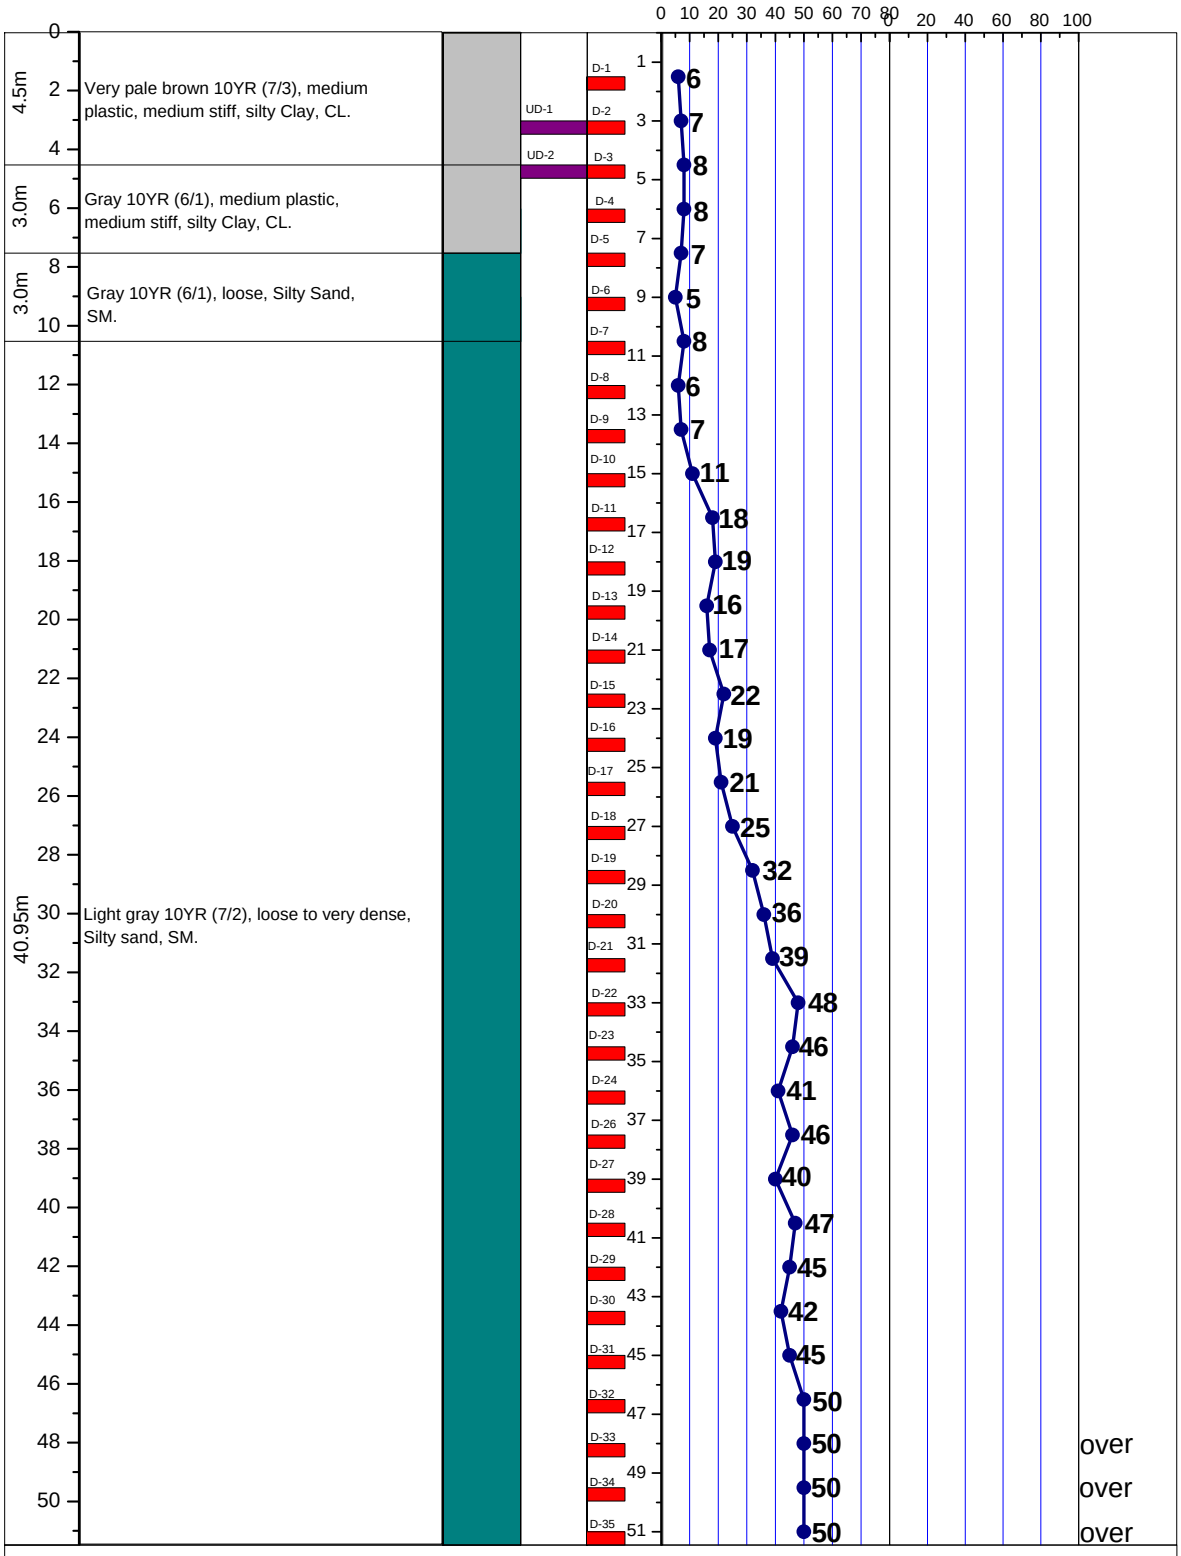


LEGEND FOR BORELOG AND GRAIN SIZE DISTRIBUTION (BASED ON 'ASTM CLASSIFICATION D-2487')

PLASTIC CLAY	SILT	PEAT/HIGHLY ORGANIC SOIL	UNDISTURBED SAMPLE
MICACEOUS FINE SAND/SILT	SAND	SHALE	DISTURBED SAMPLE

N- BLOWS DELIVERED PER FOOT BY A 140 LB HAMMER FALLING 30 INCHES

MAX^{m} PENETRATION= 50 BLOWS. AFTER 50 BLOWS PENETRATION DEPTH WERE MEASURED

A2 PROSOIL	BOREHOLE NO: BH-1	
	LOCATION : Holudia, Satkania, Chittagong.	
PROJECT : Telecommunication Tower.	DEPTH OF BORING : 51.0m	R. L.: 1.52m below from Road Level.
CLIENT : TM International, Bangladesh Ltd.	DATE OF BORING : 01-02-2009	G. W. T : 2.13m below from E. G. L.

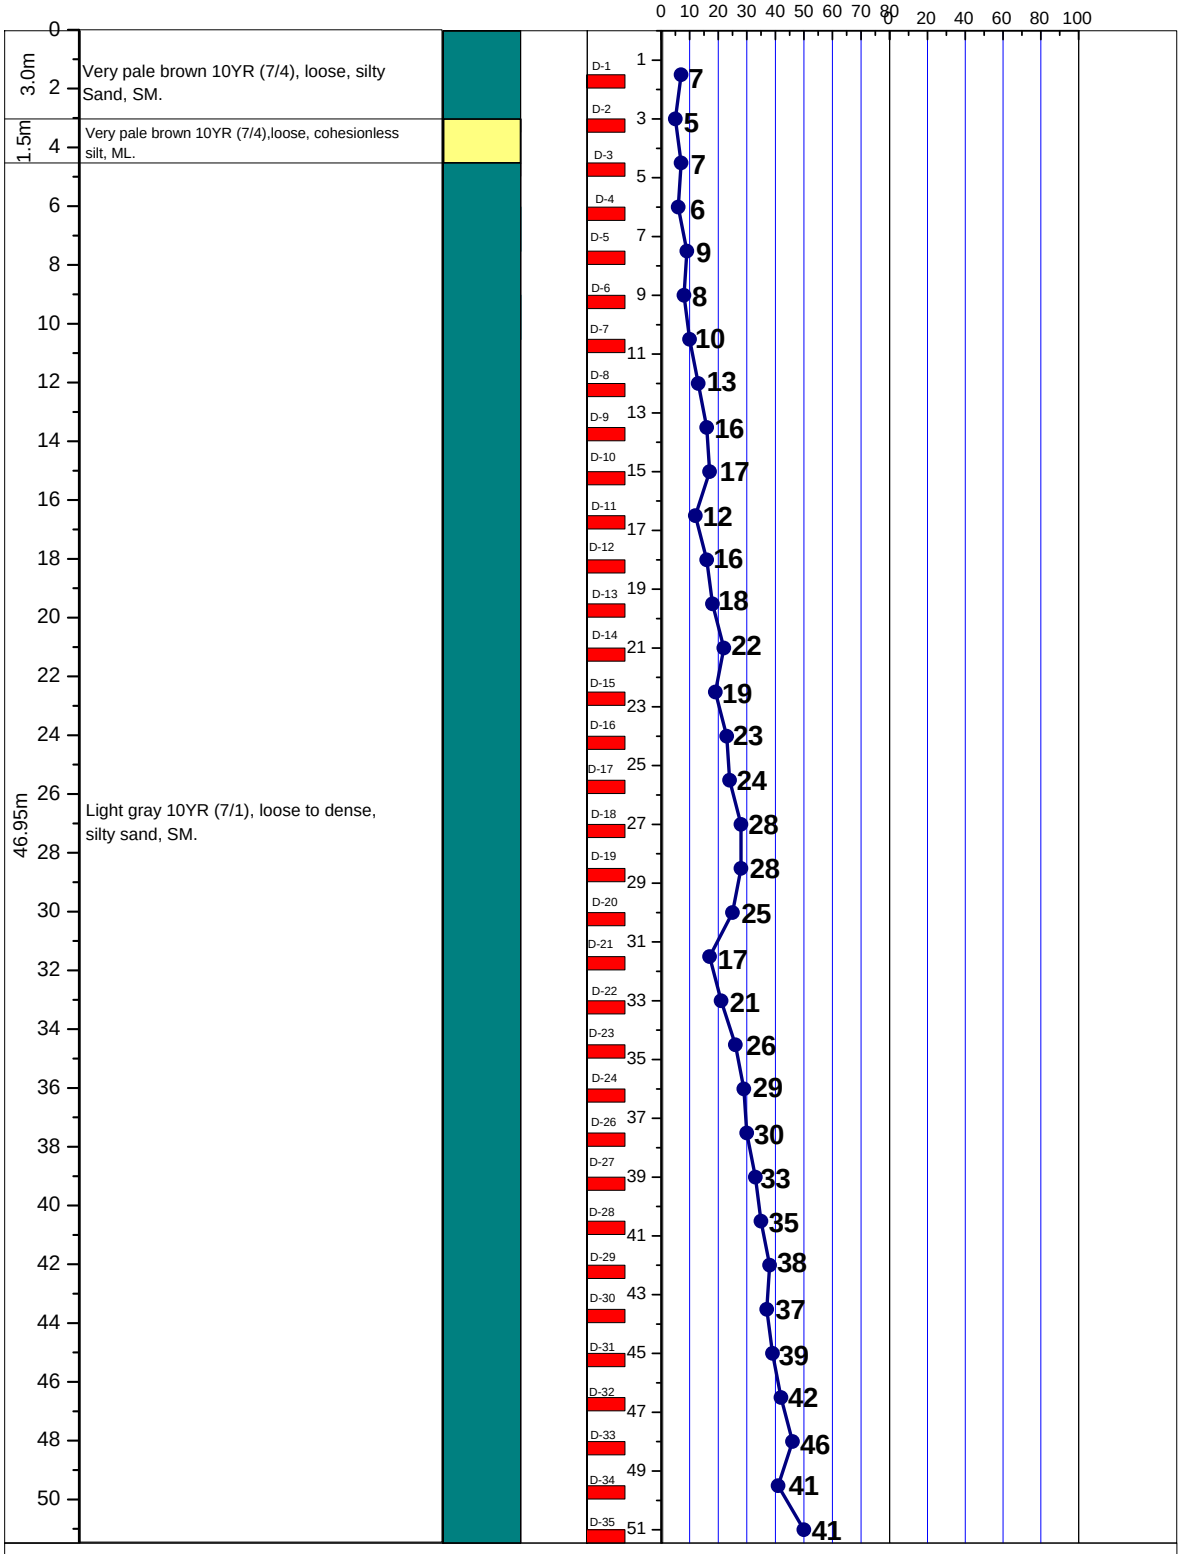


LEGEND FOR BORELOG AND GRAIN SIZE DISTRIBUTION (BASED ON 'ASTM CLASSIFICATION D-2487')

PLASTIC CLAY	SILT	PEAT/HIGHLY ORGANIC SOIL	UNDISTURBED SAMPLE
MICACEOUS FINE SAND/SILT	SAND	SHALE	DISTURBED SAMPLE

N- BLOWS DELIVERED PER FOOT BY A 140 LB HAMMER FALLING 30 INCHES

MAX^{m} PENETRATION= 50 BLOWS. AFTER 50 BLOWS PENETRATION DEPTH WERE MEASURED

A2	PROSOIL	BOREHOLE NO: BH-1	
		LOCATION : Islampur, Rangunia, Chittagong.	
PROJECT : Telecommunication Tower.		DEPTH OF BORING : 51.0m	R. L.: 1.52m below from Road Level.
CLIENT : AXIATA (Bangladesh) Ltd.		DATE OF BORING : 25-08-2009.	G. W. T : 0.10m above from E. G. L.

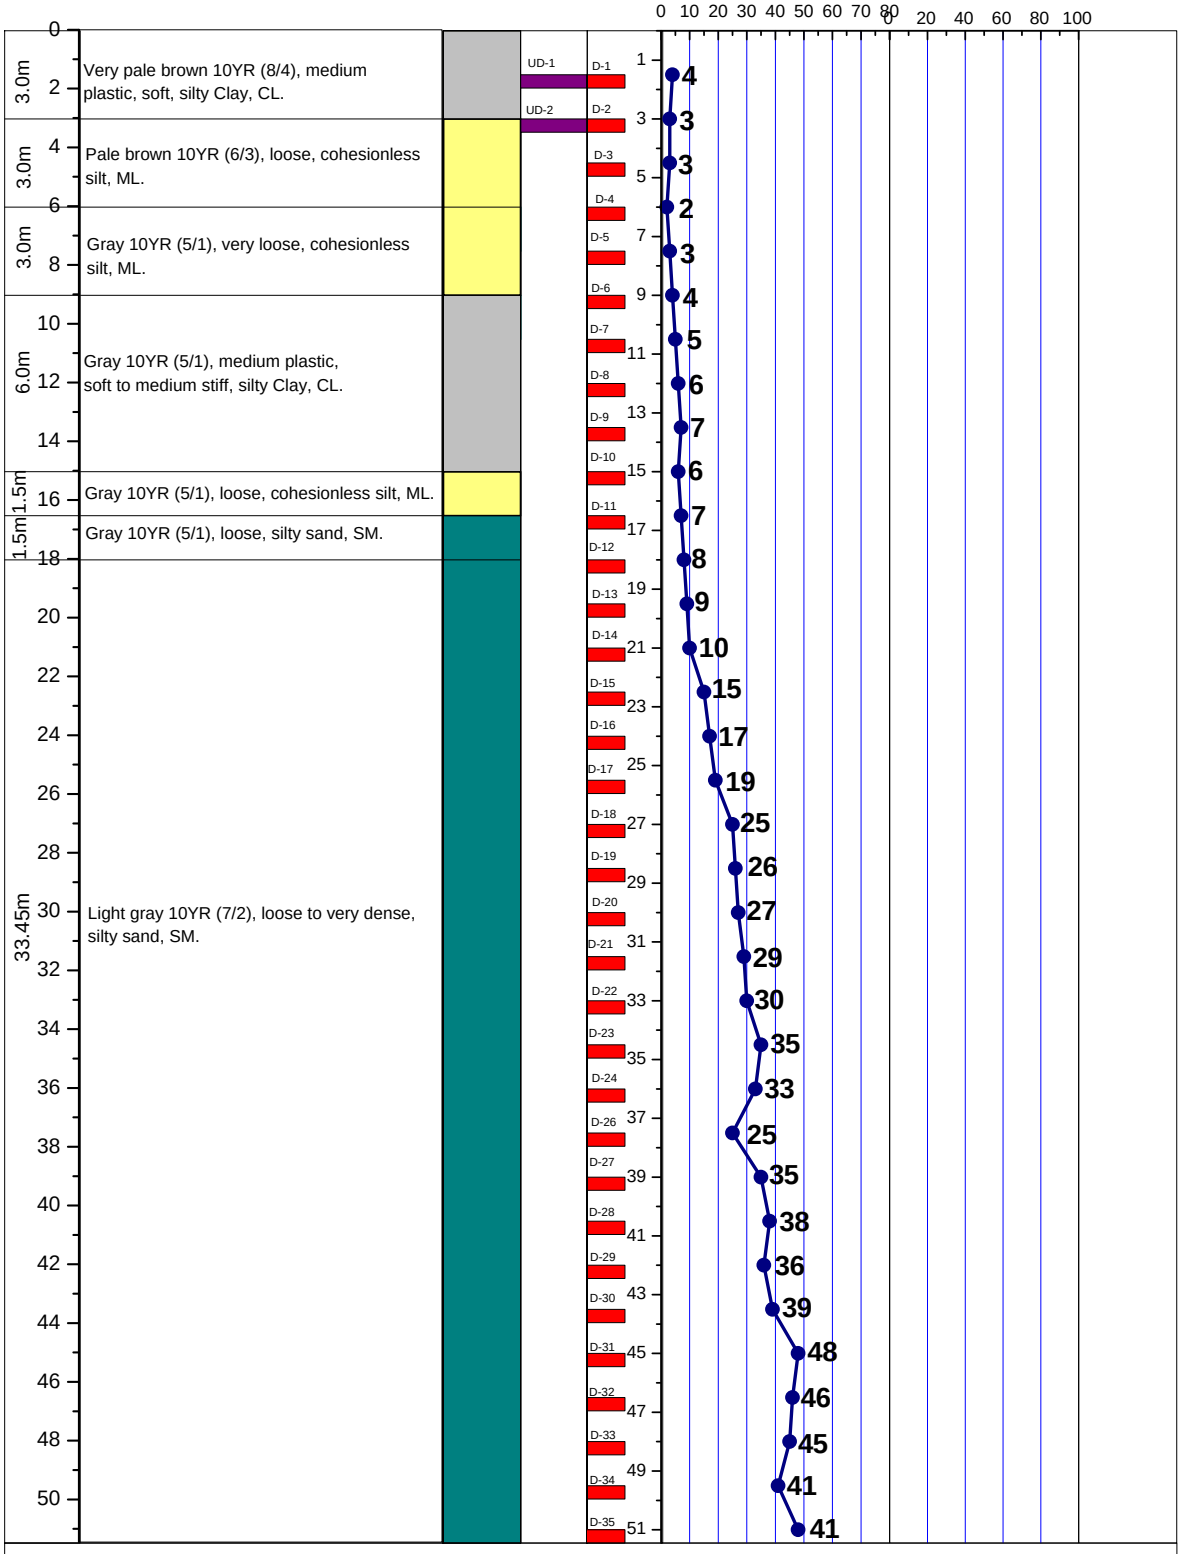


LEGEND FOR BORELOG AND GRAIN SIZE DISTRIBUTION (BASED ON 'ASTM CLASSIFICATION D-2487')

PLASTIC CLAY	SILT	PEAT/HIGHLY ORGANIC SOIL	UNDISTURBED SAMPLE
MICACEOUS FINE SAND/SILT	SAND	SHALE	DISTURBED SAMPLE

N- BLOWS DELIVERED PER FOOT BY A 140 LB HAMMER FALLING 30 INCHES

MAX^{m} PENETRATION= 50 BLOWS. AFTER 50 BLOWS PENETRATION DEPTH WERE MEASURED

A2 PROSOIL	BOREHOLE NO: BH-1	
	LOCATION : Islampur, Rangunia.	
PROJECT : Telecommunication Tower.	DEPTH OF BORING : 51.0m	R. L.: 0.30m below from Road Level.
CLIENT : TM International, Bangladesh Ltd.	DATE OF BORING : 11-03-2009.	G. W. T : 3.96m above from E. G. L.

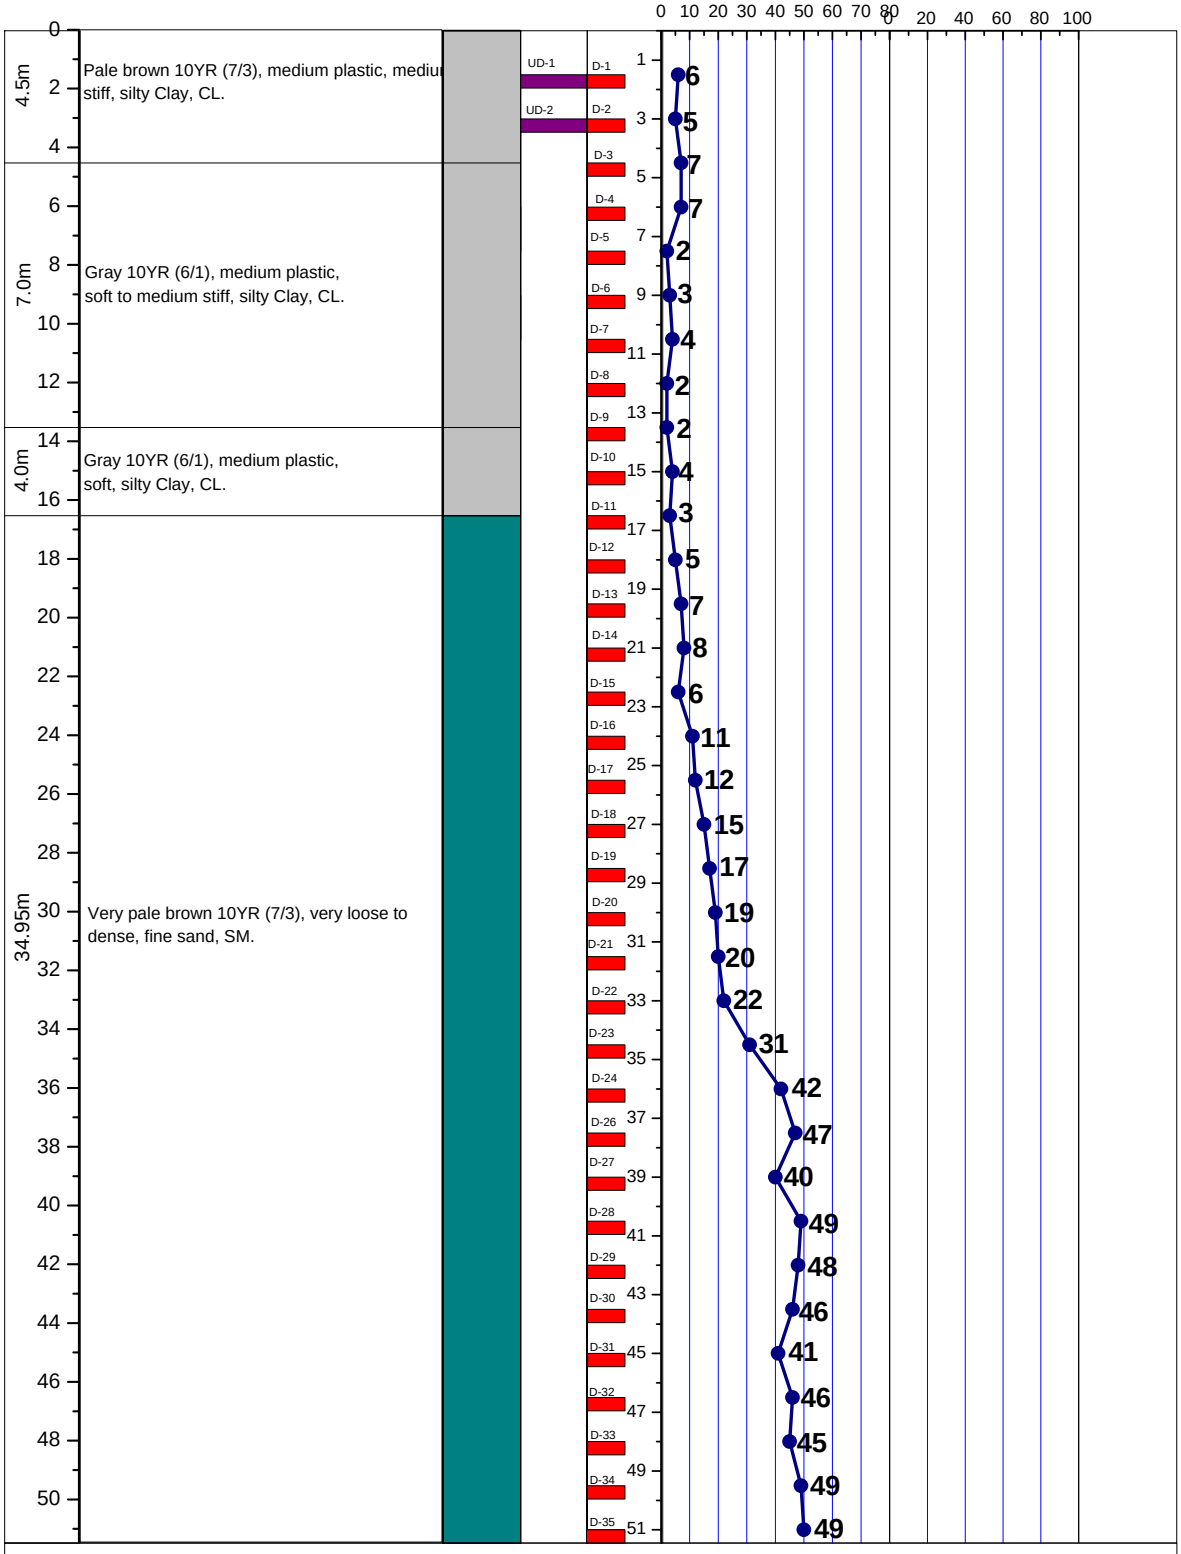


LEGEND FOR BORELOG AND GRAIN SIZE DISTRIBUTION (BASED ON 'ASTM CLASSIFICATION D-2487')

PLASTIC CLAY	SILT	PEAT/HIGHLY ORGANIC SOIL	UNDISTURBED SAMPLE
MICACEOUS FINE SAND/SILT	SAND	SHALE	DISTURBED SAMPLE

N- BLOWS DELIVERED PER FOOT BY A 140 LB HAMMER FALLING 30 INCHES

MAX^{m} PENETRATION= 50 BLOWS. AFTER 50 BLOWS PENETRATION DEPTH WERE MEASURED

A2 PROSOIL	BOREHOLE NO: BH-1	
	LOCATION : Jotermukh, Chandanaish, Chittagong.	
PROJECT : Telecommunication Tower.	DEPTH OF BORING : 51.0m	R. L.: 1.09m below from Road Level.
CLIENT : TM International, Bangladesh Ltd.	DATE OF BORING : 17-02-2009.	G. W. T : REMARKS.

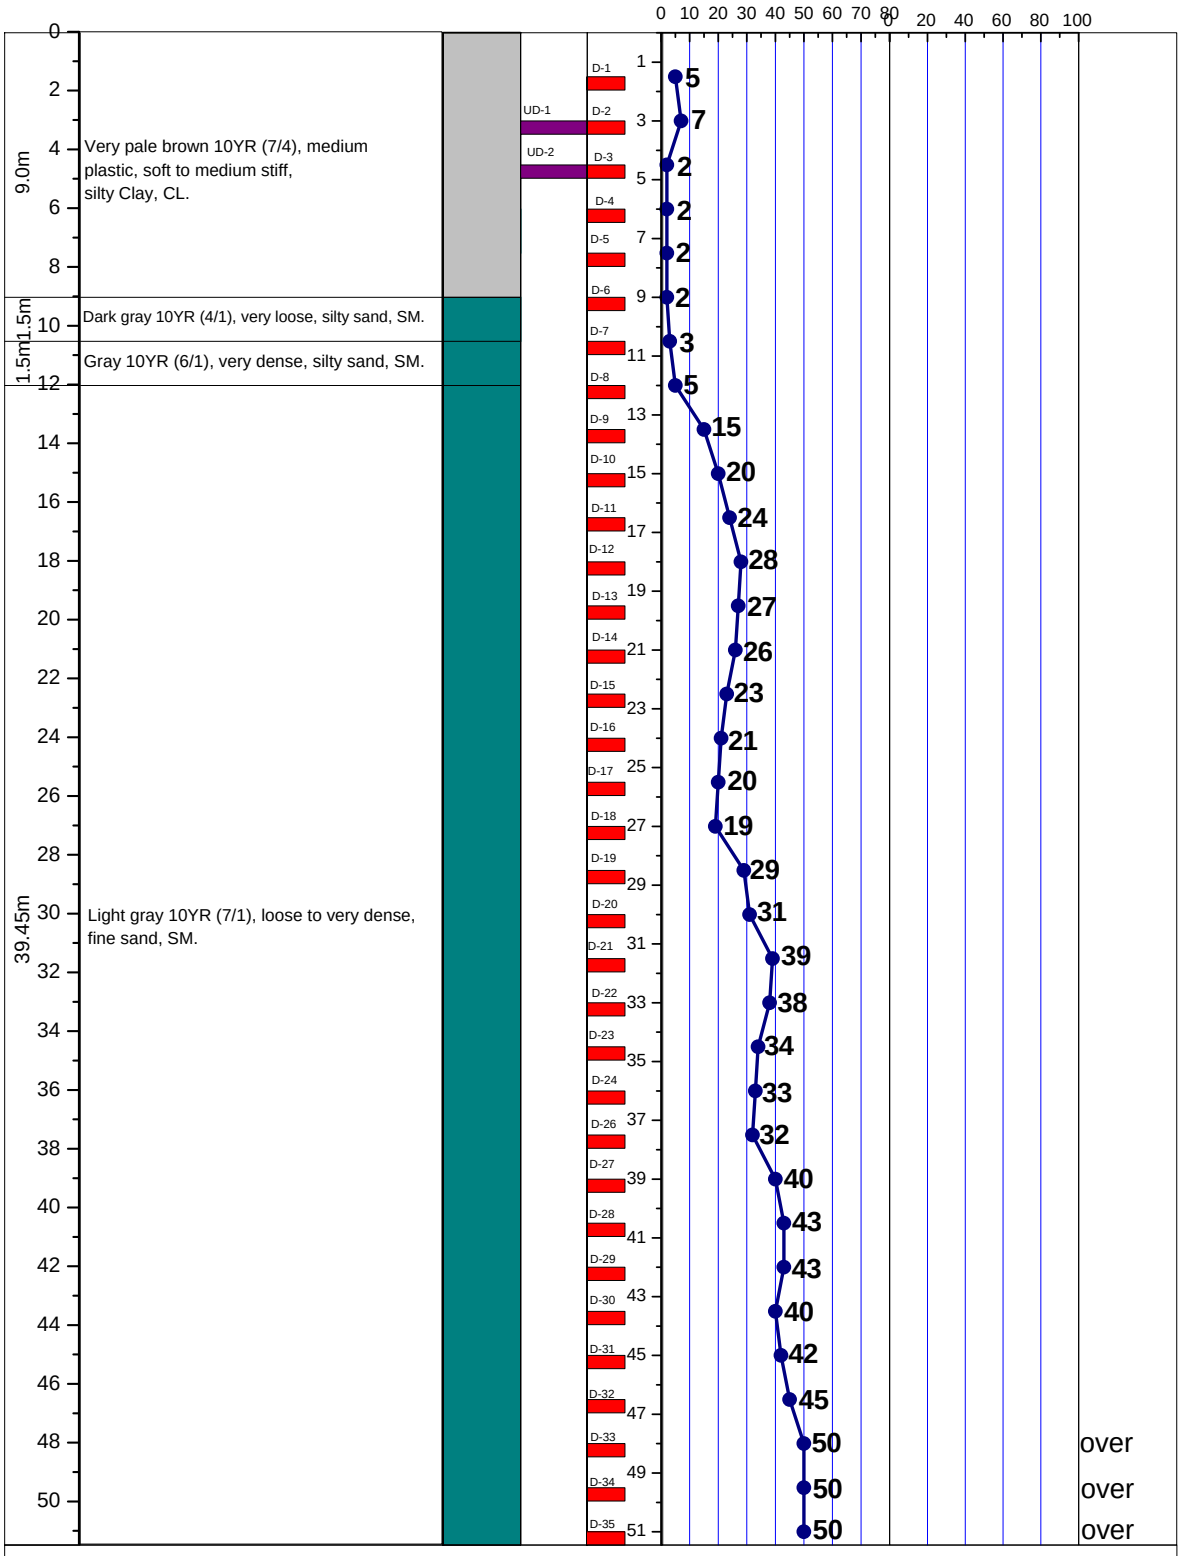


LEGEND FOR BORELOG AND GRAIN SIZE DISTRIBUTION (BASED ON 'ASTM CLASSIFICATION D-2487')

PLASTIC CLAY	SILT	PEAT/HIGHLY ORGANIC SOIL	UNDISTURBED SAMPLE
MICACEOUS FINE SAND/SILT	SAND	SHALE	DISTURBED SAMPLE

N- BLOWS DELIVERED PER FOOT BY A 140 LB HAMMER FALLING 30 INCHES

MAX^{m} PENETRATION= 50 BLOWS. AFTER 50 BLOWS PENETRATION DEPTH WERE MEASURED

A2 PROSOIL	BOREHOLE NO: BH-1	
	LOCATION : Juidandi, Chowmohoni Bazar, Anwara, Chittagong.	
PROJECT : Telecommunication Tower.	DEPTH OF BORING : 51.0m	R. L.: 0.76m below from Road Level.
CLIENT : AXIATA (Bangladesh) Ltd.	DATE OF BORING : 19-02-2010.	G. W. T : 0.05m above from E. G. L.

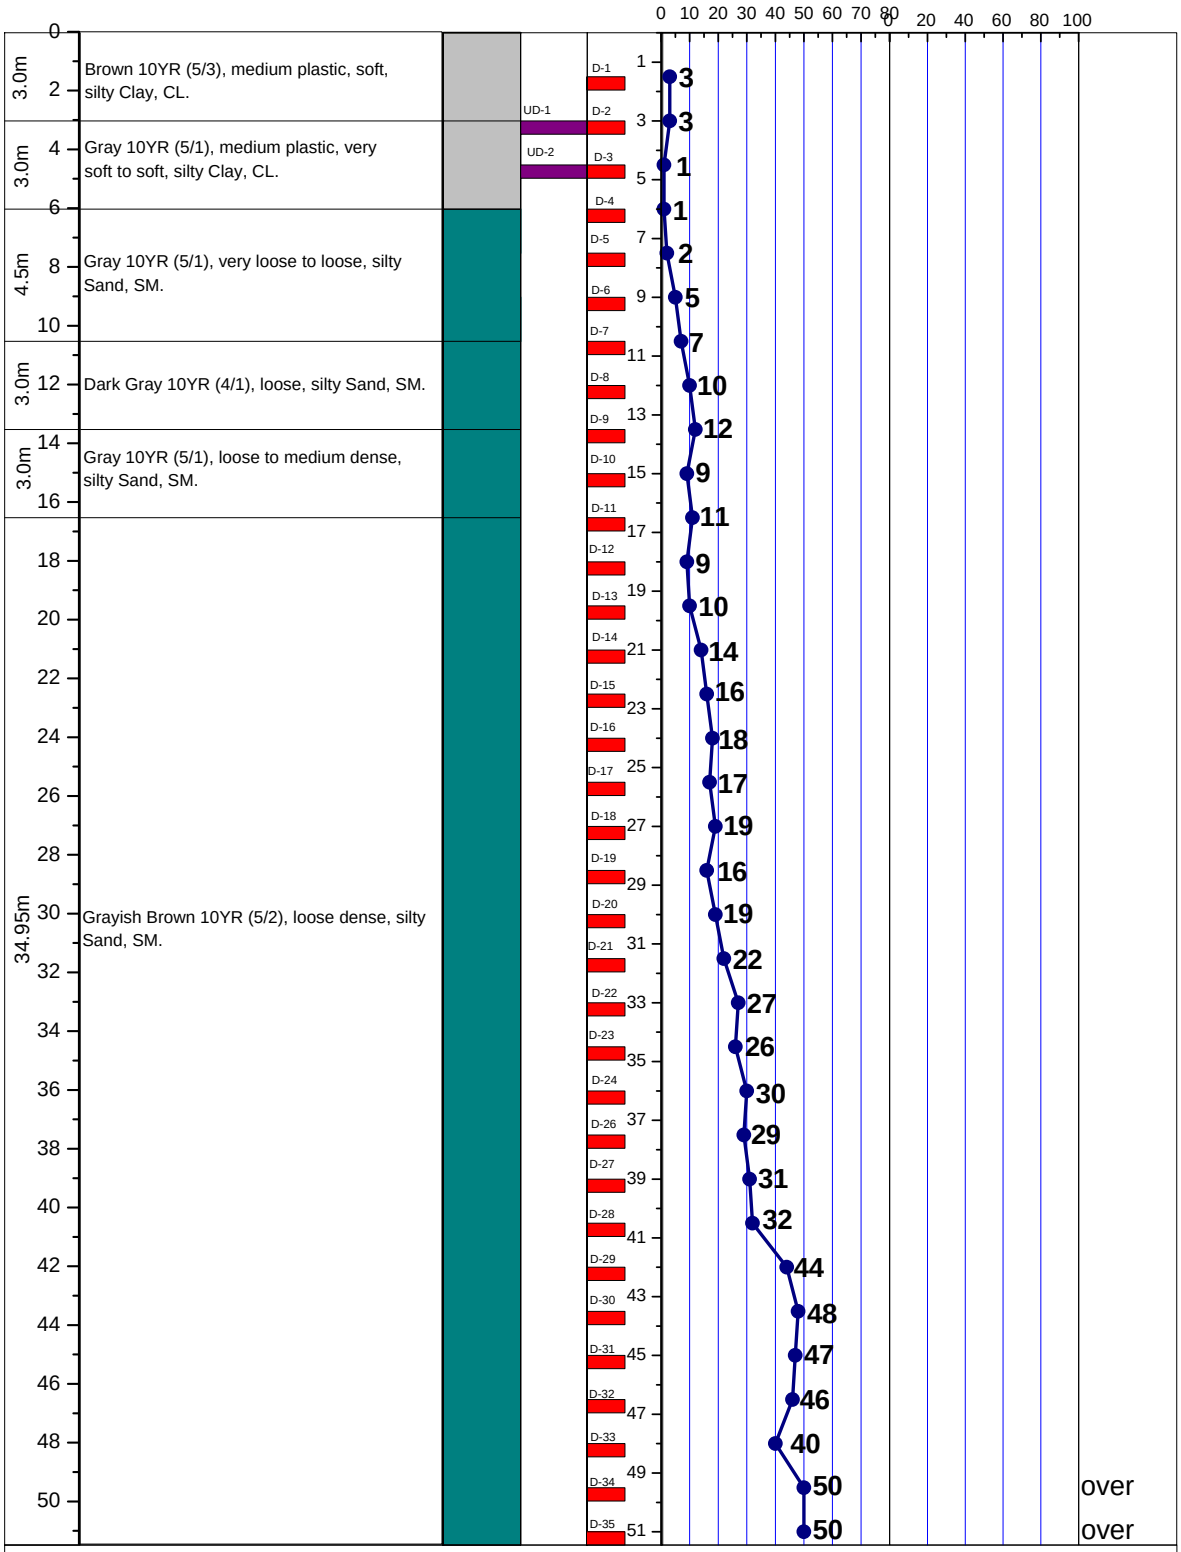


LEGEND FOR BORELOG AND GRAIN SIZE DISTRIBUTION (BASED ON 'ASTM CLASSIFICATION D-2487')

PLASTIC CLAY	SILT	PEAT/HIGHLY ORGANIC SOIL	UNDISTURBED SAMPLE
MICACEOUS FINE SAND/SILT	SAND	SHALE	DISTURBED SAMPLE

N- BLOWS DELIVERED PER FOOT BY A 140 LB HAMMER FALLING 30 INCHES

MAX^{m} PENETRATION= 50 BLOWS. AFTER 50 BLOWS PENETRATION DEPTH WERE MEASURED

A2 PROSOIL	BOREHOLE NO: BH-1	
	LOCATION : Kadomtoli, Rangunia.	
PROJECT : Telecommunication Tower.	DEPTH OF BORING : 51.0m	R. L.: 1.22m below from Road Level.
CLIENT : AXIATA (Bangladesh) Ltd.	DATE OF BORING : 30-05-2010.	G. W. T : 0.91m above from E. G. L.(Rain water)

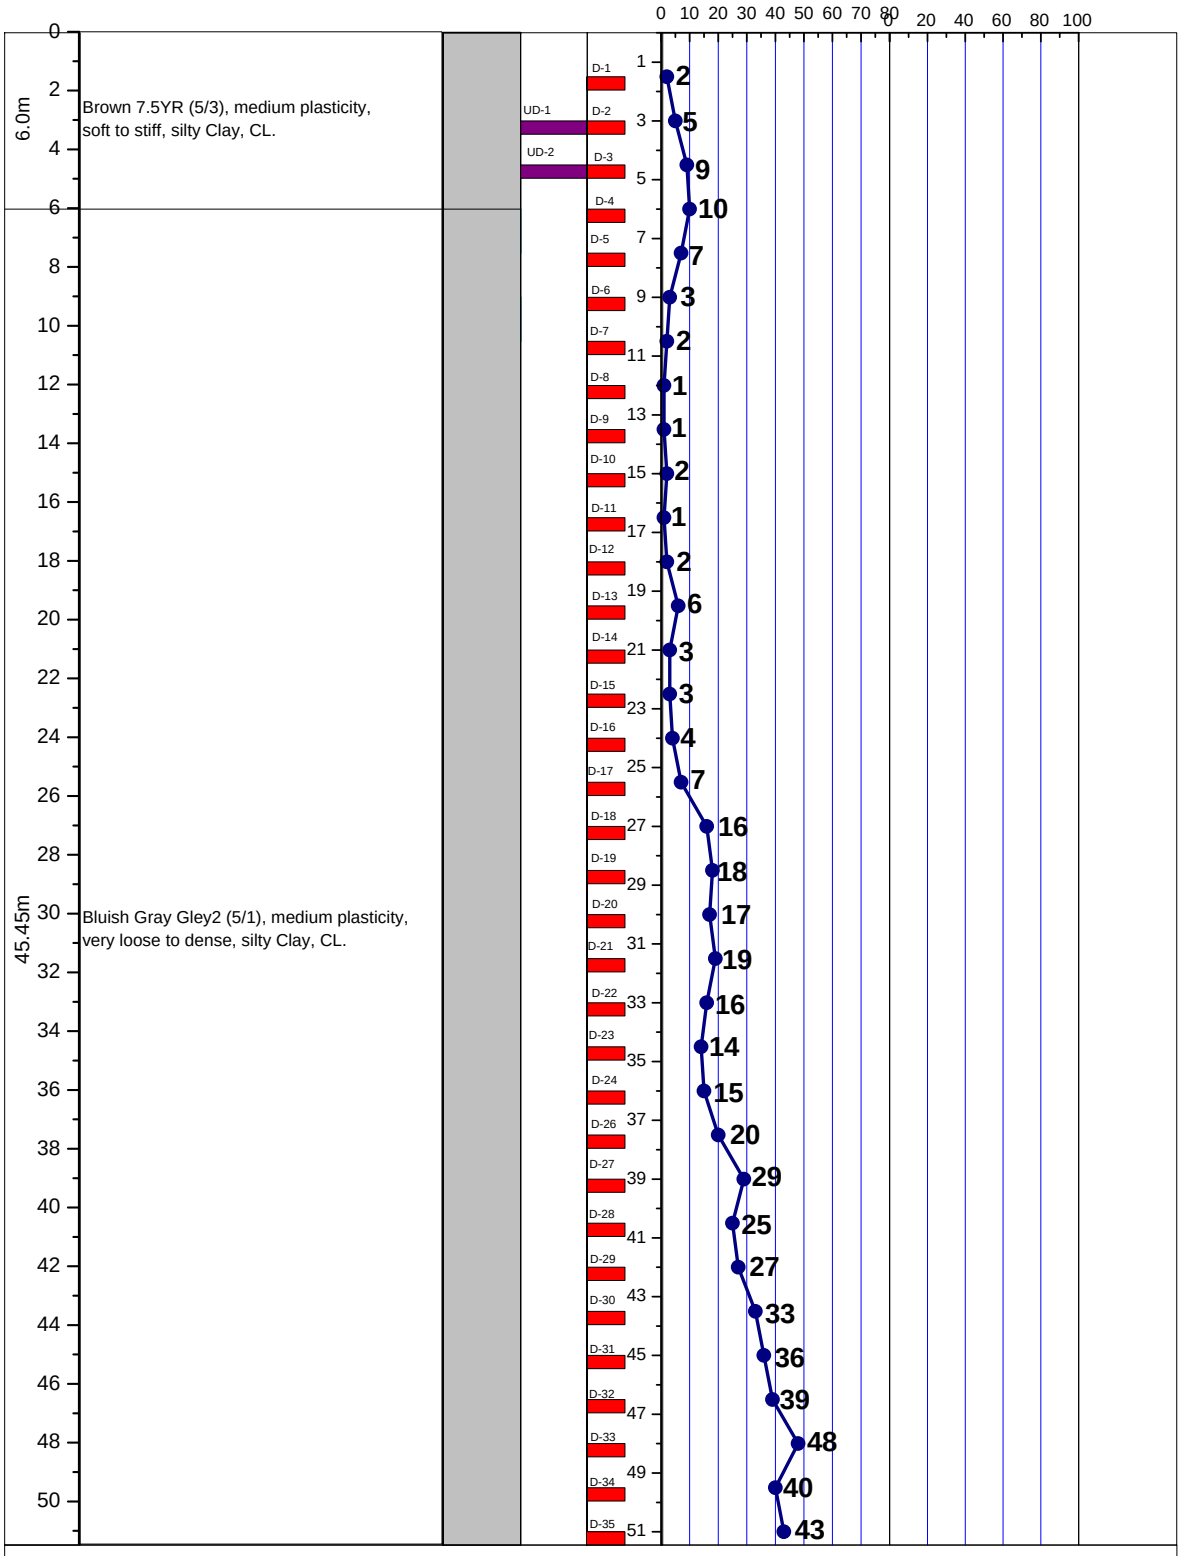


LEGEND FOR BORELOG AND GRAIN SIZE DISTRIBUTION (BASED ON 'ASTM CLASSIFICATION D-2487')

PLASTIC CLAY	SILT	PEAT/HIGHLY ORGANIC SOIL	UNDISTURBED SAMPLE
MICACEOUS FINE SAND/SILT	SAND	SHALE	DISTURBED SAMPLE

N- BLOWS DELIVERED PER FOOT BY A 140 LB HAMMER FALLING 30 INCHES

MAX^{m} PENETRATION= 50 BLOWS. AFTER 50 BLOWS PENETRATION DEPTH WERE MEASURED

A2 PROSOIL	BOREHOLE NO: BH-1	
	LOCATION : Keranirhat 55m Land, Satkania, Chittagong.	
PROJECT : Telecommunication Tower.	DEPTH OF BORING : 51.0m	R. L.: 1.82m below from Road Level.
CLIENT : AXIATA (Bangladesh) Ltd.	DATE OF BORING : 06-08-2009.	G. W. T : 0.76m above from E. G. L.

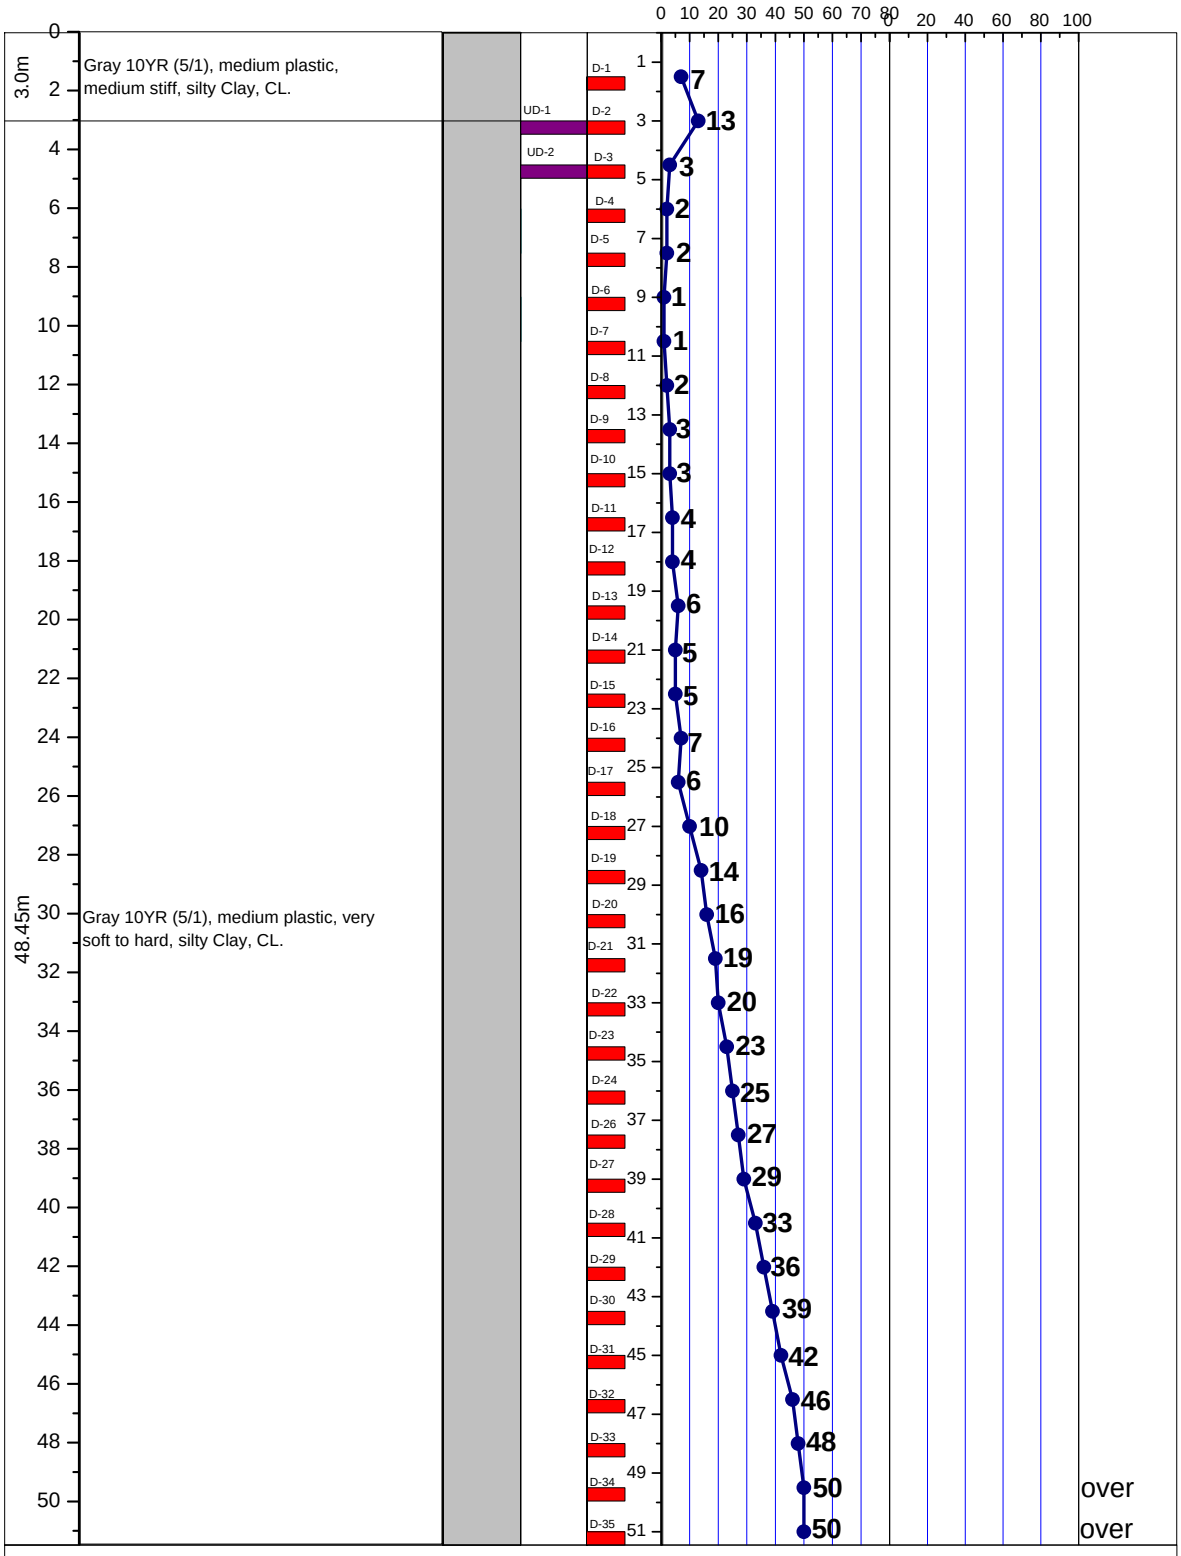


LEGEND FOR BORELOG AND GRAIN SIZE DISTRIBUTION (BASED ON 'ASTM CLASSIFICATION D-2487')

PLASTIC CLAY	SILT	PEAT/HIGHLY ORGANIC SOIL	UNDISTURBED SAMPLE
MICACEOUS FINE SAND/SILT	SAND	SHALE	DISTURBED SAMPLE

N- BLOWS DELIVERED PER FOOT BY A 140 LB HAMMER FALLING 30 INCHES

MAX^{m} PENETRATION= 50 BLOWS. AFTER 50 BLOWS PENETRATION DEPTH WERE MEASURED

A2	PROSOIL	BOREHOLE NO: BH-1	
		LOCATION : Middle Ratanpur, Patiya, Chittagong.	
PROJECT : Telecommunication Tower.		DEPTH OF BORING : 51.0m	R. L.: 1.07m below from Road Level.
CLIENT : AXIATA (Bangladesh) Ltd.		DATE OF BORING : 18-02-2010.	G. W. T : 3.05m above from E. G. L.

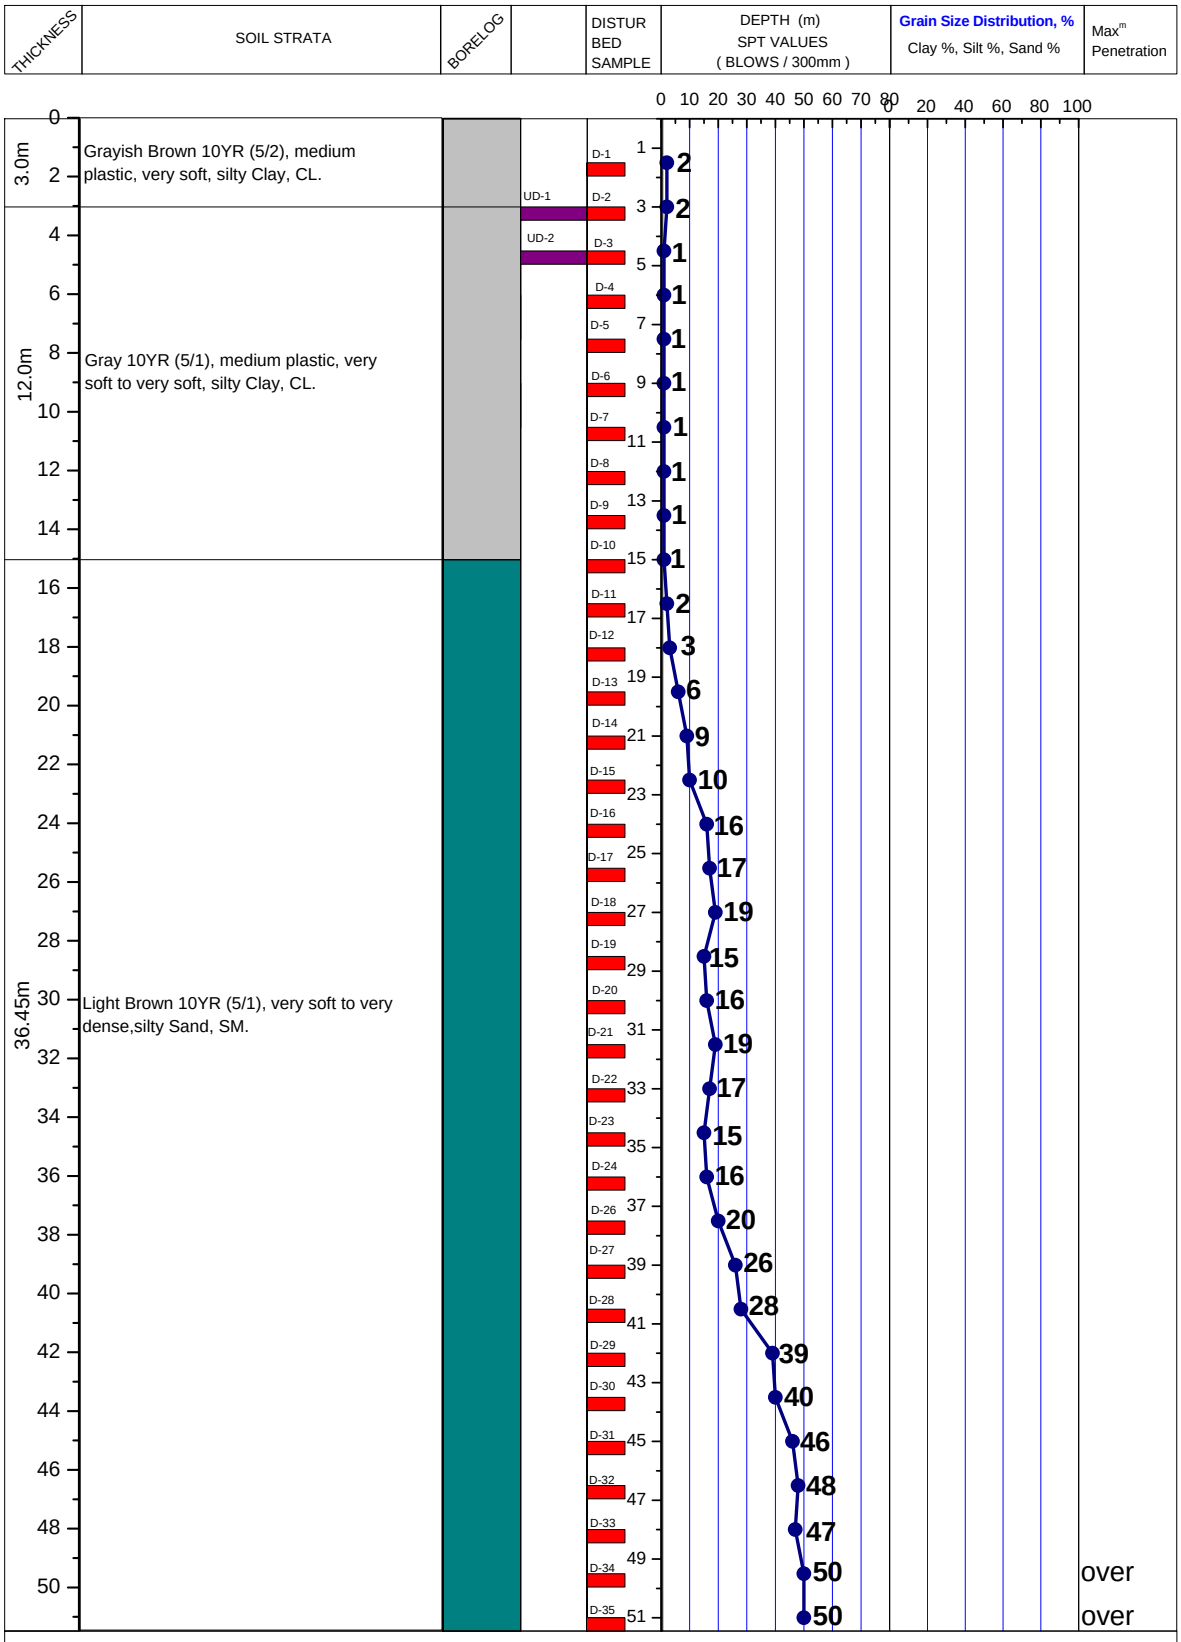


LEGEND FOR BORELOG AND GRAIN SIZE DISTRIBUTION (BASED ON 'ASTM CLASSIFICATION D-2487')

PLASTIC CLAY	SILT	PEAT/HIGHLY ORGANIC SOIL	UNDISTURBED SAMPLE
MICACEOUS FINE SAND/SILT	SAND	SHALE	DISTURBED SAMPLE

N- BLOWS DELIVERED PER FOOT BY A 140 LB HAMMER FALLING 30 INCHES

MAX^{m} PENETRATION= 50 BLOWS. AFTER 50 BLOWS PENETRATION DEPTH WERE MEASURED

A2 PROSOIL	BOREHOLE NO: BH-1	
	LOCATION : Nalarkul, Putibila Nalarkul, M. Char Hut, Lohagora, Chittagong.	
PROJECT : Telecommunication Tower.	DEPTH OF BORING : 51.0m	R. L.: 1.57m below from Road Level.
CLIENT : AXIATA (Bangladesh) Ltd.	DATE OF BORING : 27-04-2012.	G. W. T : 1.22m above from E. G. L.

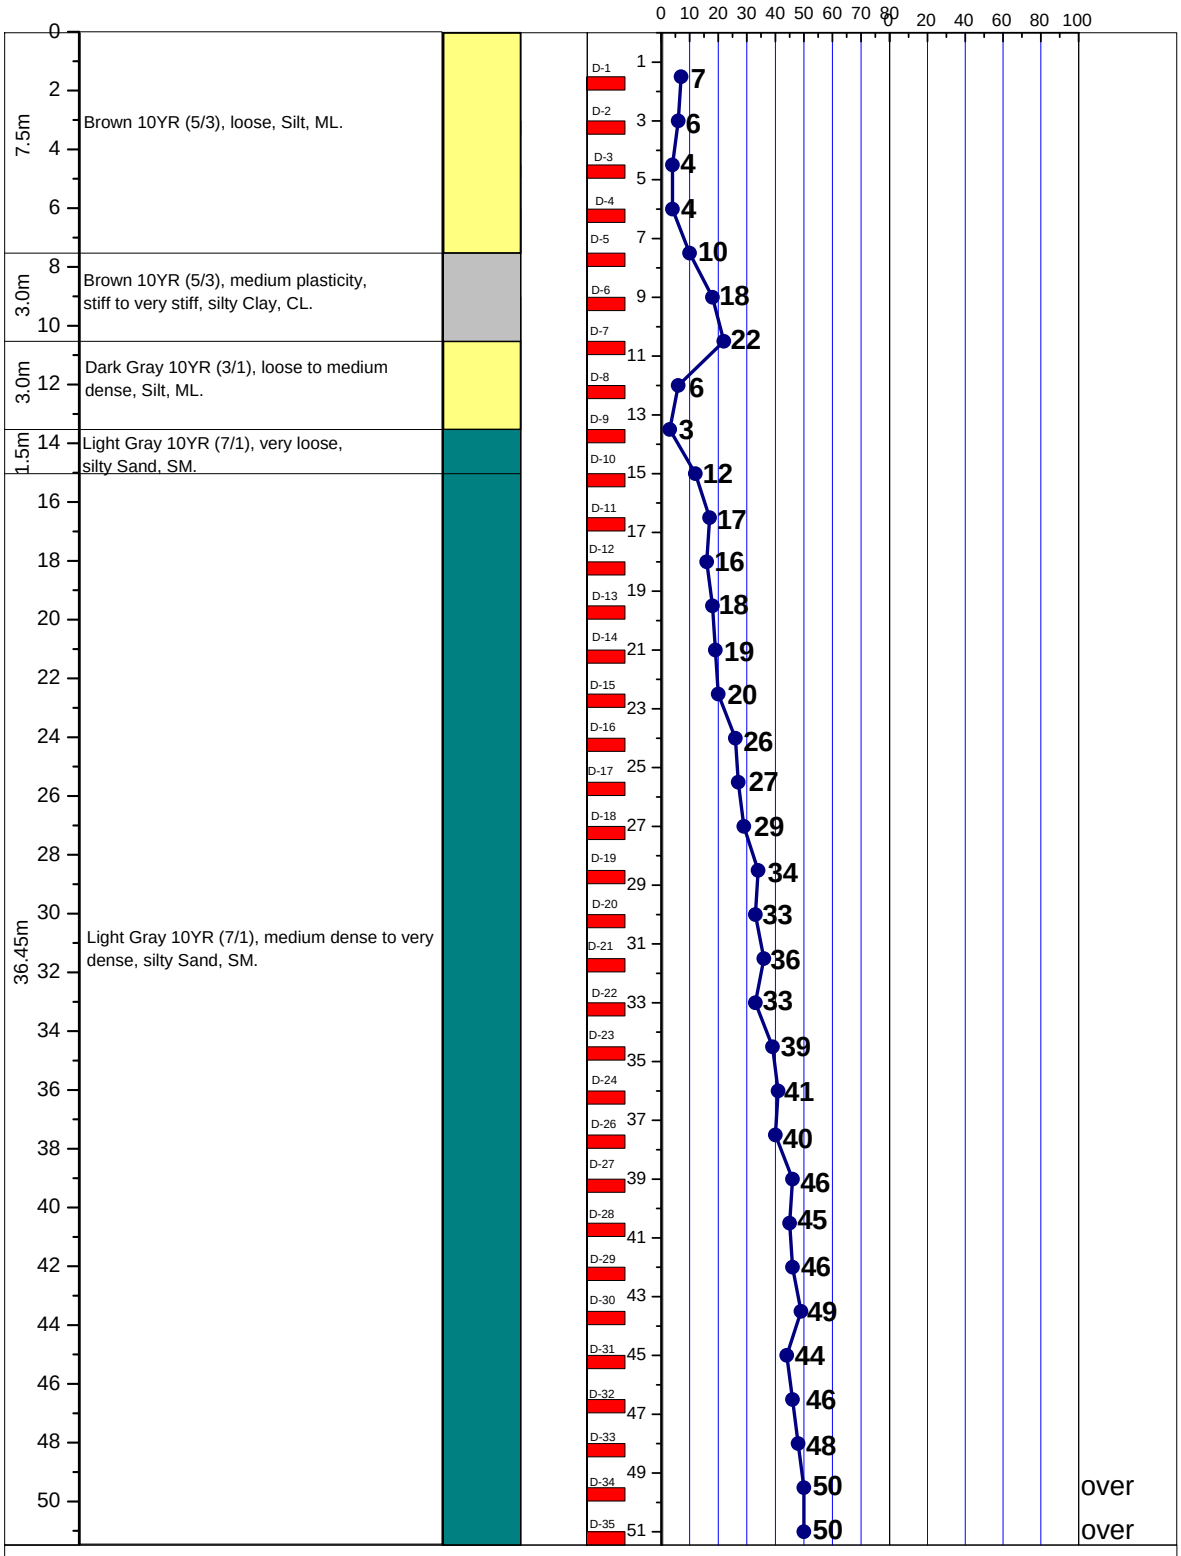


LEGEND FOR BORELOG AND GRAIN SIZE DISTRIBUTION (BASED ON 'ASTM CLASSIFICATION D-2487')

PLASTIC CLAY	SILT	PEAT/HIGHLY ORGANIC SOIL	UNDISTURBED SAMPLE
MICACEOUS FINE SAND/SILT	SAND	SHALE	DISTURBED SAMPLE

N- BLOWS DELIVERED PER FOOT BY A 140 LB HAMMER FALLING 30 INCHES

MAX^{m} PENETRATION= 50 BLOWS. AFTER 50 BLOWS PENETRATION DEPTH WERE MEASURED

A2	PROSOIL	BOREHOLE NO: BH-1	
		LOCATION : Pohor chanda, Lohagora, Chittagong.	
PROJECT : Telecommunication Tower.		DEPTH OF BORING : 51.0m	R. L.: 0.81m below from Road Level.
CLIENT : AXIATA (Bangladesh) Ltd.		DATE OF BORING : 24-05-2010.	G. W. T : 0.10m above from E. G. L. (Rain Water)

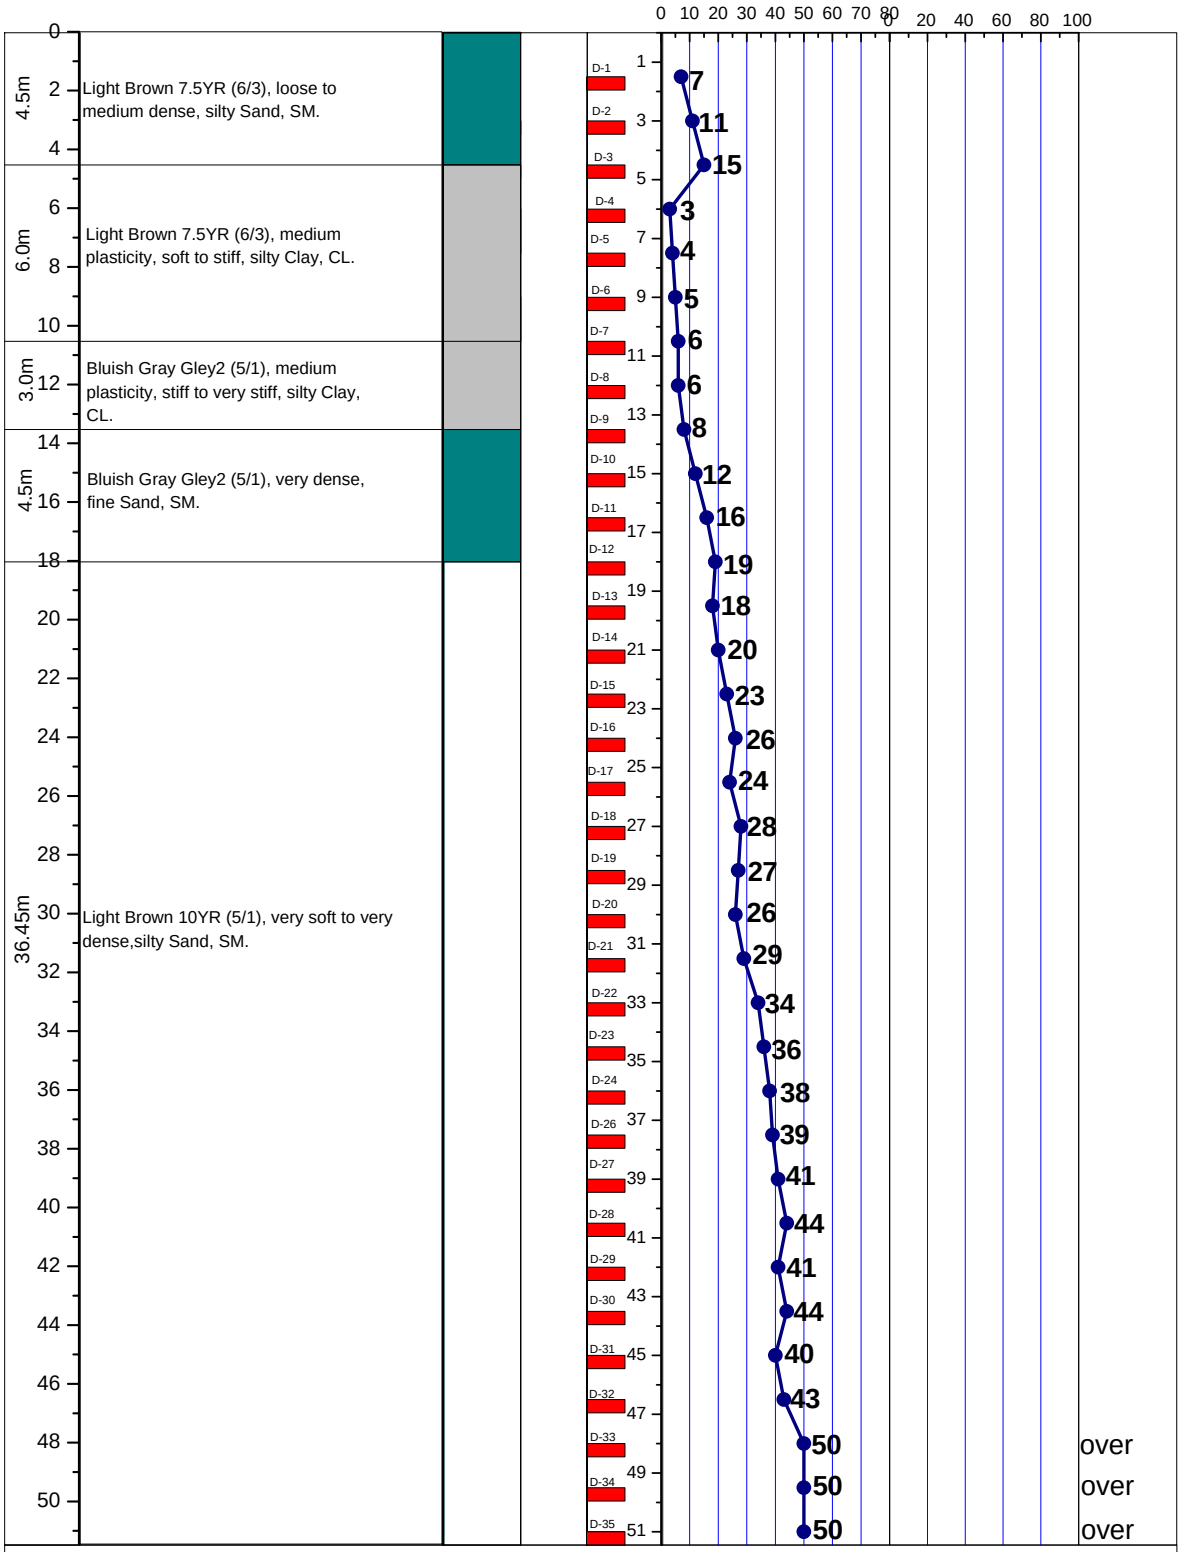


LEGEND FOR BORELOG AND GRAIN SIZE DISTRIBUTION (BASED ON 'ASTM CLASSIFICATION D-2487')

PLASTIC CLAY	SILT	PEAT/HIGHLY ORGANIC SOIL	UNDISTURBED SAMPLE
MICACEOUS FINE SAND/SILT	SAND	SHALE	DISTURBED SAMPLE

N- BLOWS DELIVERED PER FOOT BY A 140 LB HAMMER FALLING 30 INCHES

MAX^{m} PENETRATION= 50 BLOWS. AFTER 50 BLOWS PENETRATION DEPTH WERE MEASURED

A2 PROSOIL	BOREHOLE NO: BH-1	
	LOCATION : Pathandondi, Chandonaish, Chittagong.	
PROJECT : Telecommunication Tower.	DEPTH OF BORING : 51.0m	R. L.: 1.42m below from Road Level.
CLIENT : AXIATA (Bangladesh) Ltd.	DATE OF BORING : 03-11-2009.	G. W. T : 0.31m above from E. G. L.

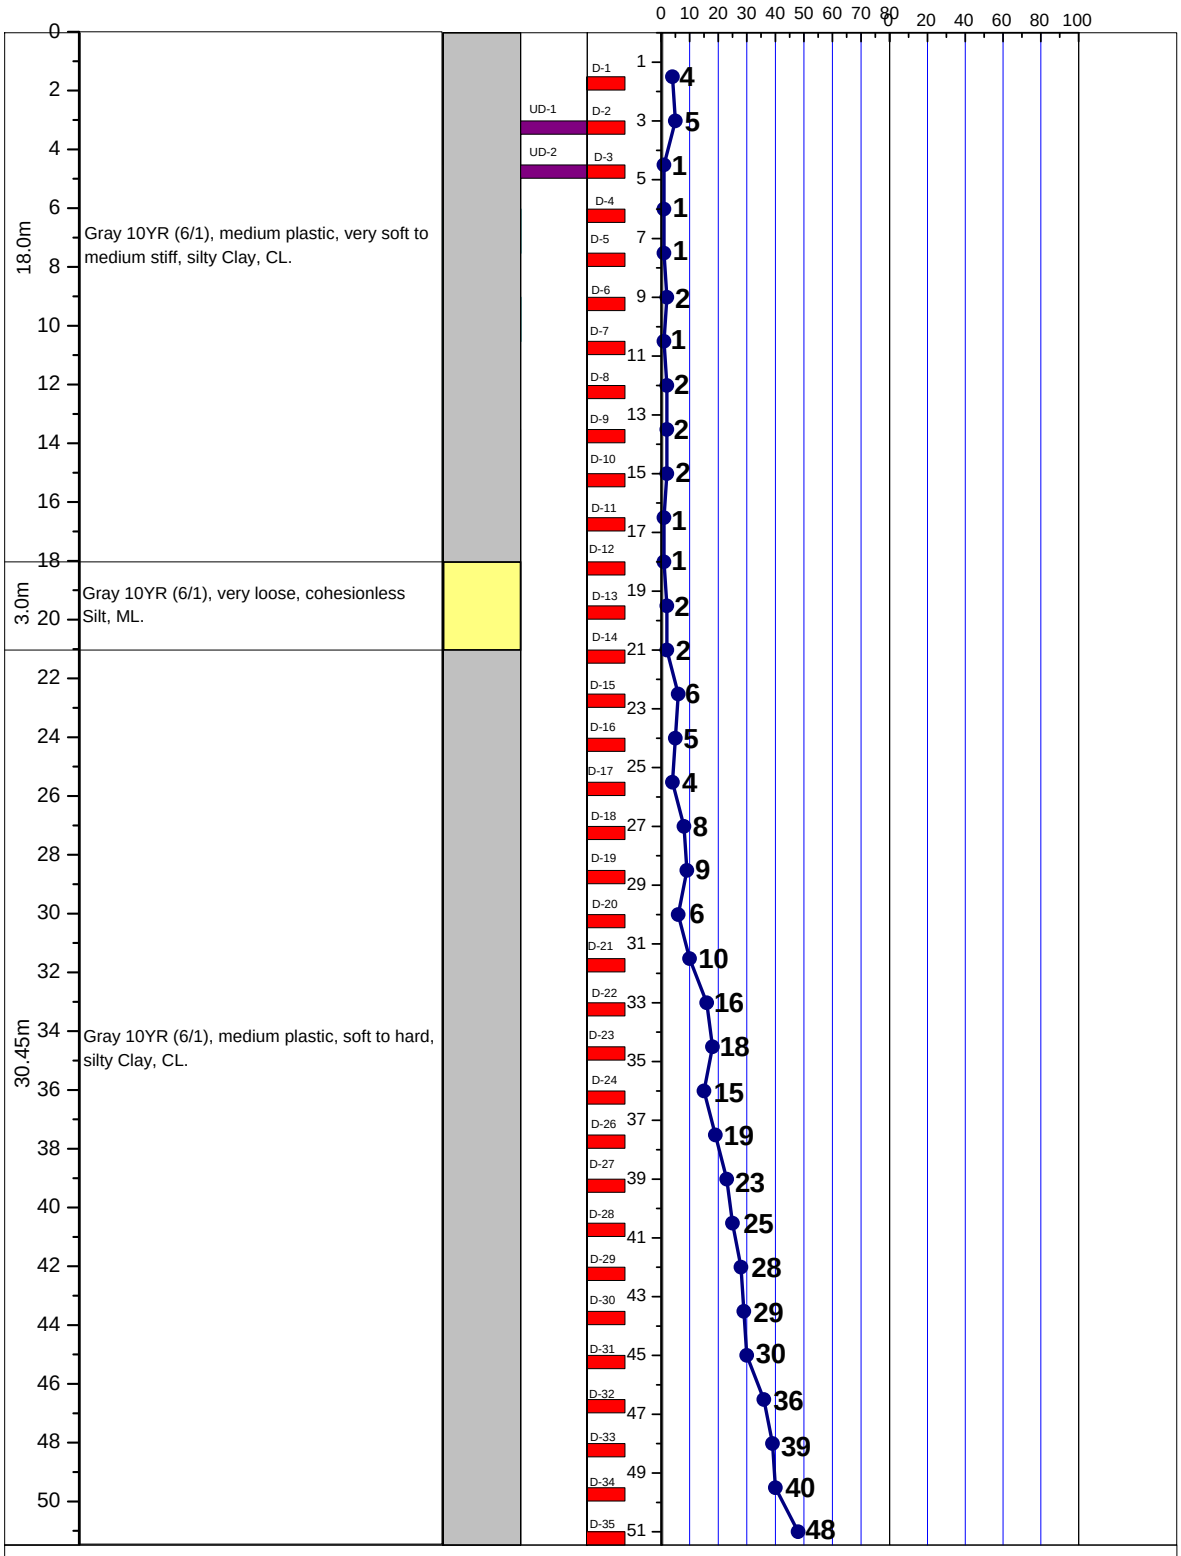


LEGEND FOR BORELOG AND GRAIN SIZE DISTRIBUTION (BASED ON 'ASTM CLASSIFICATION D-2487')

PLASTIC CLAY	SILT	PEAT/HIGHLY ORGANIC SOIL	UNDISTURBED SAMPLE
MICACEOUS FINE SAND/SILT	SAND	SHALE	DISTURBED SAMPLE

N- BLOWS DELIVERED PER FOOT BY A 140 LB HAMMER FALLING 30 INCHES

MAX^{m} PENETRATION= 50 BLOWS. AFTER 50 BLOWS PENETRATION DEPTH WERE MEASURED

A2	PROSOIL	BOREHOLE NO: BH-1	
		LOCATION : Puranghar, Satkania, Chittagong.	
PROJECT : Telecommunication Tower.		DEPTH OF BORING : 51.0m	R. L.: 1.52m below from Road Level.
CLIENT : TM International, Bangladesh Ltd.		DATE OF BORING : 14-04-2009.	G. W. T : 3.05m below from E. G. L.

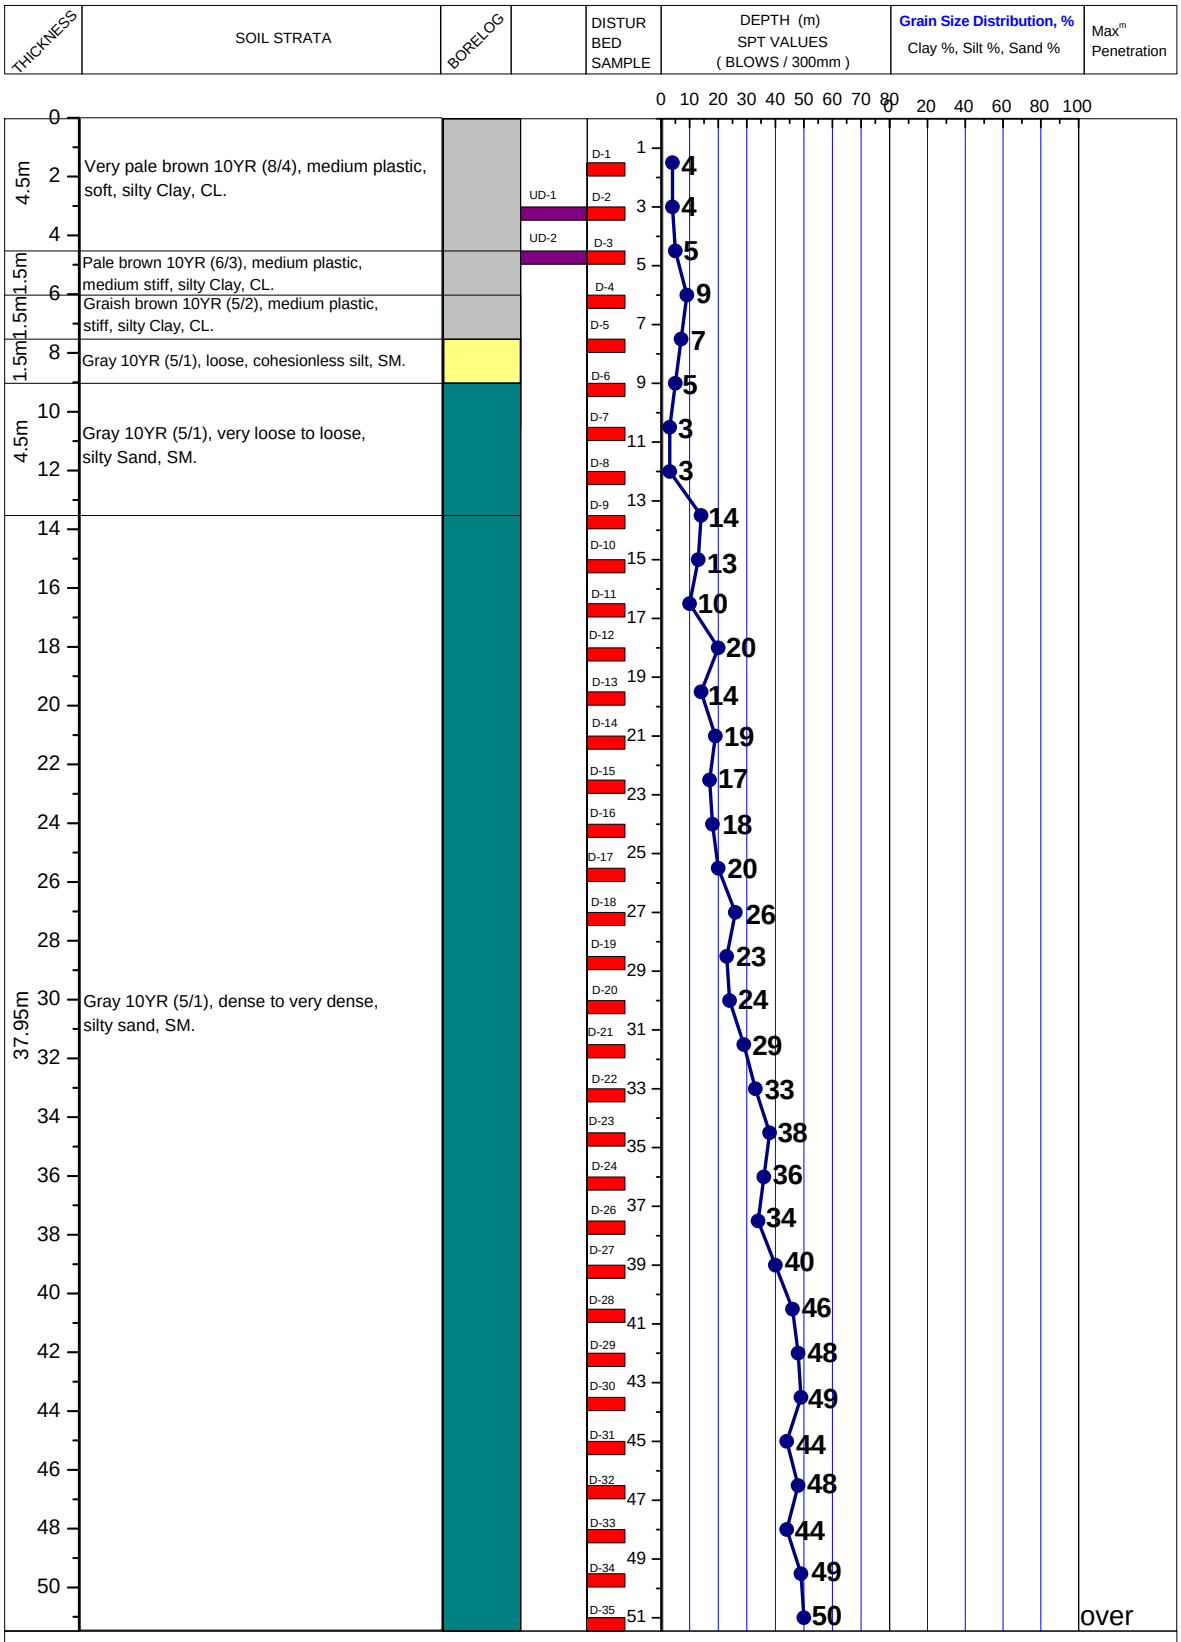


LEGEND FOR BORELOG AND GRAIN SIZE DISTRIBUTION (BASED ON 'ASTM CLASSIFICATION D-2487')

PLASTIC CLAY	SILT	PEAT/HIGHLY ORGANIC SOIL	UNDISTURBED SAMPLE
MICACEOUS FINE SAND/SILT	SAND	SHALE	DISTURBED SAMPLE

N- BLOWS DELIVERED PER FOOT BY A 140 LB HAMMER FALLING 30 INCHES

MAX^{m} PENETRATION= 50 BLOWS. AFTER 50 BLOWS PENETRATION DEPTH WERE MEASURED

A2 PROSOIL	BOREHOLE NO: BH-1	
	LOCATION : Rustom Hat2, Capatoly, Minnot Ali Hat, Anowara, Chittagong.	
PROJECT : Telecommunication Tower.	DEPTH OF BORING : 51.0m	R. L.: 0.15m below from Road Level.
CLIENT : AXIATA (Bangladesh) Ltd.	DATE OF BORING : 12-02-2012.	G. W. T : 6.1m below from E. G. L.

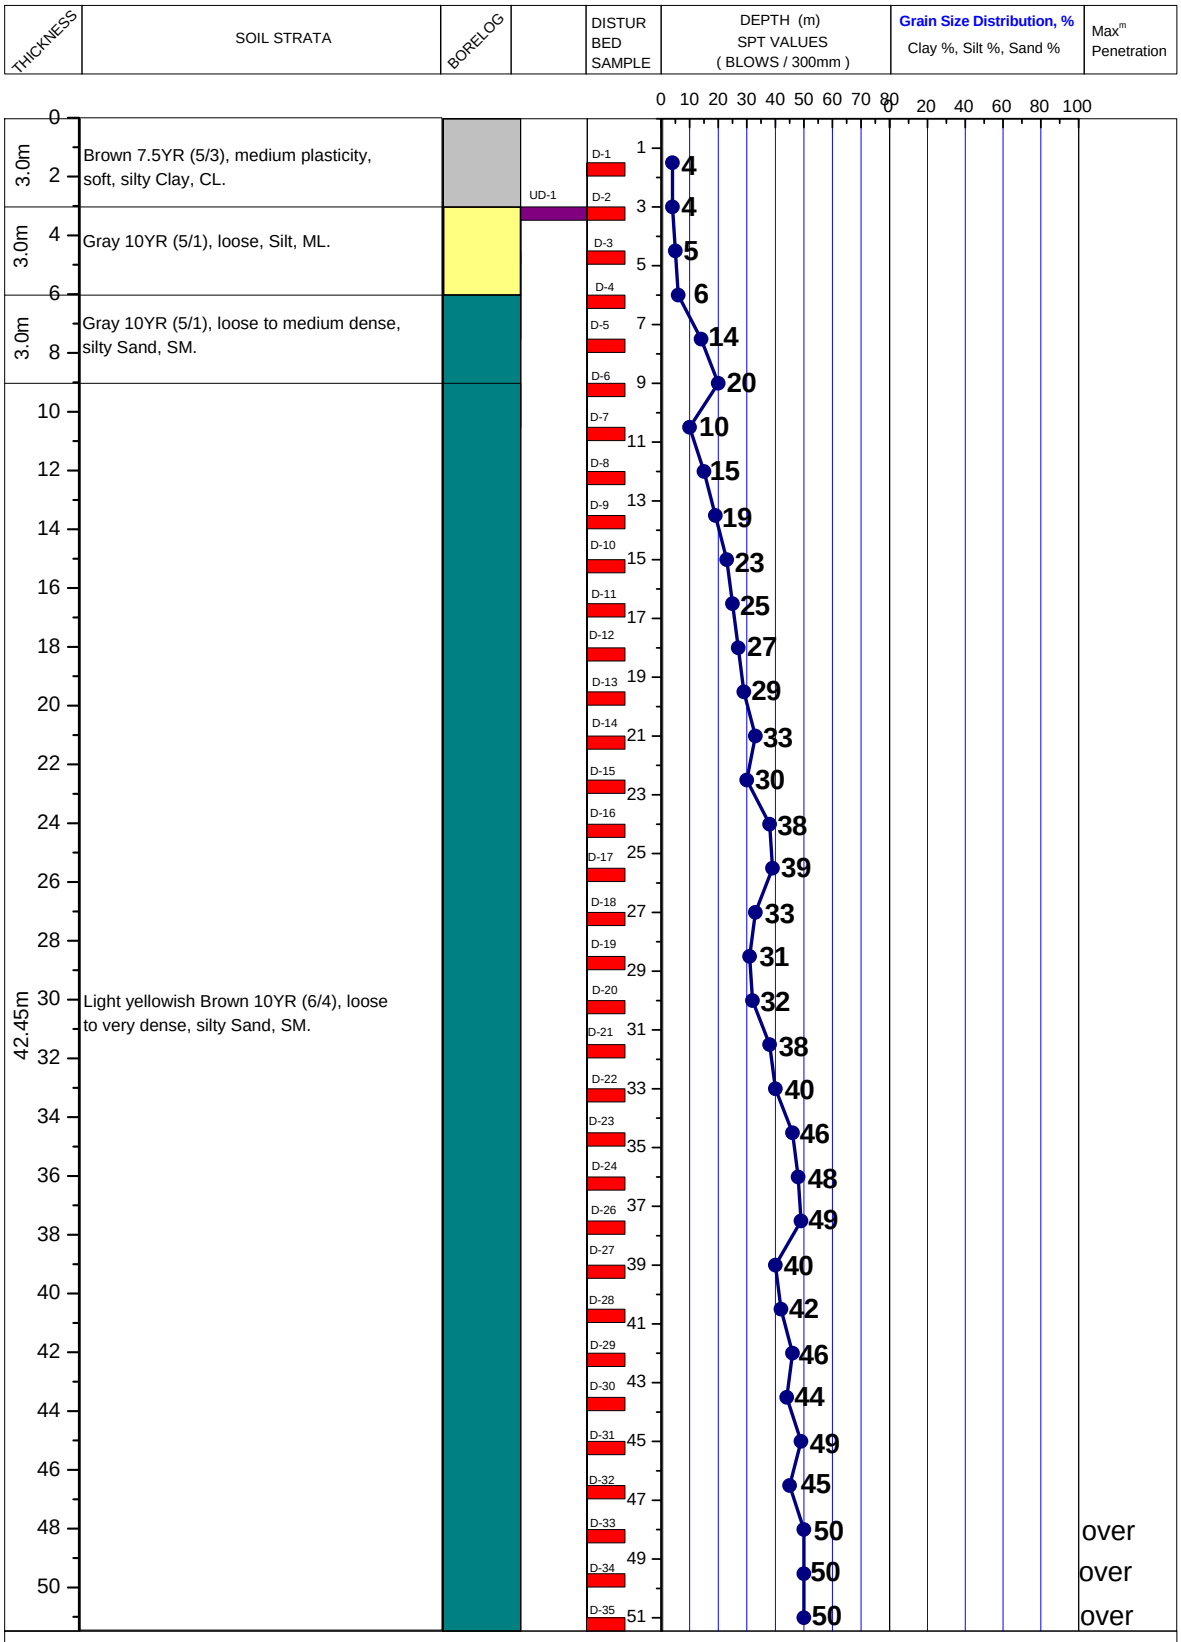


LEGEND FOR BORELOG AND GRAIN SIZE DISTRIBUTION (BASED ON 'ASTM CLASSIFICATION D-2487')

PLASTIC CLAY	SILT	PEAT/HIGHLY ORGANIC SOIL	UNDISTURBED SAMPLE
MICACEOUS FINE SAND/SILT	SAND	SHALE	DISTURBED SAMPLE

N- BLOWS DELIVERED PER FOOT BY A 140 LB HAMMER FALLING 30 INCHES

MAX^{m} PENETRATION= 50 BLOWS. AFTER 50 BLOWS PENETRATION DEPTH WERE MEASURED

A2 PROSOIL	BOREHOLE NO: BH-1	
	LOCATION : Sarol Bazar, Bashkhali, Chittagong.	
PROJECT : Telecommunication Tower.	DEPTH OF BORING : 51.0m	R. L.: 0.76m below from Road Level.
CLIENT : AXIATA (Bangladesh) Ltd.	DATE OF BORING : 09-05-2010.	G. W. T : 6.1m below from E. G. L.

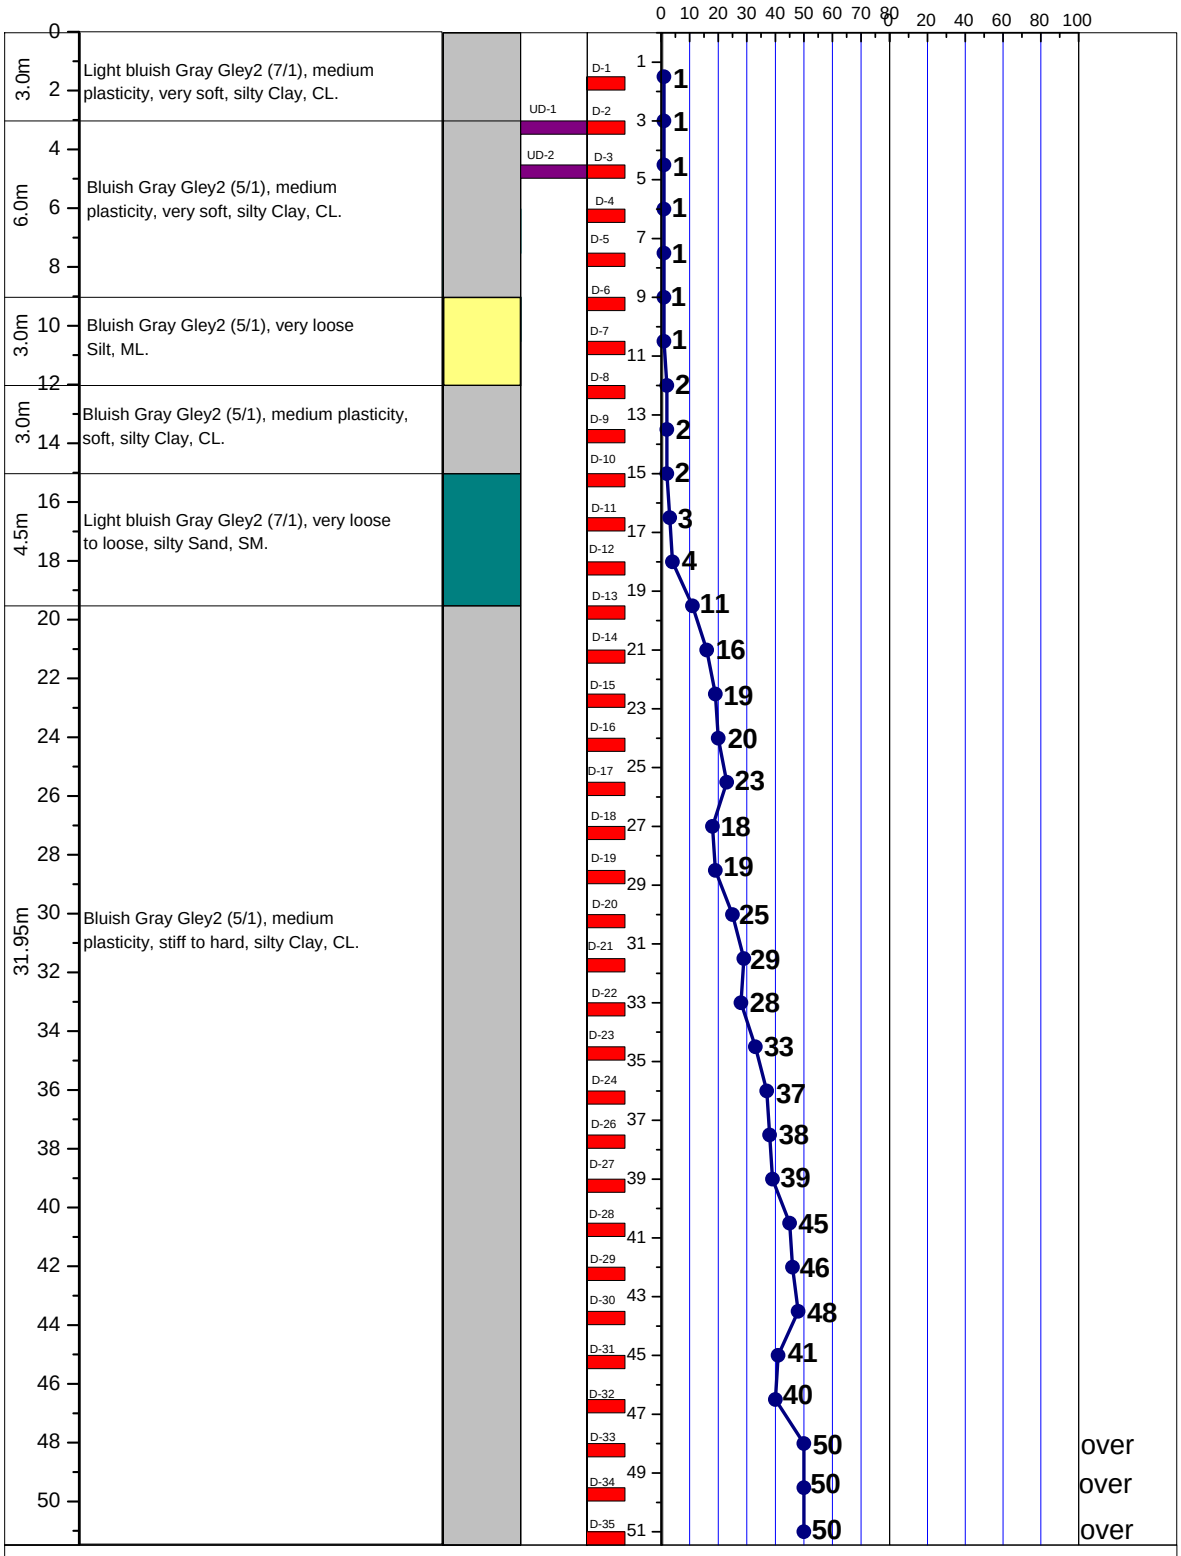


LEGEND FOR BORELOG AND GRAIN SIZE DISTRIBUTION (BASED ON 'ASTM CLASSIFICATION D-2487')

PLASTIC CLAY	SILT	PEAT/HIGHLY ORGANIC SOIL	UNDISTURBED SAMPLE
MICACEOUS FINE SAND/SILT	SAND	SHALE	DISTURBED SAMPLE

N- BLOWS DELIVERED PER FOOT BY A 140 LB HAMMER FALLING 30 INCHES

MAX^{m} PENETRATION= 50 BLOWS. AFTER 50 BLOWS PENETRATION DEPTH WERE MEASURED

A2 PROSOIL	BOREHOLE NO: BH-1	
	LOCATION : Golarhat Bazar, Satkania, Chittagong.	
PROJECT : Telecommunication Tower.	DEPTH OF BORING : 51.0m	R. L.: 1.52m below from Road Level.
CLIENT : AXIATA (Bangladesh) Ltd.	DATE OF BORING : 17-07-2010.	G. W. T : On E. G. L.

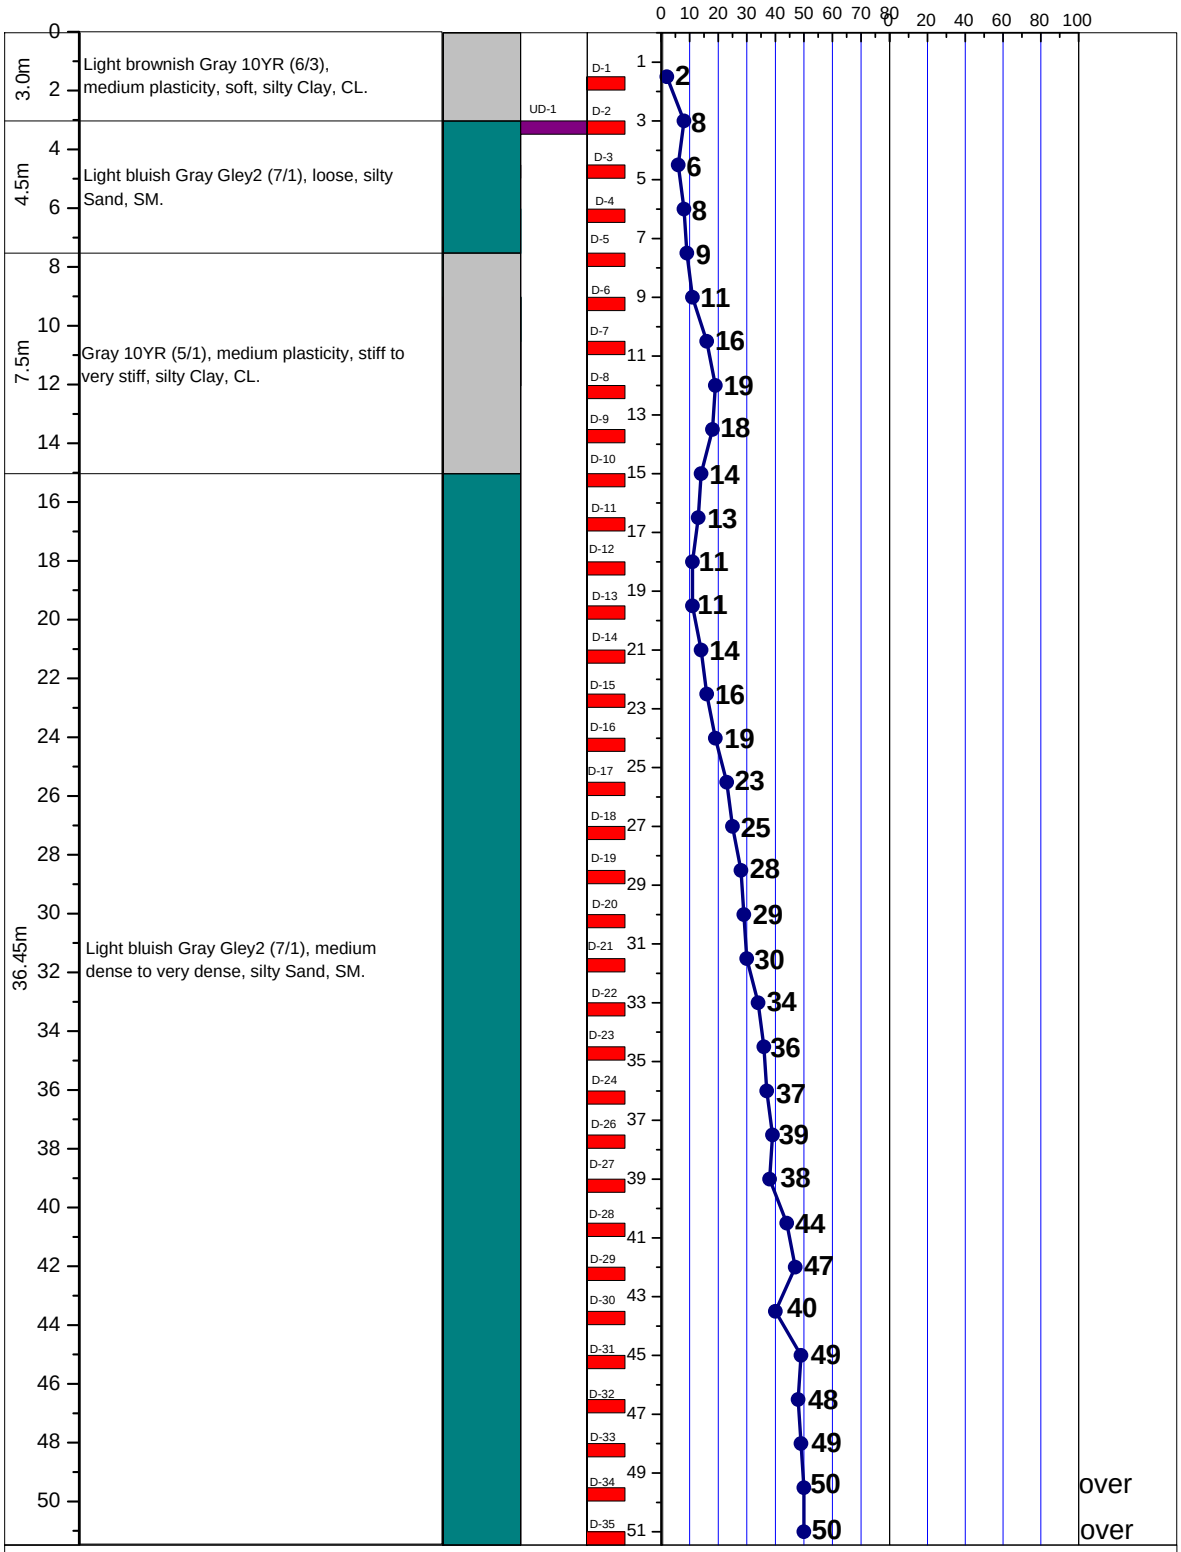


LEGEND FOR BORELOG AND GRAIN SIZE DISTRIBUTION (BASED ON 'ASTM CLASSIFICATION D-2487')

PLASTIC CLAY	SILT	PEAT/HIGHLY ORGANIC SOIL	UNDISTURBED SAMPLE
MICACEOUS FINE SAND/SILT	SAND	SHALE	DISTURBED SAMPLE

N- BLOWS DELIVERED PER FOOT BY A 140 LB HAMMER FALLING 30 INCHES

MAX^{m} PENETRATION= 50 BLOWS. AFTER 50 BLOWS PENETRATION DEPTH WERE MEASURED

A2	PROSOIL	BOREHOLE NO: BH-1	
		LOCATION : Shahabazar, Bashkhali.	
PROJECT : Telecommunication Tower.		DEPTH OF BORING : 51.0m	R. L.: 0.91m below from Road Level.
CLIENT : AXIATA (Bangladesh) Ltd.		DATE OF BORING : 03-01-2009.	G. W. T : 0.91m below from E. G. L.

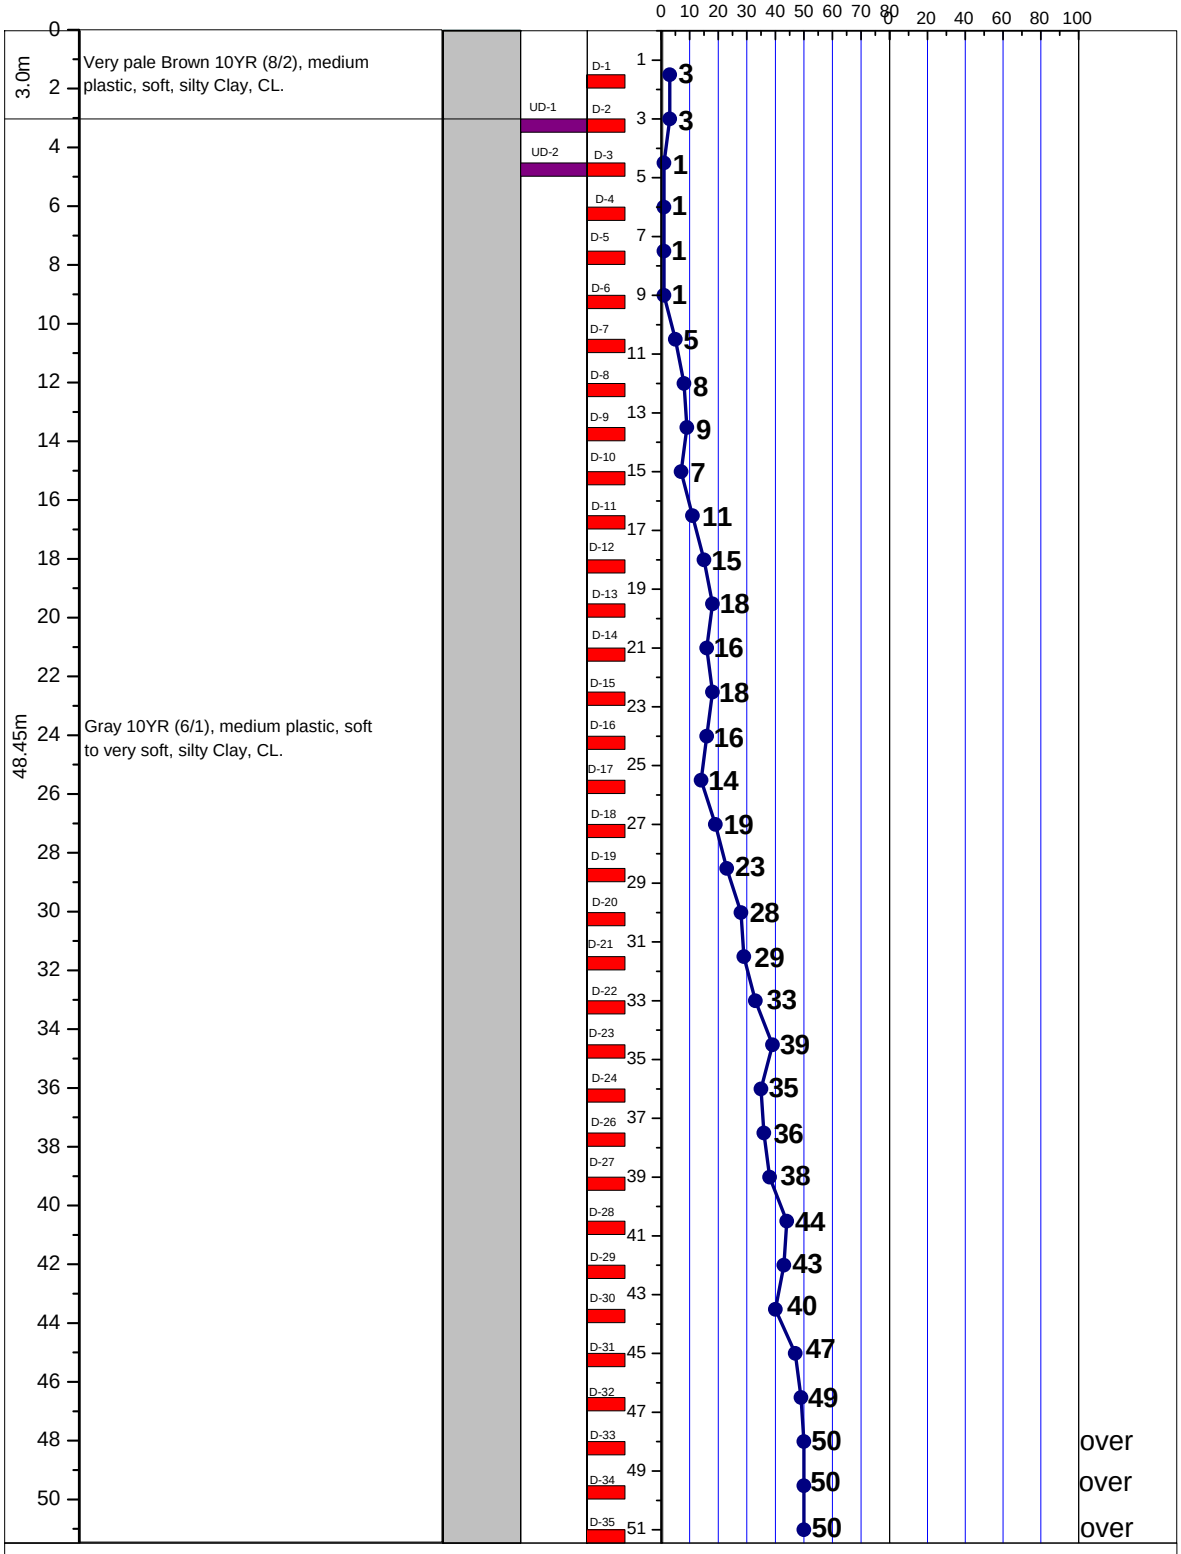


LEGEND FOR BORELOG AND GRAIN SIZE DISTRIBUTION (BASED ON 'ASTM CLASSIFICATION D-2487')

PLASTIC CLAY	SILT	PEAT/HIGHLY ORGANIC SOIL	UNDISTURBED SAMPLE
MICACEOUS FINE SAND/SILT	SAND	SHALE	DISTURBED SAMPLE

N- BLOWS DELIVERED PER FOOT BY A 140 LB HAMMER FALLING 30 INCHES

MAX^{m} PENETRATION= 50 BLOWS. AFTER 50 BLOWS PENETRATION DEPTH WERE MEASURED

A2 PROSOIL	BOREHOLE NO: BH-1	
	LOCATION : Shakal Bazar, Bashkhali.	
PROJECT : Telecommunication Tower.	DEPTH OF BORING : 51.0m	R. L.: 0.91m below from Road Level.
CLIENT : AXIATA (Bangladesh) Ltd.	DATE OF BORING : 28-03-2010.	G. W. T : 1.52m below from E. G. L.

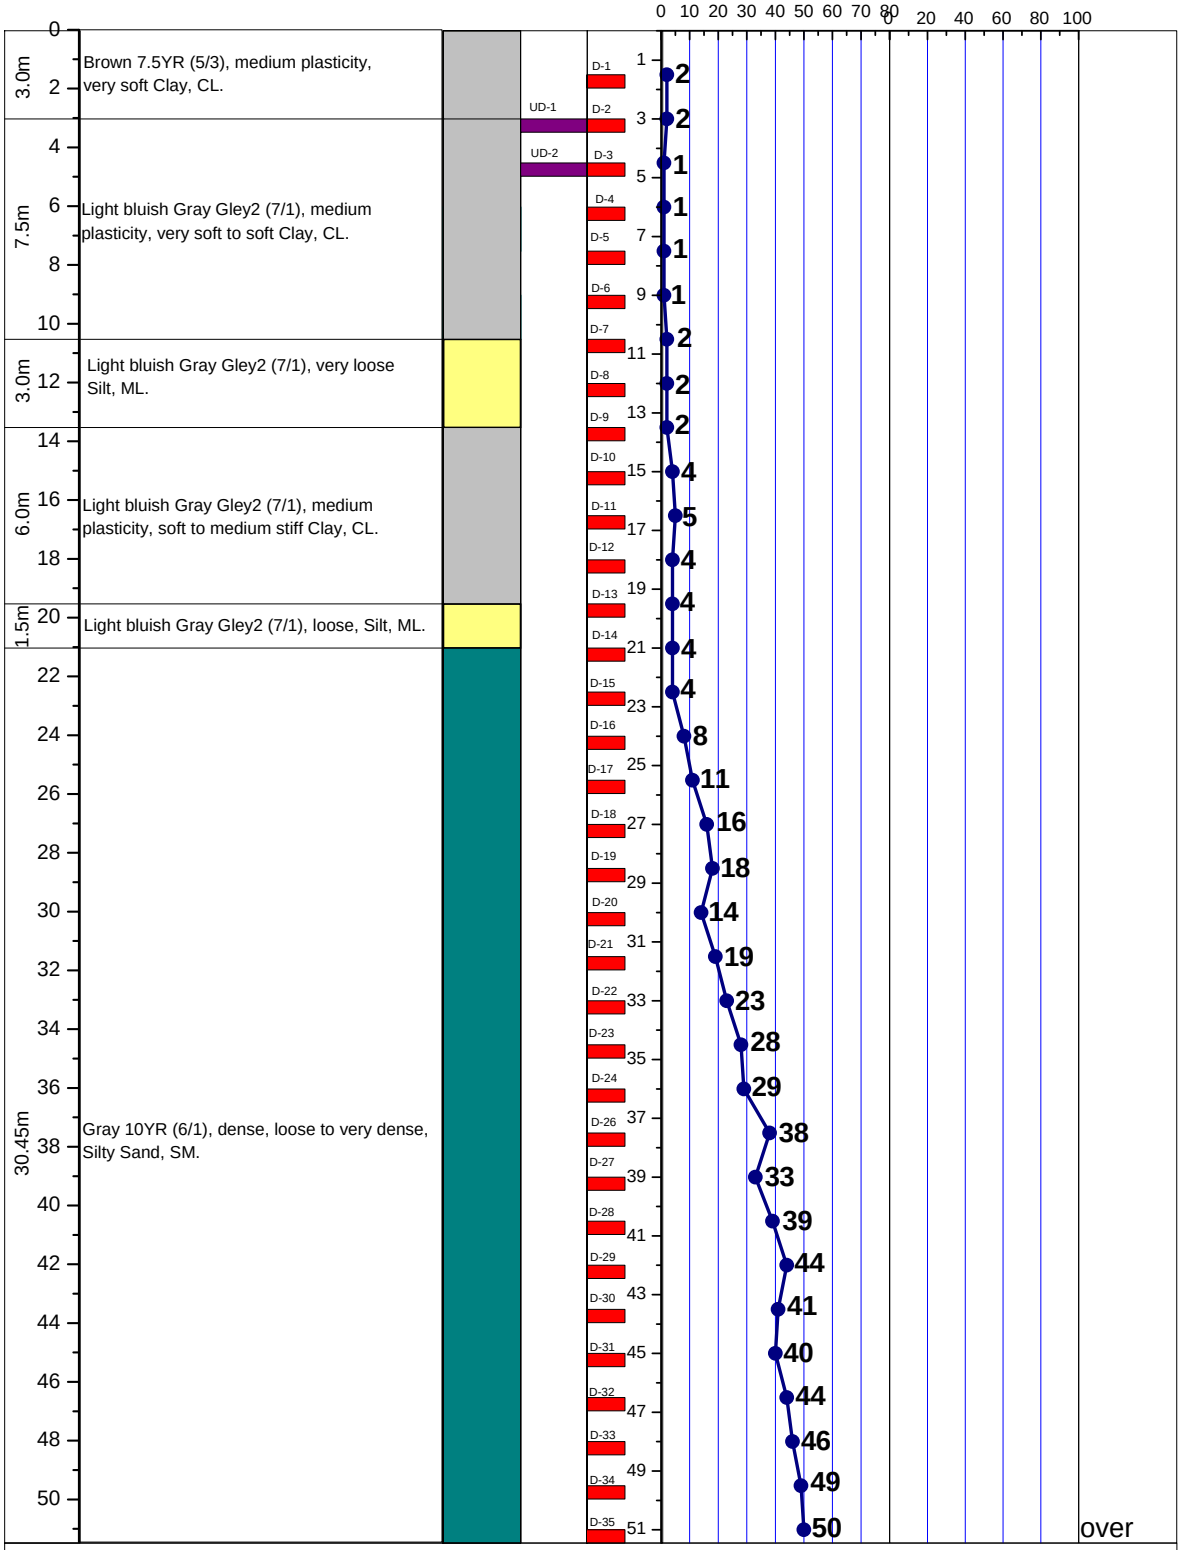


LEGEND FOR BORELOG AND GRAIN SIZE DISTRIBUTION (BASED ON 'ASTM CLASSIFICATION D-2487')

PLASTIC CLAY	SILT	PEAT/HIGHLY ORGANIC SOIL	UNDISTURBED SAMPLE
MICACEOUS FINE SAND/SILT	SAND	SHALE	DISTURBED SAMPLE

N- BLOWS DELIVERED PER FOOT BY A 140 LB HAMMER FALLING 30 INCHES

MAX^{m} PENETRATION= 50 BLOWS. AFTER 50 BLOWS PENETRATION DEPTH WERE MEASURED

A2 PROSOIL	BOREHOLE NO: BH-1	
	LOCATION : Shantir Bazar, Boalkhali, Chittagong.	
PROJECT : Telecommunication Tower.	DEPTH OF BORING : 51.0m	R. L.: 0.91m below from Road Level.
CLIENT : AXIATA (Bangladesh) Ltd.	DATE OF BORING : 17-02-2010.	G. W. T : 10.10m above from E. G. L.

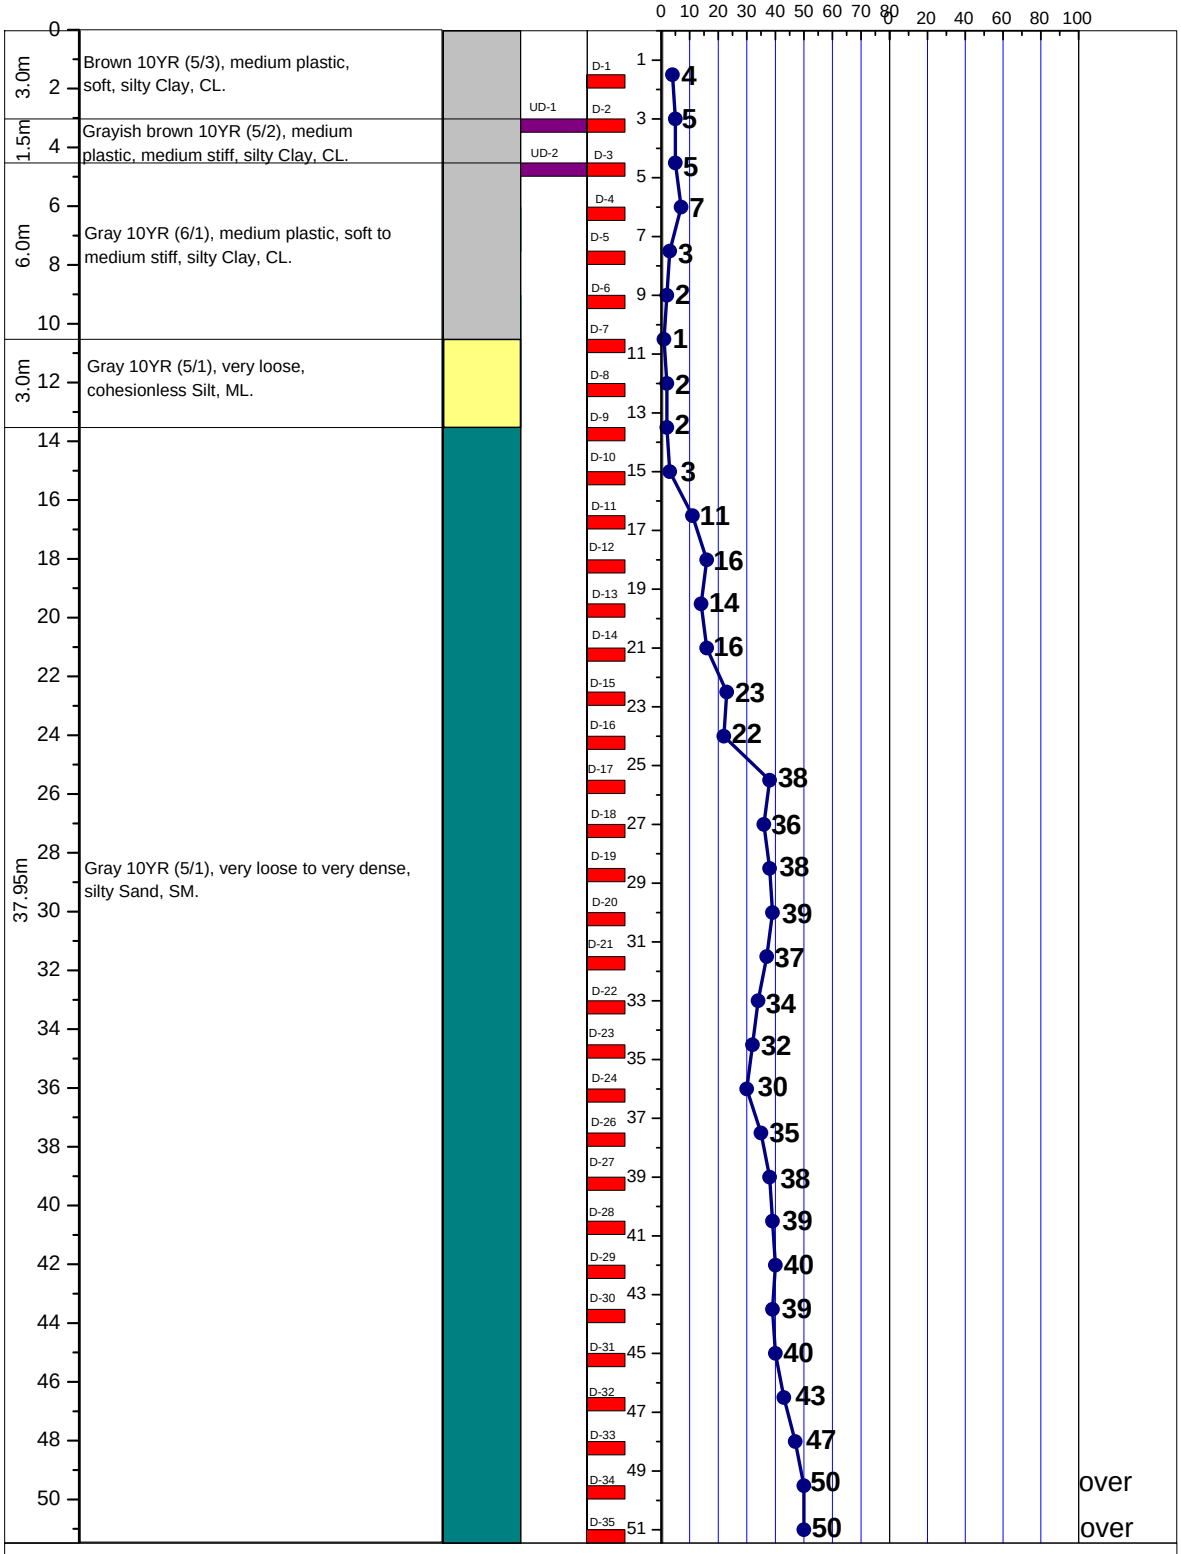


LEGEND FOR BORELOG AND GRAIN SIZE DISTRIBUTION (BASED ON 'ASTM CLASSIFICATION D-2487')

PLASTIC CLAY	SILT	PEAT/HIGHLY ORGANIC SOIL	UNDISTURBED SAMPLE
MICACEOUS FINE SAND/SILT	SAND	SHALE	DISTURBED SAMPLE

N- BLOWS DELIVERED PER FOOT BY A 140 LB HAMMER FALLING 30 INCHES

MAX^{m} PENETRATION= 50 BLOWS. AFTER 50 BLOWS PENETRATION DEPTH WERE MEASURED

A2 PROSOIL	BOREHOLE NO: BH-1	
	LOCATION : Shilghata, Satkania, Chittagong.	
PROJECT : Telecommunication Tower.	DEPTH OF BORING : 51.0m	R. L.: 0.45m below from Road Level.
CLIENT : TM International, Bangladesh Ltd.	DATE OF BORING : 05-02-2009	G. W. T : 4.57m below from E. G. L.

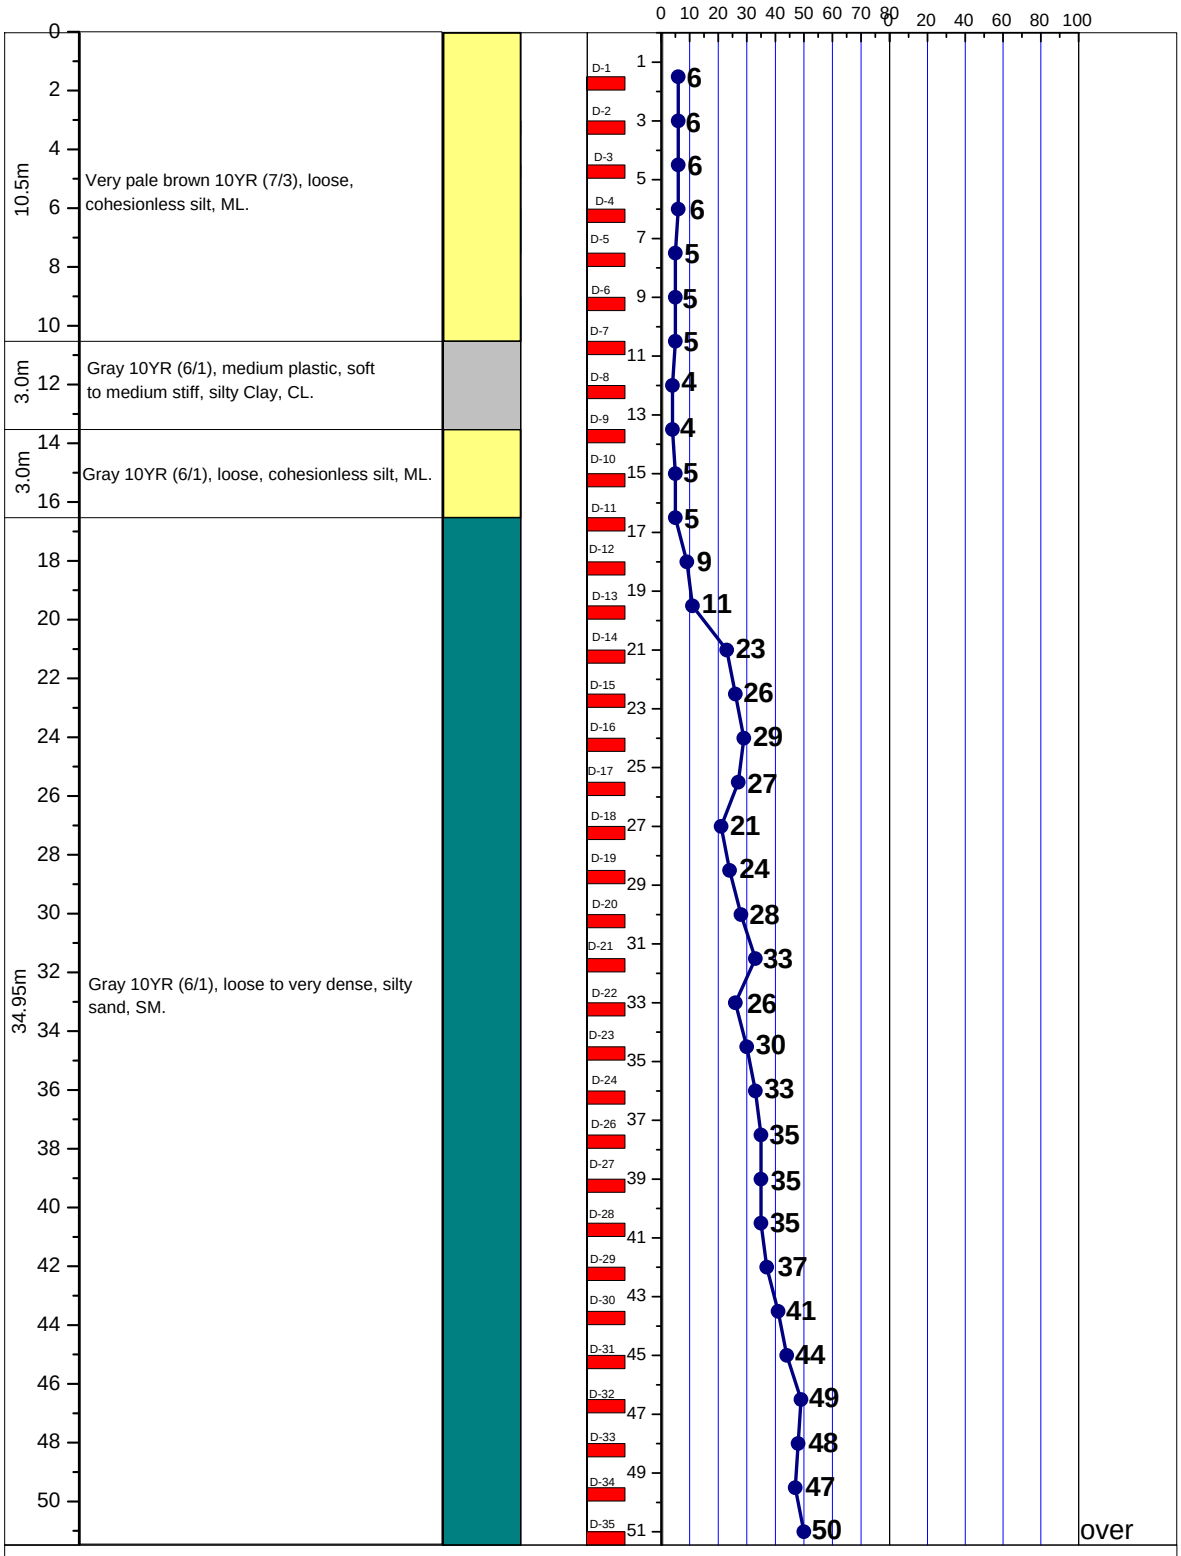


LEGEND FOR BORELOG AND GRAIN SIZE DISTRIBUTION (BASED ON 'ASTM CLASSIFICATION D-2487')

PLASTIC CLAY	SILT	PEAT/HIGHLY ORGANIC SOIL	UNDISTURBED SAMPLE
MICACEOUS FINE SAND/SILT	SAND	SHALE	DISTURBED SAMPLE

N- BLOWS DELIVERED PER FOOT BY A 140 LB HAMMER FALLING 30 INCHES

MAX^{m} PENETRATION= 50 BLOWS. AFTER 50 BLOWS PENETRATION DEPTH WERE MEASURED

A2 PROSOIL	BOREHOLE NO: BH-1	
	LOCATION : South Joarey, Chandanish, Chittagong.	
PROJECT : Telecommunication Tower.	DEPTH OF BORING : 51.0m	R. L.: 0.91m below from Road Level.
CLIENT : AXIATA (Bangladesh) Ltd.	DATE OF BORING : 29-05-2010.	G. W. T : 0.1m above from E. G. L.

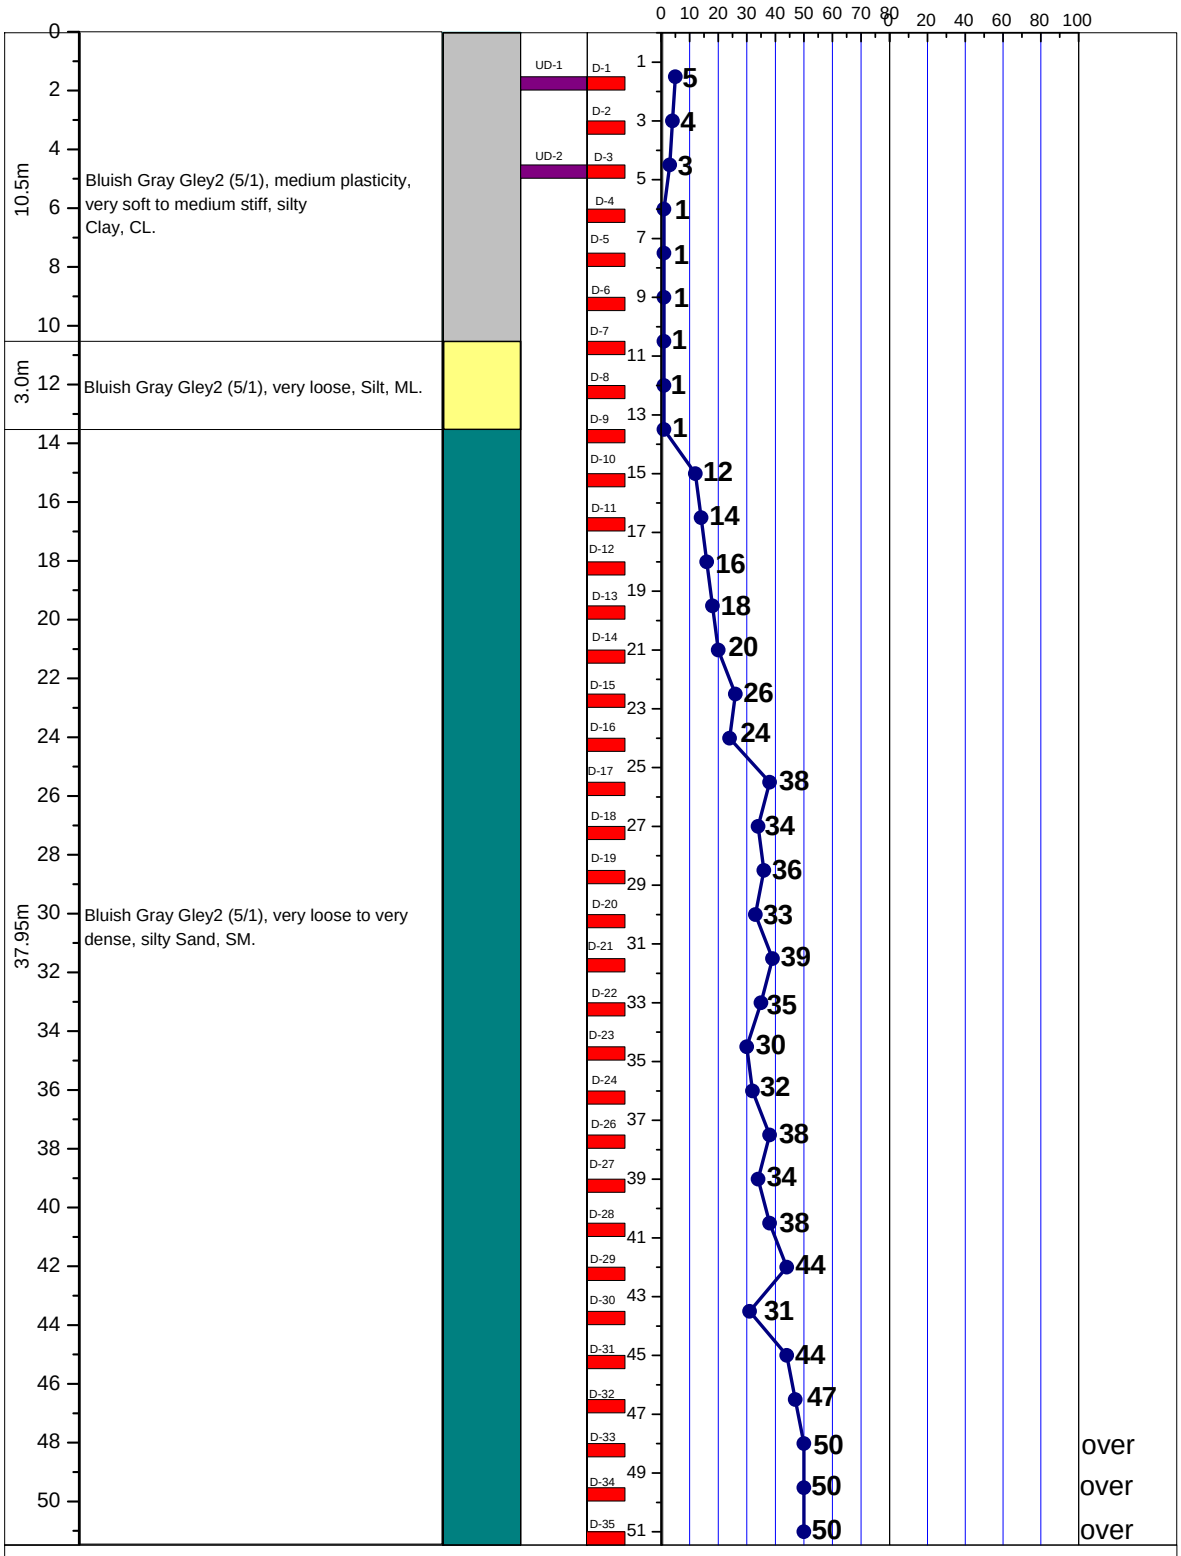


LEGEND FOR BORELOG AND GRAIN SIZE DISTRIBUTION (BASED ON 'ASTM CLASSIFICATION D-2487')

PLASTIC CLAY	SILT	PEAT/HIGHLY ORGANIC SOIL	UNDISTURBED SAMPLE
MICACEOUS FINE SAND/SILT	SAND	SHALE	DISTURBED SAMPLE

N- BLOWS DELIVERED PER FOOT BY A 140 LB HAMMER FALLING 30 INCHES

MAX^{m} PENETRATION= 50 BLOWS. AFTER 50 BLOWS PENETRATION DEPTH WERE MEASURED

A2 PROSOIL	BOREHOLE NO: BH-1	
	LOCATION : Teurikhil, Lohagora, Chittagong.	
PROJECT : Telecommunication Tower.	DEPTH OF BORING : 51.0m	R. L.: 1.71m below from Road Level.
CLIENT : AXIATA (Bangladesh) Ltd.	DATE OF BORING : 13-05-2010.	G. W. T : 4.57m below from E. G. L.

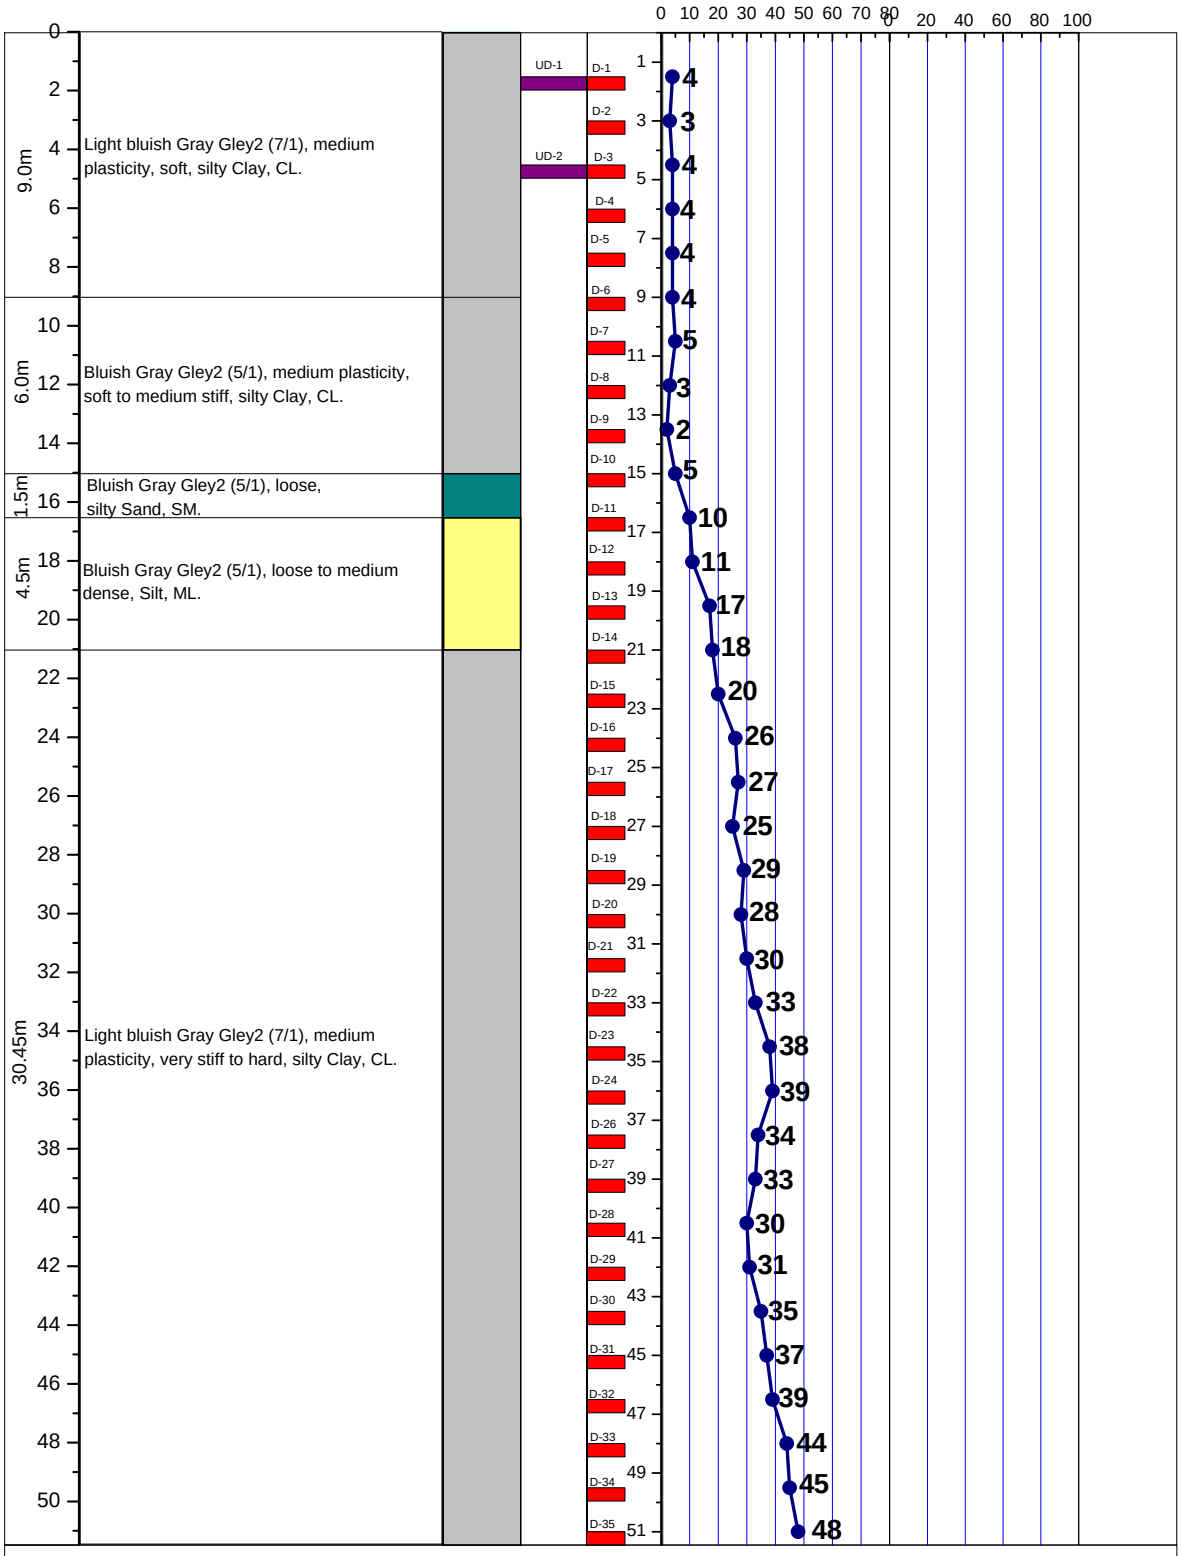


LEGEND FOR BORELOG AND GRAIN SIZE DISTRIBUTION (BASED ON 'ASTM CLASSIFICATION D-2487')

PLASTIC CLAY	SILT	PEAT/HIGHLY ORGANIC SOIL	UNDISTURBED SAMPLE
MICACEOUS FINE SAND/SILT	SAND	SHALE	DISTURBED SAMPLE

N- BLOWS DELIVERED PER FOOT BY A 140 LB HAMMER FALLING 30 INCHES

MAX^{m} PENETRATION= 50 BLOWS. AFTER 50 BLOWS PENETRATION DEPTH WERE MEASURED

A2 PROSOIL	BOREHOLE NO: BH-1	
	LOCATION : Uttar Bakkhain, Khashiaish, Patiya, Chittagong.	
PROJECT : Telecommunication Tower.	DEPTH OF BORING : 51.0m	R. L.: 0.91m below from Road Level.
CLIENT : AXIATA (Bangladesh) Ltd.	DATE OF BORING : 23-12-2012.	G. W. T : 0.30m above from E. G. L.

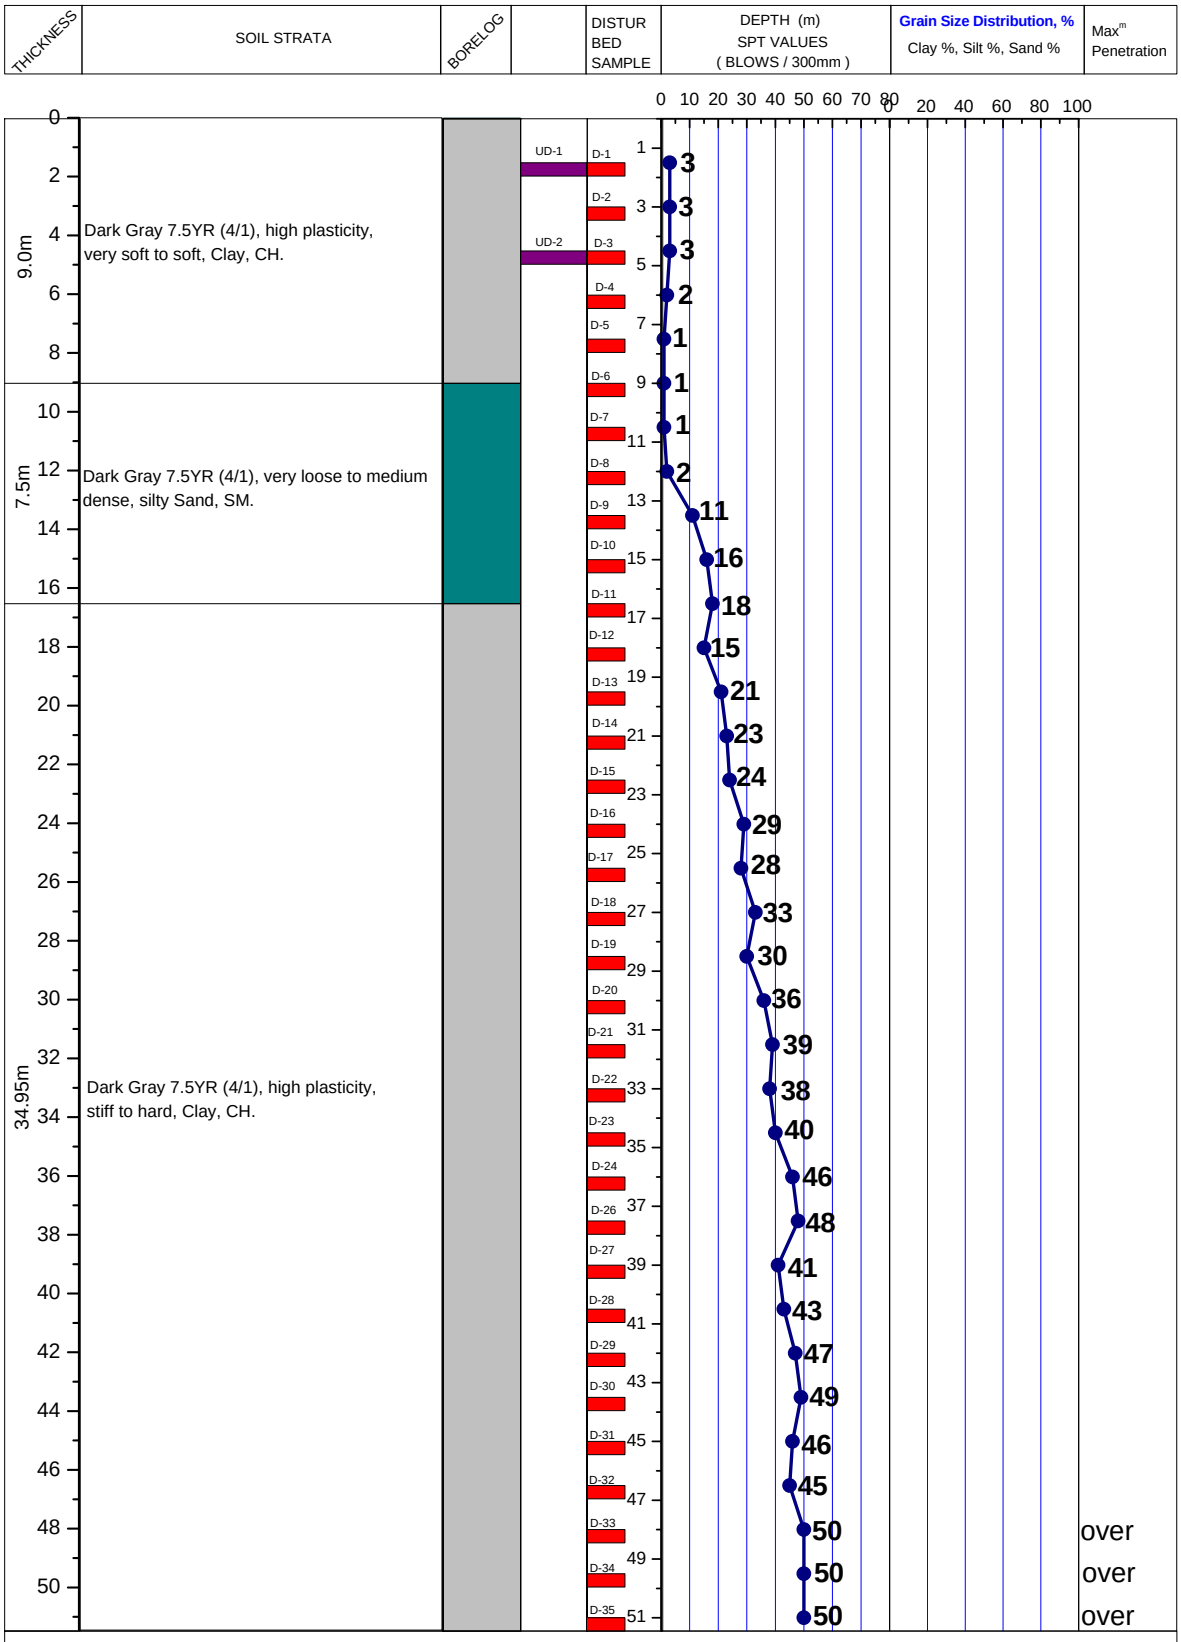


LEGEND FOR BORELOG AND GRAIN SIZE DISTRIBUTION (BASED ON 'ASTM CLASSIFICATION D-2487')

PLASTIC CLAY	SILT	PEAT/HIGHLY ORGANIC SOIL	UNDISTURBED SAMPLE
MICACEOUS FINE SAND/SILT	SAND	SHALE	DISTURBED SAMPLE

N- BLOWS DELIVERED PER FOOT BY A 140 LB HAMMER FALLING 30 INCHES

MAX^{m} PENETRATION= 50 BLOWS. AFTER 50 BLOWS PENETRATION DEPTH WERE MEASURED

A2 PROSOIL	BOREHOLE NO: BH-1	
	LOCATION : Amin Centre Bazar, Satkania, Chittagong.	
PROJECT : Telecommunication Tower.	DEPTH OF BORING : 51.0m	R. L.: 0.91m below from Road Level.
CLIENT : AXIATA (Bangladesh) Ltd.	DATE OF BORING : 06-10-2010.	G. W. T : Rain Water.

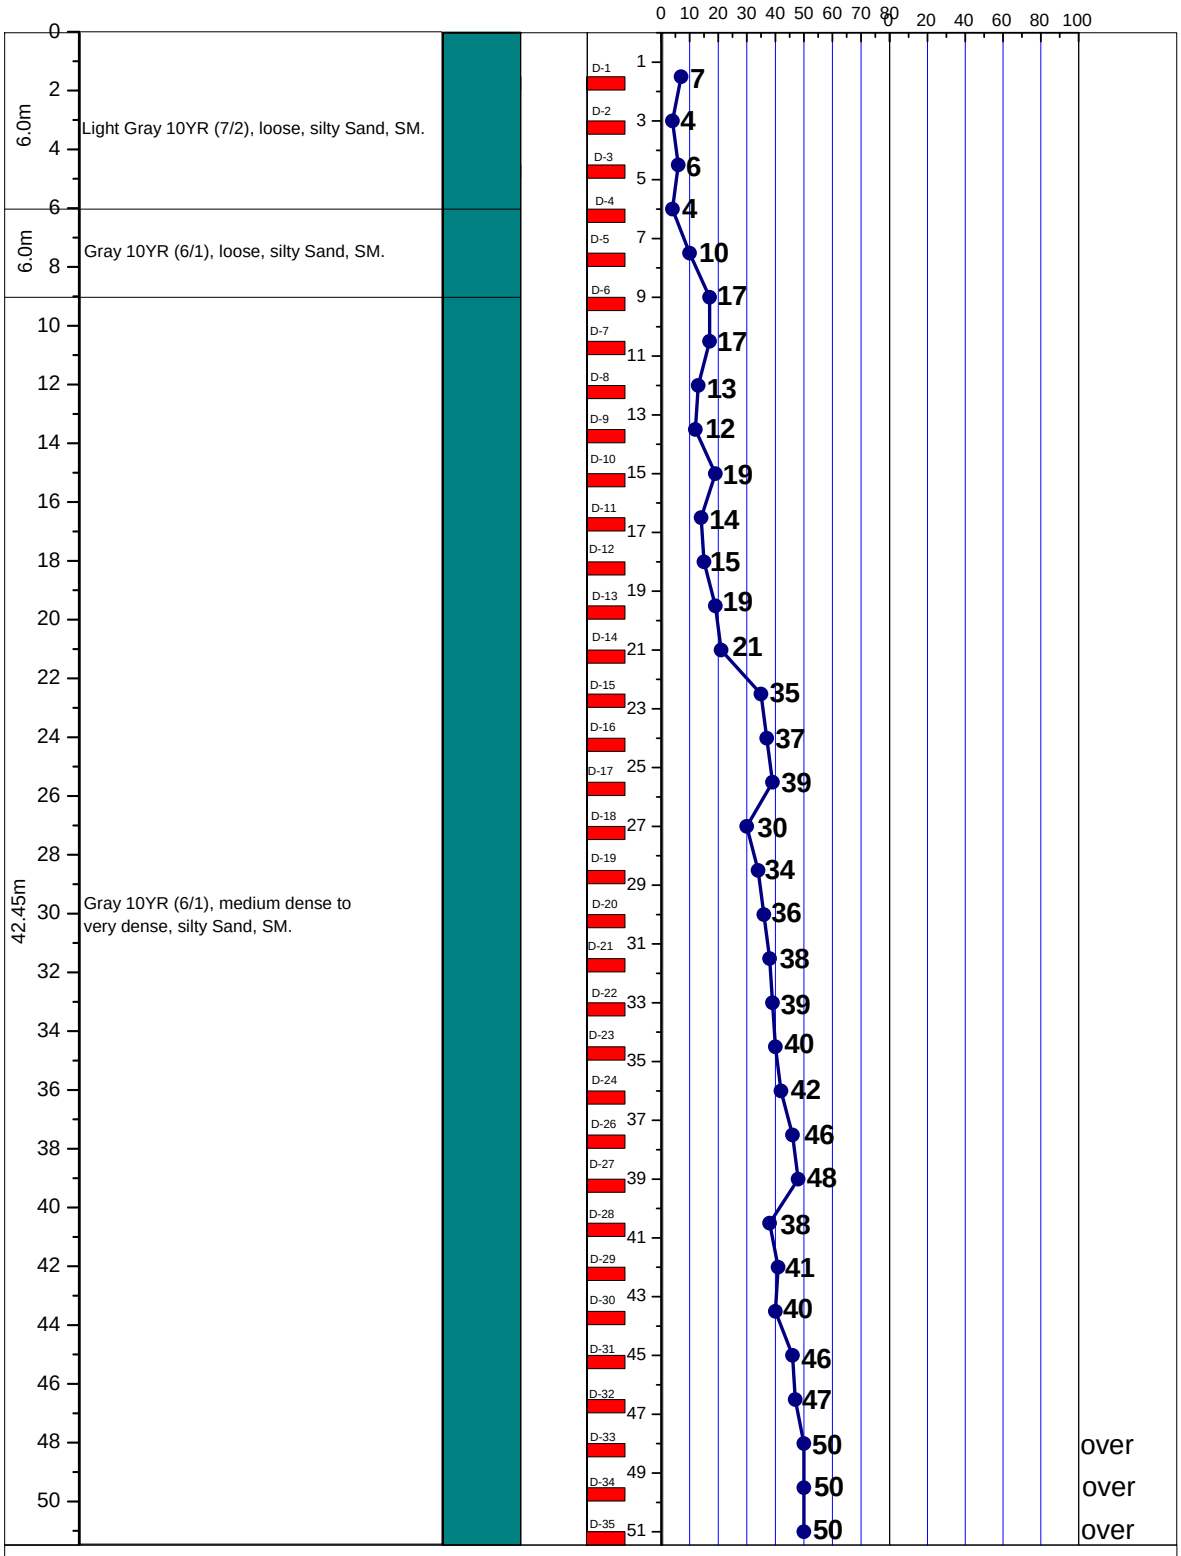

LEGEND FOR BORELOG AND GRAIN SIZE DISTRIBUTION (BASED ON 'ASTM CLASSIFICATION D-2487')


PLASTIC CLAY	SILT	PEAT/HIGHLY ORGANIC SOIL	UNDISTURBED SAMPLE
MICACEOUS FINE SAND/SILT	SAND	SHALE	DISTURBED SAMPLE

N- BLOWS DELIVERED PER FOOT BY A 140 LB HAMMER FALLING 30 INCHES

MAX^{m} PENETRATION= 50 BLOWS. AFTER 50 BLOWS PENETRATION DEPTH WERE MEASURED

A2 PROSOIL	BOREHOLE NO: BH-1	
	LOCATION : Dohazari2, Chandonish, Chittagong.	
PROJECT : Telecommunication Tower.	DEPTH OF BORING : 51.0m	R. L.: 1.37m below from Road Level.
CLIENT : AXIATA (Bangladesh) Ltd.	DATE OF BORING : 27-11-2010.	G. W. T : 2.44m below from E. G. L.

THICKNESS	SOIL STRATA	BORELOG		DISTURBED SAMPLE	DEPTH (m) SPT VALUES (BLOWS / 300mm)	Grain Size Distribution, % Clay %, Silt %, Sand %	Max^{m} Penetration
4.5m	Brown 10YR (5/3), high plasticity, very soft, silty Clay, CH.		UD-1	D-1	1		
			UD-2	D-2	3		
3.0m	Light Gray 10YR (7/2), medium plasticity, soft to medium stiff, silty Clay, CL.			D-3	5		
				D-4	7		
7.5m	Light Gray 10YR (7/1),high plasticity, very soft to medium stiff, silty Clay, CH.			D-5	9		
				D-6	11		
				D-7	13		
				D-8	15		
				D-9	17		
				D-10	19		
36.45m	Gray 10YR (6/1), high plasticity, very soft to hard, organic Clay, CL.			D-11	21		
				D-12	23		
				D-13	25		
				D-14	27		
				D-15	29		
				D-16	31		
				D-17	33		
				D-18	35		
				D-19	37		
				D-20	39		
				D-21	41		
				D-22	43		
				D-23	45		
				D-24	47		
				D-26	49		
				D-27	51		
				D-28			
				D-29			
				D-30			
				D-31			
				D-32			
				D-33			
				D-34			
				D-35			

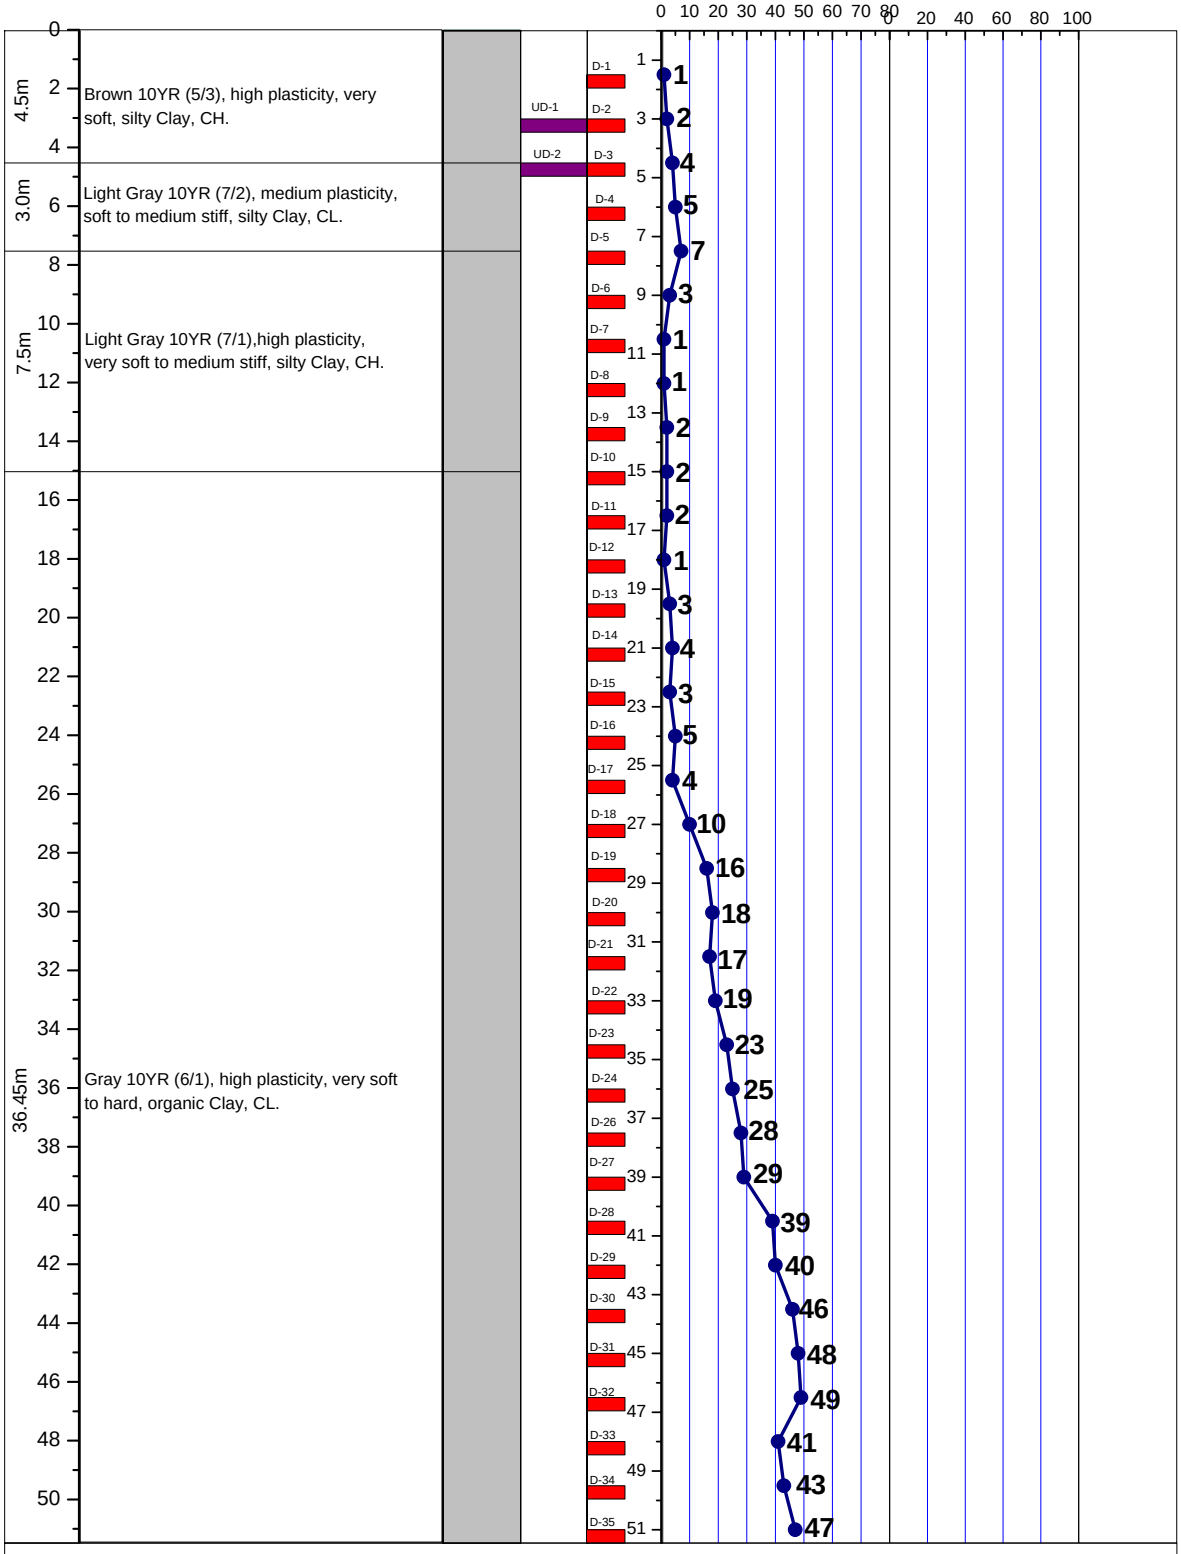


LEGEND FOR BORELOG AND GRAIN SIZE DISTRIBUTION (BASED ON 'ASTM CLASSIFICATION D-2487')

PLASTIC CLAY	SILT	PEAT/HIGHLY ORGANIC SOIL	UNDISTURBED SAMPLE
MICACEOUS FINE SAND/SILT	SAND	SHALE	DISTURBED SAMPLE

N- BLOWS DELIVERED PER FOOT BY A 140 LB HAMMER FALLING 30 INCHES

MAX^{m} PENETRATION= 50 BLOWS. AFTER 50 BLOWS PENETRATION DEPTH WERE MEASURED

A2 PROSOIL	BOREHOLE NO: BH-1	
	LOCATION : Gasbari2, Chandainash, Chittagong.	
PROJECT : Telecommunication Tower.	DEPTH OF BORING : 51.0m	R. L.: 1.35m below from Road Level.
CLIENT : AXIATA (Bangladesh) Ltd.	DATE OF BORING : 20-10-2010.	G. W. T : 0.60m above from E. G. L.

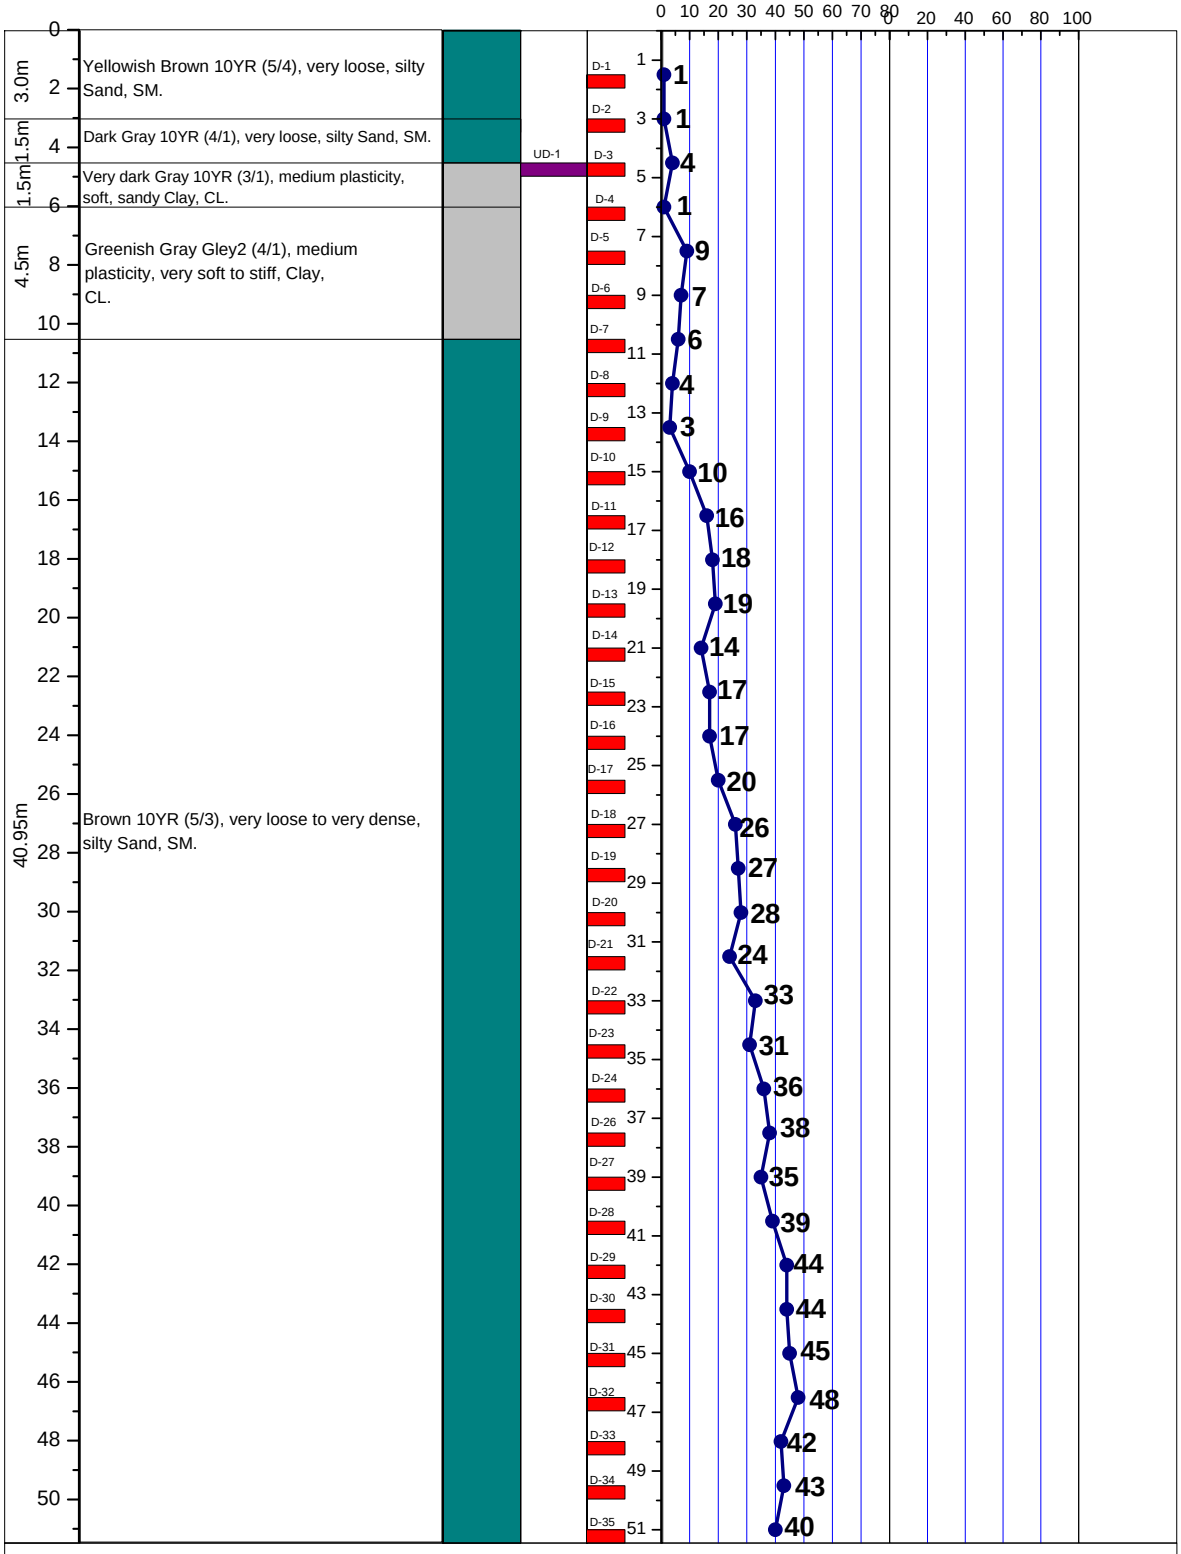


LEGEND FOR BORELOG AND GRAIN SIZE DISTRIBUTION (BASED ON 'ASTM CLASSIFICATION D-2487')

PLASTIC CLAY	SILT	PEAT/HIGHLY ORGANIC SOIL	UNDISTURBED SAMPLE
MICACEOUS FINE SAND/SILT	SAND	SHALE	DISTURBED SAMPLE

N- BLOWS DELIVERED PER FOOT BY A 140 LB HAMMER FALLING 30 INCHES

MAX^{m} PENETRATION= 50 BLOWS. AFTER 50 BLOWS PENETRATION DEPTH WERE MEASURED

A2 PROSOIL	BOREHOLE NO: BH-1	
	LOCATION : Hollain 55m Land, Potiya, Chittagong.	
PROJECT : Telecommunication Tower.	DEPTH OF BORING : 51.0m	R. L.: 1.52m below from Road Level.
CLIENT : AXIATA (Bangladesh) Ltd.	DATE OF BORING : 21-10-2010.	G. W. T : On E. G. L.

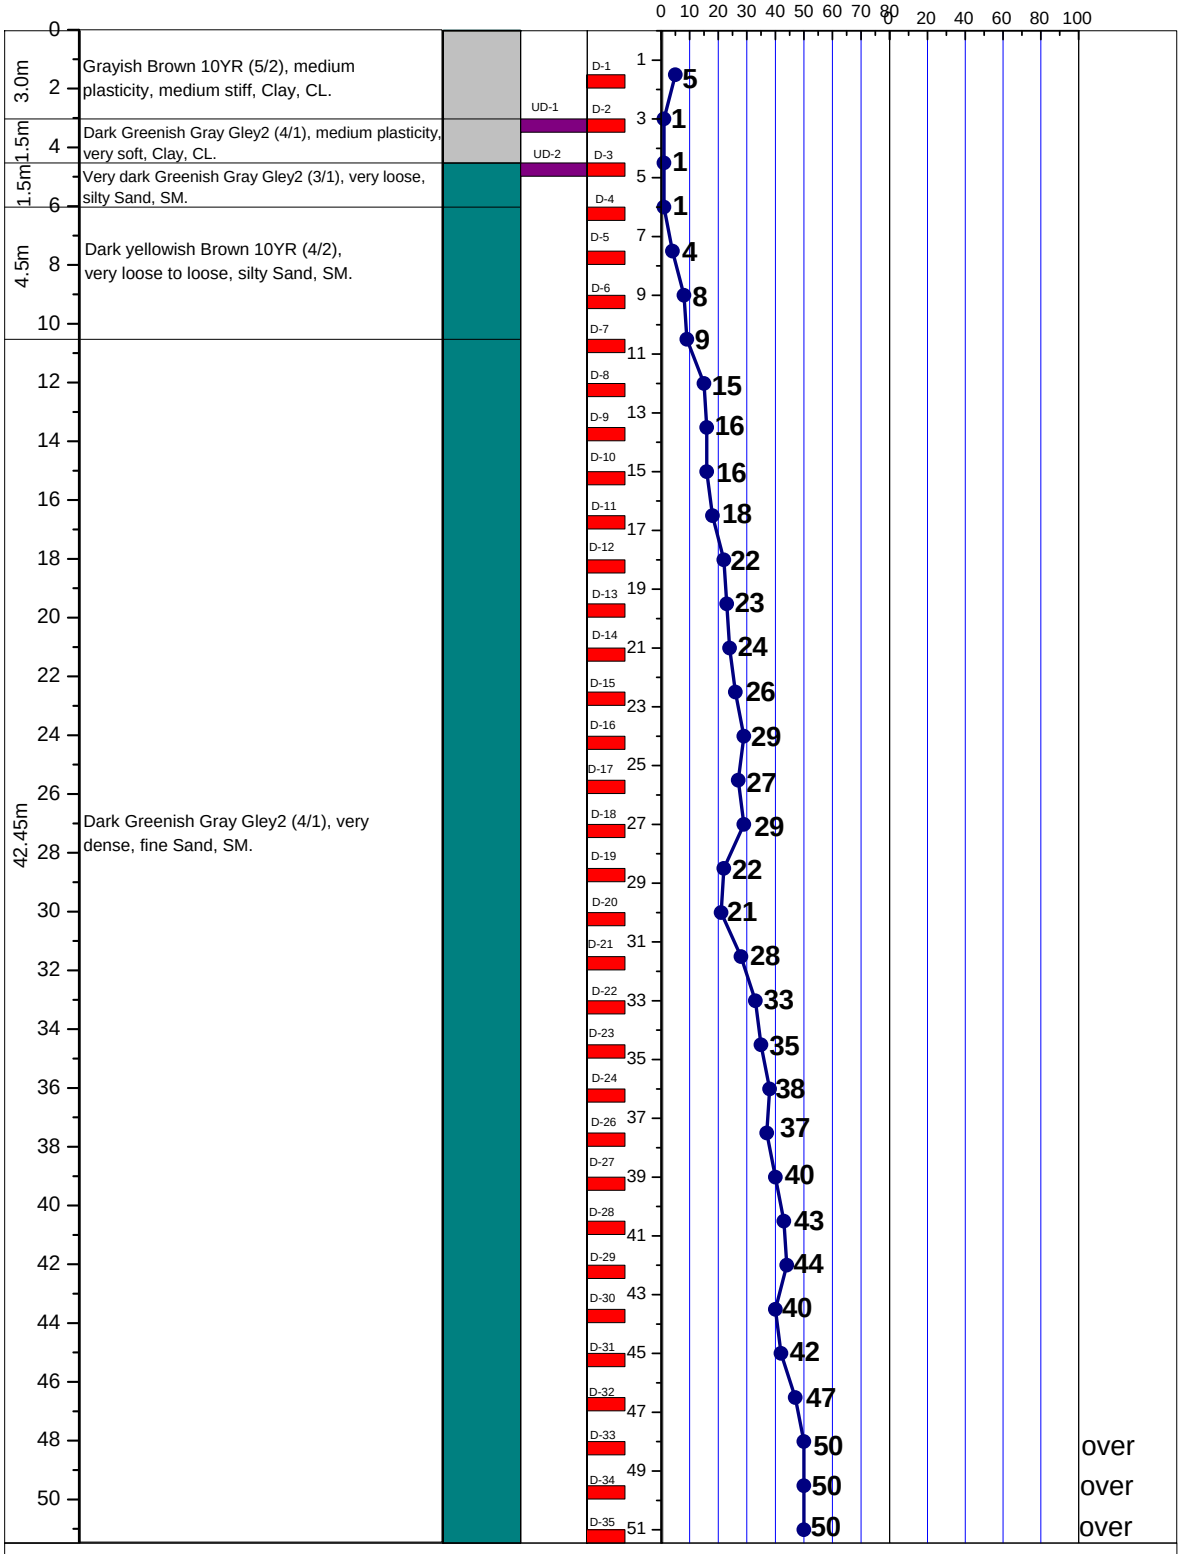


LEGEND FOR BORELOG AND GRAIN SIZE DISTRIBUTION (BASED ON 'ASTM CLASSIFICATION D-2487')

PLASTIC CLAY	SILT	PEAT/HIGHLY ORGANIC SOIL	UNDISTURBED SAMPLE
MICACEOUS FINE SAND/SILT	SAND	SHALE	DISTURBED SAMPLE

N- BLOWS DELIVERED PER FOOT BY A 140 LB HAMMER FALLING 30 INCHES

MAX^{m} PENETRATION= 50 BLOWS. AFTER 50 BLOWS PENETRATION DEPTH WERE MEASURED

A2 PROSOIL	BOREHOLE NO: BH-1	
	LOCATION : Horina, Lohagara, Chittagong.	
PROJECT : Telecommunication Tower.	DEPTH OF BORING : 51.0m	R. L.: 1.22m below from Road Level.
CLIENT : AXIATA (Bangladesh) Ltd.	DATE OF BORING : 31-07-2010.	G. W. T : On E. G. L.

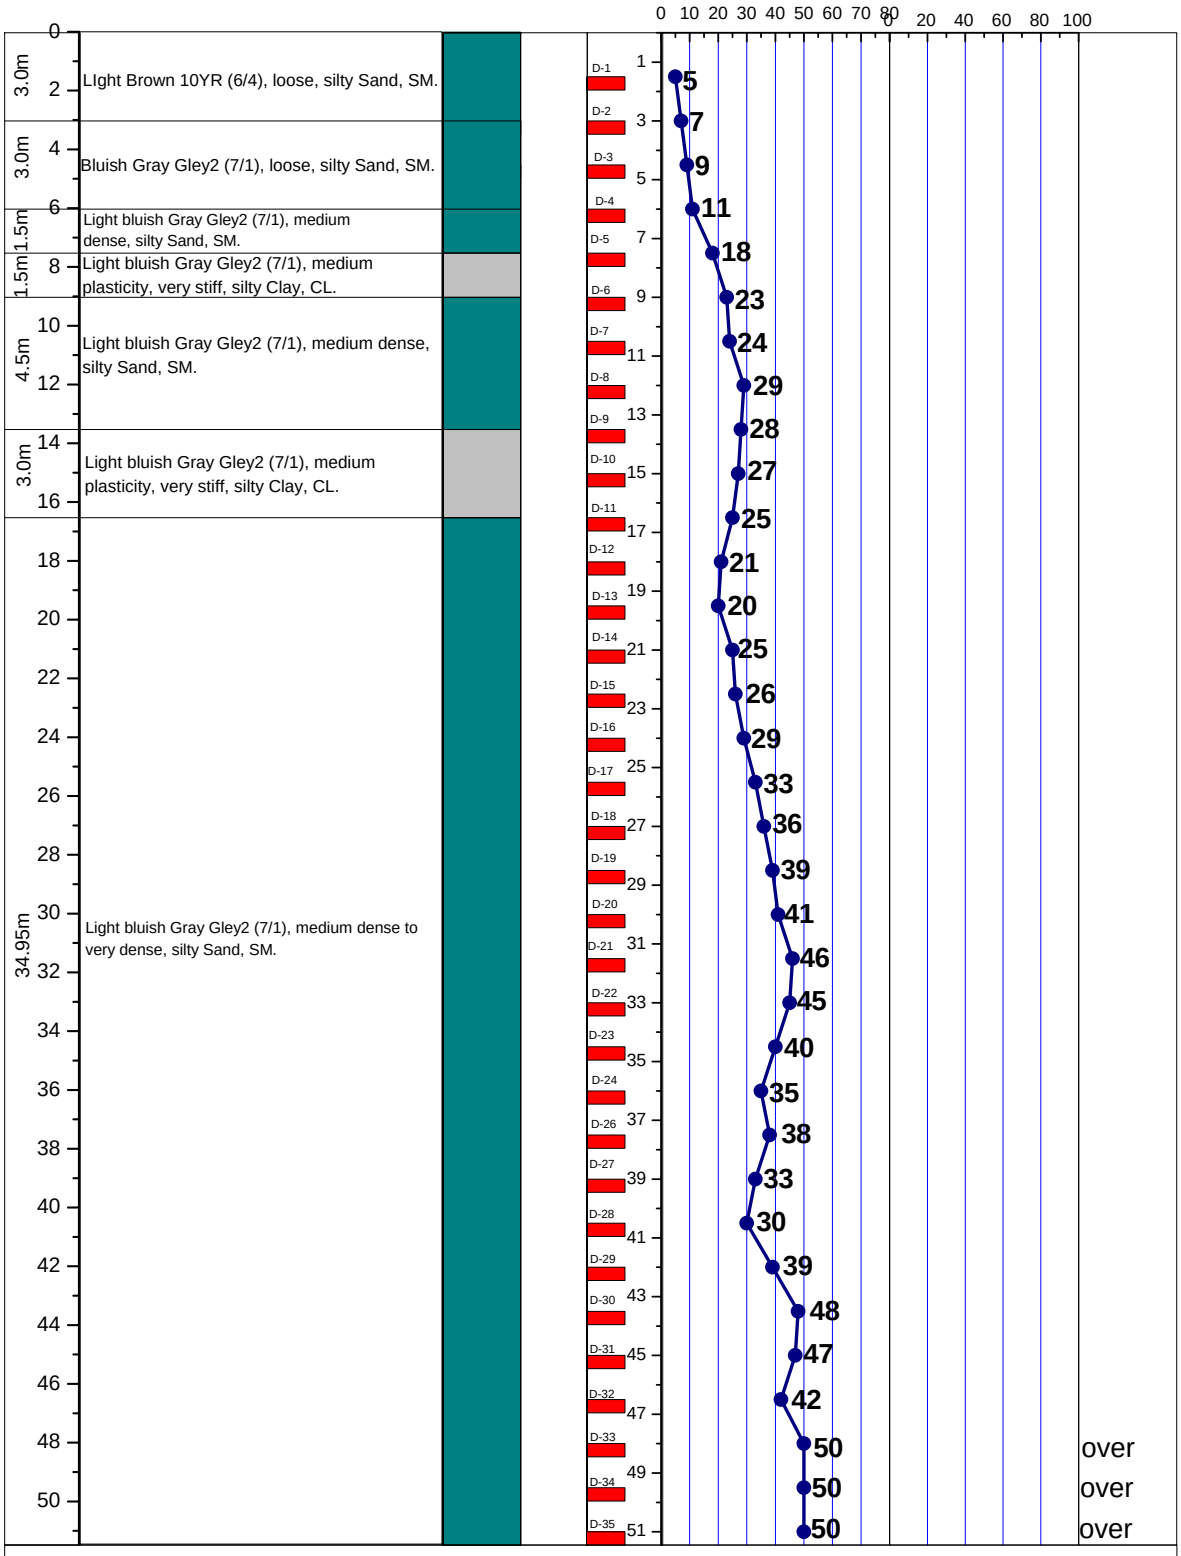


LEGEND FOR BORELOG AND GRAIN SIZE DISTRIBUTION (BASED ON 'ASTM CLASSIFICATION D-2487')

PLASTIC CLAY	SILT	PEAT/HIGHLY ORGANIC SOIL	UNDISTURBED SAMPLE
MICACEOUS FINE SAND/SILT	SAND	SHALE	DISTURBED SAMPLE

N- BLOWS DELIVERED PER FOOT BY A 140 LB HAMMER FALLING 30 INCHES

MAX^{m} PENETRATION= 50 BLOWS. AFTER 50 BLOWS PENETRATION DEPTH WERE MEASURED

A2 PROSOIL	BOREHOLE NO: BH-1	
	LOCATION : Shekerkhil, bashkhali, Chittagong.	
PROJECT : Telecommunication Tower.	DEPTH OF BORING : 51.0m	R. L.: 0.91m below from Road Level.
CLIENT : AXIATA (Bangladesh) Ltd.	DATE OF BORING : 02-07-2010.	G. W. T : 0.91m below from E. G. L.

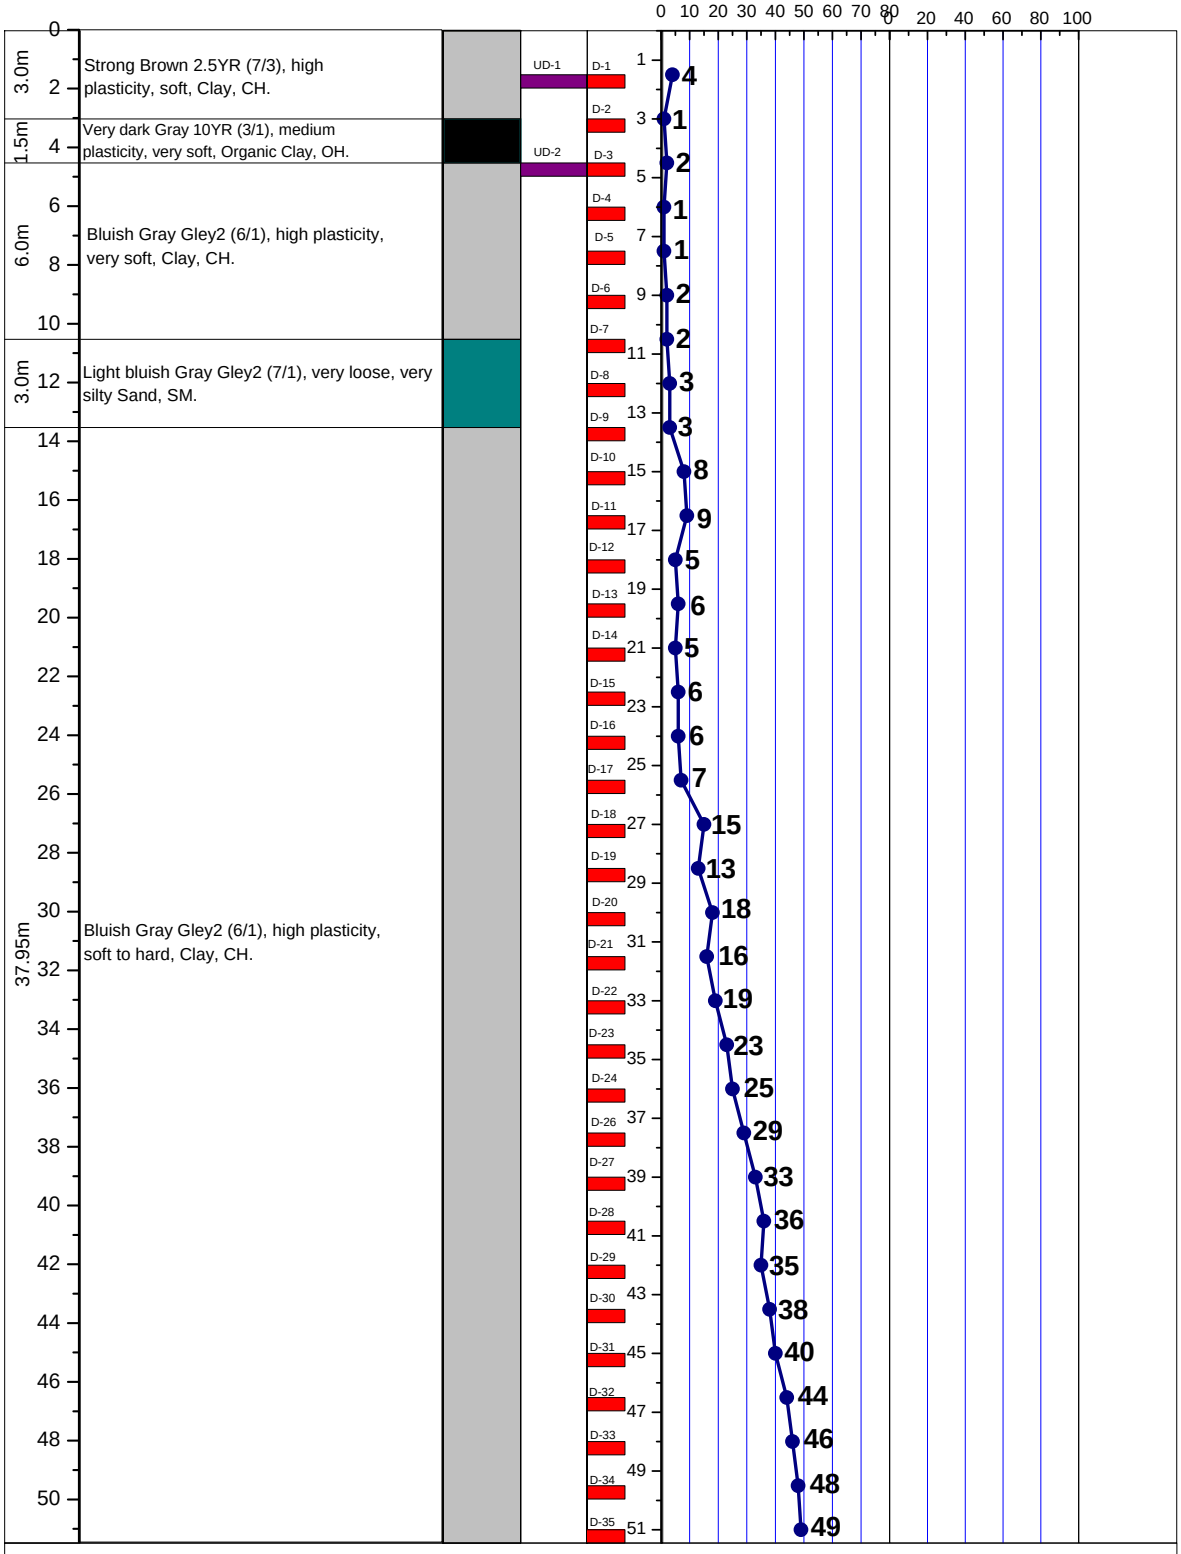


LEGEND FOR BORELOG AND GRAIN SIZE DISTRIBUTION (BASED ON 'ASTM CLASSIFICATION D-2487')

PLASTIC CLAY	SILT	PEAT/HIGHLY ORGANIC SOIL	UNDISTURBED SAMPLE
MICACEOUS FINE SAND/SILT	SAND	SHALE	DISTURBED SAMPLE

N- BLOWS DELIVERED PER FOOT BY A 140 LB HAMMER FALLING 30 INCHES

MAX^{m} PENETRATION= 50 BLOWS. AFTER 50 BLOWS PENETRATION DEPTH WERE MEASURED

A2 PROSOIL	BOREHOLE NO: BH-1	
	LOCATION : Shukchari, Lohagara, Chittagong.	
PROJECT : Telecommunication Tower.	DEPTH OF BORING : 51.0m	R. L.: 1.22m below from Road Level.
CLIENT : AXIATA (Bangladesh) Ltd.	DATE OF BORING : 01-08-2010.	G. W. T : On E. G. L.

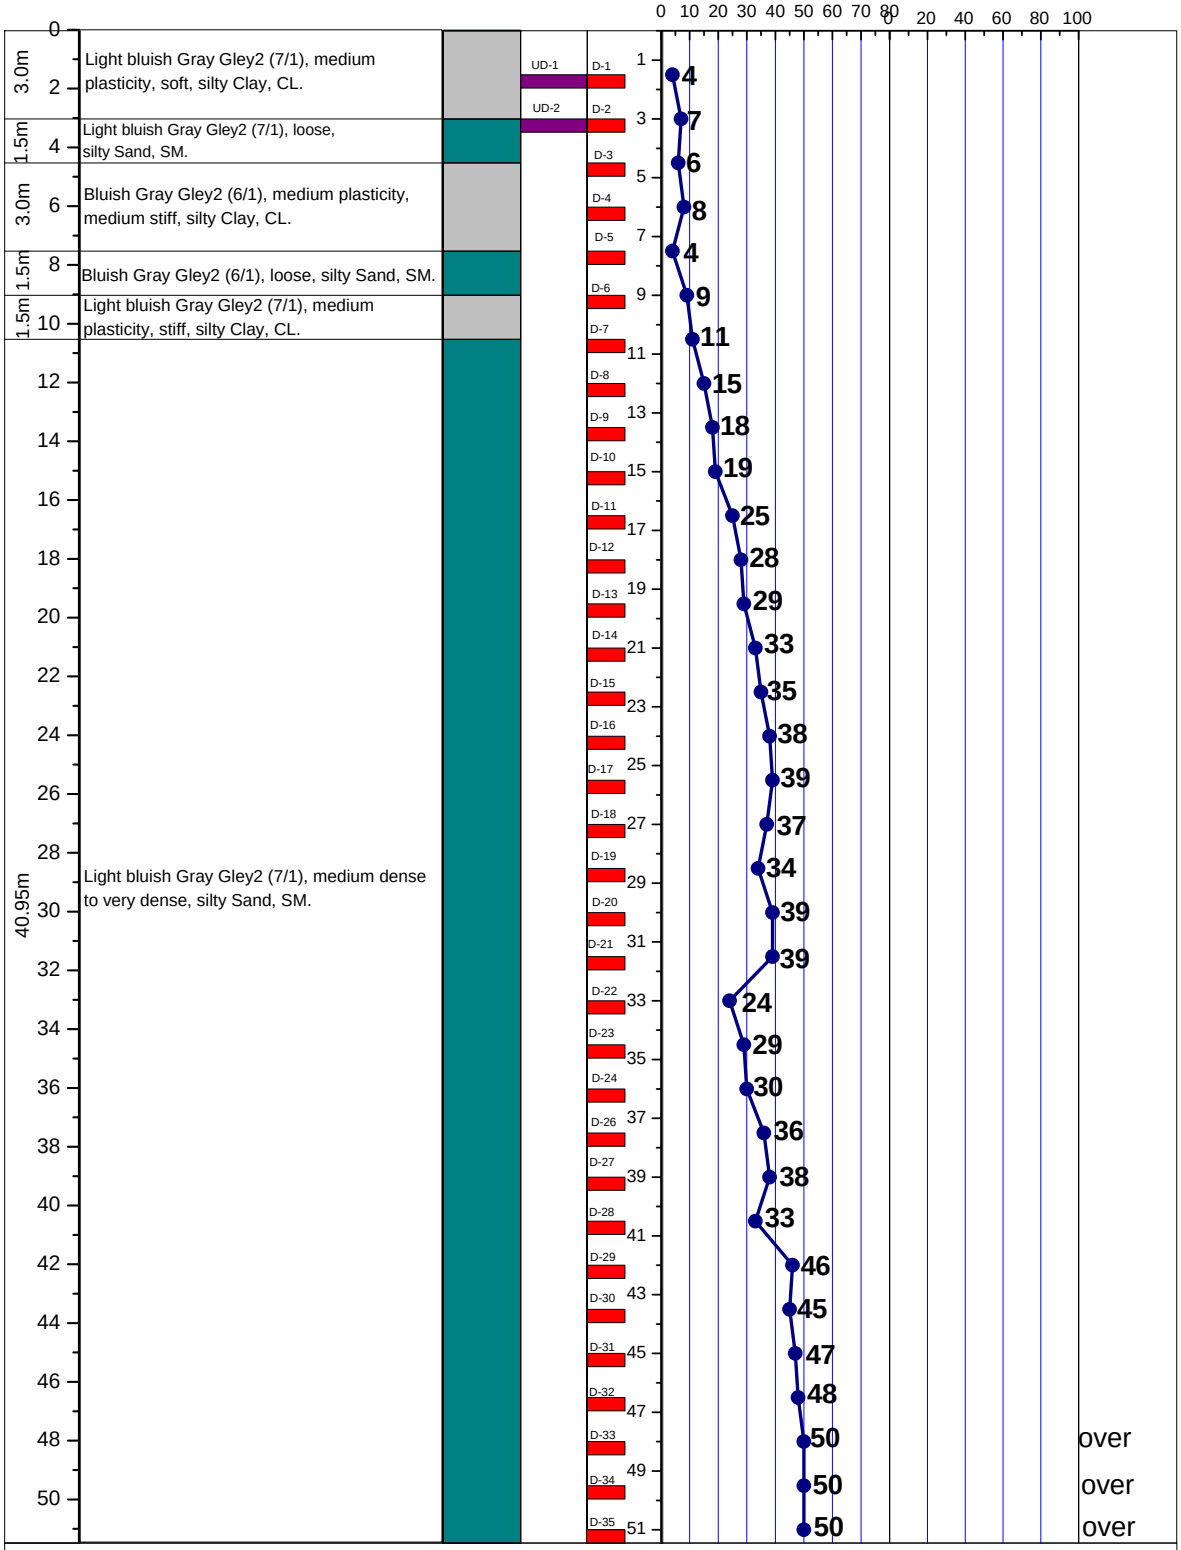


LEGEND FOR BORELOG AND GRAIN SIZE DISTRIBUTION (BASED ON 'ASTM CLASSIFICATION D-2487')

PLASTIC CLAY	SILT	PEAT/HIGHLY ORGANIC SOIL	UNDISTURBED SAMPLE
MICACEOUS FINE SAND/SILT	SAND	SHALE	DISTURBED SAMPLE

N- BLOWS DELIVERED PER FOOT BY A 140 LB HAMMER FALLING 30 INCHES

MAX^{m} PENETRATION= 50 BLOWS. AFTER 50 BLOWS PENETRATION DEPTH WERE MEASURED

A2 PROSOIL	BOREHOLE NO: BH-1	
	LOCATION : Tishorighut, Anowara, Chittagong.	
PROJECT : Telecommunication Tower.	DEPTH OF BORING : 51.0m	R. L.: 0.91m below from Road Level.
CLIENT : AXIATA (Bangladesh) Ltd.	DATE OF BORING : 30-06-2010.	G. W. T : 0.61m above from E. G. L.(Rain Water)

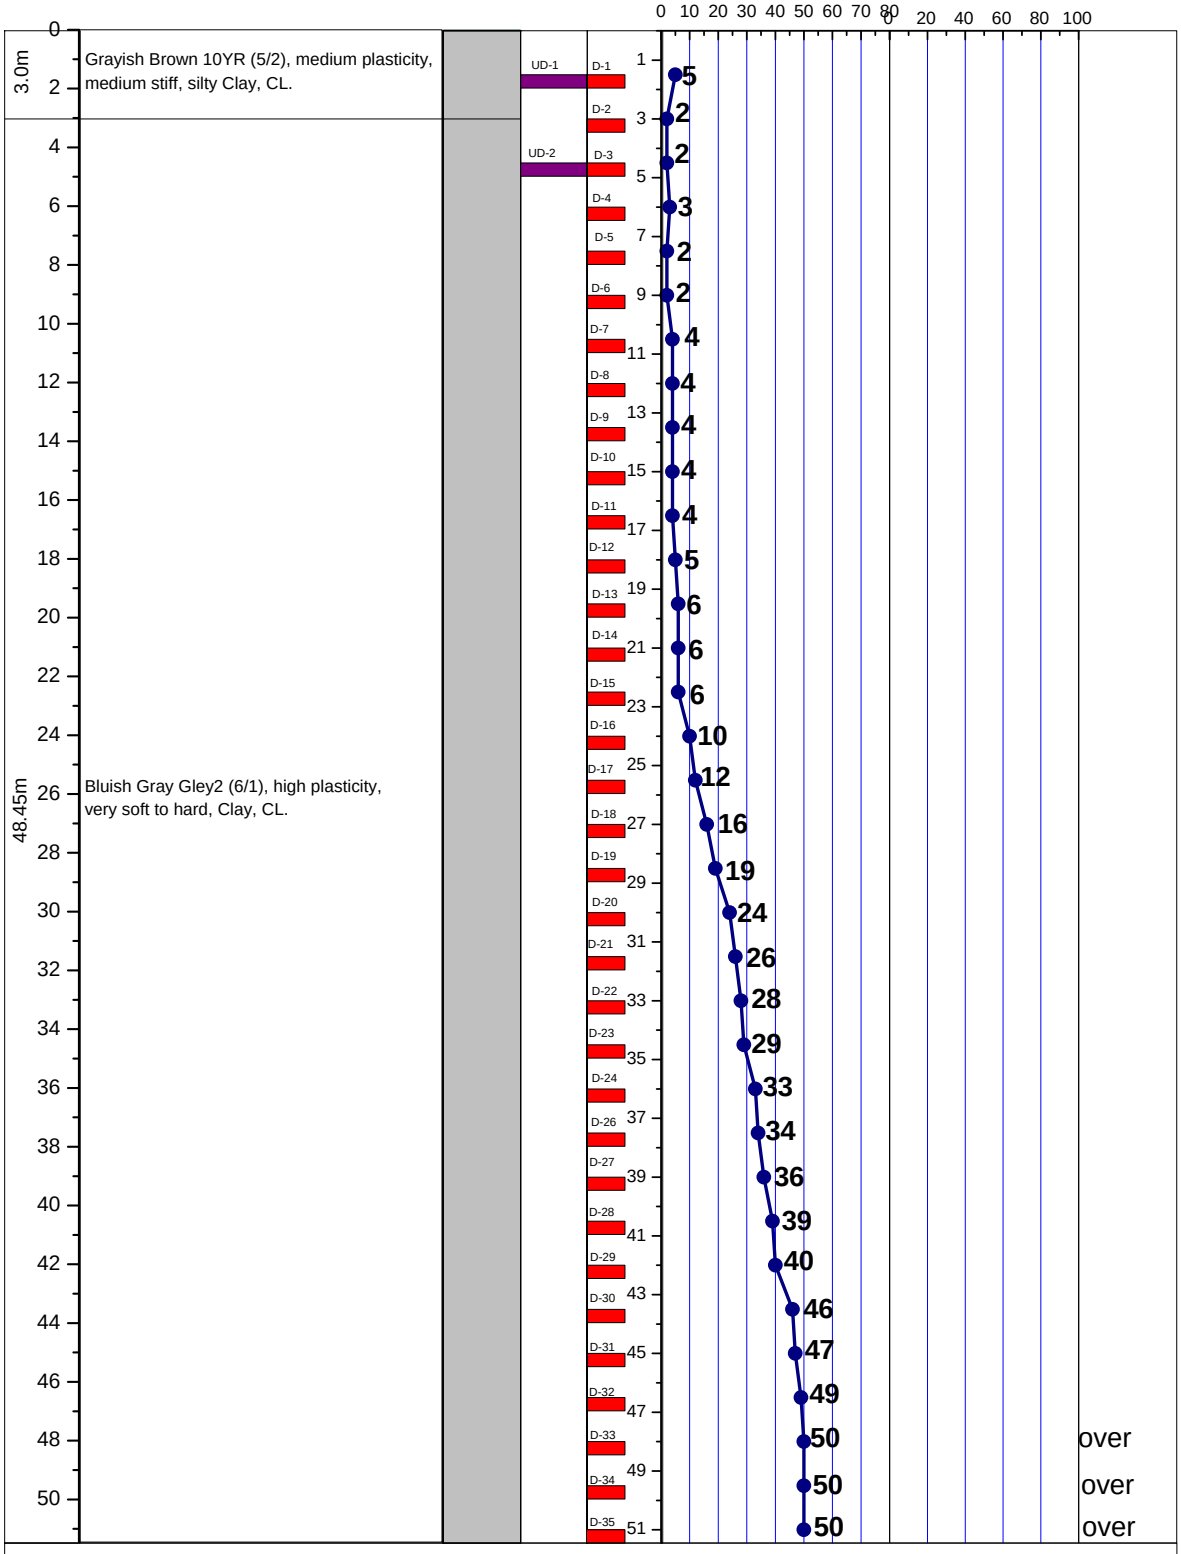


LEGEND FOR BORELOG AND GRAIN SIZE DISTRIBUTION (BASED ON 'ASTM CLASSIFICATION D-2487')

PLASTIC CLAY	SILT	PEAT/HIGHLY ORGANIC SOIL	UNDISTURBED SAMPLE
MICACEOUS FINE SAND/SILT	SAND	SHALE	DISTURBED SAMPLE

N- BLOWS DELIVERED PER FOOT BY A 140 LB HAMMER FALLING 30 INCHES

MAX^{m} PENETRATION= 50 BLOWS. AFTER 50 BLOWS PENETRATION DEPTH WERE MEASURED

A2 PROSOIL	BOREHOLE NO: BH-1	
	LOCATION : Boroghona, Purbo Boroghona, Bashkhali, Chittagong.	
PROJECT : Telecommunication Tower.	DEPTH OF BORING : 51.0m	R. L.: 0.91m below from Road Level.
CLIENT : AXIATA (Bangladesh) Ltd.	DATE OF BORING : 29-04-2012.	G. W. T : 1.52m below from E. G. L.

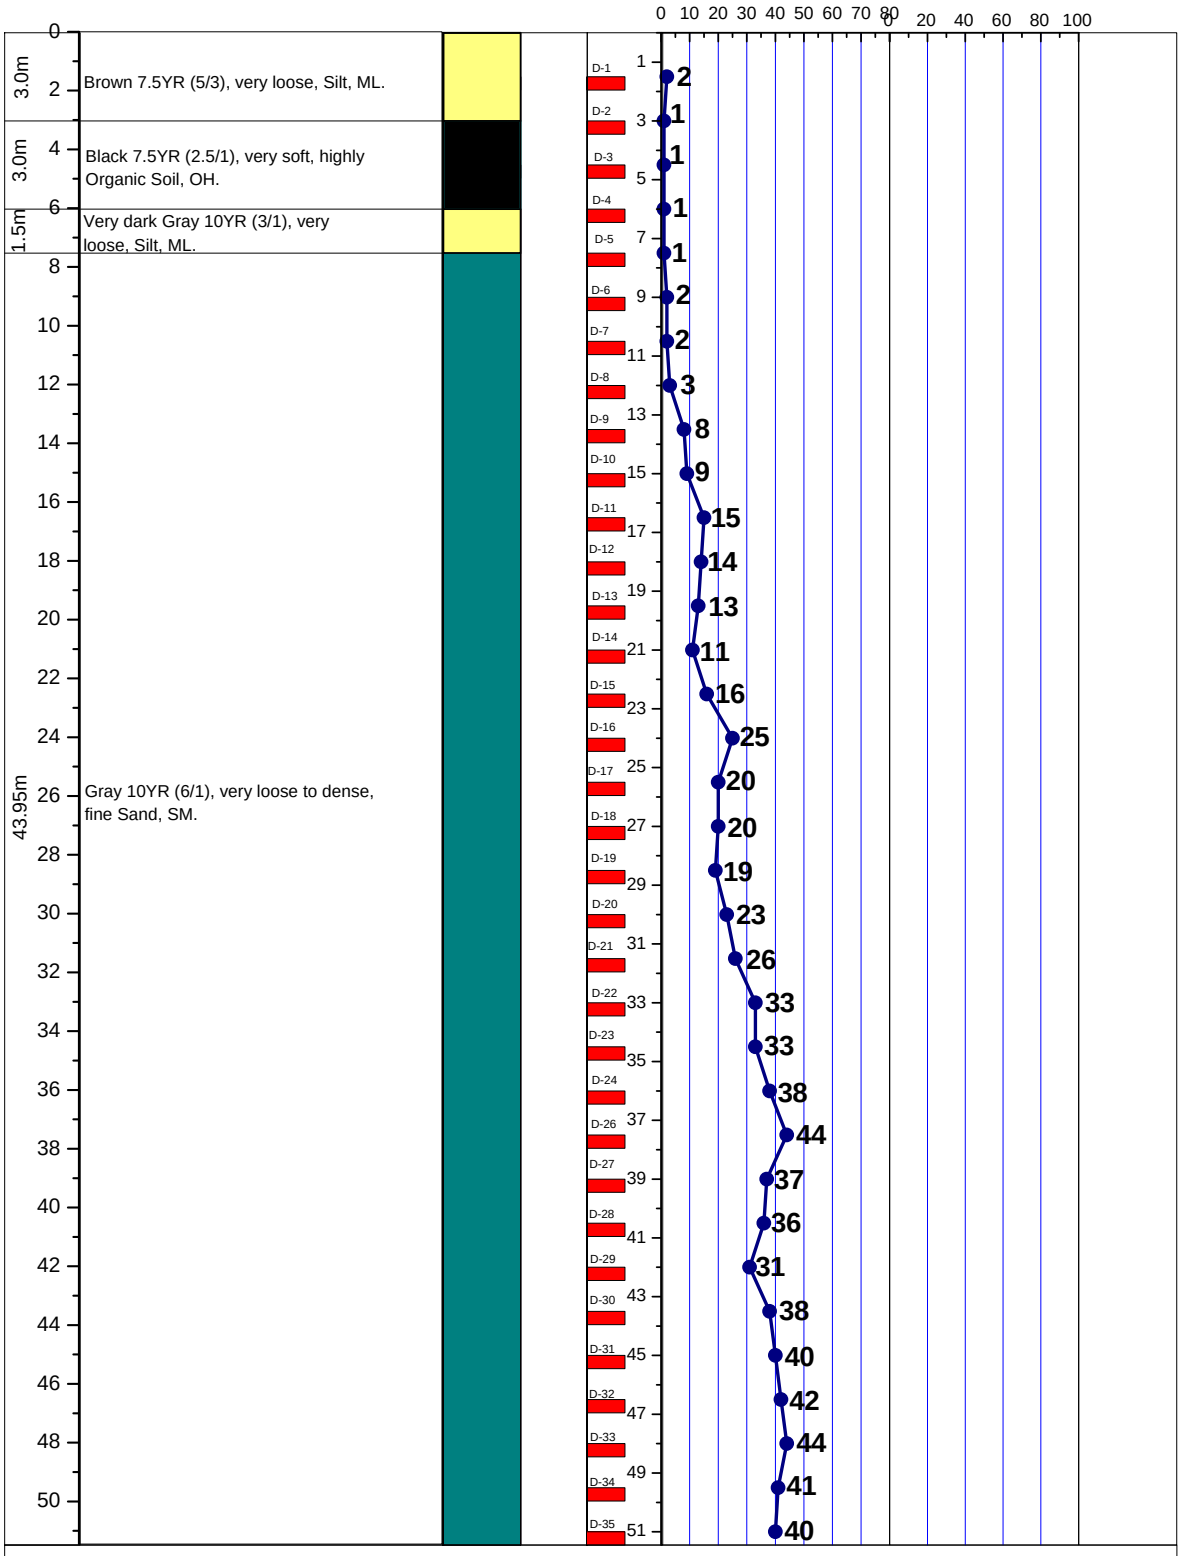


LEGEND FOR BORELOG AND GRAIN SIZE DISTRIBUTION (BASED ON 'ASTM CLASSIFICATION D-2487')

PLASTIC CLAY	SILT	PEAT/HIGHLY ORGANIC SOIL	UNDISTURBED SAMPLE
MICACEOUS FINE SAND/SILT	SAND	SHALE	DISTURBED SAMPLE

N- BLOWS DELIVERED PER FOOT BY A 140 LB HAMMER FALLING 30 INCHES

MAX^{m} PENETRATION= 50 BLOWS. AFTER 50 BLOWS PENETRATION DEPTH WERE MEASURED

A2 PROSOIL	BOREHOLE NO: BH-1	
	LOCATION : Gohira, Dovashir Hat, Anwara , Chittagong.	
PROJECT : Telecommunication Tower.	DEPTH OF BORING : 51.0m	R. L.: 0.3m below from Road Level.
CLIENT : AXIATA (Bangladesh) Ltd.	DATE OF BORING : 07-07-2013.	G. W. T : 1.21m below from E. G. L.

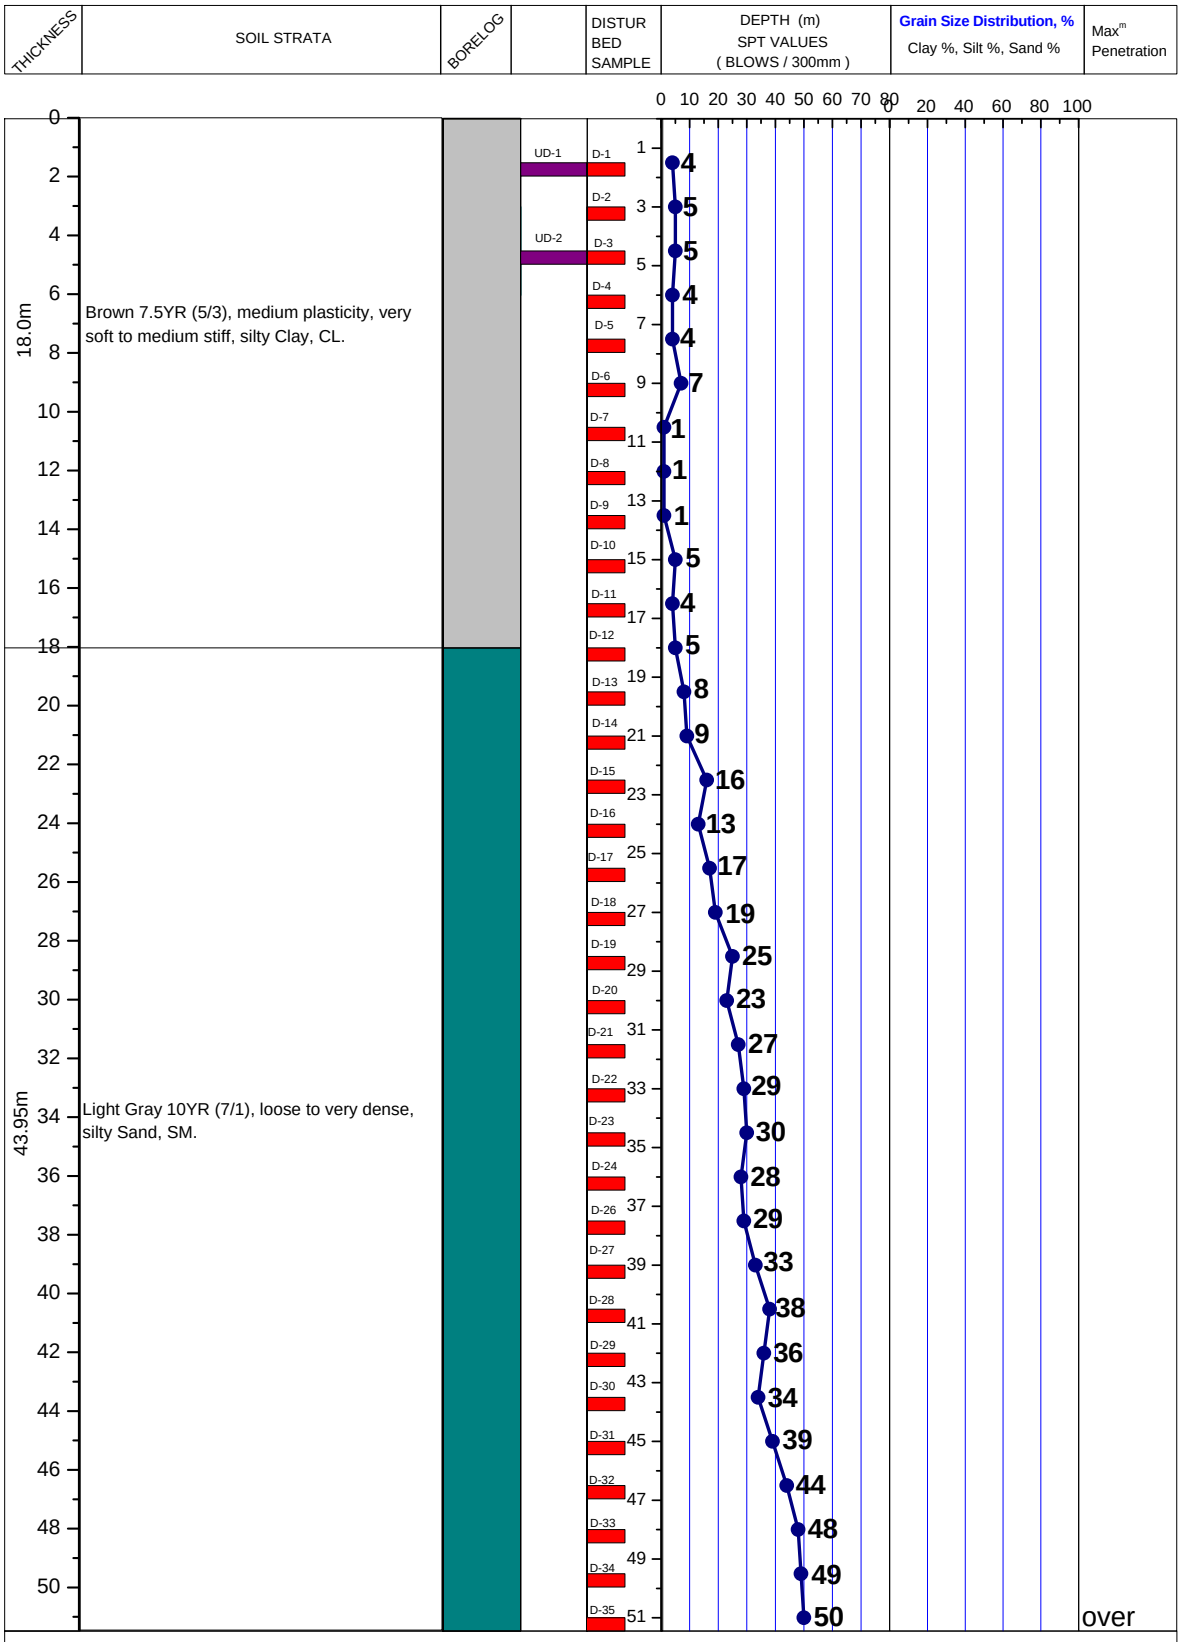


LEGEND FOR BORELOG AND GRAIN SIZE DISTRIBUTION (BASED ON 'ASTM CLASSIFICATION D-2487')

PLASTIC CLAY	SILT	PEAT/HIGHLY ORGANIC SOIL	UNDISTURBED SAMPLE
MICACEOUS FINE SAND/SILT	SAND	SHALE	DISTURBED SAMPLE

N- BLOWS DELIVERED PER FOOT BY A 140 LB HAMMER FALLING 30 INCHES

MAX^{m} PENETRATION= 50 BLOWS. AFTER 50 BLOWS PENETRATION DEPTH WERE MEASURED

A2	PROSOIL	BOREHOLE NO: BH-1	
		LOCATION : Vill: North Bondar, P.O: Muhal Khan Bazar, P.S: Anowara, District: Chittagong.	
PROJECT : Telecommunication Tower.		DEPTH OF BORING : 51.0m	R. L.: 0.31m below from Road Level.
CLIENT : AXIATA (Bangladesh) Ltd.		DATE OF BORING : 06-04-2014.	G. W. T : 2.13m below from E. G. L.

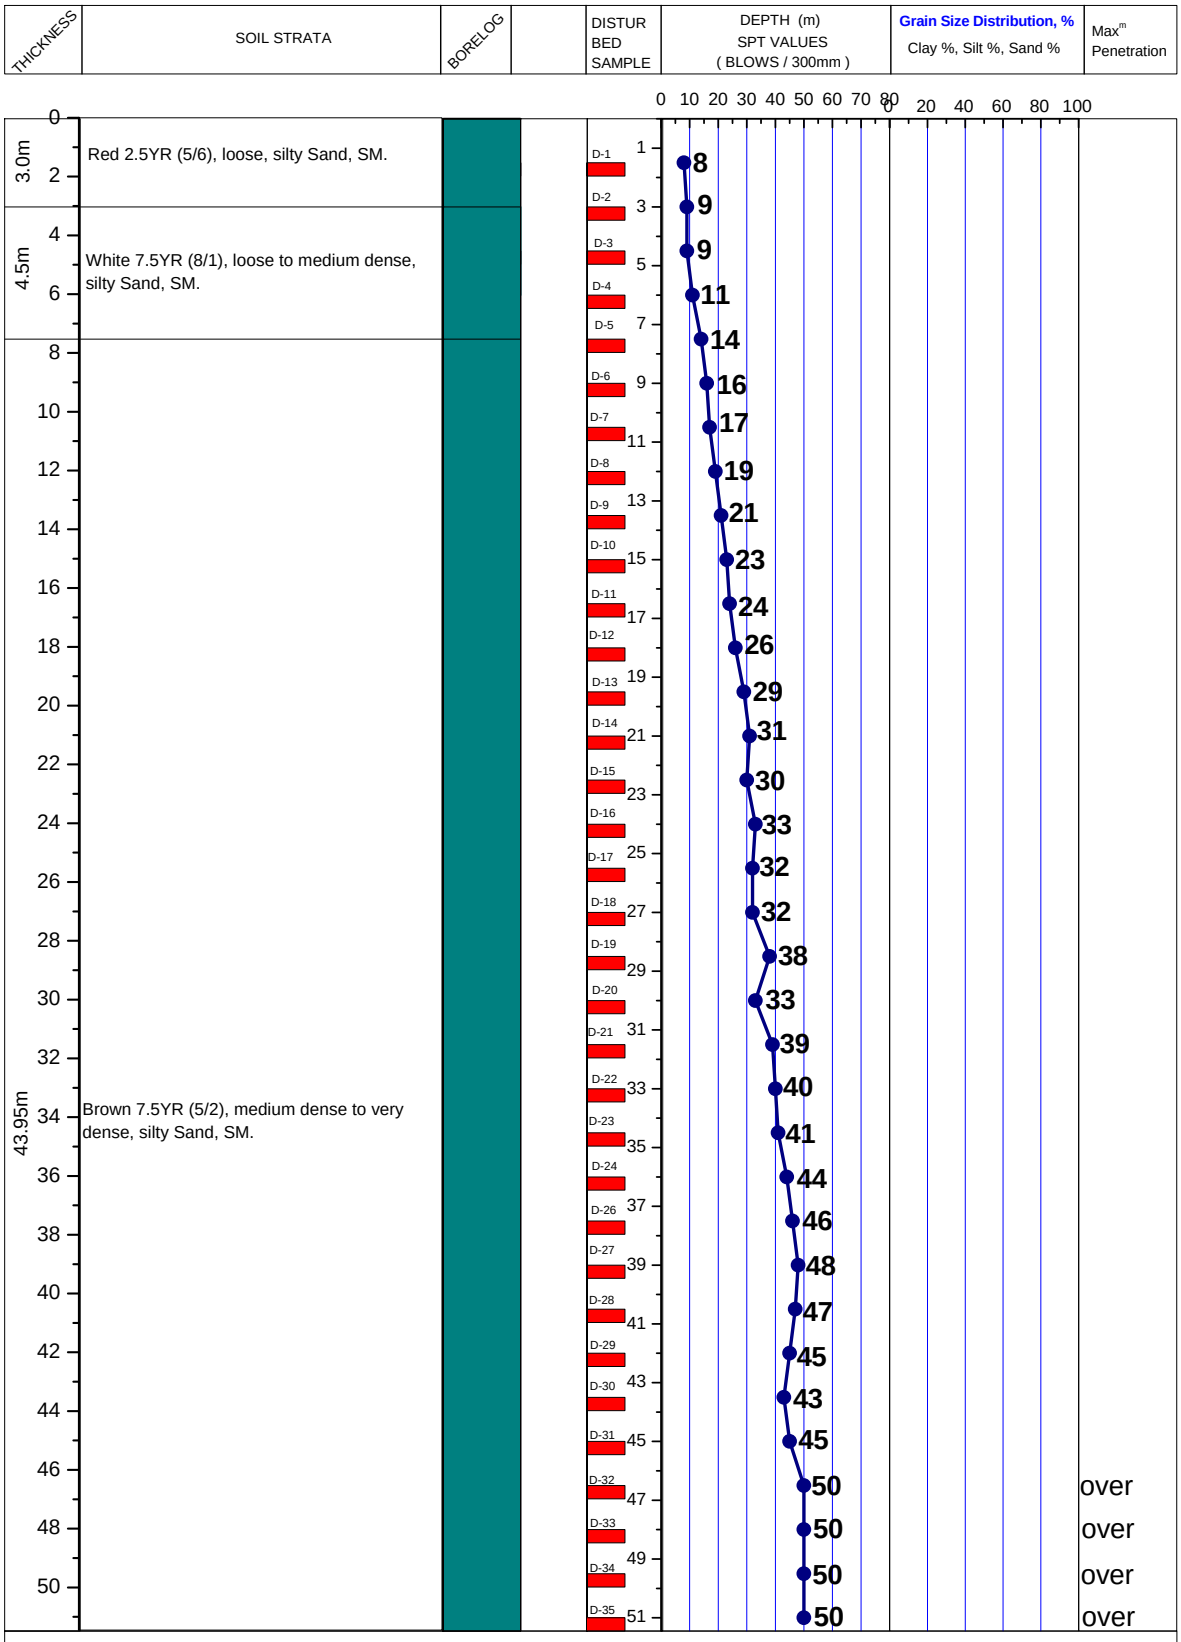


LEGEND FOR BORELOG AND GRAIN SIZE DISTRIBUTION (BASED ON 'ASTM CLASSIFICATION D-2487')

PLASTIC CLAY	SILT	PEAT/HIGHLY ORGANIC SOIL	UNDISTURBED SAMPLE
MICACEOUS FINE SAND/SILT	SAND	SHALE	DISTURBED SAMPLE

N- BLOWS DELIVERED PER FOOT BY A 140 LB HAMMER FALLING 30 INCHES

MAX^{m} PENETRATION= 50 BLOWS. AFTER 50 BLOWS PENETRATION DEPTH WERE MEASURED

A2	PROSOIL	BOREHOLE NO: BH-1	
		LOCATION : Vill: East Buiragi, P.S.: Anwara, District: Chittagong.	
PROJECT : Telecommunication Tower.		DEPTH OF BORING : 51.0m	R. L.: On Road Level.
CLIENT : AXIATA (Bangladesh) Ltd.		DATE OF BORING : 29-03-2014.	G. W. T : 1.83m below from E. G. L.

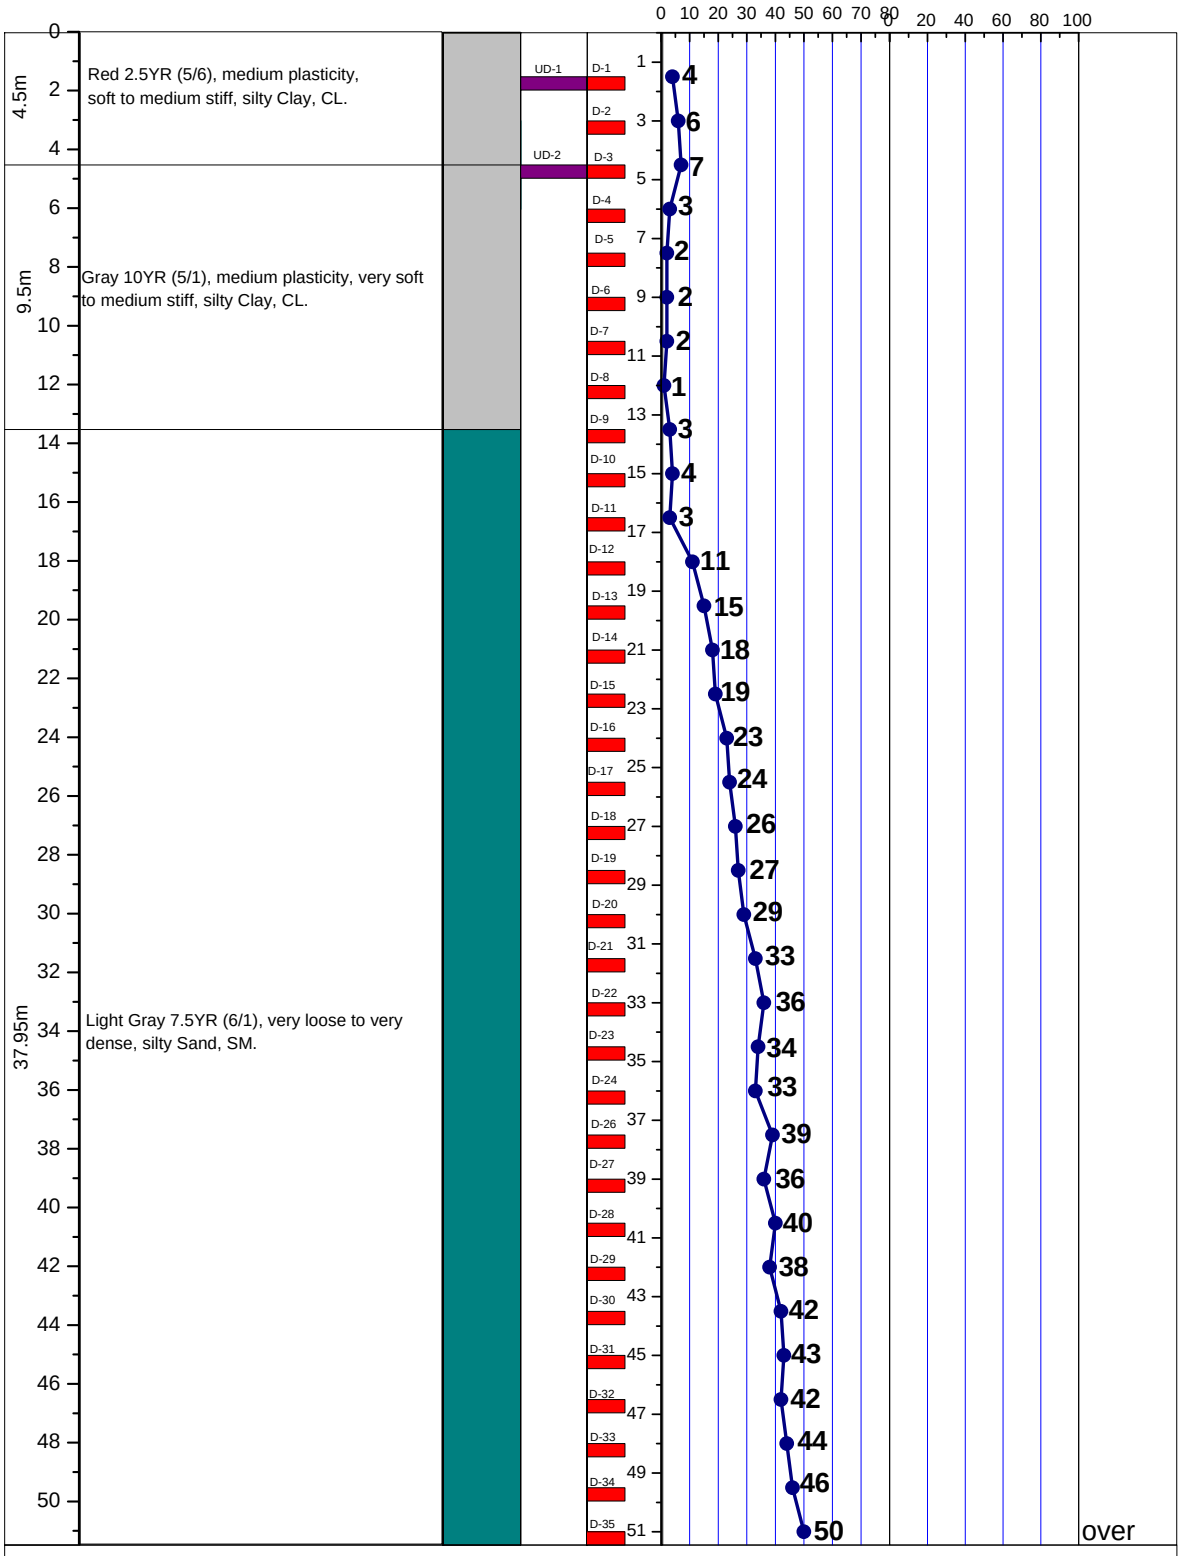


LEGEND FOR BORELOG AND GRAIN SIZE DISTRIBUTION (BASED ON 'ASTM CLASSIFICATION D-2487')

PLASTIC CLAY	SILT	PEAT/HIGHLY ORGANIC SOIL	UNDISTURBED SAMPLE
MICACEOUS FINE SAND/SILT	SAND	SHALE	DISTURBED SAMPLE

N- BLOWS DELIVERED PER FOOT BY A 140 LB HAMMER FALLING 30 INCHES

MAX^{m} PENETRATION= 50 BLOWS. AFTER 50 BLOWS PENETRATION DEPTH WERE MEASURED

A2	PROSOIL	BOREHOLE NO: BH-1	
		LOCATION : Vill: Vill: Chandondi, P. O: Iqbal Park, P.S : Boalkhali, Dist: Chittagong.	
PROJECT : Telecommunication Tower.		DEPTH OF BORING : 51.0m	R. L.: 0.30m below from Road Level.
CLIENT : AXIATA (Bangladesh) Ltd.		DATE OF BORING : 20-04-2014.	G. W. T : 1.52m below from E. G. L.

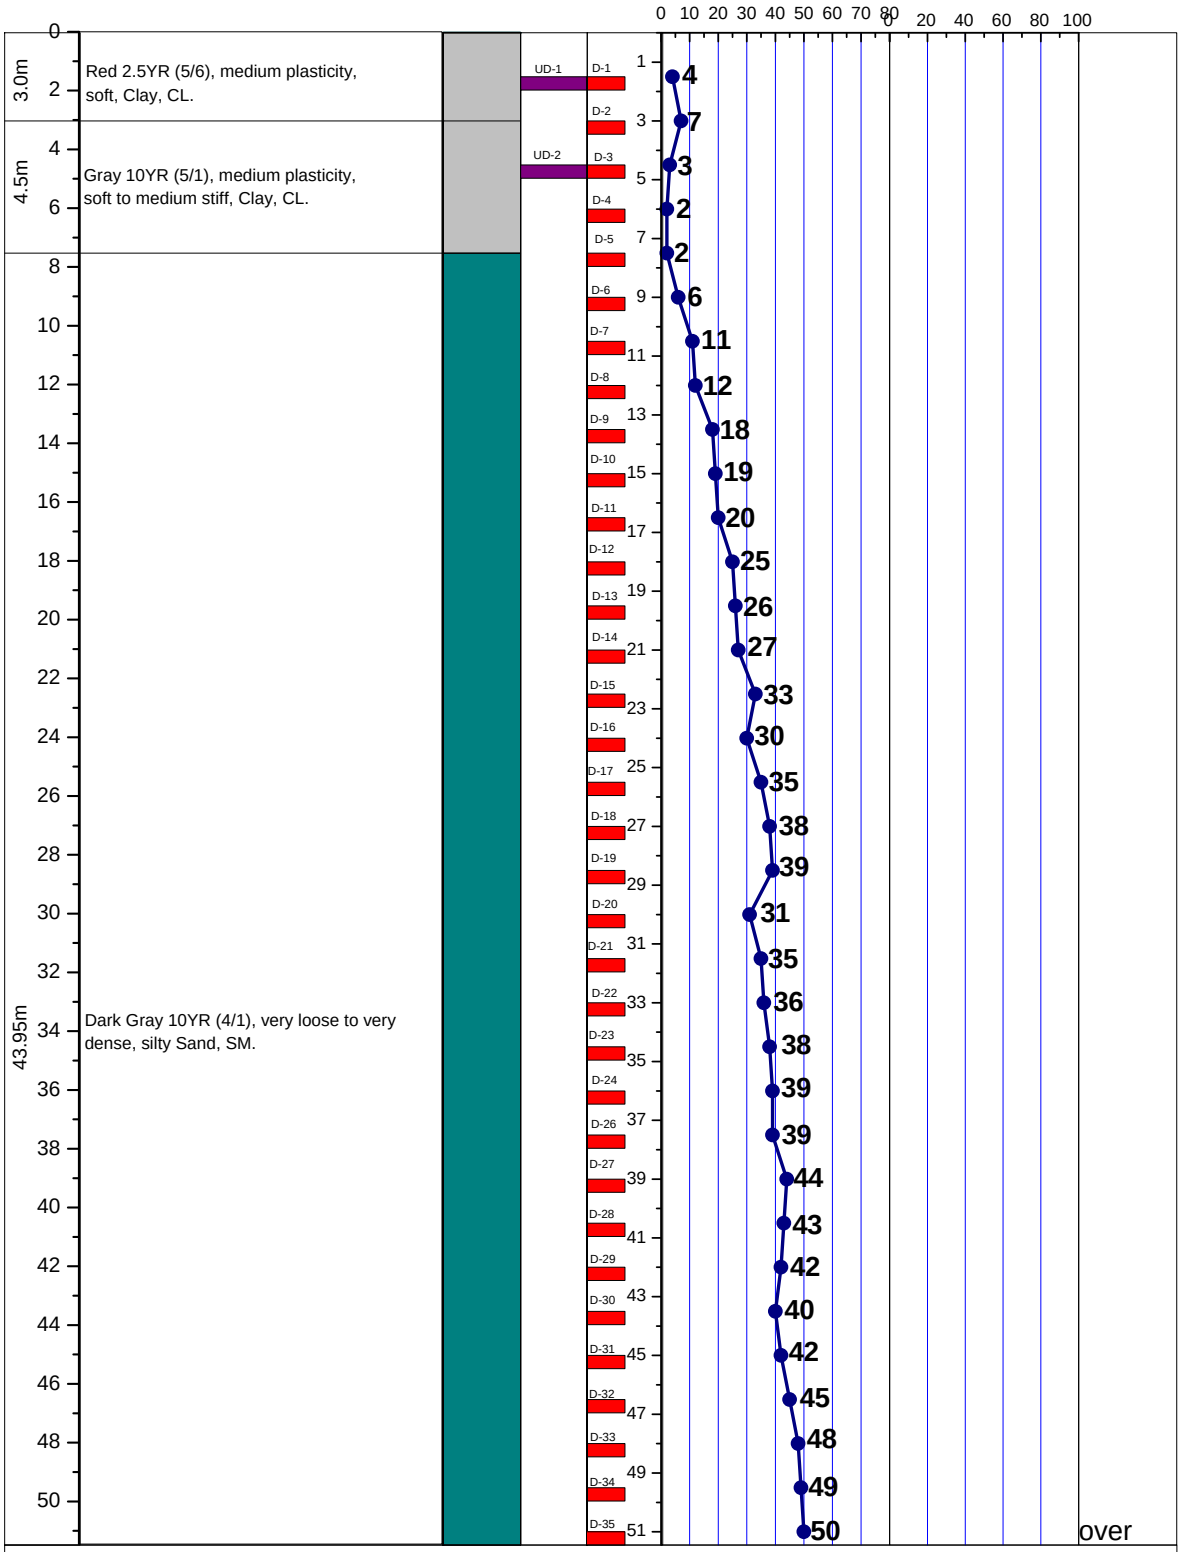


LEGEND FOR BORELOG AND GRAIN SIZE DISTRIBUTION (BASED ON 'ASTM CLASSIFICATION D-2487')

PLASTIC CLAY	SILT	PEAT/HIGHLY ORGANIC SOIL	UNDISTURBED SAMPLE
MICACEOUS FINE SAND/SILT	SAND	SHALE	DISTURBED SAMPLE

N- BLOWS DELIVERED PER FOOT BY A 140 LB HAMMER FALLING 30 INCHES

MAX^{m} PENETRATION= 50 BLOWS. AFTER 50 BLOWS PENETRATION DEPTH WERE MEASURED

A2	PROSOIL	BOREHOLE NO: BH-1	
		LOCATION : Vill: Vill: Akubdondi, P.O: Hawla Sharif, P.S: Boal Khali, Dist: Chittagong.	
PROJECT : Telecommunication Tower.		DEPTH OF BORING : 51.0m	R. L.: 0.31m below from Road Level.
CLIENT : AXIATA (Bangladesh) Ltd.		DATE OF BORING : 28-11-2014.	G. W. T : 0.91m below from E. G. L.

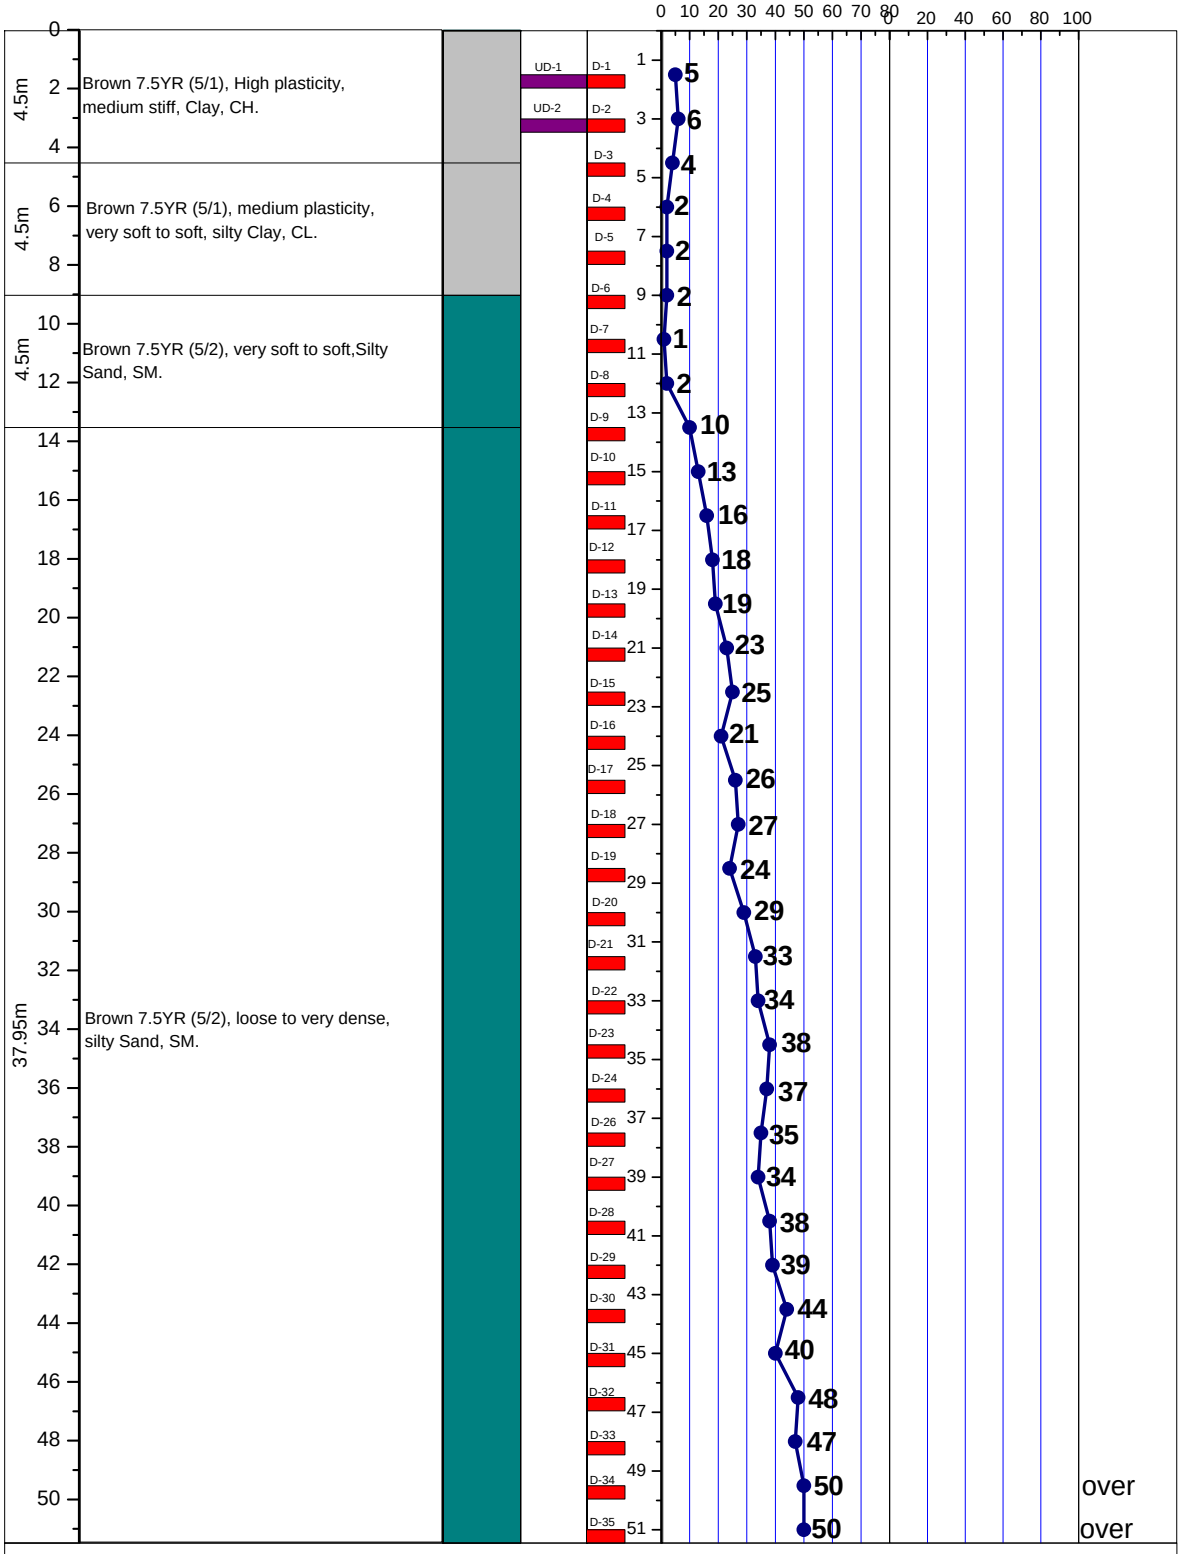


LEGEND FOR BORELOG AND GRAIN SIZE DISTRIBUTION (BASED ON 'ASTM CLASSIFICATION D-2487')

PLASTIC CLAY	SILT	PEAT/HIGHLY ORGANIC SOIL	UNDISTURBED SAMPLE
MICACEOUS FINE SAND/SILT	SAND	SHALE	DISTURBED SAMPLE

N- BLOWS DELIVERED PER FOOT BY A 140 LB HAMMER FALLING 30 INCHES

MAX^{m} PENETRATION= 50 BLOWS. AFTER 50 BLOWS PENETRATION DEPTH WERE MEASURED

A2	PROSOIL	BOREHOLE NO: BH-1	
		LOCATION : Vill: Roushanhat, Chandanaish, West Elahabad, Chittagong, R.S 86, Dag-R.S 386.	
PROJECT : Telecommunication Tower.		DEPTH OF BORING : 51.0m	R. L.: 0.90m below from Road Level.
CLIENT : AXIATA (Bangladesh) Ltd.		DATE OF BORING : 07-02-2013.	G. W. T : 0.60m below from E. G. L.

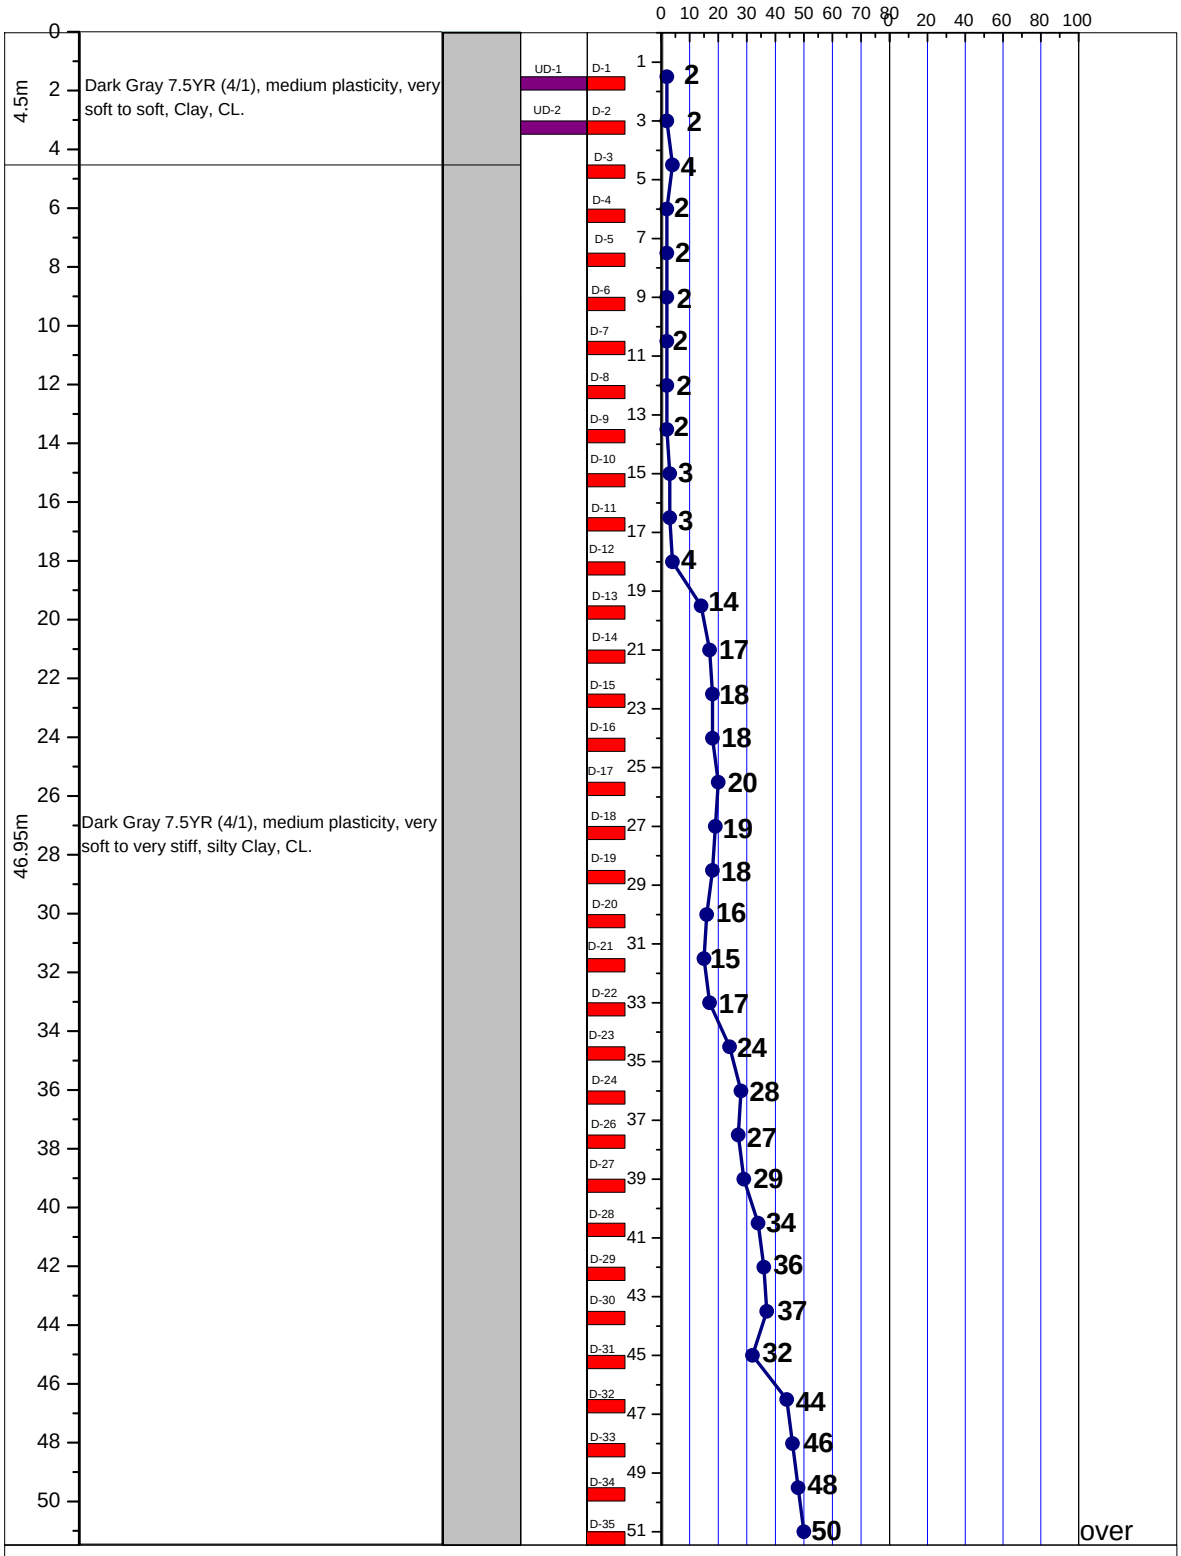


LEGEND FOR BORELOG AND GRAIN SIZE DISTRIBUTION (BASED ON 'ASTM CLASSIFICATION D-2487')

PLASTIC CLAY	SILT	PEAT/HIGHLY ORGANIC SOIL	UNDISTURBED SAMPLE
MICACEOUS FINE SAND/SILT	SAND	SHALE	DISTURBED SAMPLE

N- BLOWS DELIVERED PER FOOT BY A 140 LB HAMMER FALLING 30 INCHES

MAX^{m} PENETRATION= 50 BLOWS. AFTER 50 BLOWS PENETRATION DEPTH WERE MEASURED

A2	PROSOIL	BOREHOLE NO: BH-1	
		LOCATION : Vill: Kanai Madari, Pathandandi, Chandanaish, Chittagong.	
PROJECT : Telecommunication Tower.		DEPTH OF BORING : 51.0m	R. L.: 0.31m below from Road Level.
CLIENT : AXIATA (Bangladesh) Ltd.		DATE OF BORING : 27-05-2013.	G. W. T : 1.52m below from E. G. L.

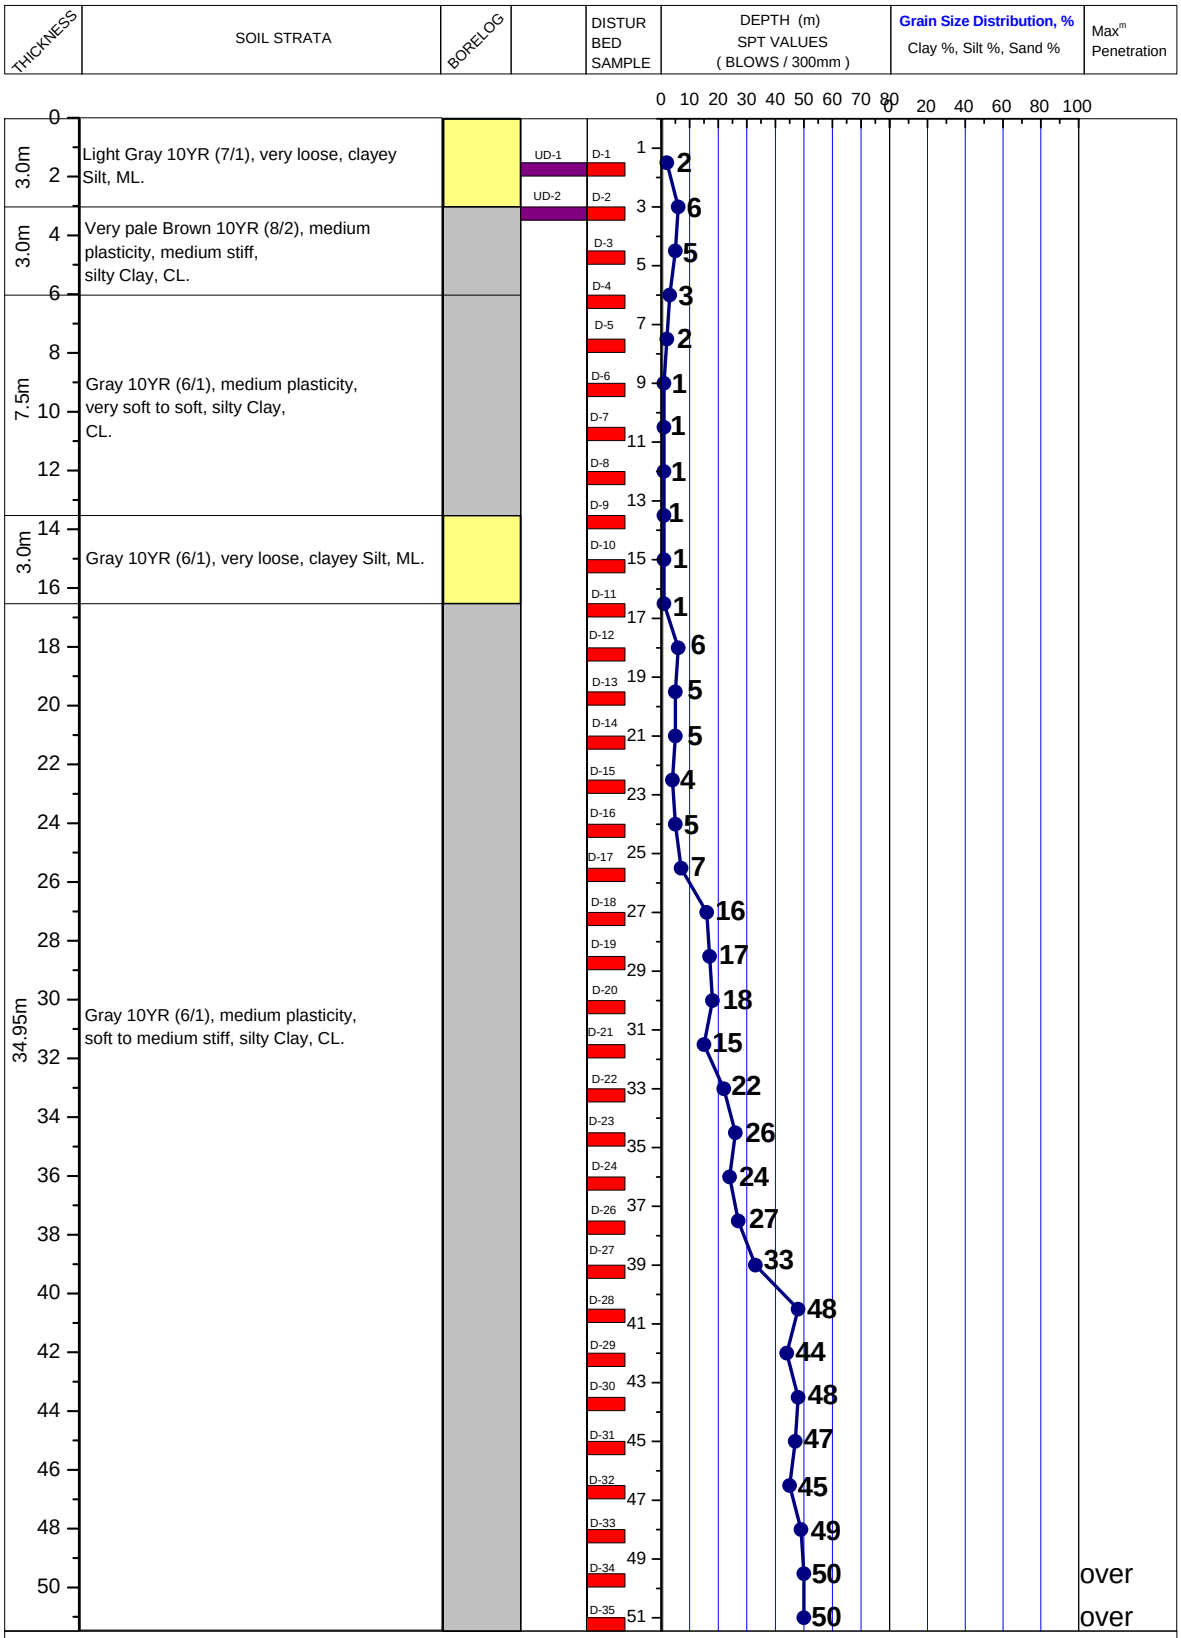

LEGEND FOR BORELOG AND GRAIN SIZE DISTRIBUTION (BASED ON 'ASTM CLASSIFICATION D-2487')

PLASTIC CLAY	SILT	PEAT/HIGHLY ORGANIC SOIL	UNDISTURBED SAMPLE
MICACEOUS FINE SAND/SILT	SAND	SHALE	DISTURBED SAMPLE

N- BLOWS DELIVERED PER FOOT BY A 140 LB HAMMER FALLING 30 INCHES

MAX^{m} PENETRATION= 50 BLOWS. AFTER 50 BLOWS PENETRATION DEPTH WERE MEASURED