A2	PROSOIL	BOREHOLE NO: BH-1	
		LOCATION : **Chainage 14+583.7 km on Darbos (Sylhet-Jaflong High Way) -Kanaighat Road, Sylhet.**	
PROJECT : Proposed Darbos-Kanaighat Bridge from Chainage 14+583.7 to 14+635.4 km.)		DEPTH OF BORING : 30.0m	**Chainage: 14+586.7** **R. L. : 8.61**
CLIENT : Road Division, Sylhet.		DATE OF BORING : 21-02-2010.	G. W. T : 0.91m below from E.G.L.

THICKNESS	SOIL STRATA	BORELOG	RL	DISTURBED SAMPLE	DEPTH (m) SPT VALUES (BLOWS / 300mm)	Grain Size Distribution, % Clay %, Silt %, Sand %	Max^{m} Penetration

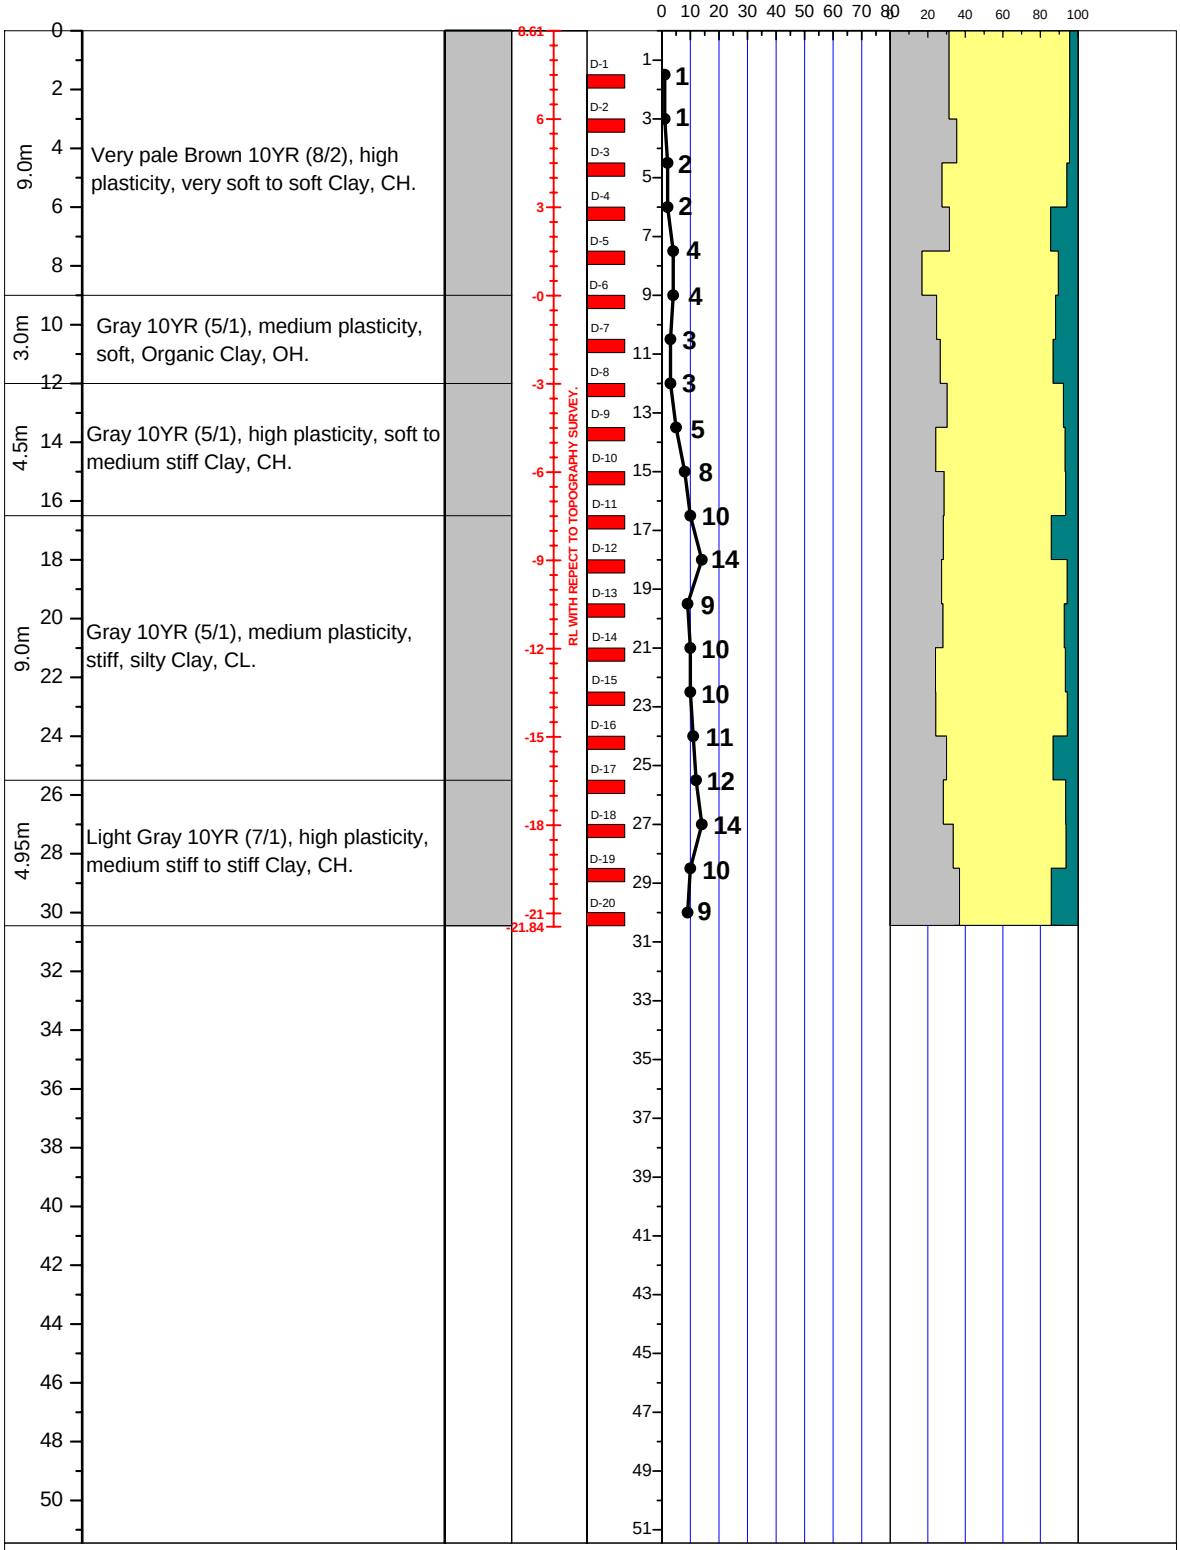

LEGEND FOR BORELOG AND GRAIN SIZE DISTRIBUTION (BASED ON 'ASTM CLASSIFICATION D-2487')

PLASTIC CLAY	SILT	PEAT/HIGHLY ORGANIC SOIL	UNDISTURBED SAMPLE
MICACEOUS FINE SAND/SILT	SAND	SHALE	DISTURBED SAMPLE

N- BLOWS DELIVERED PER FOOT BY A 140 LB HAMMER FALLING 30 INCHES

MAX^{m} PENETRATION= 50 BLOWS. AFTER 50 BLOWS PENETRATION DEPTH WERE MEASURED