A2	PROSOIL	BOREHOLE NO: BH-1	
		LOCATION : 74th km (LRP 673c:Ch.73+118) of Comilla(Mainamoti) -B.Baria(Sarail) Road (N102).	
PROJECT : Proposed Poirtala Bridge.		DEPTH OF BORING : 45.0m	Chainage: 73+121 R. L. : 3.15
CLIENT : Road Division, Brahmanbaria.		DATE OF BORING : 05-12-2010.	G. W. T : 0.91m below from E.G.L.

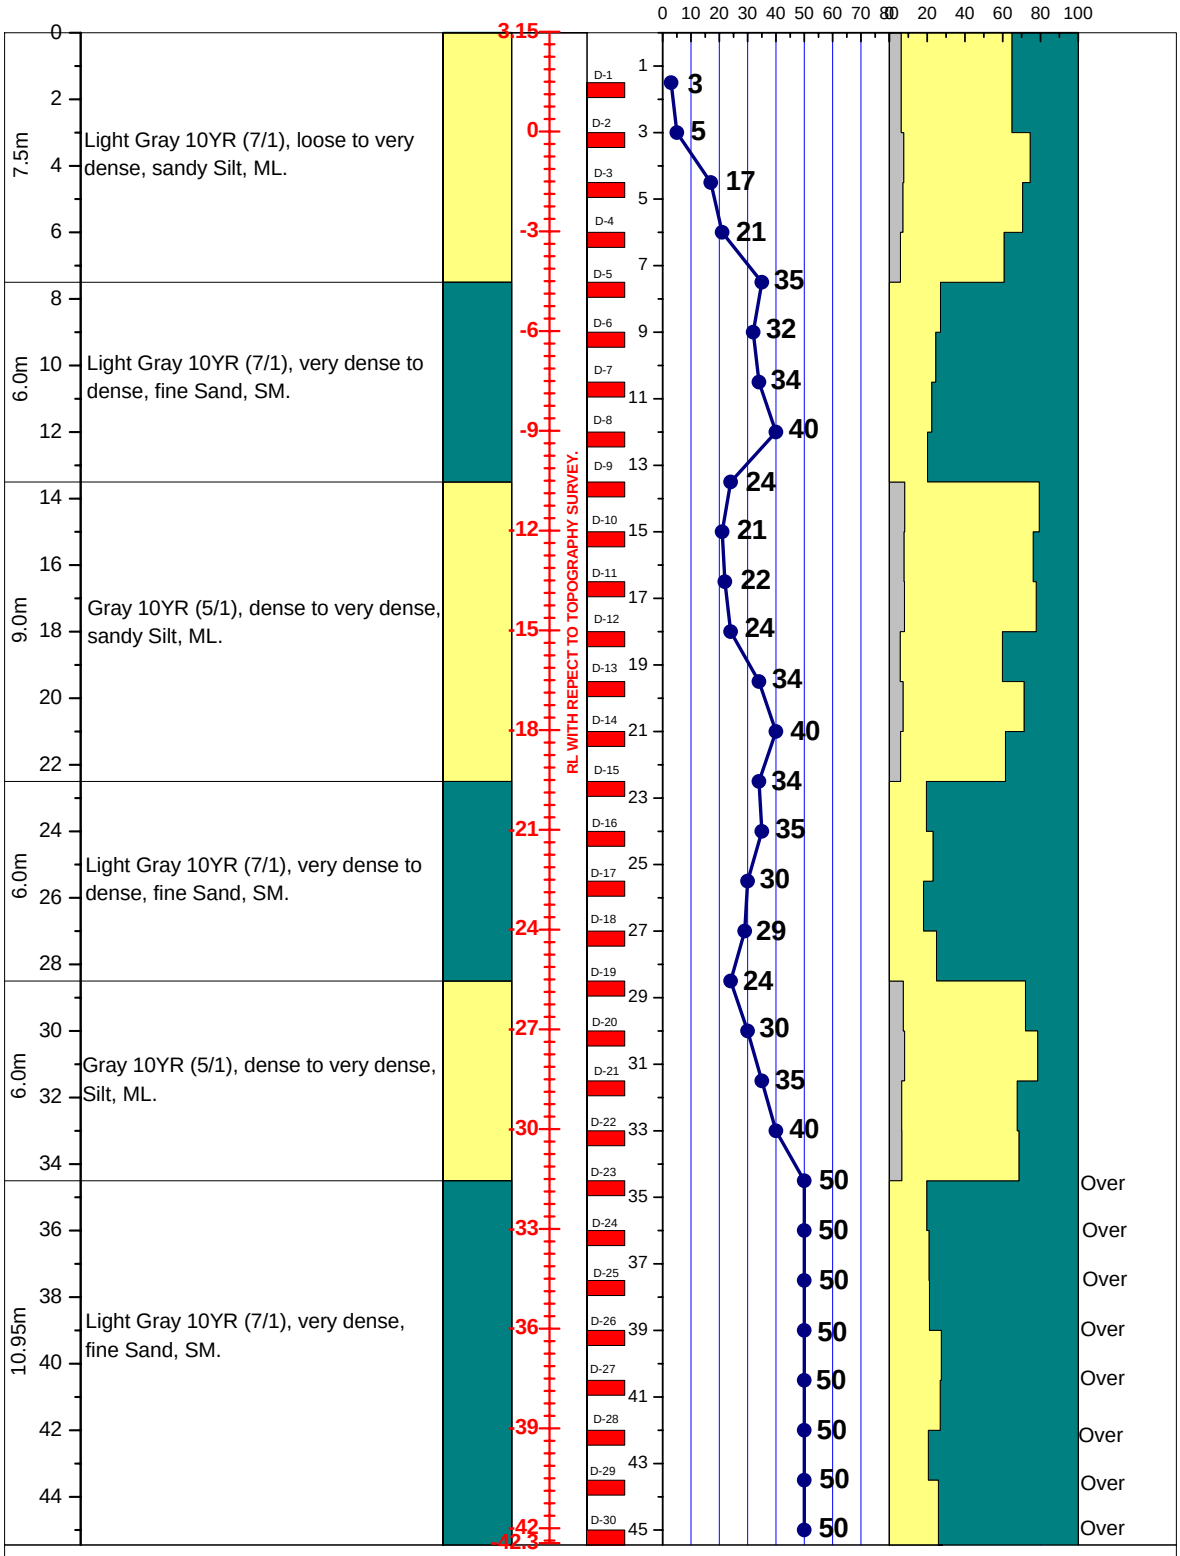

LEGEND FOR BORELOG AND GRAIN SIZE DISTRIBUTION (BASED ON 'ASTM CLASSIFICATION D-2487')

PLASTIC CLAY	SILT	PEAT/HIGHLY ORGANIC SOIL	UNDISTURBED SAMPLE
MICACEOUS FINE SAND/SILT	SAND	SHALE	DISTURBED SAMPLE

N- BLOWS DELIVERED PER FOOT BY A 140 LB HAMMER FALLING 30 INCHES

MAX^m PENETRATION= 50 BLOWS. AFTER 50 BLOWS PENETRATION DEPTH WERE MEASURED