A2	PROSOIL	BOREHOLE NO: BH-1	
		LOCATION : Chinage 7+621 At Gap No (8/1) of Bancharampur -Homna Road (Z1043), B.Baria.	
PROJECT : Proposed Bridge.		DEPTH OF BORING : 42.0m	Chainage: 7+646 R. L. : 7.48
CLIENT : Road Division, B.Baria.		DATE OF BORING : 10-02-2011.	G. W. T : 1.52m below from E.G.L.

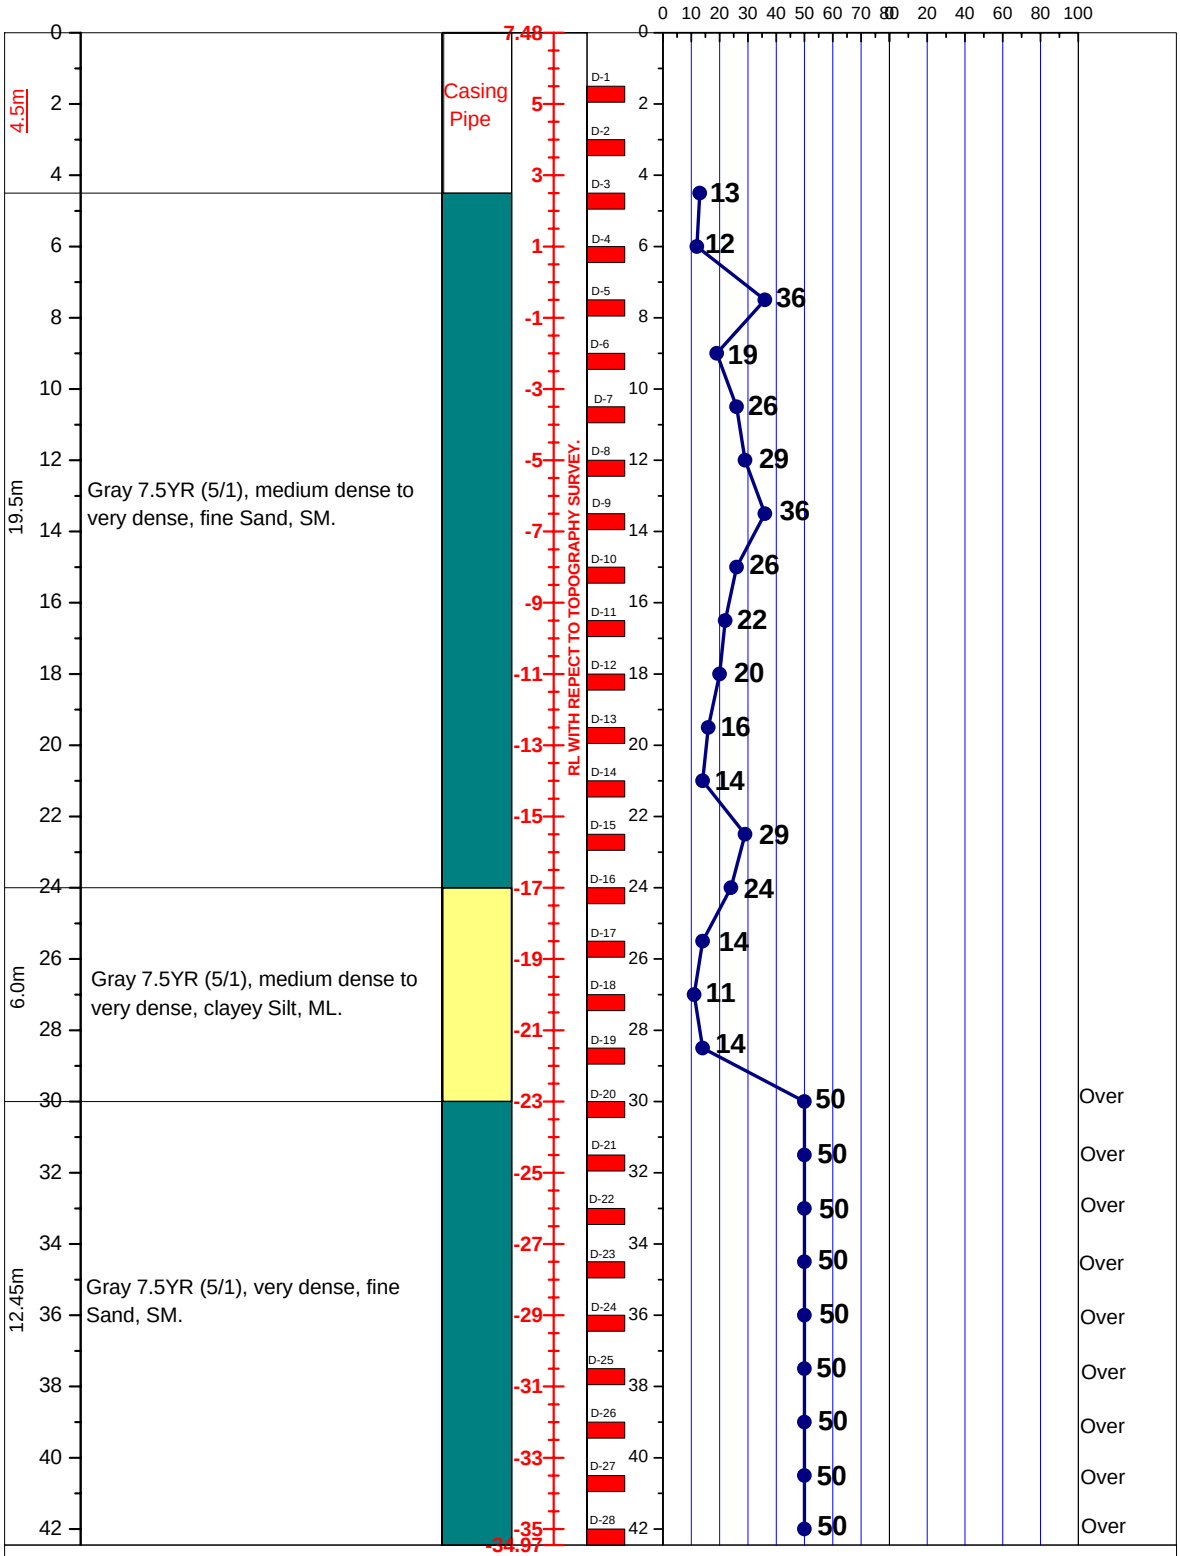

LEGEND FOR BORELOG AND GRAIN SIZE DISTRIBUTION (BASED ON 'ASTM CLASSIFICATION D-2487')

PLASTIC CLAY	SILT	PEAT/HIGHLY ORGANIC SOIL	UNDISTURBED SAMPLE
MICACEOUS FINE SAND/SILT	SAND	SHALE	DISTURBED SAMPLE

N- BLOWS DELIVERED PER FOOT BY A 140 LB HAMMER FALLING 30 INCHES

MAX^{m} PENETRATION= 50 BLOWS. AFTER 50 BLOWS PENETRATION DEPTH WERE MEASURED