| A2 PROSOIL | BOREHOLE NO: BH-1 | |
|---|---|---|
| | LOCATION : Sreerampur, Montoli Bazar, Nagolkoat, Comilla. | |
| PROJECT : Telecommunication Tower. | DEPTH OF BORING : 21.0m | R. L.:0.30m below from Road Level. |
| CLIENT : Warid Telecom International Ltd. | DATE OF BORING: 27-02-2011. | G. W. T : 3.05m below from E.G.L. |

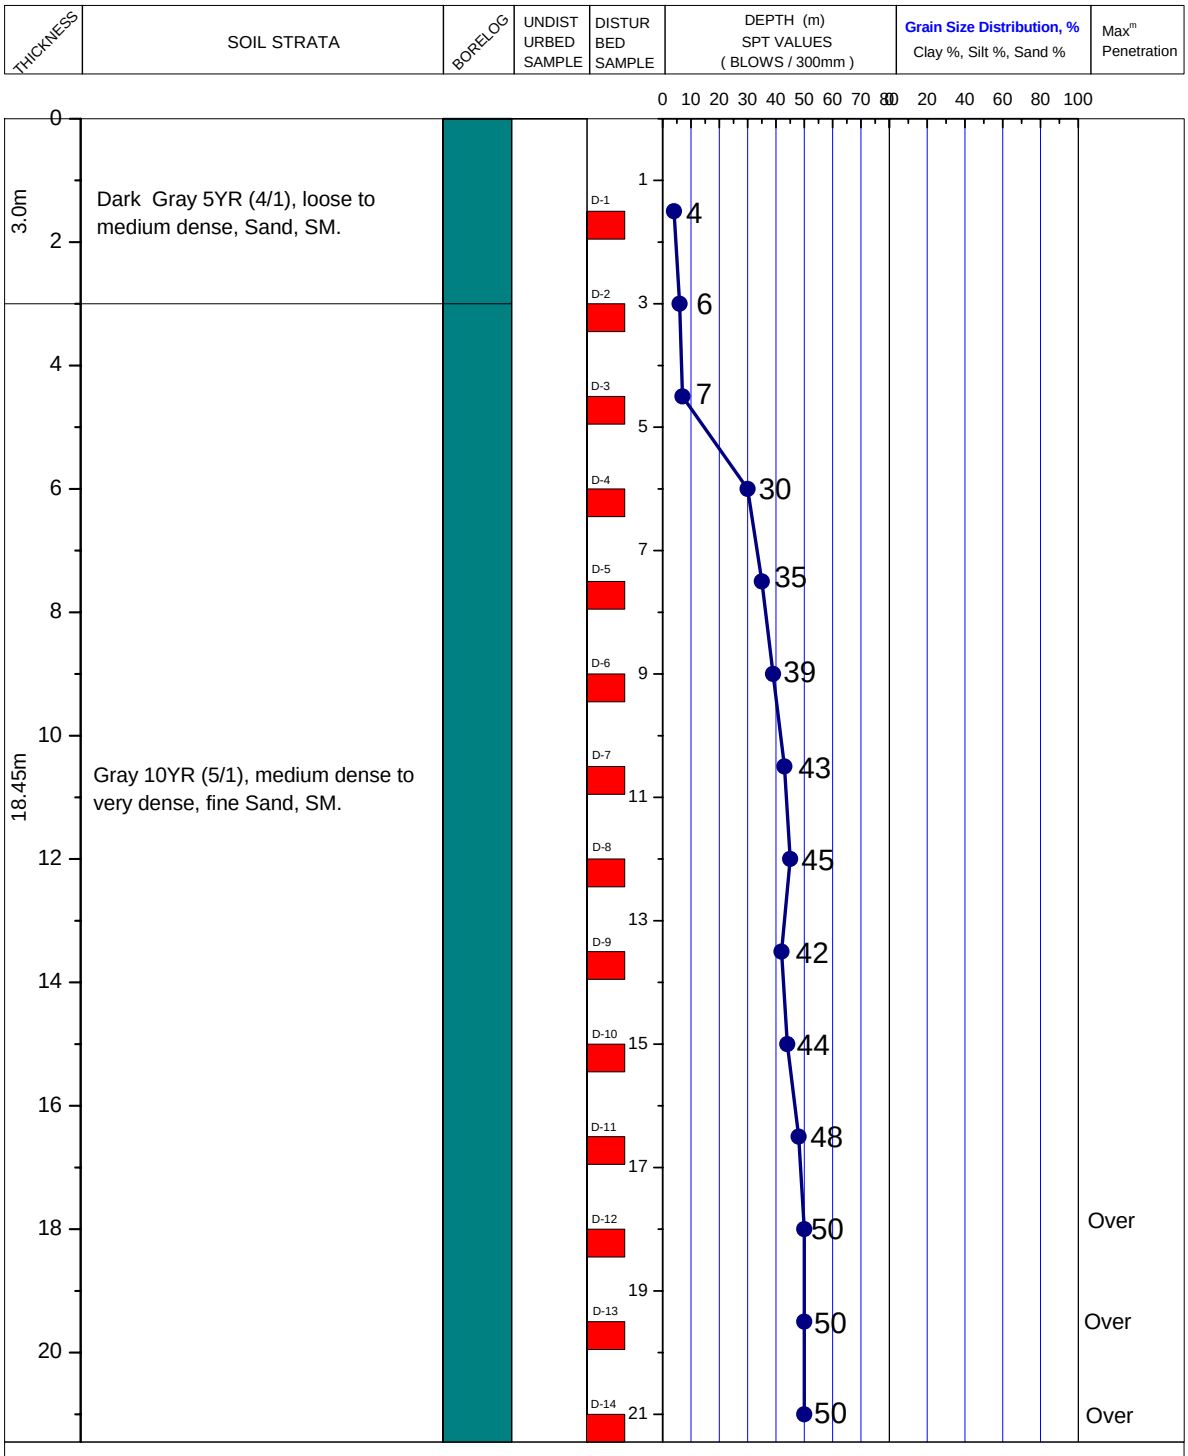


LEGEND FOR BORELOG AND GRAIN SIZE DISTRIBUTION (BASED ON 'ASTM CLASSIFICATION D-2487')

| | | | |
|---|---|---|---|
| PLASTIC CLAY | SAND | SHALE | UNDISTURBED SAMPLE |
| MICACEOUS FINE SAND/SILT | SILT | PEAT/HIGHLY ORGANIC SOIL | DISTURBED SAMPLE |

N- BLOWS DELIVERED PER FOOT BY A 140 LB HAMMER FALLING 30 INCHES

MAX$^{m}$ PENETRATION= 50 BLOWS

AFTER 50 BLOWS PENETRATION DEPTH WERE MEASURED