A2 PROSOIL	BOREHOLE NO: BH-1	
	LOCATION : 34th km of Barisal-Patuakhali Road, Patuakhali.	
PROJECT : Proposed Telekhal Bridge.	DEPTH OF BORING : 45.0m	Chainage: 34+000 R. L. :
CLIENT : Road Division, Patuakhali.	DATE OF BORING : 24-06-2010.	G. W. T : 1.83m below from E.G.L.

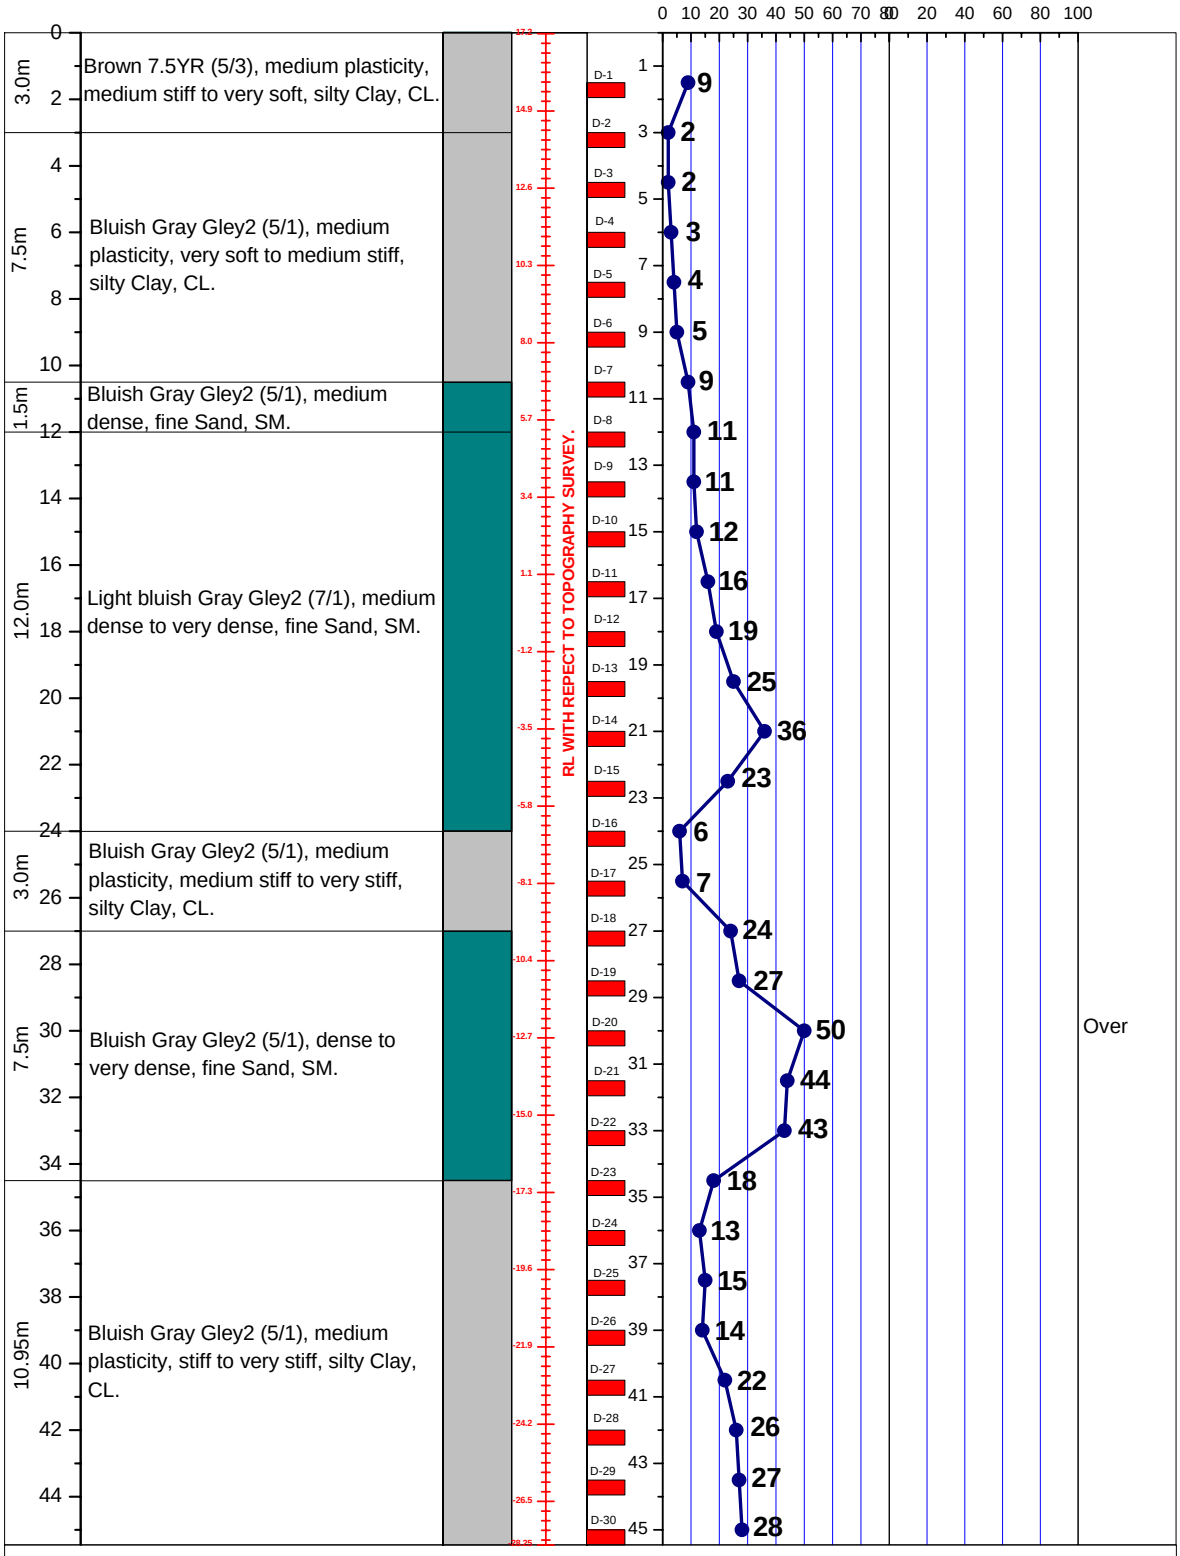

LEGEND FOR BORELOG AND GRAIN SIZE DISTRIBUTION (BASED ON 'ASTM CLASSIFICATION D-2487')

PLASTIC CLAY	SILT	PEAT/HIGHLY ORGANIC SOIL	UNDISTURBED SAMPLE
MICACEOUS FINE SAND/SILT	SAND	SHALE	DISTURBED SAMPLE

N- BLOWS DELIVERED PER FOOT BY A 140 LB HAMMER FALLING 30 INCHES

MAX^m PENETRATION= 50 BLOWS. AFTER 50 BLOWS PENETRATION DEPTH WERE MEASURED