A2 PROSOIL	BOREHOLE NO: BH-1	
	LOCATION : Leda Bazar, Teknaf, Cox's Bazar.	
PROJECT : Telecommunication Tower.	DEPTH OF BORING : 9.0m	R. L.: 0.30m above from Road Level.
CLIENT : TM International, Bangladesh Ltd.	DATE OF BORING : 25-04-2007	G. W. T : Not found.

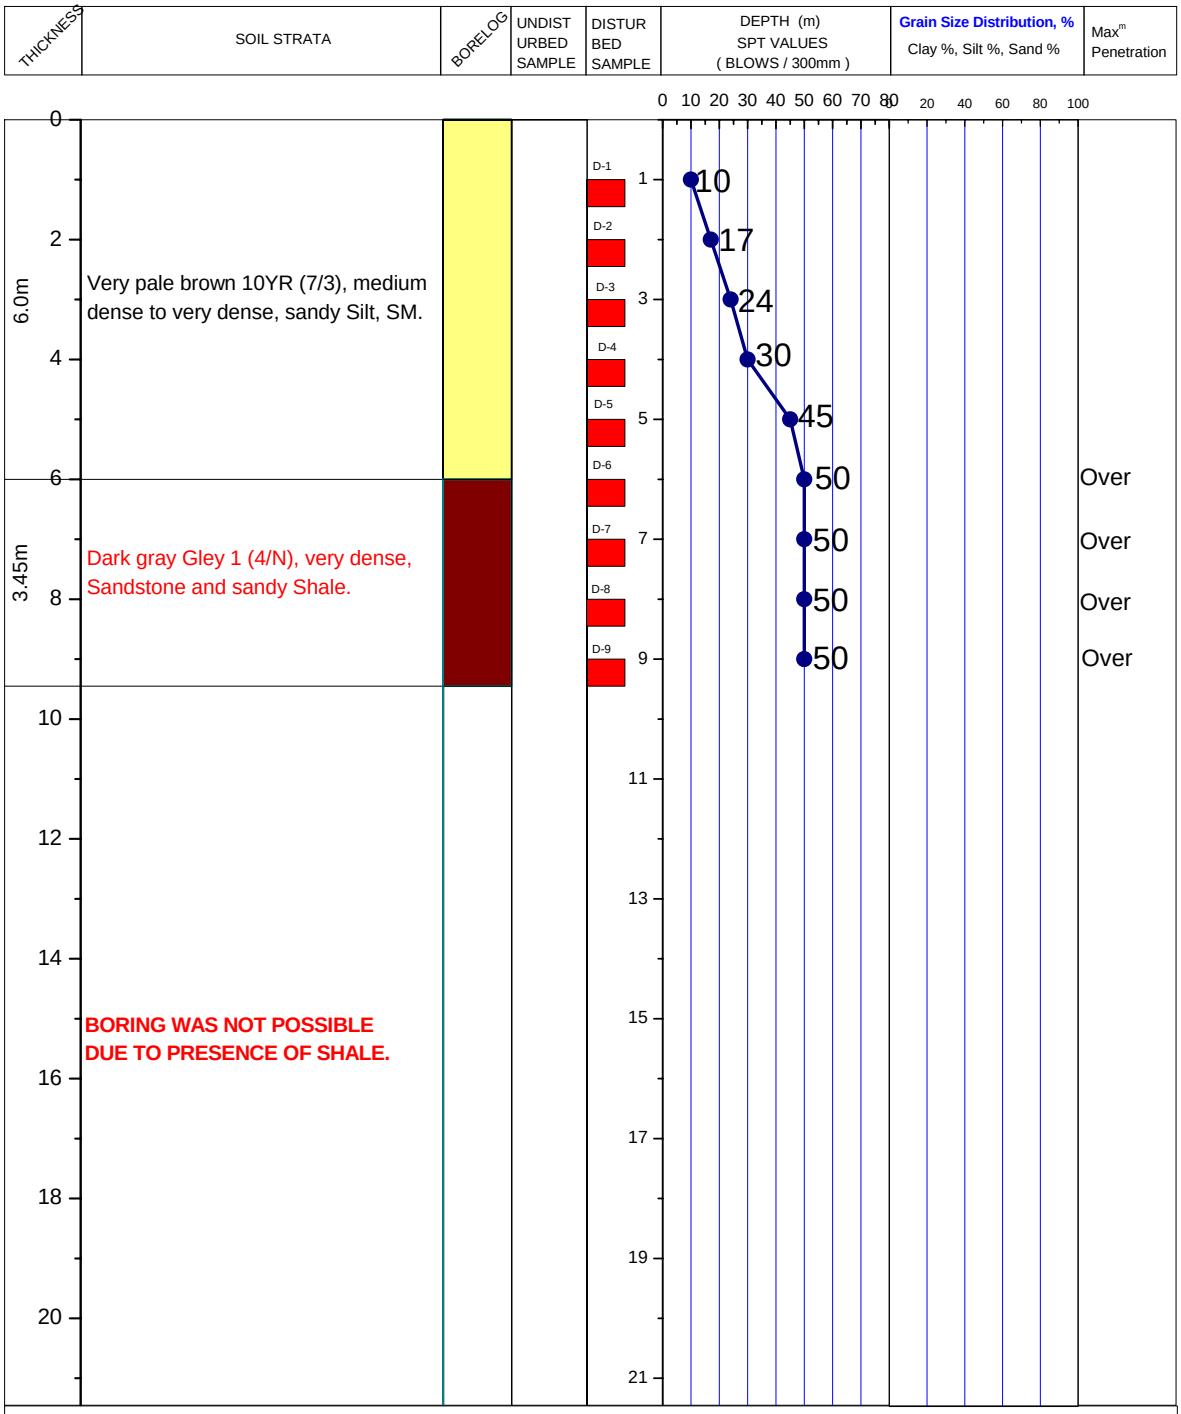

LEGEND FOR BORELOG AND GRAIN SIZE DISTRIBUTION

PLASTIC SILTY CLAY

LOW PLASTIC CLAYEY SILT

NON PLASTIC SILT

SAND

ORGANIC

UNDISTURBED SAMPLE

DISTURBED SAMPLE

SHALE

N- BLOWS DELIVERED PER FOOT BY A 140 LB HAMMER FALLING 30 INCHES

MAX^{m} PENETRATION= 50 BLOWS

AFTER 50 BLOWS PENETRATION DEPTH WERE MEASURED