A2 PROSOIL	BOREHOLE NO: BH-1	
	LOCATION : 11th k.m. of Gap No. 11/1 on the Bancharampur-Homna Road.	
PROJECT : Construction of Proposed Radhanagar Bridge.	DEPTH OF BORING : 51.5m	R. L.: 5.48m below from Road Level.
CLIENT : Road Division, B.Baria.	DATE OF BORING : 25-02-2009.	G. W. T : 0.60m below from E.G.L.

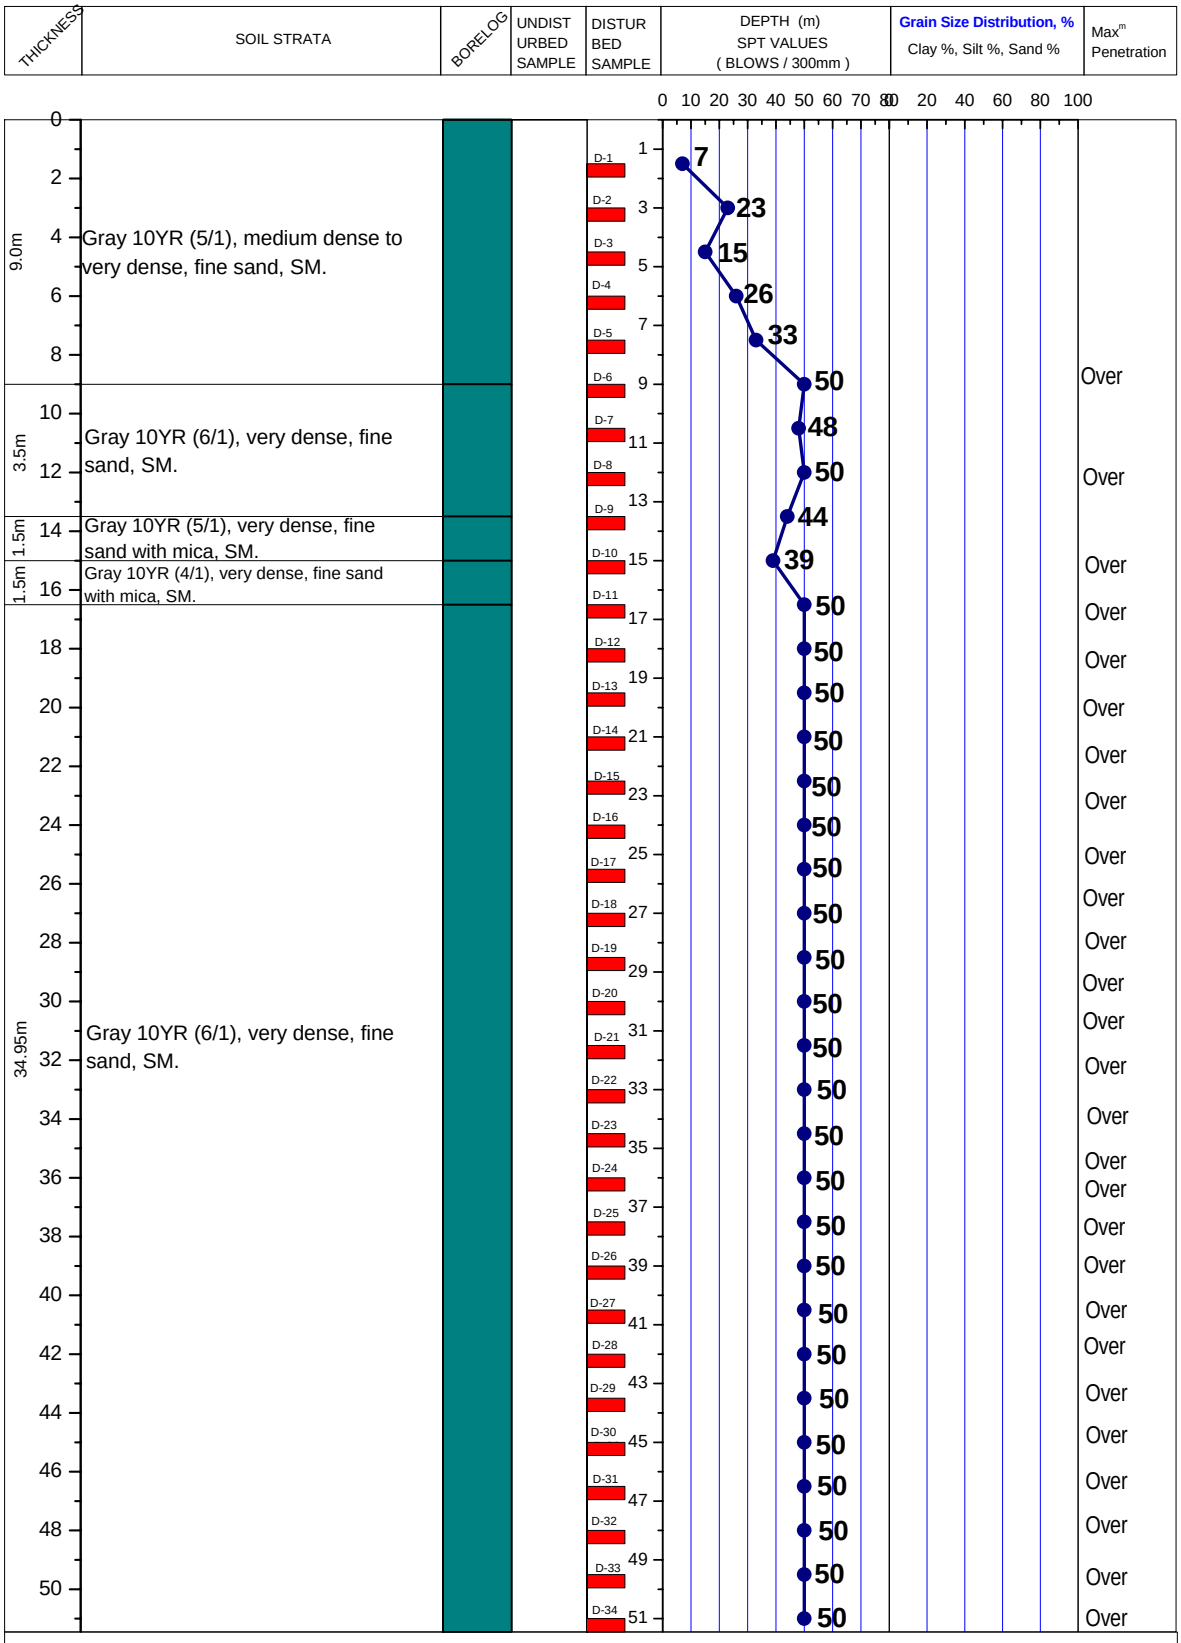

LEGEND FOR BORELOG AND GRAIN SIZE DISTRIBUTION

PLASTIC SILTY CLAY | NON PLASTIC SILT | ORGANIC | DISTURBED SAMPLE

LOW PLASTIC CLAYEY SILT | SAND | SHALE | UNDISTURBED SAMPLE

N- BLOWS DELIVERED PER FOOT BY A 140 LB HAMMER FALLING 30 INCHES

MAX^m PENETRATION= 50 BLOWS. AFTER 50 BLOWS PENETRATION DEPTH WERE MEASURED