| A2 | PROSOIL | BOREHOLE NO: BH-1 | |
|---|---|---|---|
| | | LOCATION : Pirer Bazar, Bishwanath, Sylhet. | |
| PROJECT : Telecommunication Tower. | | DEPTH OF BORING: 21.0m | R. L.: On Road Level. |
| CLIENT : Orascom Telecom Bangladesh Limited. | | DATE OF BORING : 17-09-2010. | G. W. T : 0.05m above from E. G. L. |

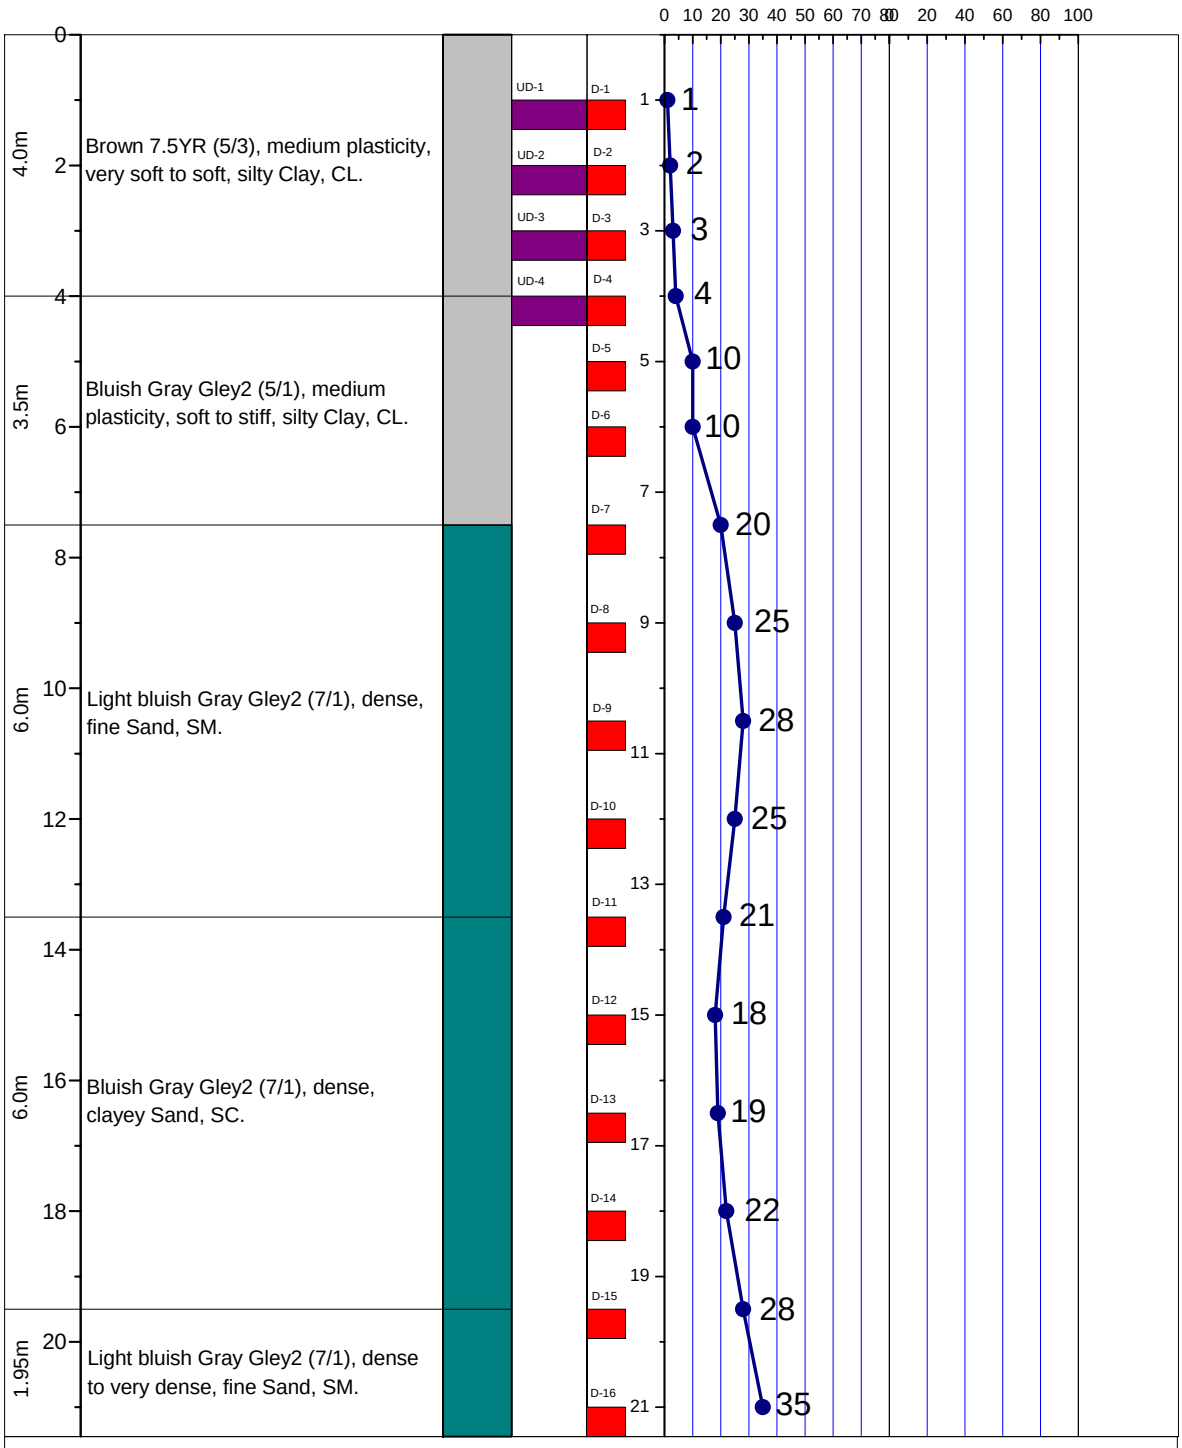


LEGEND FOR BORELOG AND GRAIN SIZE DISTRIBUTION (BASED ON 'ASTM CLASSIFICATION D-2487')

| | | | |
|---|---|---|---|
| PLASTIC CLAY | SAND | SILT | SHALE |
| PEAT/HIGHLY ORGANIC SOIL | MICACEOUS FINE SAND/SILT | UNDISTURBED SAMPLE | DISTURBED SAMPLE |

N- BLOWS DELIVERED PER FOOT BY A 140 LB HAMMER FALLING 30 INCHES

MAX$^{m}$ PENETRATION= 50 BLOWS
AFTER 50 BLOWS PENETRATION DEPTH WERE MEASURED