A2	PROSOIL	BOREHOLE NO: BH-1	
		LOCATION : Plot #24A, Road #10, Gulshan, Dhaka.	
PROJECT : Pacific Motors Limited.		DEPTH OF BORING : 27.0m	R. L.: 0.30m above from Road Level.
CLIENT : Rangs Properties Ltd.		DATE OF BORING : 11-03-2010.	G. W. T : 3.66m below from E. G. L.

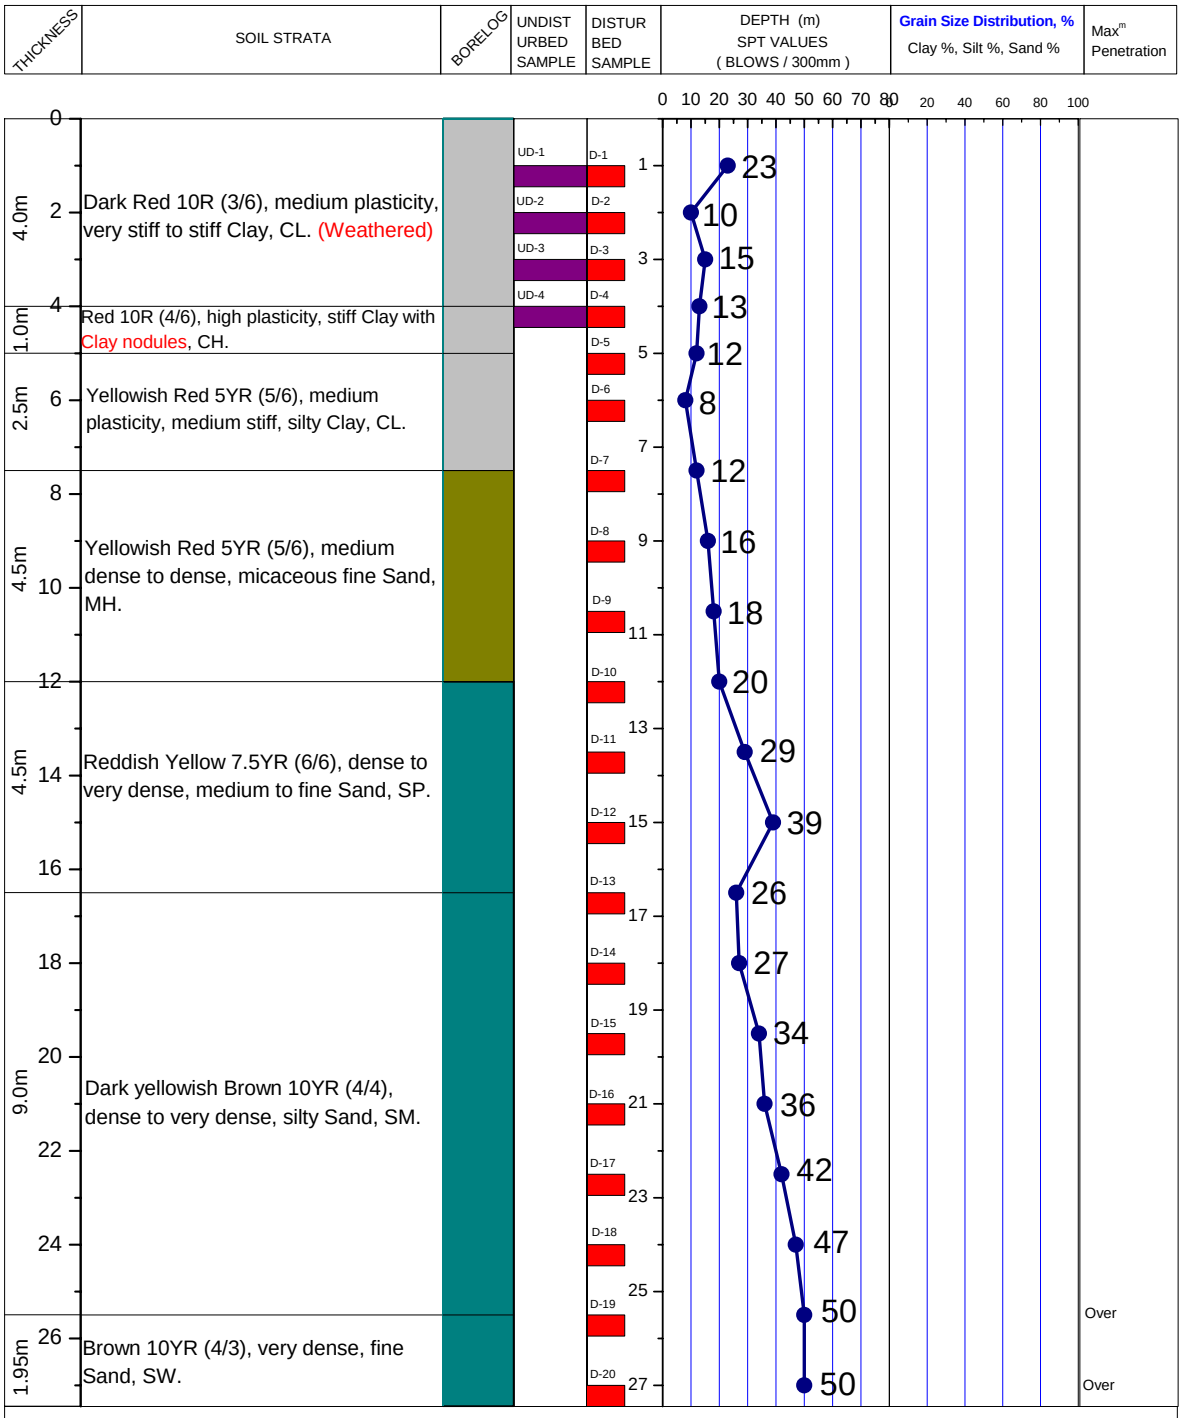

LEGEND FOR BORELOG AND GRAIN SIZE DISTRIBUTION (BASED ON 'ASTM CLASSIFICATION D-2487')

PLASTIC CLAY | SAND | SILT | SHALE

HIGHLY ORGANIC SOIL | MICACEOUS FINE SAND/SILT | UNDISTURBED SAMPLE | DISTURBED SAMPLE

N- BLOWS DELIVERED PER FOOT BY A 140 LB HAMMER FALLING 30 INCHES

MAX^{m} PENETRATION= 50 BLOWS

AFTER 50 BLOWS PENETRATION DEPTH WERE MEASURED