A2 PROSOIL	BOREHOLE NO: BH-1	
	LOCATION : Natore Sadar, Natore.	
PROJECT : Telecommunication Tower.	DEPTH OF BORING : 21.0m	R. L.: 0.60m below from Road Level.
CLIENT : Sheba Telecom (PVT.) Ltd.	DATE OF BORING : 16-07-2007.	G. W. T : 1.21m below from E. G. L.

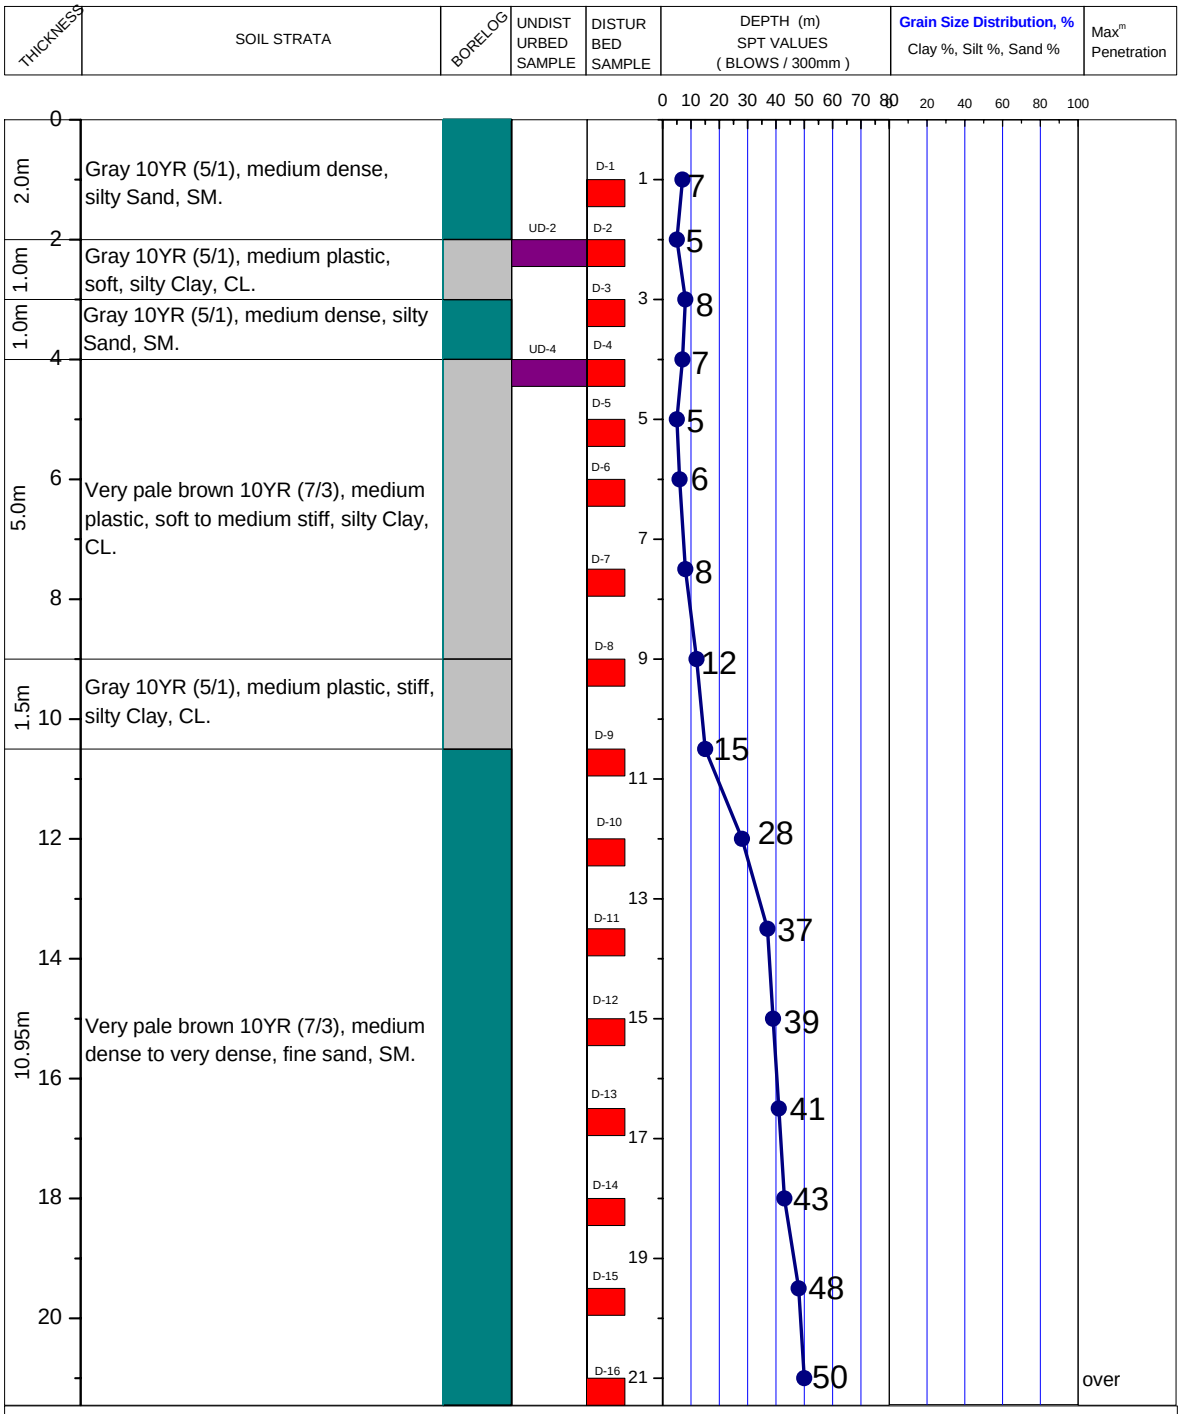

LEGEND FOR BORELOG AND GRAIN SIZE DISTRIBUTION

PLASTIC SILTY CLAY

LOW PLASTIC CLAYEY SILT

NON PLASTIC SILT

SAND

ORGANIC

UNDISTURBED SAMPLE

DISTURBED SAMPLE

SHALE

N- BLOWS DELIVERED PER FOOT BY A 140 LB HAMMER FALLING 30 INCHES

MAX^{m} PENETRATION= 50 BLOWS

AFTER 50 BLOWS PENETRATION DEPTH WERE MEASURED