A2 PROSOIL	BOREHOLE NO: BH-1	
	LOCATION: Kadomtola Bazar, Kaligonj, Satkhira.	
PROJECT : Telecommunication Tower.	DEPTH OF BORING: 21.0m	R. L.: 0.40m below from Road Level.
CLIENT : Orascom Telecom Bangladesh Limited.	DATE OF BORING : 23-09-2013.	G. W. T : On E. G. L.

THICKNESS	SOIL STRATA	BORELOG	UNDISTURBED SAMPLE	DISTURBED SAMPLE	DEPTH (m) SPT VALUES (BLOWS / 300mm)	Grain Size Distribution, % Clay %, Silt %, Sand %	Max^{m} Penetration
3.0m	Brown 7.5YR (5/3), very loose to loose, silty Sand, SM.			D-1 to D-3	4, 3, 2		
1.0m	Brown 7.5YR (5/3), medium plasticity, very soft, silty Clay, CL.			D-4	1		
3.5m	Gray 7.5YR (5/1), very loose to dense, silty Sand, SM.			D-5 to D-6	1, 3		
13.95m	Gray 10YR (6/1), dense to very dense, fine Sand, SM.			D-7 to D-16	20, 38, 36, 35, 32, 30, 33, 35, 42, 43		

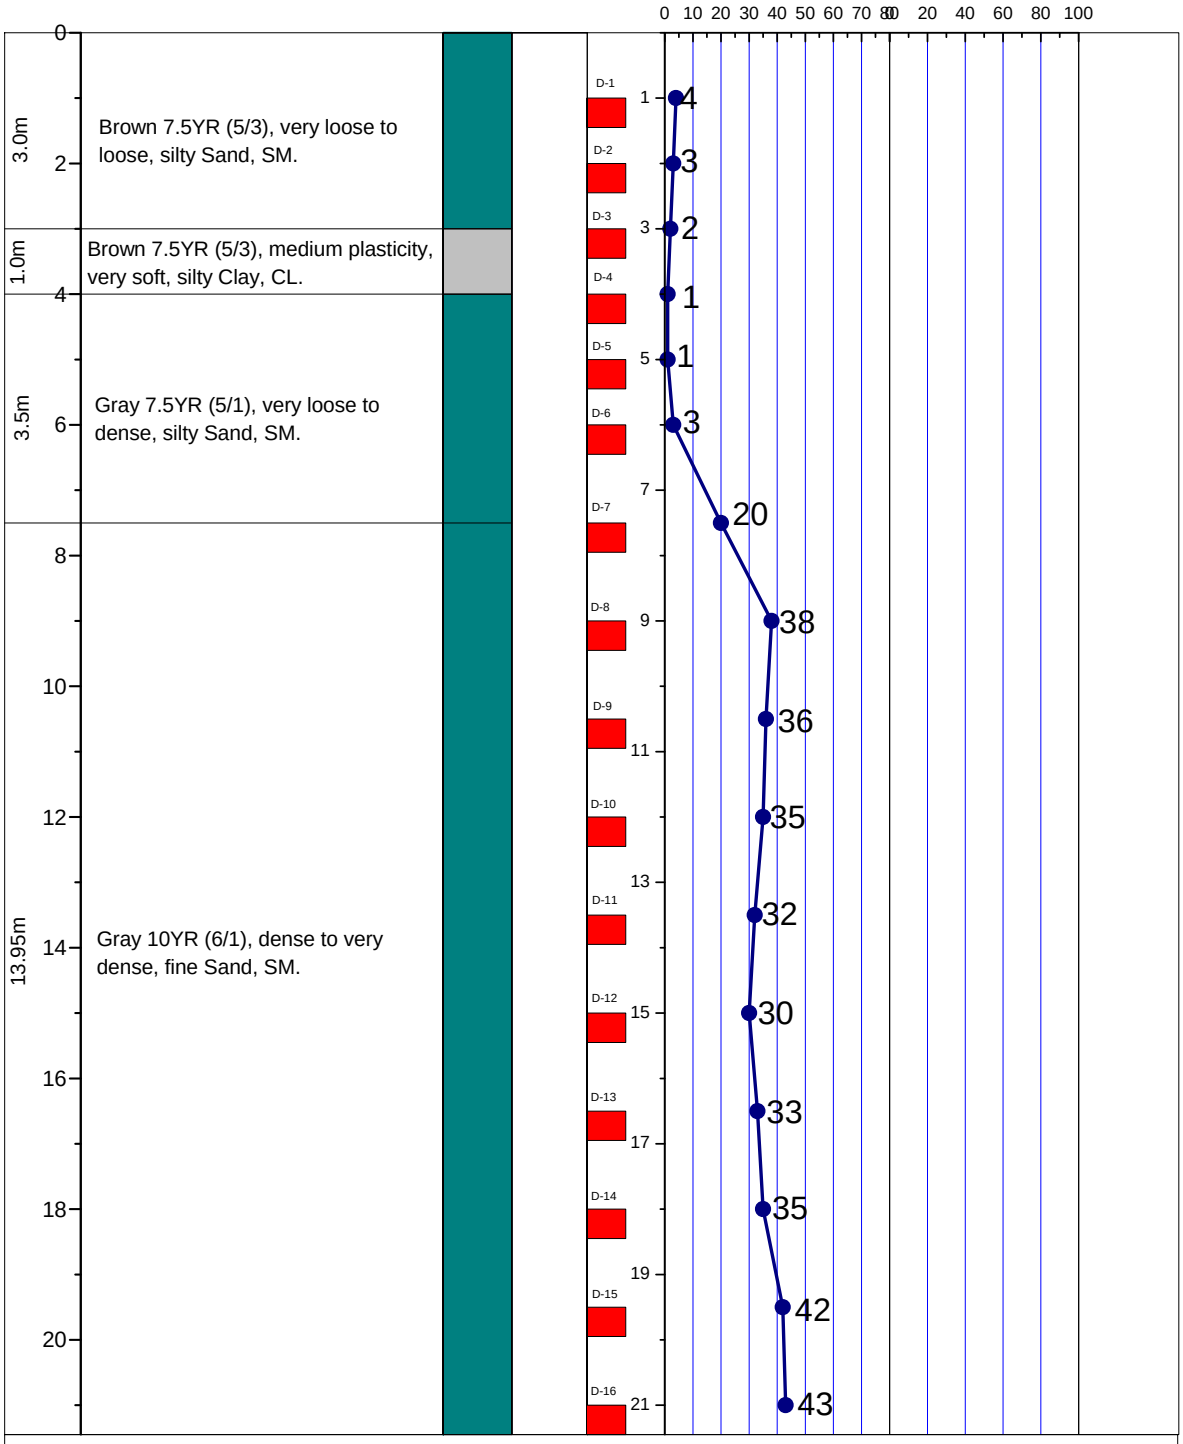

LEGEND FOR BORELOG AND GRAIN SIZE DISTRIBUTION (BASED ON 'ASTM CLASSIFICATION D-2487')

PLASTIC CLAY	SAND	SILT	SHALE
PEAT/HIGHLY ORGANIC SOIL	MICACEOUS FINE SAND/SILT	UNDISTURBED SAMPLE	DISTURBED SAMPLE

N- BLOWS DELIVERED PER FOOT BY A 140 LB HAMMER FALLING 30 INCHES

MAX^{m} PENETRATION= 50 BLOWS
AFTER 50 BLOWS PENETRATION DEPTH WERE MEASURED