A2	PROSOIL	BOREHOLE NO: BH-1	
		LOCATION : Gap No 20/1 Of 20th Km Of Narsingdi-Madongonj (Up To Bastol) Road, Narayangonj.	
PROJECT : Proposed Bridge at Gap No 20/1.		DEPTH OF BORING : 30.0m	Chainage: 0+038 R. L. : 20.2
CLIENT : Road Division, Narayangonj.		DATE OF BORING : 03-04-2011.	G. W. T : 2.75m below from E.G.L.

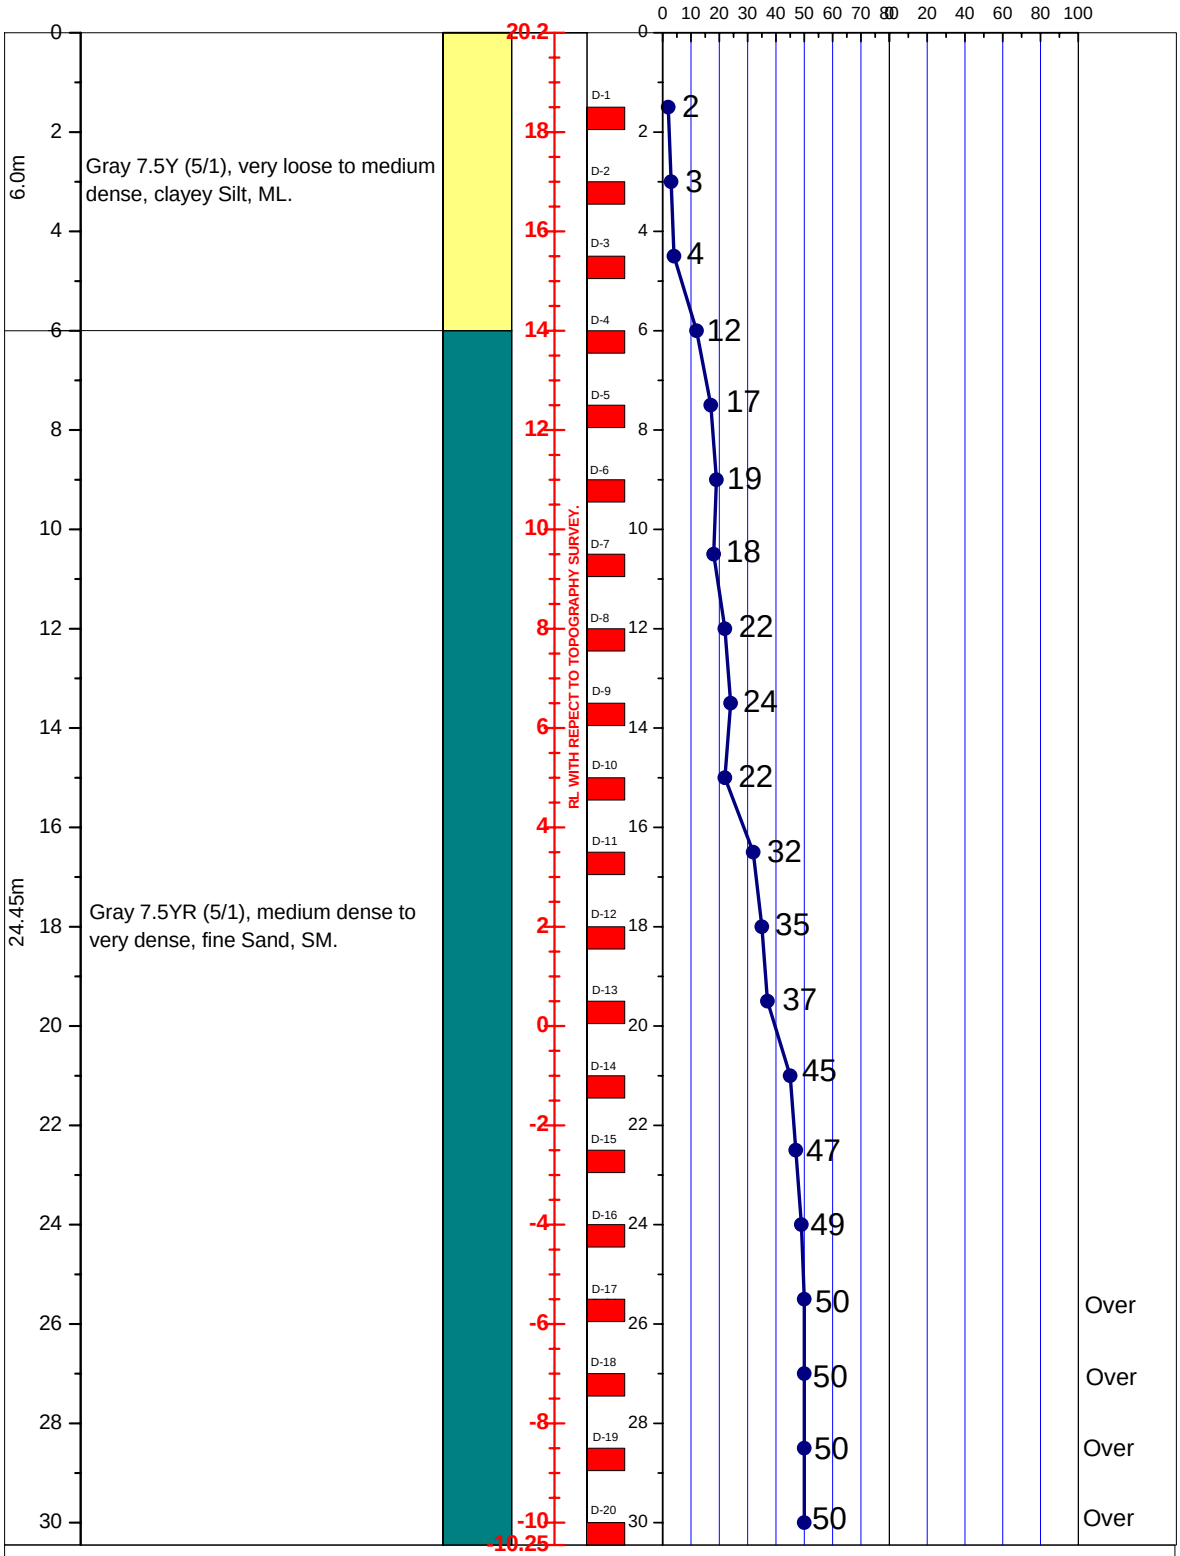

LEGEND FOR BORELOG AND GRAIN SIZE DISTRIBUTION (BASED ON 'ASTM CLASSIFICATION D-2487')

PLASTIC CLAY	SILT	PEAT/HIGHLY ORGANIC SOIL	UNDISTURBED SAMPLE
MICACEOUS FINE SAND/SILT	SAND	SHALE	DISTURBED SAMPLE

N- BLOWS DELIVERED PER FOOT BY A 140 LB HAMMER FALLING 30 INCHES

MAX^m PENETRATION= 50 BLOWS. AFTER 50 BLOWS PENETRATION DEPTH WERE MEASURED