A2 PROSOIL	BOREHOLE NO: BH-1	
	LOCATION : LRP 008+2368 of Kasba-Kuti Road.	
PROJECT : Construction of Proposed Existing bailey Bridge.	DEPTH OF BORING : 51.0m	R. L.: 3.35m below from Road Level.
CLIENT : Road Division, B.Baria.	DATE OF BORING : 03-06-2009.	G. W. T : 1.80m below from E.G.L.

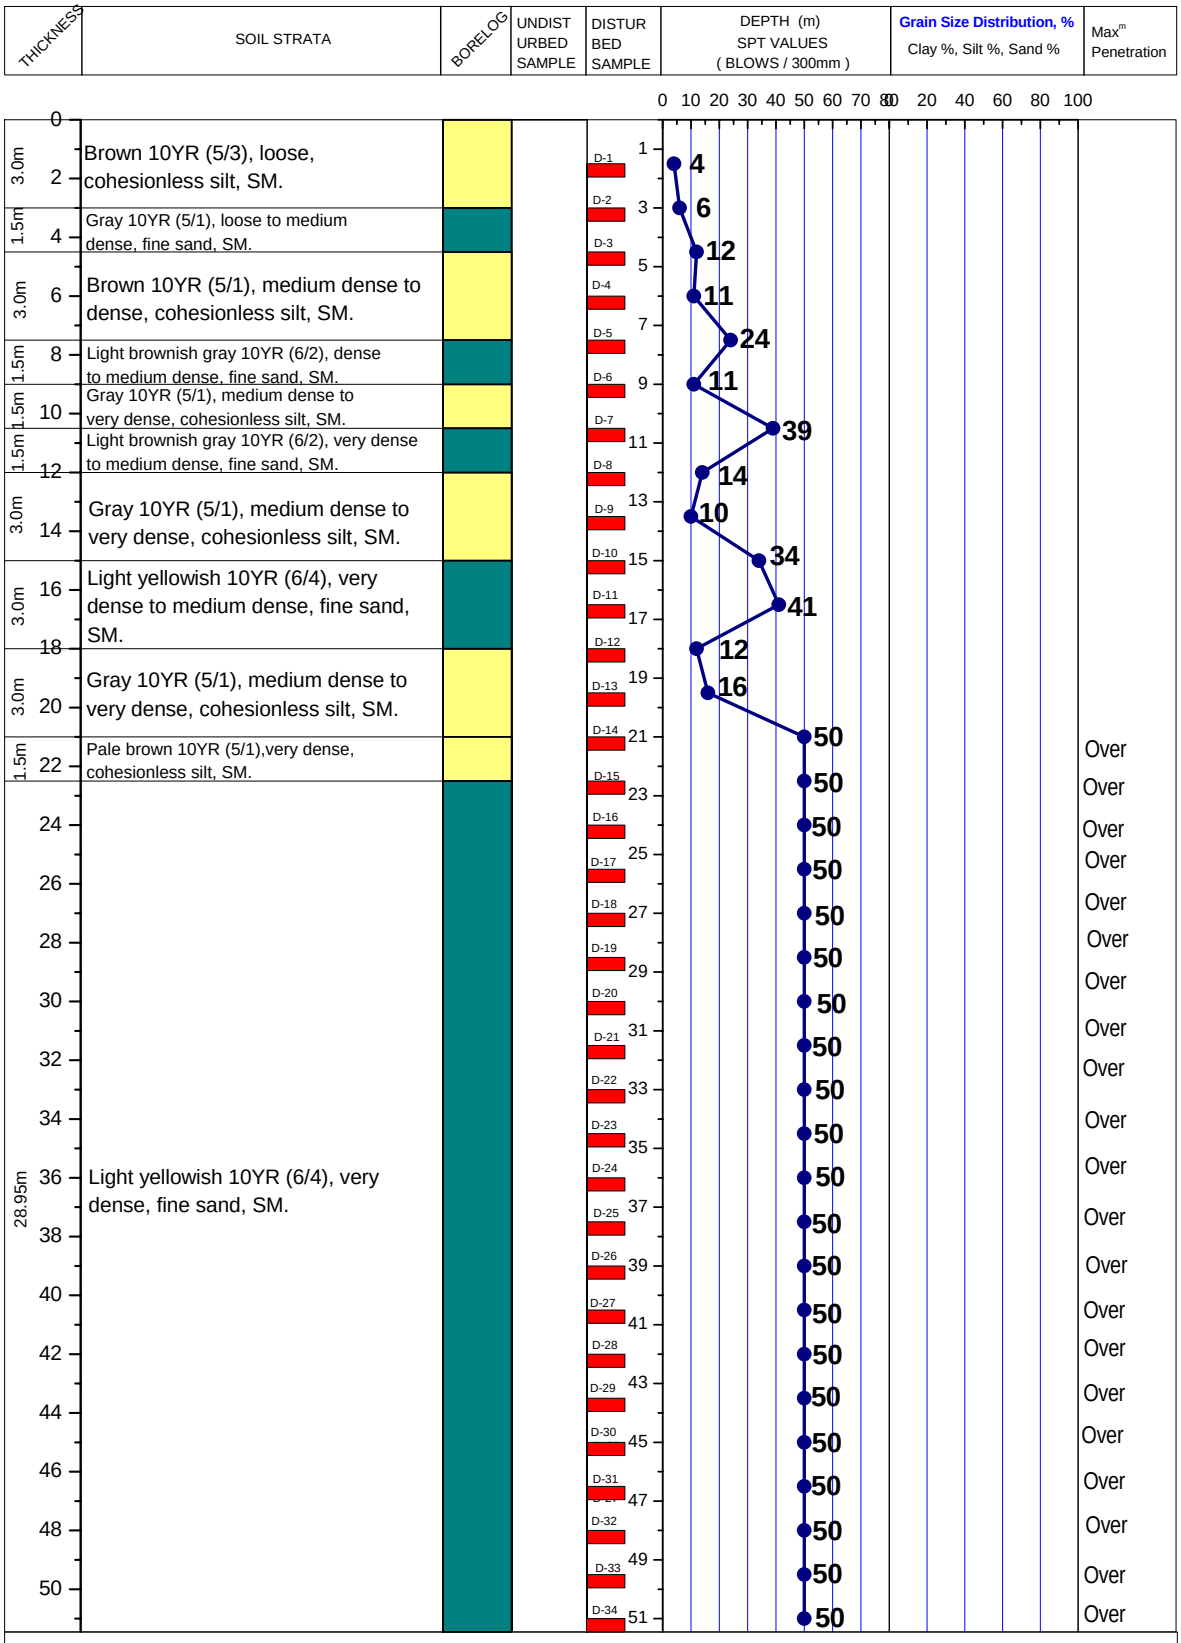

LEGEND FOR BORELOG AND GRAIN SIZE DISTRIBUTION

PLASTIC SILTY CLAY | NON PLASTIC SILT | ORGANIC | DISTURBED SAMPLE

LOW PLASTIC CLAYEY SILT | SAND | SHALE | UNDISTURBED SAMPLE

N- BLOWS DELIVERED PER FOOT BY A 140 LB HAMMER FALLING 30 INCHES

MAX^{m} PENETRATION= 50 BLOWS. AFTER 50 BLOWS PENETRATION DEPTH WERE MEASURED