A2 PROSOIL	BOREHOLE NO: BH-1	
	LOCATION : 30m Bridge over on Dhantara GC-Kushura GC, at Ch. 1+450m.	
PROJECT : Proposed 30.0m Bridge.	DEPTH OF BORING : 16.5m	R. L.: 4.665m
CLIENT : DS&M Consultant, RIIP-II, LGED.	DATE OF BORING : 22-10-2008.	G. W. T : 1.22m above from E. G. L.

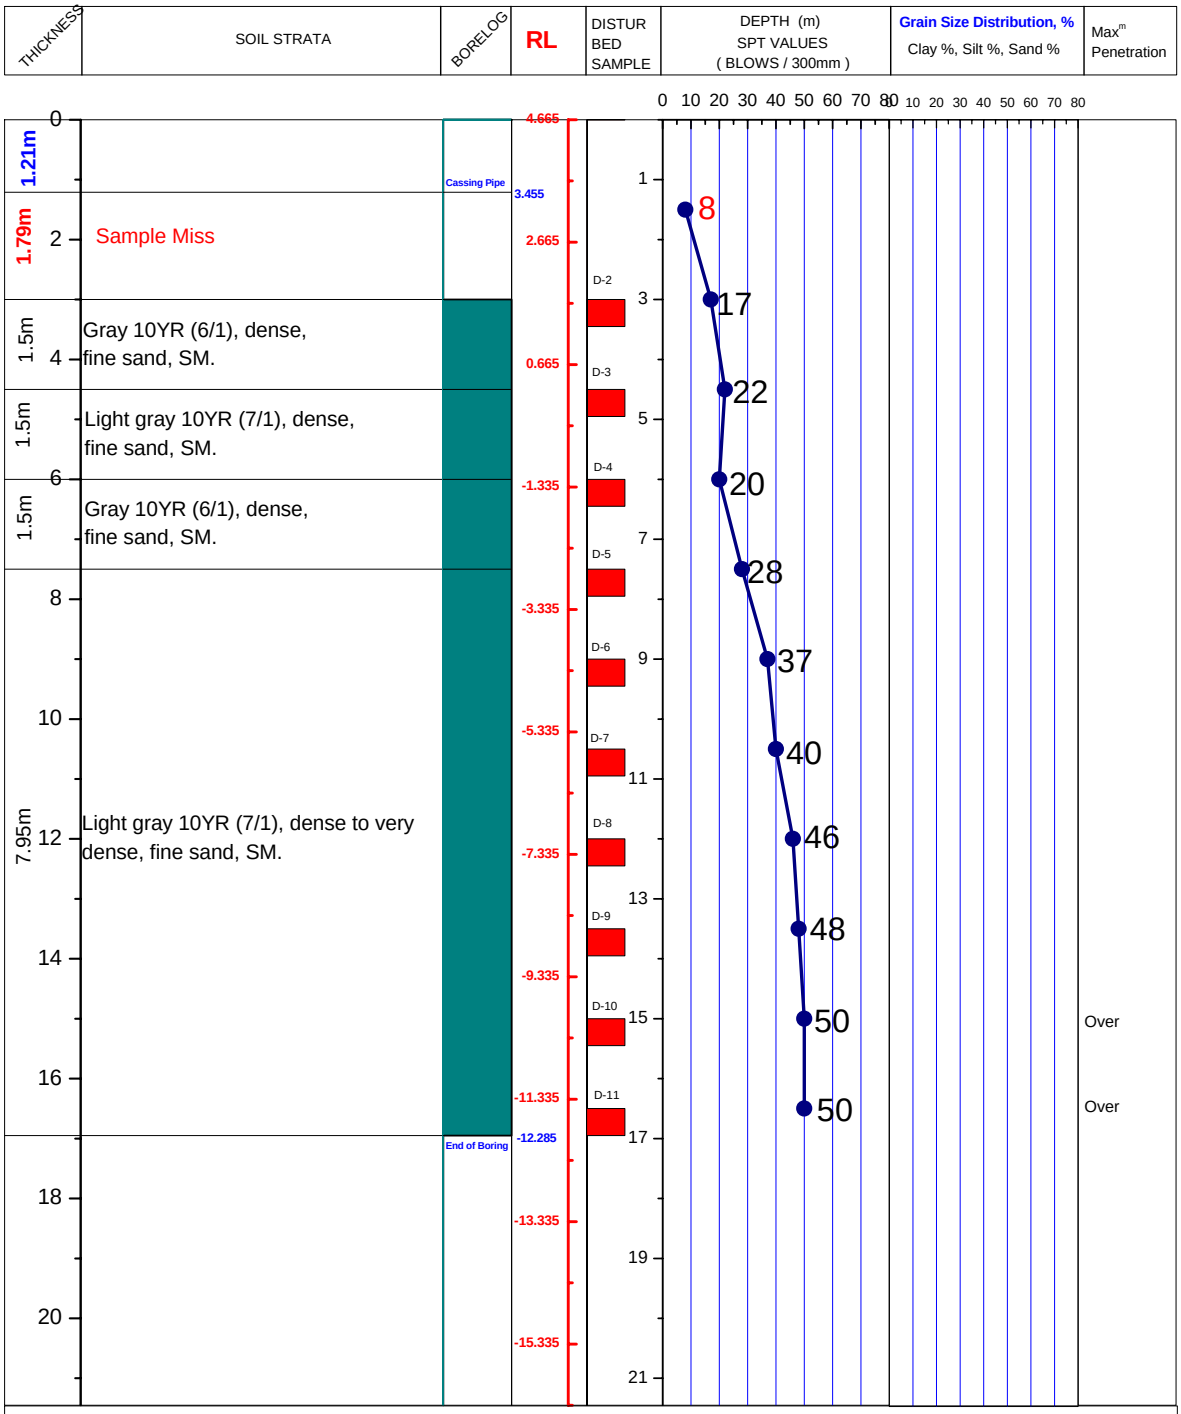

LEGEND FOR BORELOG AND GRAIN SIZE DISTRIBUTION

PLASTIC SILTY CLAY

LOW PLASTIC CLAYEY SILT

NON PLASTIC SILT

SAND

ORGANIC

UNDISTURBED SAMPLE

DISTURBED SAMPLE

SHALE

N- BLOWS DELIVERED PER FOOT BY A 140 LB HAMMER FALLING 30 INCHES

MAX^{m} PENETRATION= 50 BLOWS

AFTER 50 BLOWS PENETRATION DEPTH WERE MEASURED