A2	PROSOIL	BOREHOLE NO: BH-1	
		LOCATION : 21st k.m. of Gap no. (21/2) of Sarail-Nasirngar-Lakhai-Hobigonj Road.	
PROJECT : Construction of Proposed Bridge.		DEPTH OF BORING : 42.0m	Chainage: 20+350 R. L. : 10.94
CLIENT : Road Division, B.Baria.		DATE OF BORING : 10-09-2009	G. W. T : 3.05m below from E.G.L.

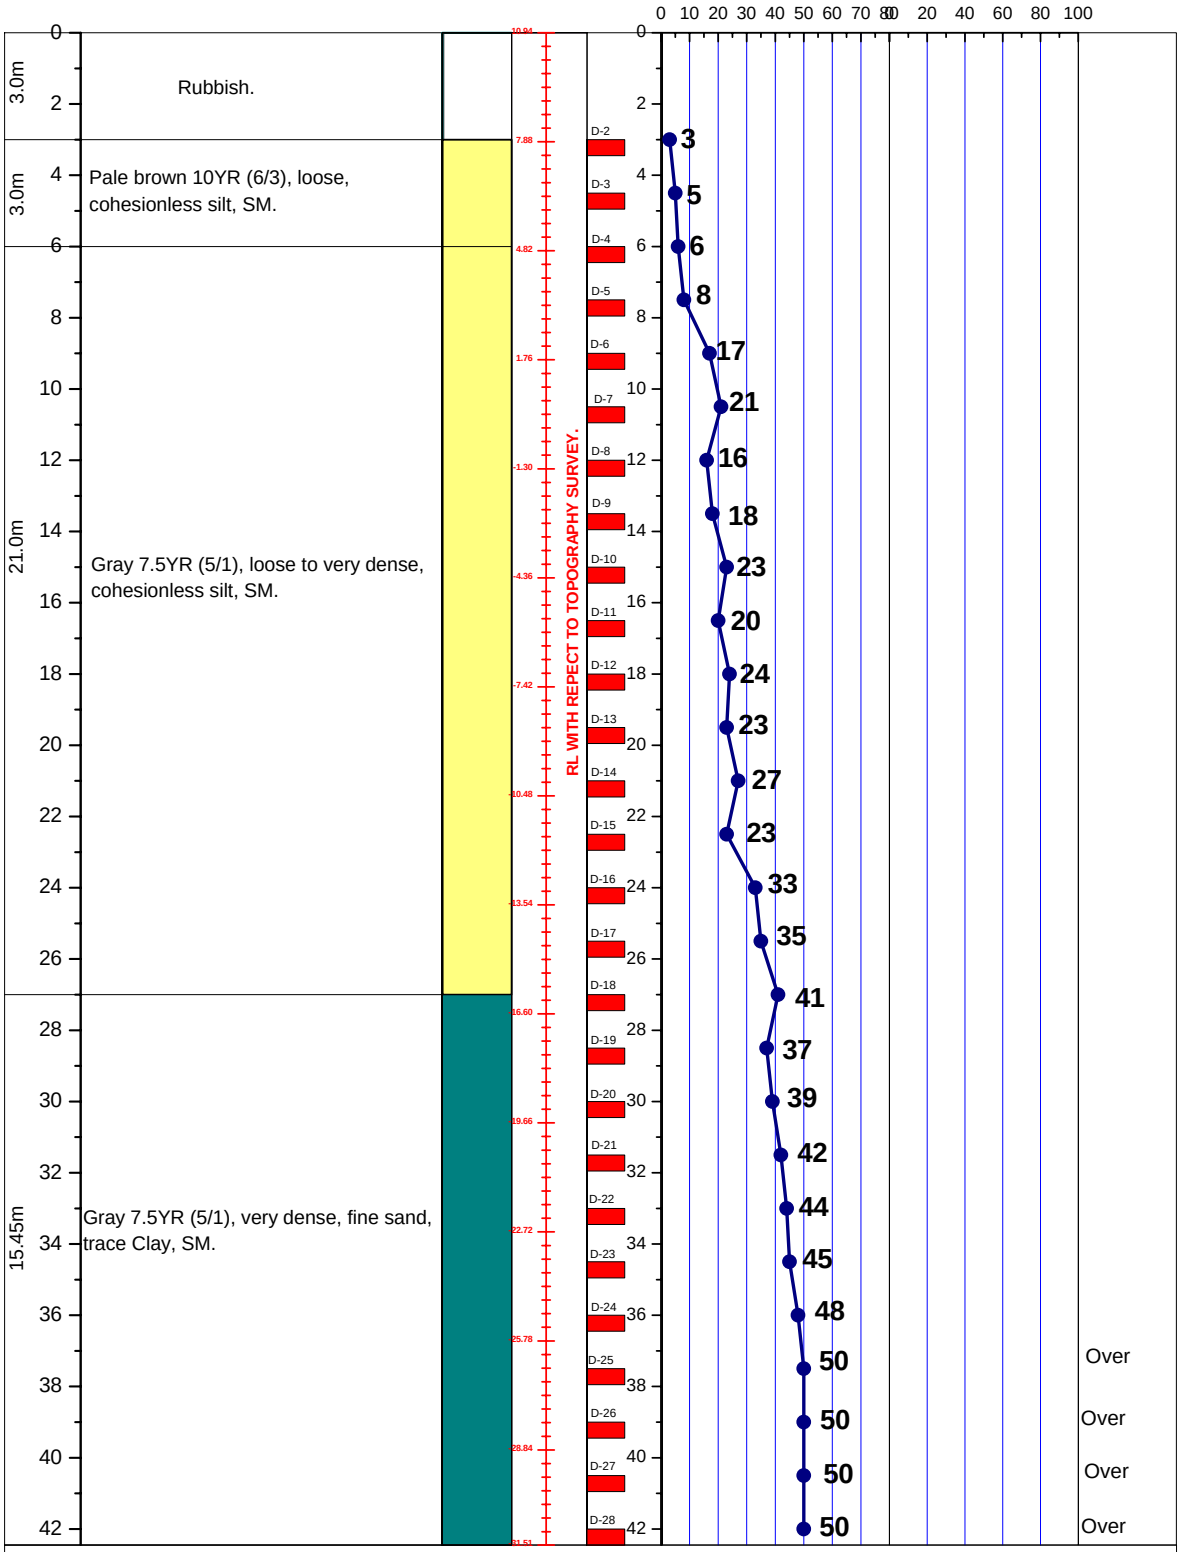

LEGEND FOR BORELOG AND GRAIN SIZE DISTRIBUTION (BASED ON 'ASTM CLASSIFICATION D-2487')

PLASTIC CLAY	SILT	PEAT/HIGHLY ORGANIC SOIL	UNDISTURBED SAMPLE
MICACEOUS FINE SAND/SILT	SAND	SHALE	DISTURBED SAMPLE

N- BLOWS DELIVERED PER FOOT BY A 140 LB HAMMER FALLING 30 INCHES

MAX^m PENETRATION= 50 BLOWS. AFTER 50 BLOWS PENETRATION DEPTH WERE MEASURED