A2	PROSOIL	BOREHOLE NO: BH-1	
		LOCATION : Habiganj Sadar, Habiganj.	
PROJECT : Construction Of Two-Storied Residential Building For The Residence Of Executive Engineer.		DEPTH OF BORING : 33.0m	R. L. : On Road Level.
CLIENT : Road Division, Habiganj.		DATE OF BORING : 20-05-2013.	G. W. T : 0.91m below from E.G.L.

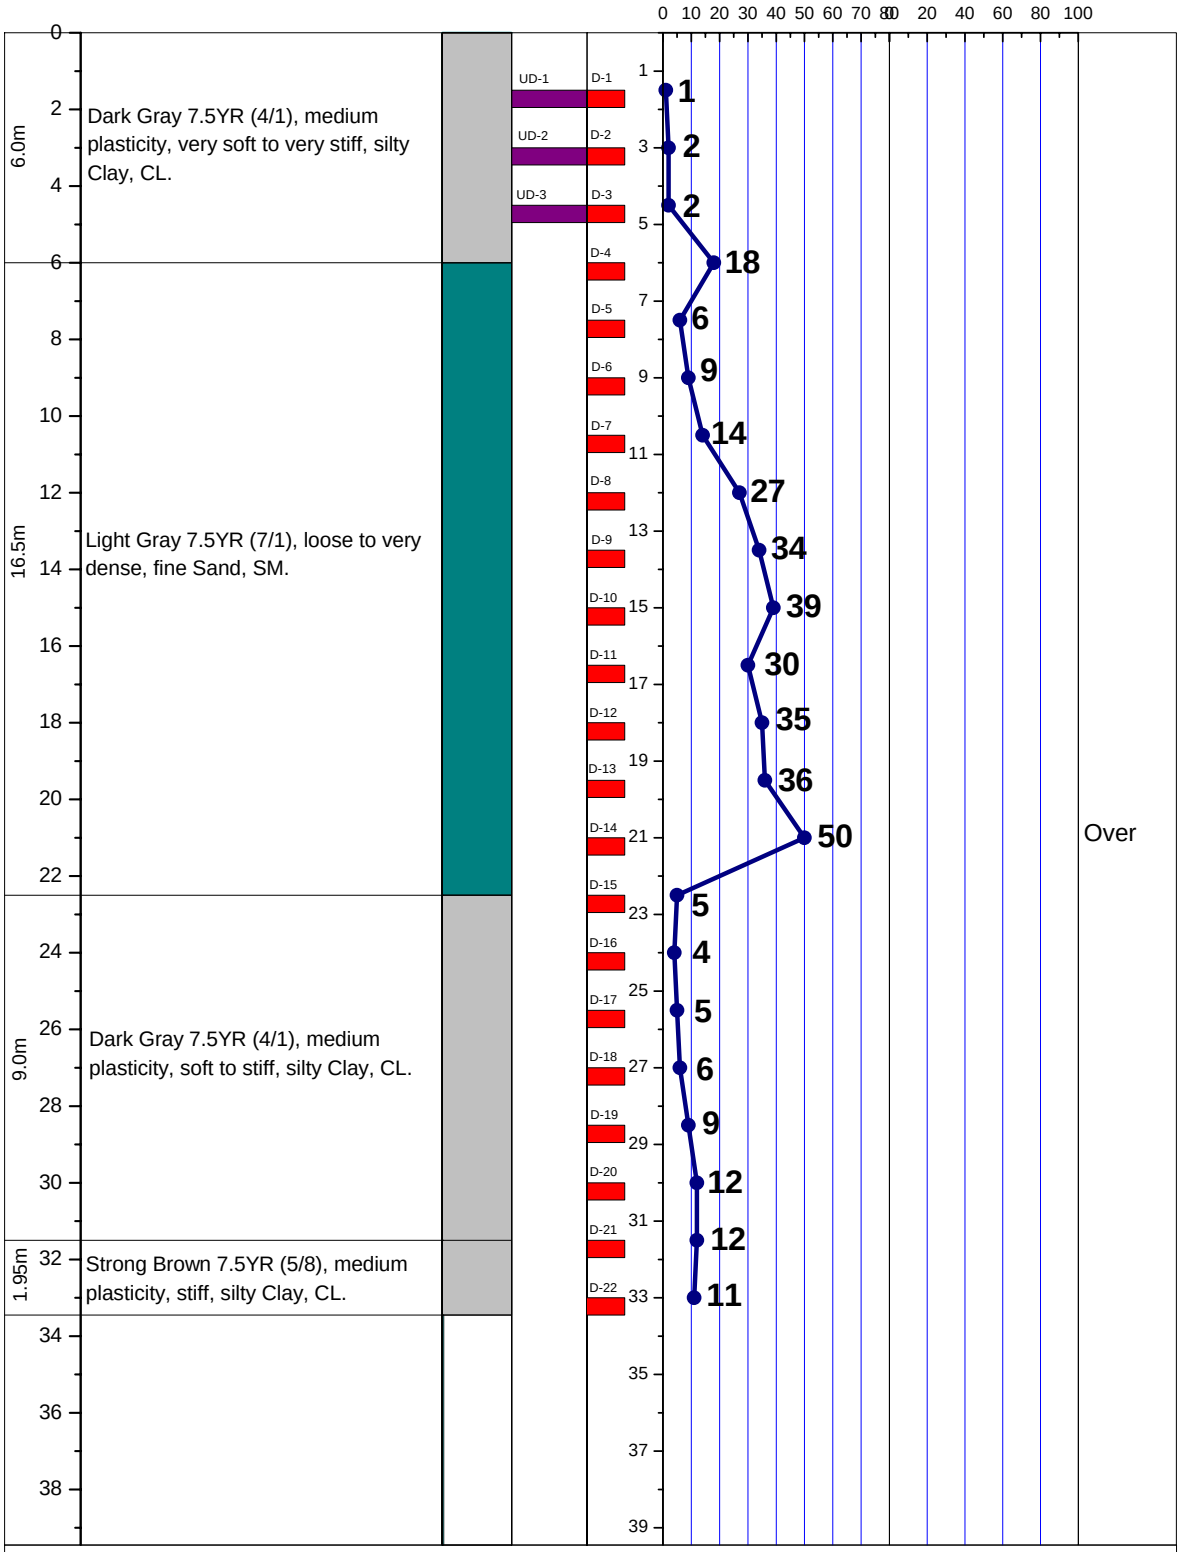

LEGEND FOR BORELOG AND GRAIN SIZE DISTRIBUTION (BASED ON 'ASTM CLASSIFICATION D-2487')

PLASTIC CLAY	SILT	PEAT/HIGHLY ORGANIC SOIL	UNDISTURBED SAMPLE
MICACEOUS FINE SAND/SILT	SAND	SHALE	DISTURBED SAMPLE

N- BLOWS DELIVERED PER FOOT BY A 140 LB HAMMER FALLING 30 INCHES

MAX^{m} PENETRATION= 50 BLOWS. AFTER 50 BLOWS PENETRATION DEPTH WERE MEASURED

A2	PROSOIL	BOREHOLE NO: BH-2	
		LOCATION : Habiganj Sadar, Habiganj.	
PROJECT : Construction Of Two-Storied Residential Building For The Residence Of Executive Engineer.		DEPTH OF BORING : 39.0m	R. L. : On Road Level.
CLIENT : Road Division, Habiganj.		DATE OF BORING : 22-05-2013.	G. W. T : 0.91m below from E.G.L.

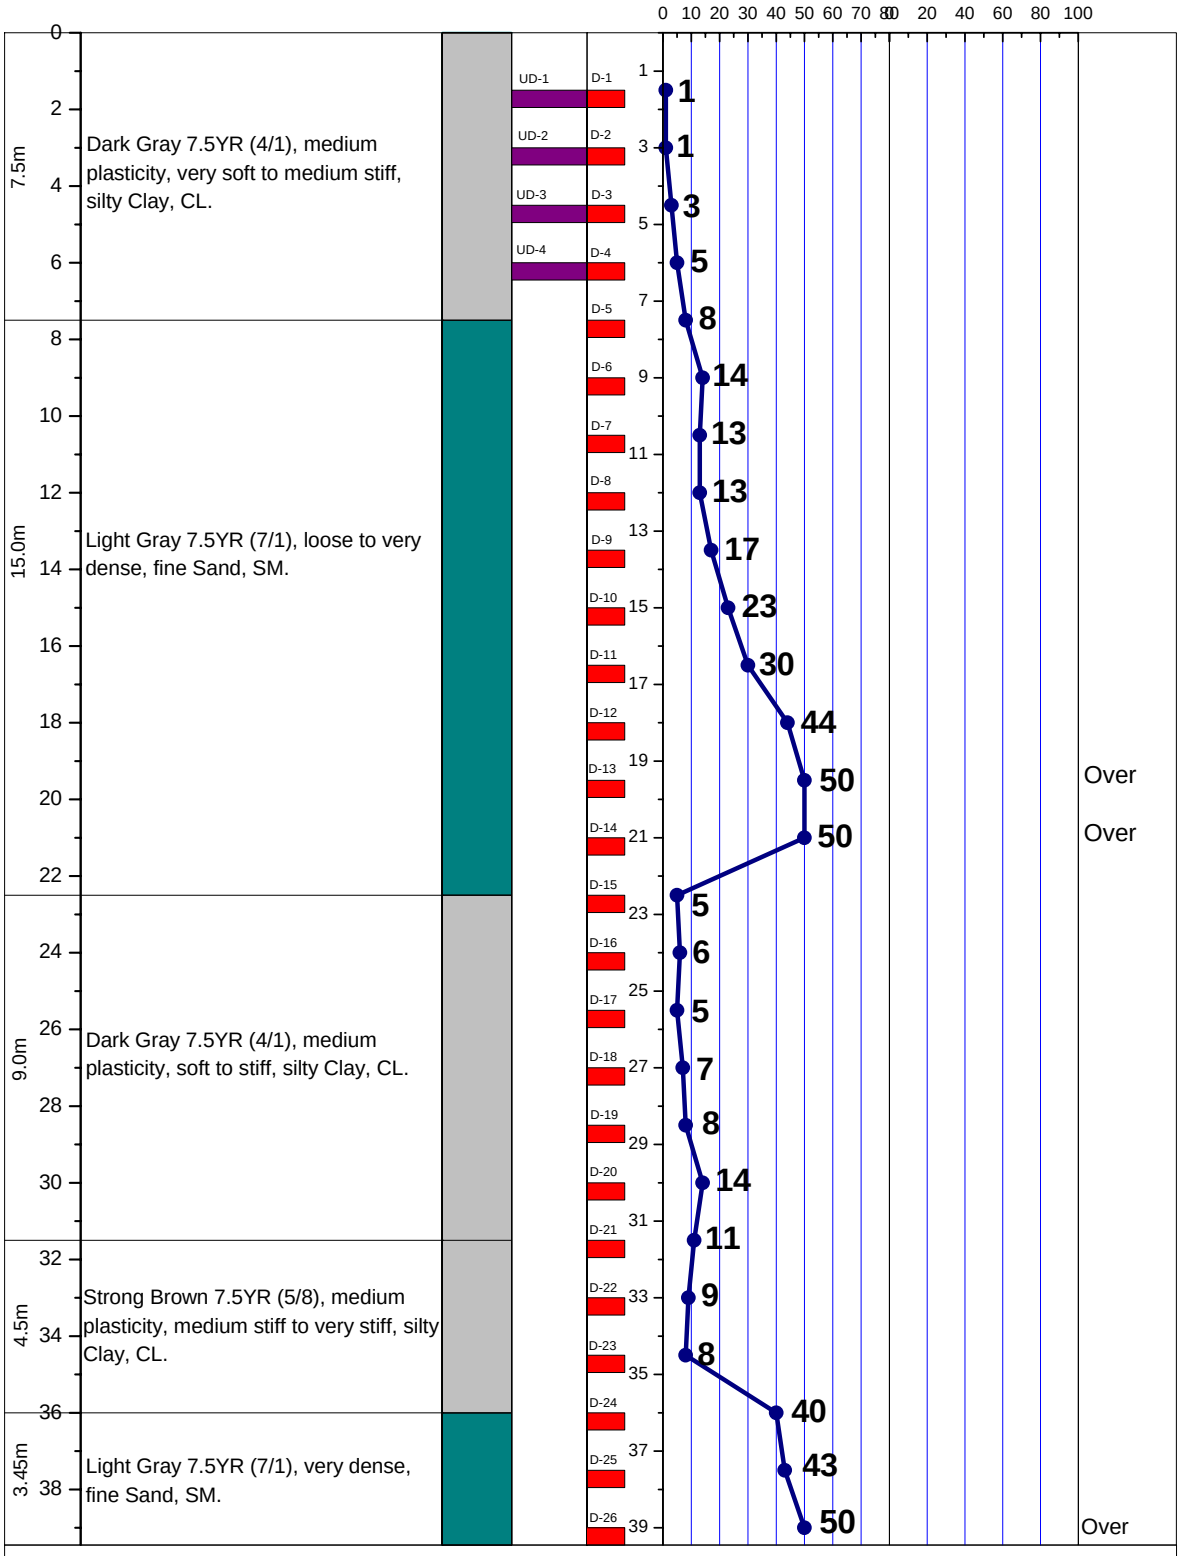

LEGEND FOR BORELOG AND GRAIN SIZE DISTRIBUTION (BASED ON 'ASTM CLASSIFICATION D-2487')

PLASTIC CLAY	SILT	PEAT/HIGHLY ORGANIC SOIL	UNDISTURBED SAMPLE
MICACEOUS FINE SAND/SILT	SAND	SHALE	DISTURBED SAMPLE

N- BLOWS DELIVERED PER FOOT BY A 140 LB HAMMER FALLING 30 INCHES

MAX^{m} PENETRATION= 50 BLOWS. AFTER 50 BLOWS PENETRATION DEPTH WERE MEASURED

A2	PROSOIL	BOREHOLE NO: BH-3	
		LOCATION : Habiganj Sadar, Habiganj.	
PROJECT : Construction Of Two-Storied Residential Building For The Residence Of Executive Engineer.		DEPTH OF BORING : 39.0m	R. L. : On Road Level.
CLIENT : Road Division, Habiganj.		DATE OF BORING : 24-05-2013.	G. W. T : 0.91m below from E.G.L.

THICKNESS	SOIL STRATA	BORELOG	UNDISTURBED SAMPLE	DISTURBED SAMPLE	DEPTH (m) SPT VALUES (BLOWS / 300mm)	Grain Size Distribution, % Clay %, Silt %, Sand %	Max^{m} Penetration
7.5m	Dark Gray 7.5YR (4/1), medium plasticity, very soft to medium stiff, silty Clay, CL.		UD-1, UD-2, UD-3, UD-4	D-1 to D-5	3, 3, 2, 2, 7		
16.5m	Light Gray 7.5YR (7/1), medium dense to very dense, fine Sand, SM.			D-6 to D-14	13, 11, 18, 35, 36, 38, 45, 39, 26		
7.5m	Dark Gray 7.5YR (4/1), medium plasticity, medium stiff to stiff, silty Clay, CL.			D-15 to D-20	11, 8, 6, 9, 9, 8		
4.5m	Strong Brown 7.5YR (5/8), medium plasticity, medium stiff to very stiff, silty Clay, CL.			D-21 to D-24	11, 8, 10, 18		
3.45m	Light Gray 7.5YR (7/1), dense to very dense, fine Sand, SM.			D-25, D-26	41, 50		

Over

LEGEND FOR BORELOG AND GRAIN SIZE DISTRIBUTION (BASED ON 'ASTM CLASSIFICATION D-2487')

PLASTIC CLAY | SILT | PEAT/HIGHLY ORGANIC SOIL | UNDISTURBED SAMPLE

MICACEOUS FINE SAND/SILT | SAND | SHALE | DISTURBED SAMPLE

N- BLOWS DELIVERED PER FOOT BY A 140 LB HAMMER FALLING 30 INCHES

MAX^{m} PENETRATION= 50 BLOWS. AFTER 50 BLOWS PENETRATION DEPTH WERE MEASURED