
A2 PROSOIL	BOREHOLE NO: BH-01	
	LOCATION : BGB Rajshahi.	
PROJECT : Proposed 6 Storied Sainik Barrack at Border Guard Battalion, Rajshahi.	DEPTH OF BORING : 18.0m	**R. L. : 10.125m**
CLIENT : Sheltech Engineering Ltd.	DATE OF BORING : 11-03-2019	B. W. T : 1.75m below from E. G. L.

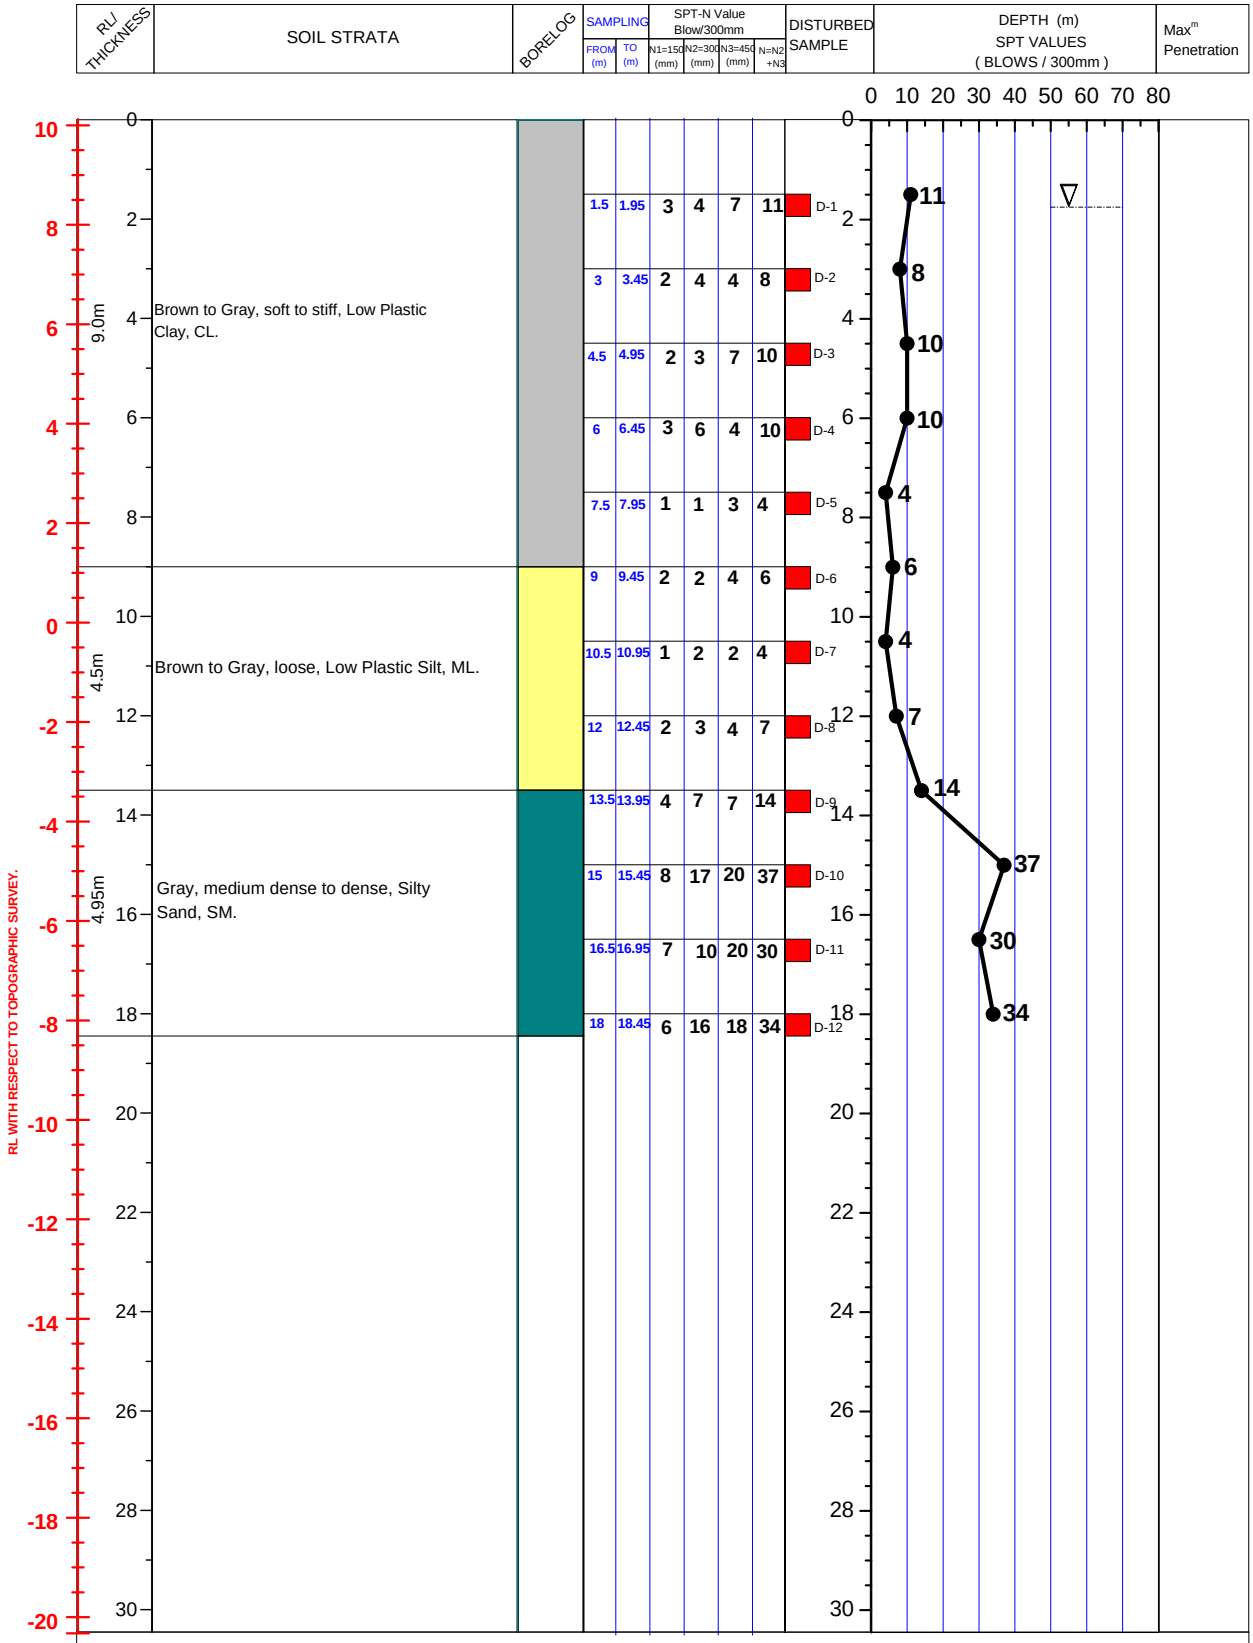

LEGEND FOR BORELOG AND GRAIN SIZE DISTRIBUTION (BASED ON 'ASTM CLASSIFICATION D-2487')

PLASTIC CLAY	SILT	PEAT/HIGHLY ORGANIC SOIL	UNDISTURBED SAMPLE
MICACEOUS FINE SAND/SILT	SAND	SHALE	DISTURBED SAMPLE

N- BLOWS DELIVERED PER FOOT BY A 140 LB HAMMER FALLING 30 INCHES

MAX^{m} PENETRATION= 50 BLOWS. AFTER 50 BLOWS PENETRATION DEPTH WERE MEASURED