A2	PROSOIL	BOREHOLE NO: BH-1	
		LOCATION : 78, Balashpur Bazar, Mymensing.	
PROJECT : AHL SHAHARA RIVER VIEW.		DEPTH OF BORING : 30.0m	R. L.: On Road Level.
CLIENT : Alam Homes Ltd.		DATE OF BORING : 15-04-2011.	G. W. T : 3.66m below from E.G.L.

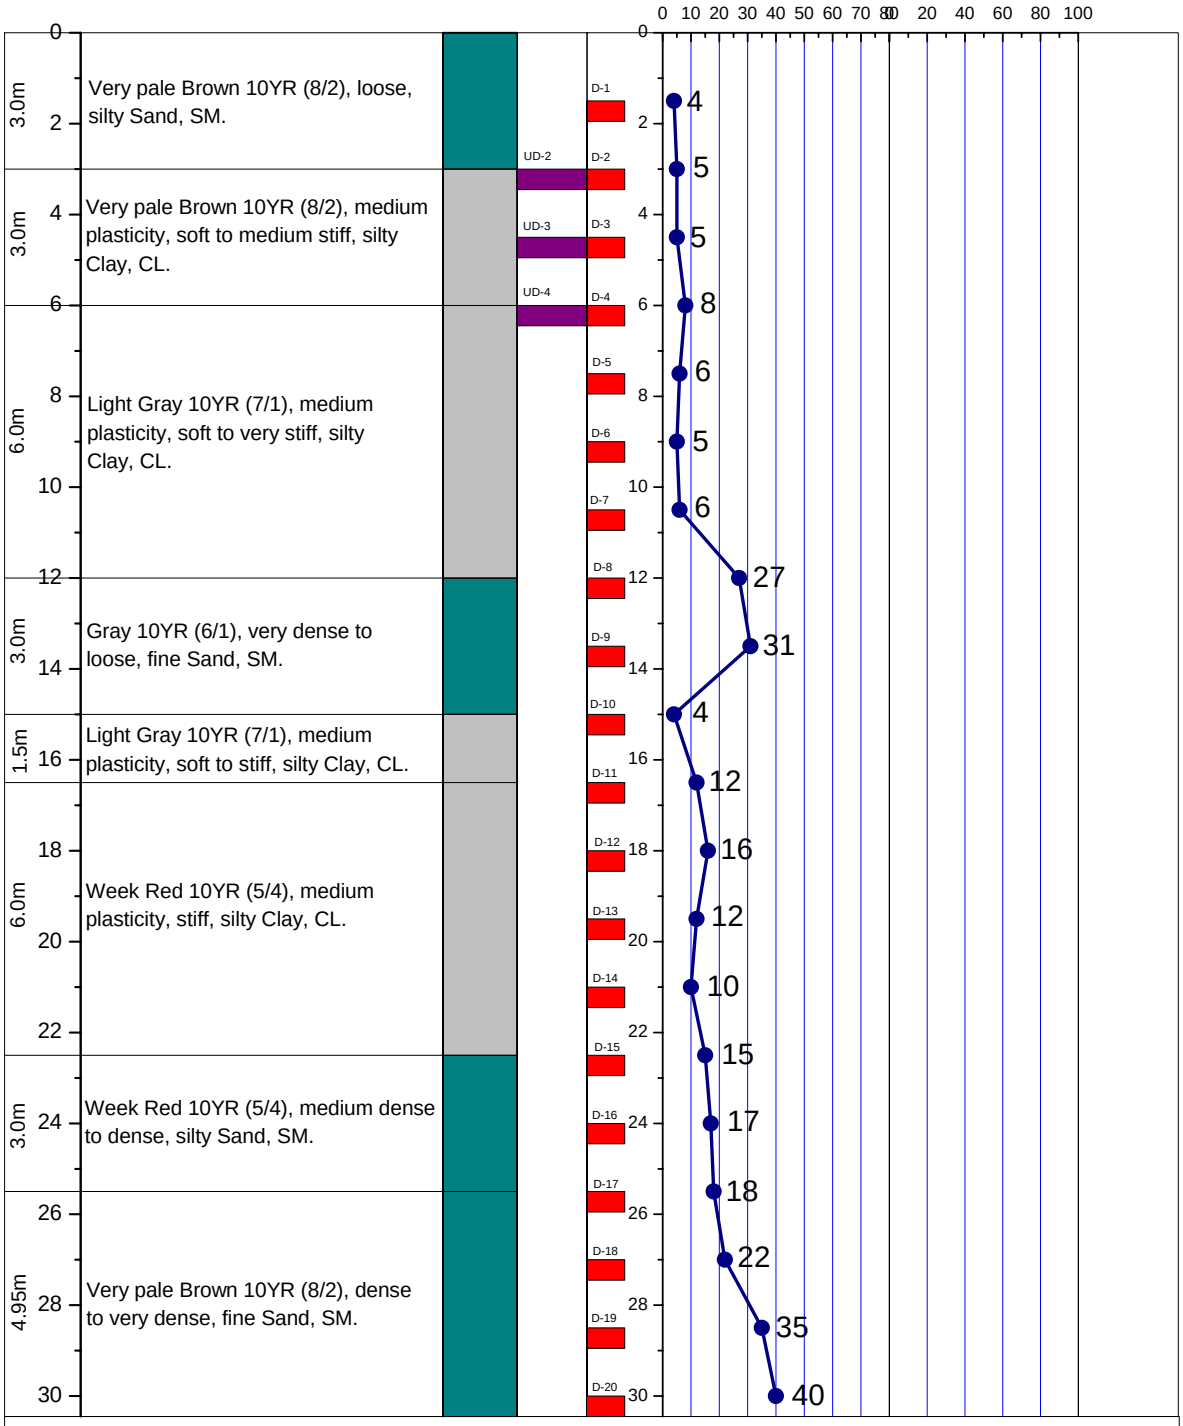

LEGEND FOR BORELOG AND GRAIN SIZE DISTRIBUTION (BASED ON 'ASTM CLASSIFICATION D-2487')

PLASTIC CLAY	SILT	SHALE	UNDISTURBED SAMPLE
MICACEOUS FINE SAND/SILT	SAND	PEAT/HIGHLY ORGANIC SOIL	DISTURBED SAMPLE

N- BLOWS DELIVERED PER FOOT BY A 140 LB HAMMER FALLING 30 INCHES

MAX^{m} PENETRATION= 50 BLOWS
AFTER 50 BLOWS PENETRATION DEPTH WERE MEASURED