A2 PROSOIL	BOREHOLE NO: BH-1	
	LOCATION : Gosninga, Sreepur, Gazipur.	
PROJECT : Telecommunication Tower.	DEPTH OF BORING : 21.0m	R. L.: 0.69m below from Road Level.
CLIENT : Grameen Phone Ltd.	DATE OF BORING : 20-01-2006	G. W. T : 3.96m below from E.G.L.

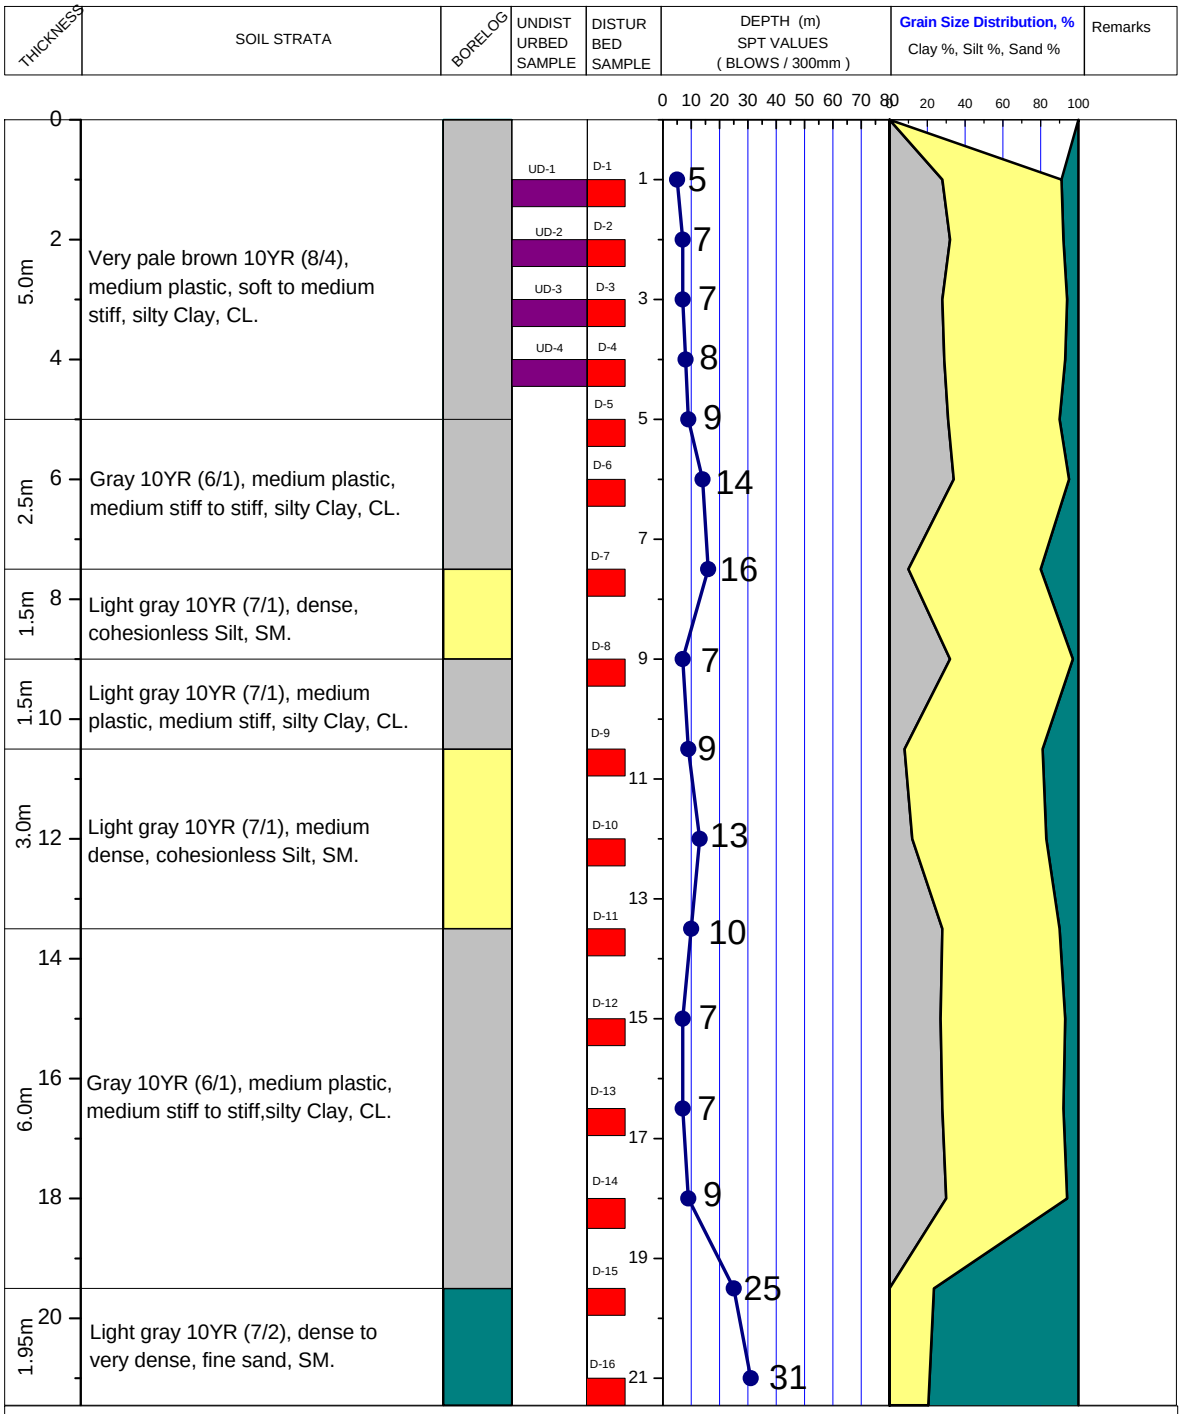

ID FOR BORELOG A RAIN SIZE DISTRIBU

PLASTIC SILTY CLAY

LOW PLASTIC CLAYEY SILT

NON PLASTIC SILT

SAND

UNDISTURBED SAMPLE

ORGANIC

DISTURBED SAMPLE

N- BLOWS DELIVERED PER FOOT BY A 140 LB HAMMER FALLING 30 INCHES

MAX^{m} PENETRATION= 50 BLOWS

AFTER 50 BLOWS PENETRATION DEPTH WERE MEASURED