A2	Tarique Hasan & Associates Ltd.	BOREHOLE NO: 12	Easting: 691596	Northing: 2849414
		LOCATION : Saidpur Airport, Saidpur, Nilphamari.		
PROJECT : Consultancy Services for Development of Saidpur, Barisal and Osmani International Airport Projects (Design Phase)		DEPTH OF BORING : 18.0m		R. L. : m.
CLIENT : Civil Aviation Authority of Bangladesh.		DATE OF BORING : 18-10-2018		B. W. T : 1.0 m below from E. G. L.

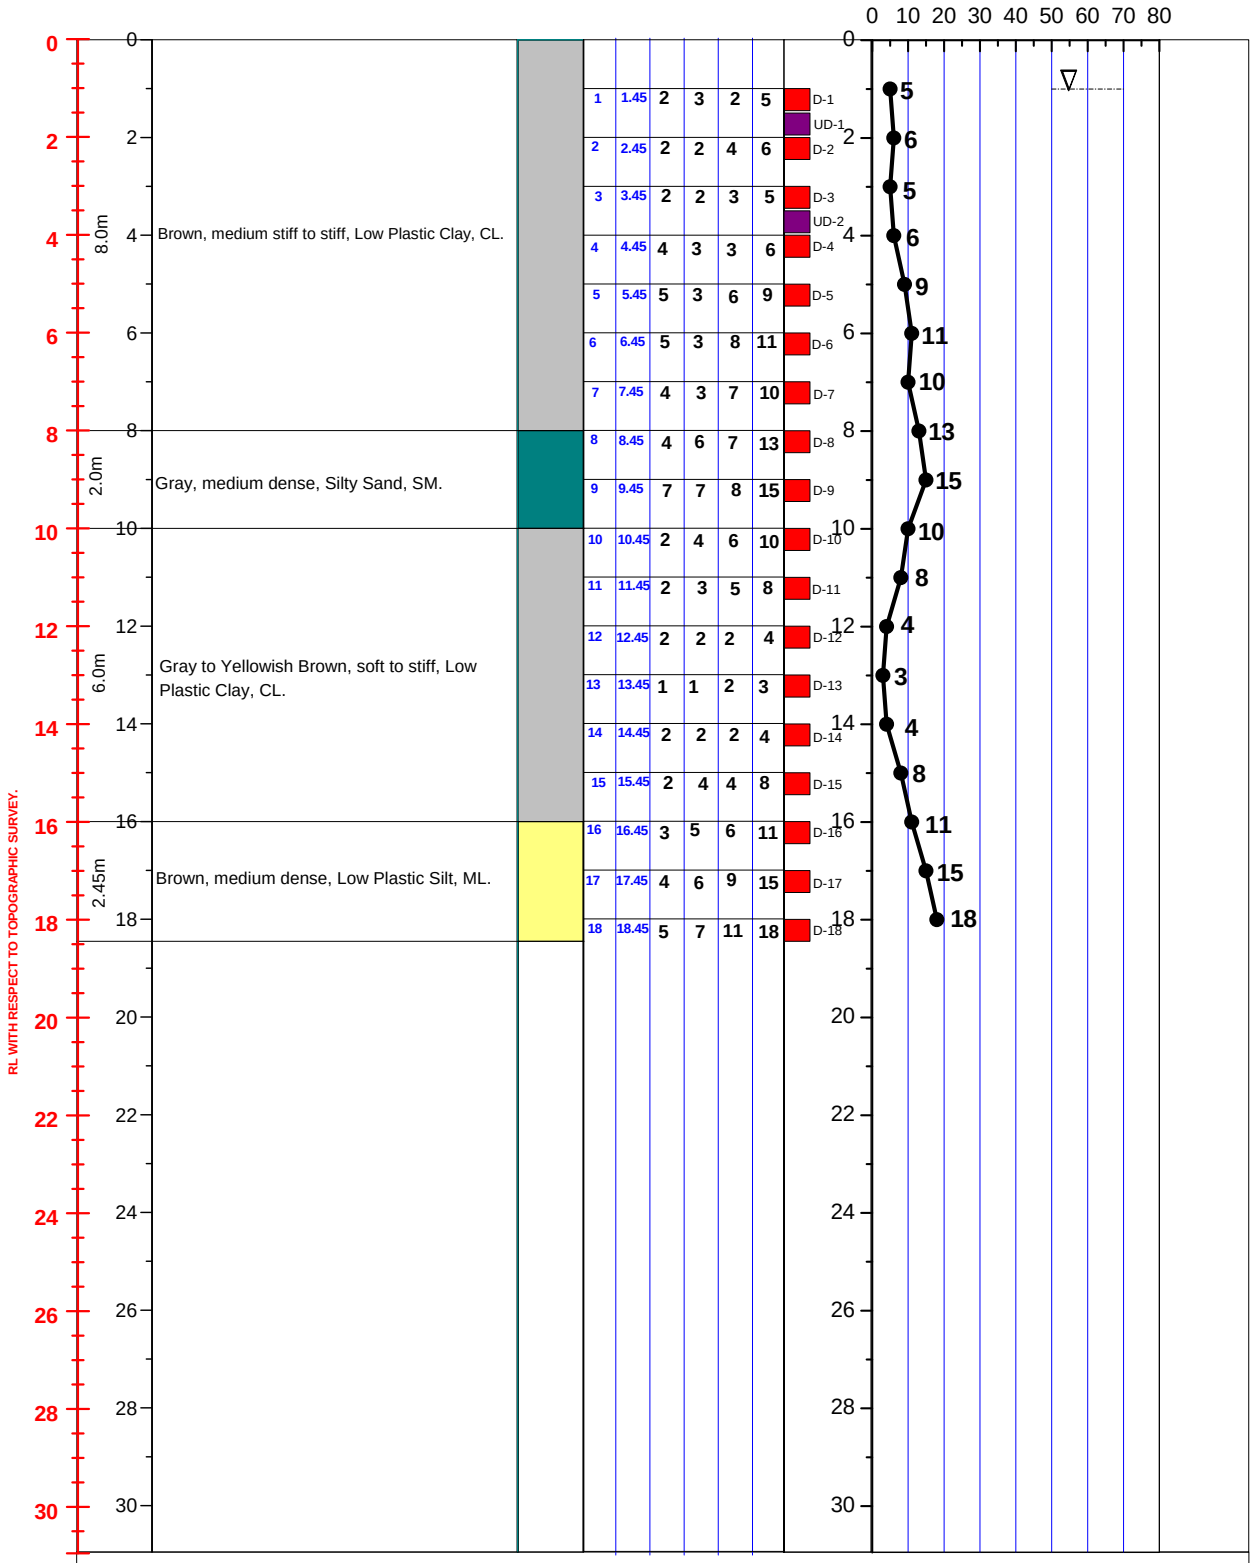

1	1.45	2	3	2	5	D-1
						UD-1
2	2.45	2	2	4	6	D-2
3	3.45	2	2	3	5	D-3
						UD-2
4	4.45	4	3	3	6	D-4
5	5.45	5	3	6	9	D-5
6	6.45	5	3	8	11	D-6
7	7.45	4	3	7	10	D-7
8	8.45	4	6	7	13	D-8
9	9.45	7	7	8	15	D-9
10	10.45	2	4	6	10	D-10
11	11.45	2	3	5	8	D-11
12	12.45	2	2	2	4	D-12
13	13.45	1	1	2	3	D-13
14	14.45	2	2	2	4	D-14
15	15.45	2	4	4	8	D-15
16	16.45	3	5	6	11	D-16
17	17.45	4	6	9	15	D-17
18	18.45	5	7	11	18	D-18

LEGEND FOR BOREHOLE AND GRAIN SIZE DISTRIBUTION (BASED ON 'ASTM CLASSIFICATION D-2487')

PLASTIC CLAY | SILT | PEAT/HIGHLY ORGANIC SOIL | UNDISTURBED SAMPLE

MICACEOUS FINE SAND/SILT | SAND | SHALE | DISTURBED SAMPLE

N- BLOWS DELIVERED PER FOOT BY A 140 LB HAMMER FALLING 30 INCHES

MAX^m PENETRATION= 50 BLOWS. AFTER 50 BLOWS PENETRATION DEPTH WERE MEASURED