A2	PROSOIL	BOREHOLE NO: BH-1	
		LOCATION : Akhaura, Railway Station, B.Baria	
PROJECT : Telecommunication Tower.		DEPTH OF BORING : 25.5m	R. L.: 0.0m from Road Level.
CLIENT : Grameen Phone Ltd.		DATE OF BORING : 02-06-2005	G. W. T : 3.20m below from E. G. L.

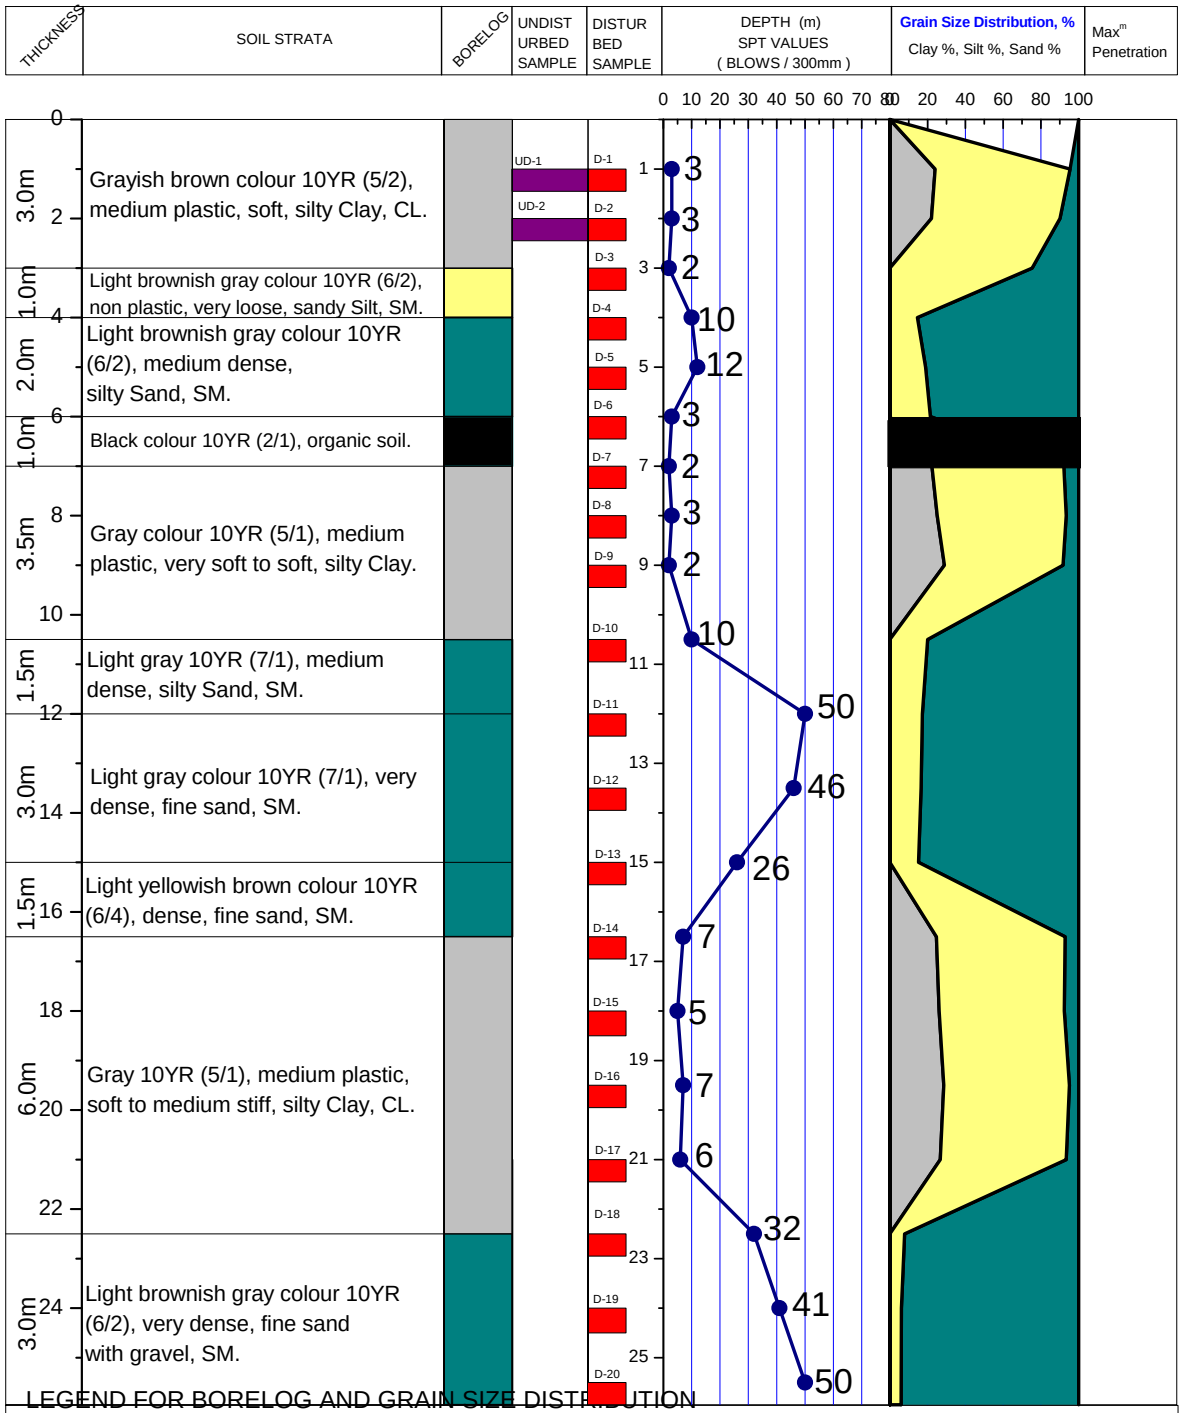

LEGEND FOR BORELOG AND GRAIN SIZE DISTRIBUTION

PLASTIC SILTY CLAY

LOW PLASTIC CLAYEY SILT

NON PLASTIC SILT

SAND

ORGANIC

UNDISTURBED SAMPLE

DISTURBED SAMPLE

N- BLOWS DELIVERED PER FOOT BY A 140 LB HAMMER FALLING 30 INCHES

MAX^{m} PENETRATION= 50 BLOWS

AFTER 50 BLOWS PENETRATION DEPTH WERE MEASURED