A2 PROSOIL	BOREHOLE NO: BH-1	
	LOCATION : Dhampara Policeline, Chittagong Sadar, Chittagong.	
PROJECT : Telecommunication Tower.	DEPTH OF BORING : 12.0m	R. L.: Road Level.
CLIENT : Bangladesh Police.	DATE OF BORING : 02-11-2008.	G. W. T : 4.57m below from E. G. L.

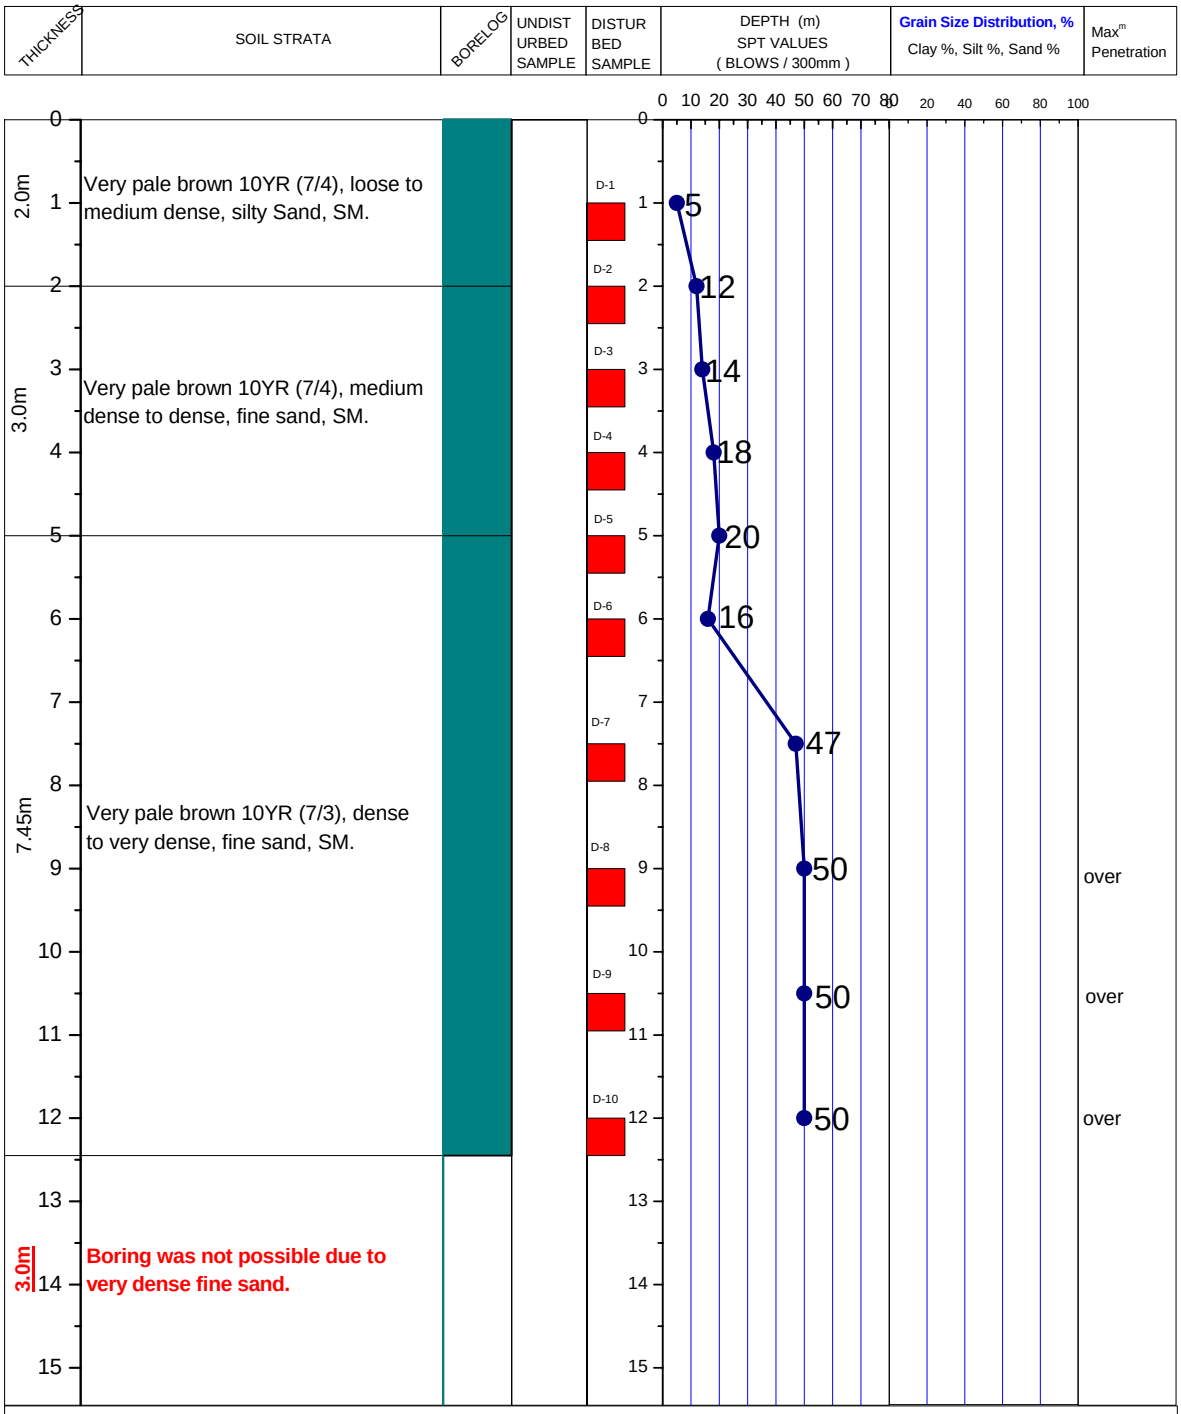

LEGEND FOR BORELOG AND GRAIN SIZE DISTRIBUTION

PLASTIC SILTY CLAY

LOW PLASTIC CLAYEY SILT

NON PLASTIC SILT

SAND

ORGANIC

UNDISTURBED SAMPLE

DISTURBED SAMPLE

SHALE

N- BLOWS DELIVERED PER FOOT BY A 140 LB HAMMER FALLING 30 INCHES

MAX^{m} PENETRATION= 50 BLOWS

AFTER 50 BLOWS PENETRATION DEPTH WERE MEASURED