A2	PROSOIL	BOREHOLE NO: BH-1	
		LOCATION : Zindabazar, Sylhet.	
PROJECT : Al-Hamra Tower(Extension of) (Al-Hamra Shopping City).		DEPTH OF BORING : 22.5m	R. L.: 0.61m below from Road Level.
CLIENT : Zayedur Rahim.		DATE OF BORING: 22-11-2011.	G. W. T : 1.52m below from E.G.L.

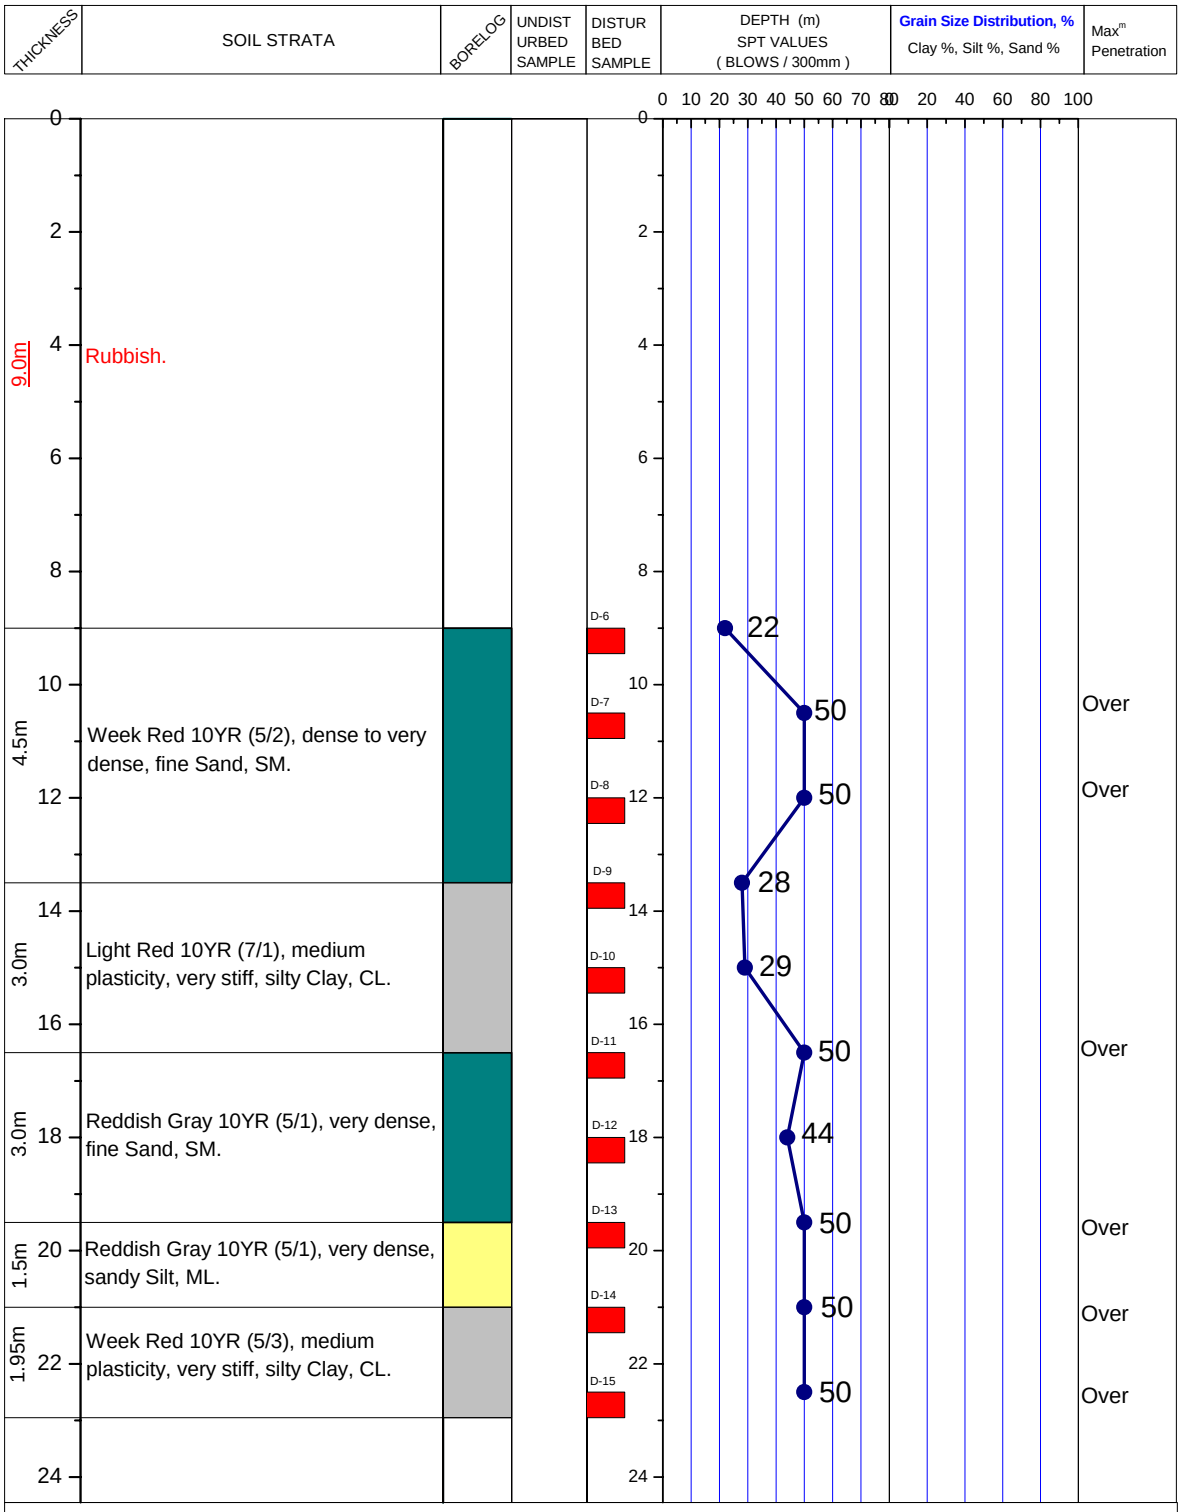

LEGEND FOR BORELOG AND GRAIN SIZE DISTRIBUTION (BASED ON 'ASTM CLASSIFICATION D-2487')

PLASTIC CLAY	SILT	SHALE	UNDISTURBED SAMPLE
MICACEOUS FINE SAND/SILT	SAND	PEAT/HIGHLY ORGANIC SOIL	DISTURBED SAMPLE

N- BLOWS DELIVERED PER FOOT BY A 140 LB HAMMER FALLING 30 INCHES

MAX^m PENETRATION= 50 BLOWS
AFTER 50 BLOWS PENETRATION DEPTH WERE MEASURED