
A2	PROSOIL	BOREHOLE NO: BH-1	
		LOCATION : Baharpur, Mirsharai, Chittagong.	
PROJECT : Telecommunication Tower.		DEPTH OF BORING : 51.0m	R. L.: 0.91m below from Road Level.
CLIENT : AXIATA (Bangladesh) Ltd.		DATE OF BORING : 23-06-2010.	G. W. T : 0.31m below from E. G. L.

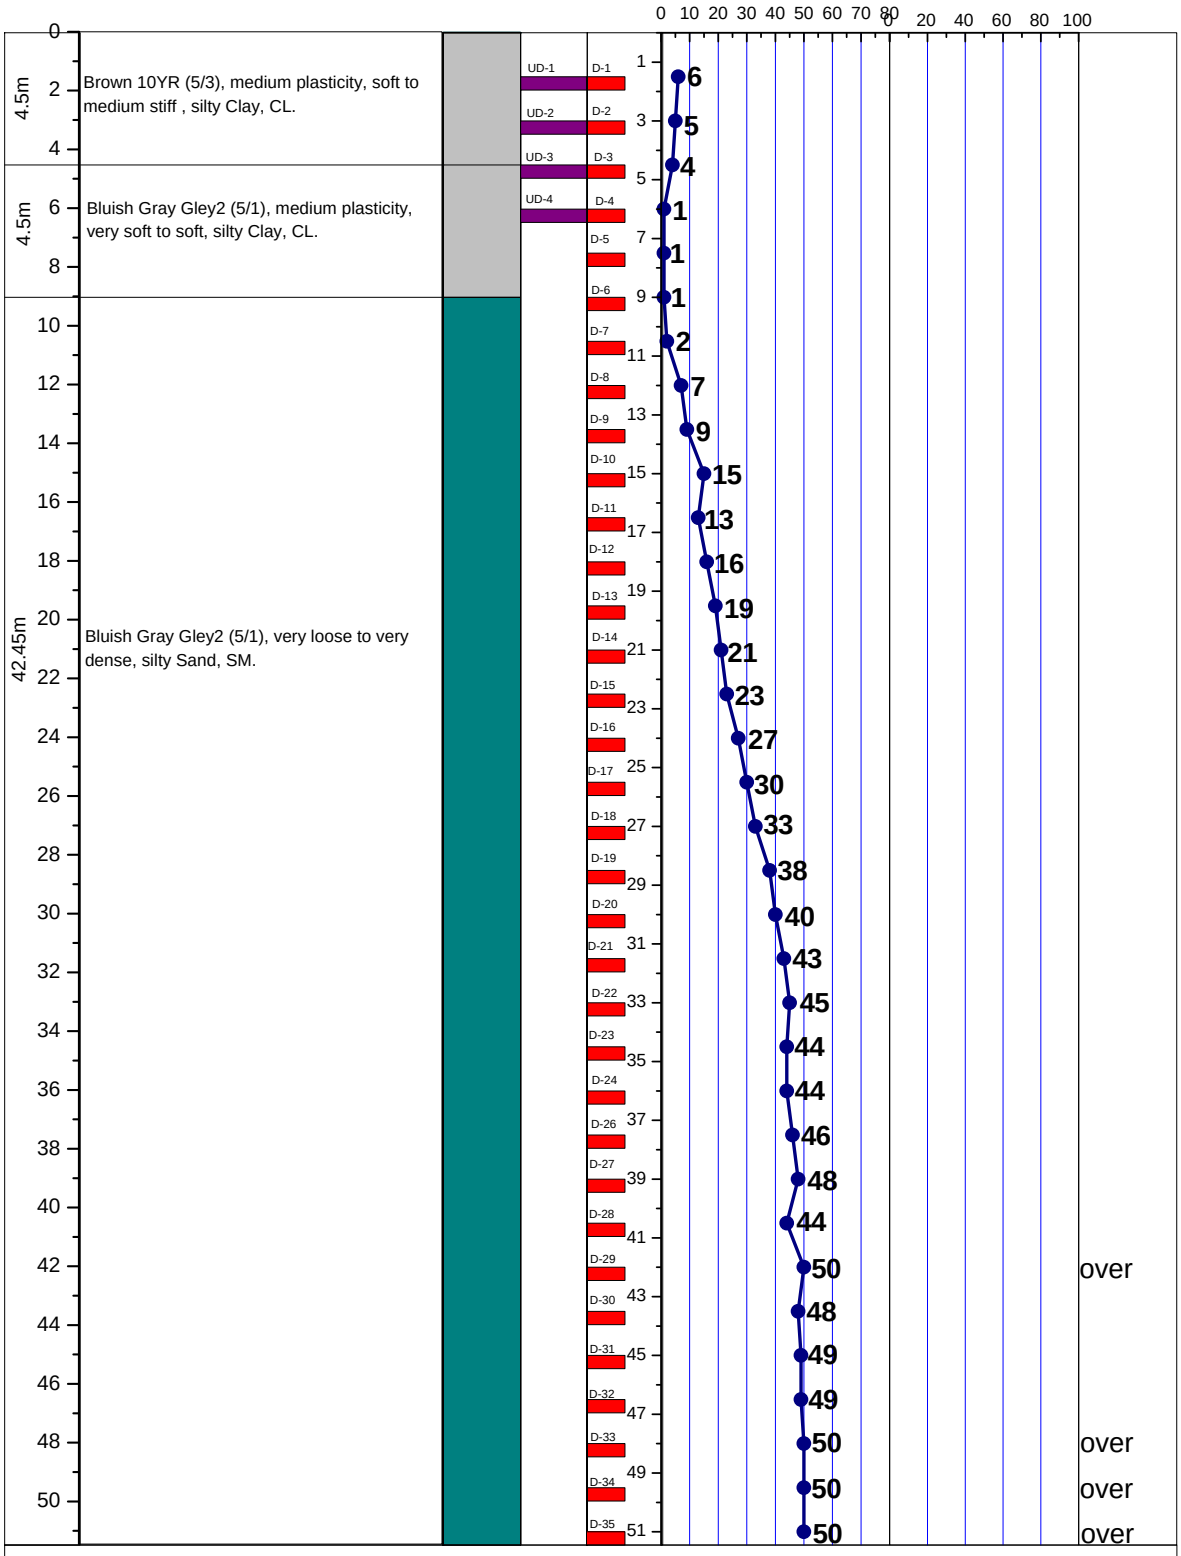


LEGEND FOR BORELOG AND GRAIN SIZE DISTRIBUTION (BASED ON 'ASTM CLASSIFICATION D-2487')

PLASTIC CLAY	SILT	PEAT/HIGHLY ORGANIC SOIL	UNDISTURBED SAMPLE
MICACEOUS FINE SAND/SILT	SAND	SHALE	DISTURBED SAMPLE

N- BLOWS DELIVERED PER FOOT BY A 140 LB HAMMER FALLING 30 INCHES

MAX^{m} PENETRATION= 50 BLOWS. AFTER 50 BLOWS PENETRATION DEPTH WERE MEASURED

A2	PROSOIL	BOREHOLE NO: BH-1	
		LOCATION : Banirhat_GP, Gasua, Banirhat, Sandwip, Chittagong.	
PROJECT : Telecommunication Tower.		DEPTH OF BORING : 51.0m	R. L.: 0.60m below from Road Level.
CLIENT : AXIATA (Bangladesh) Ltd.		DATE OF BORING : 26-11-2011.	G. W. T : 1.83m below from E. G. L.

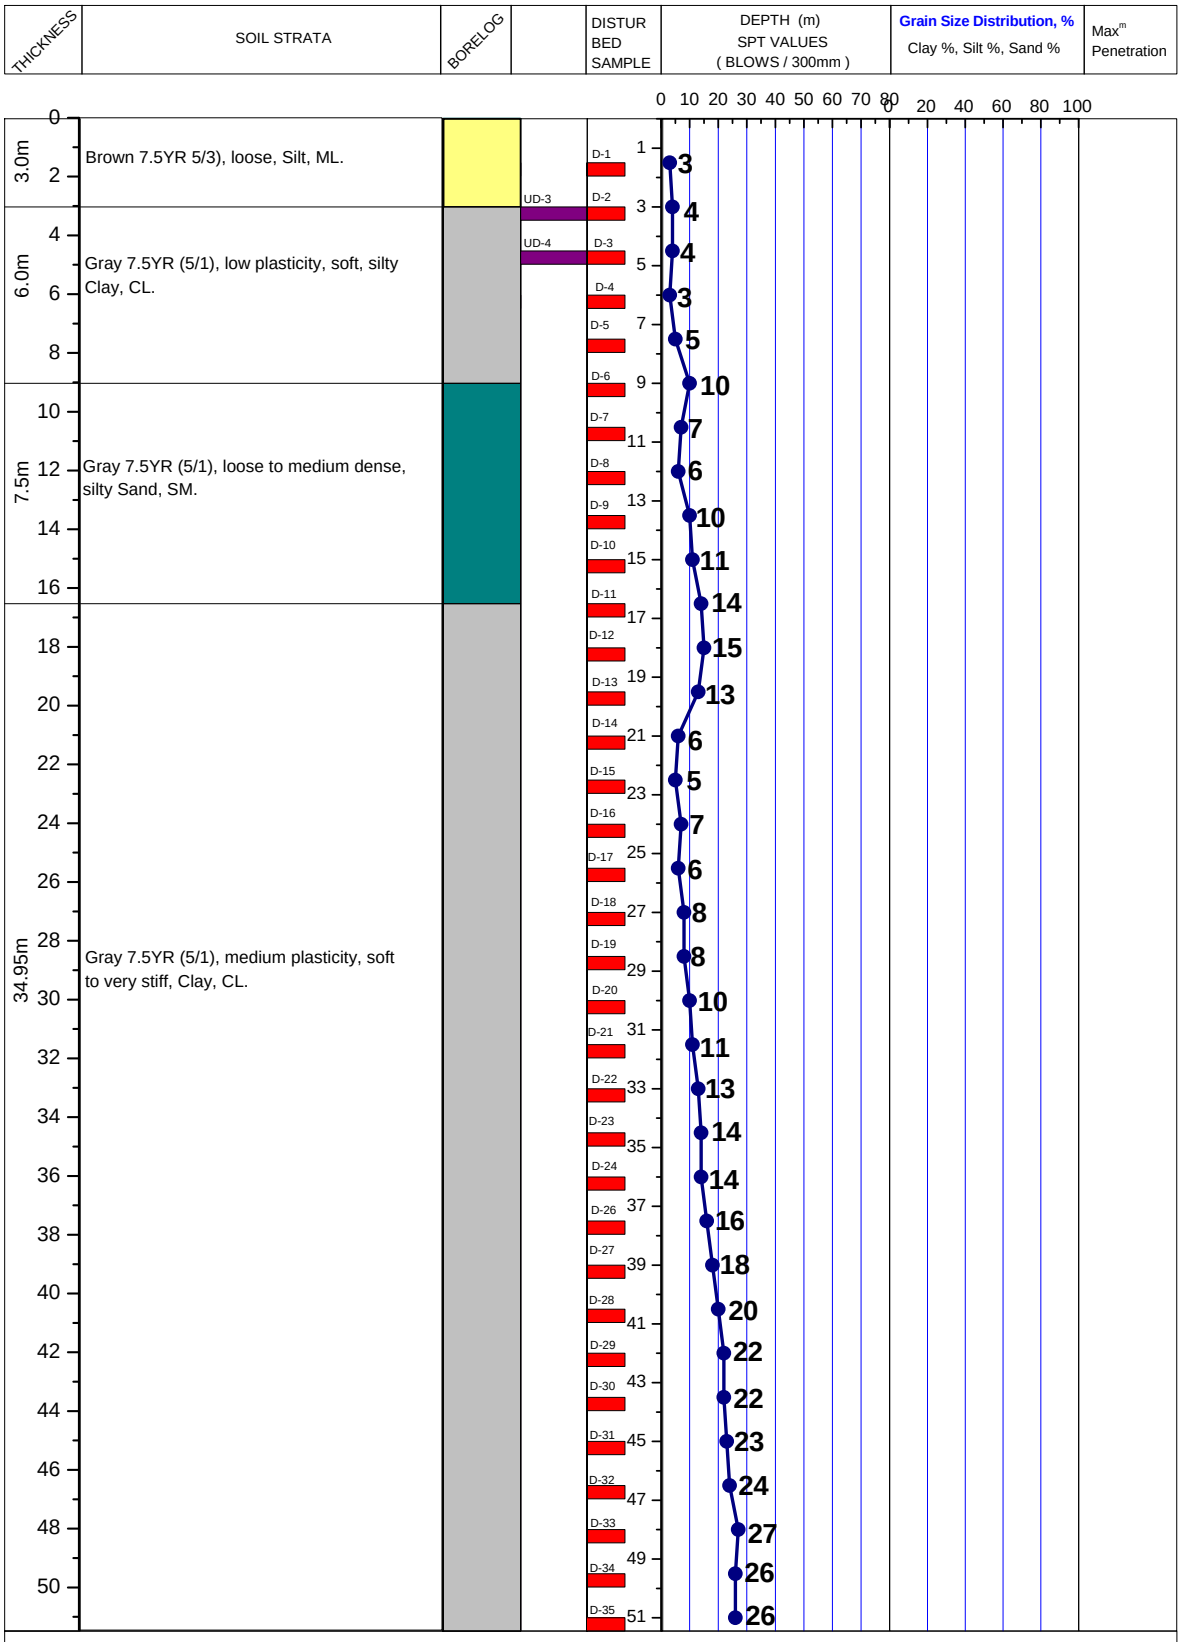


LEGEND FOR BORELOG AND GRAIN SIZE DISTRIBUTION (BASED ON 'ASTM CLASSIFICATION D-2487')

PLASTIC CLAY	SILT	PEAT/HIGHLY ORGANIC SOIL	UNDISTURBED SAMPLE
MICACEOUS FINE SAND/SILT	SAND	SHALE	DISTURBED SAMPLE

N- BLOWS DELIVERED PER FOOT BY A 140 LB HAMMER FALLING 30 INCHES

MAX^{m} PENETRATION= 50 BLOWS. AFTER 50 BLOWS PENETRATION DEPTH WERE MEASURED

A2	PROSOIL	BOREHOLE NO: BH-1	
		LOCATION : Banirhat_GP, Gasua, Banirhat, Sandwip, Chittagong.	
PROJECT : Telecommunication Tower.		DEPTH OF BORING : 51.0m	R. L.: 0.60m below from Road Level.
CLIENT : AXIATA (Bangladesh) Ltd.		DATE OF BORING : 26-11-2011.	G. W. T : 1.83m below from E. G. L.

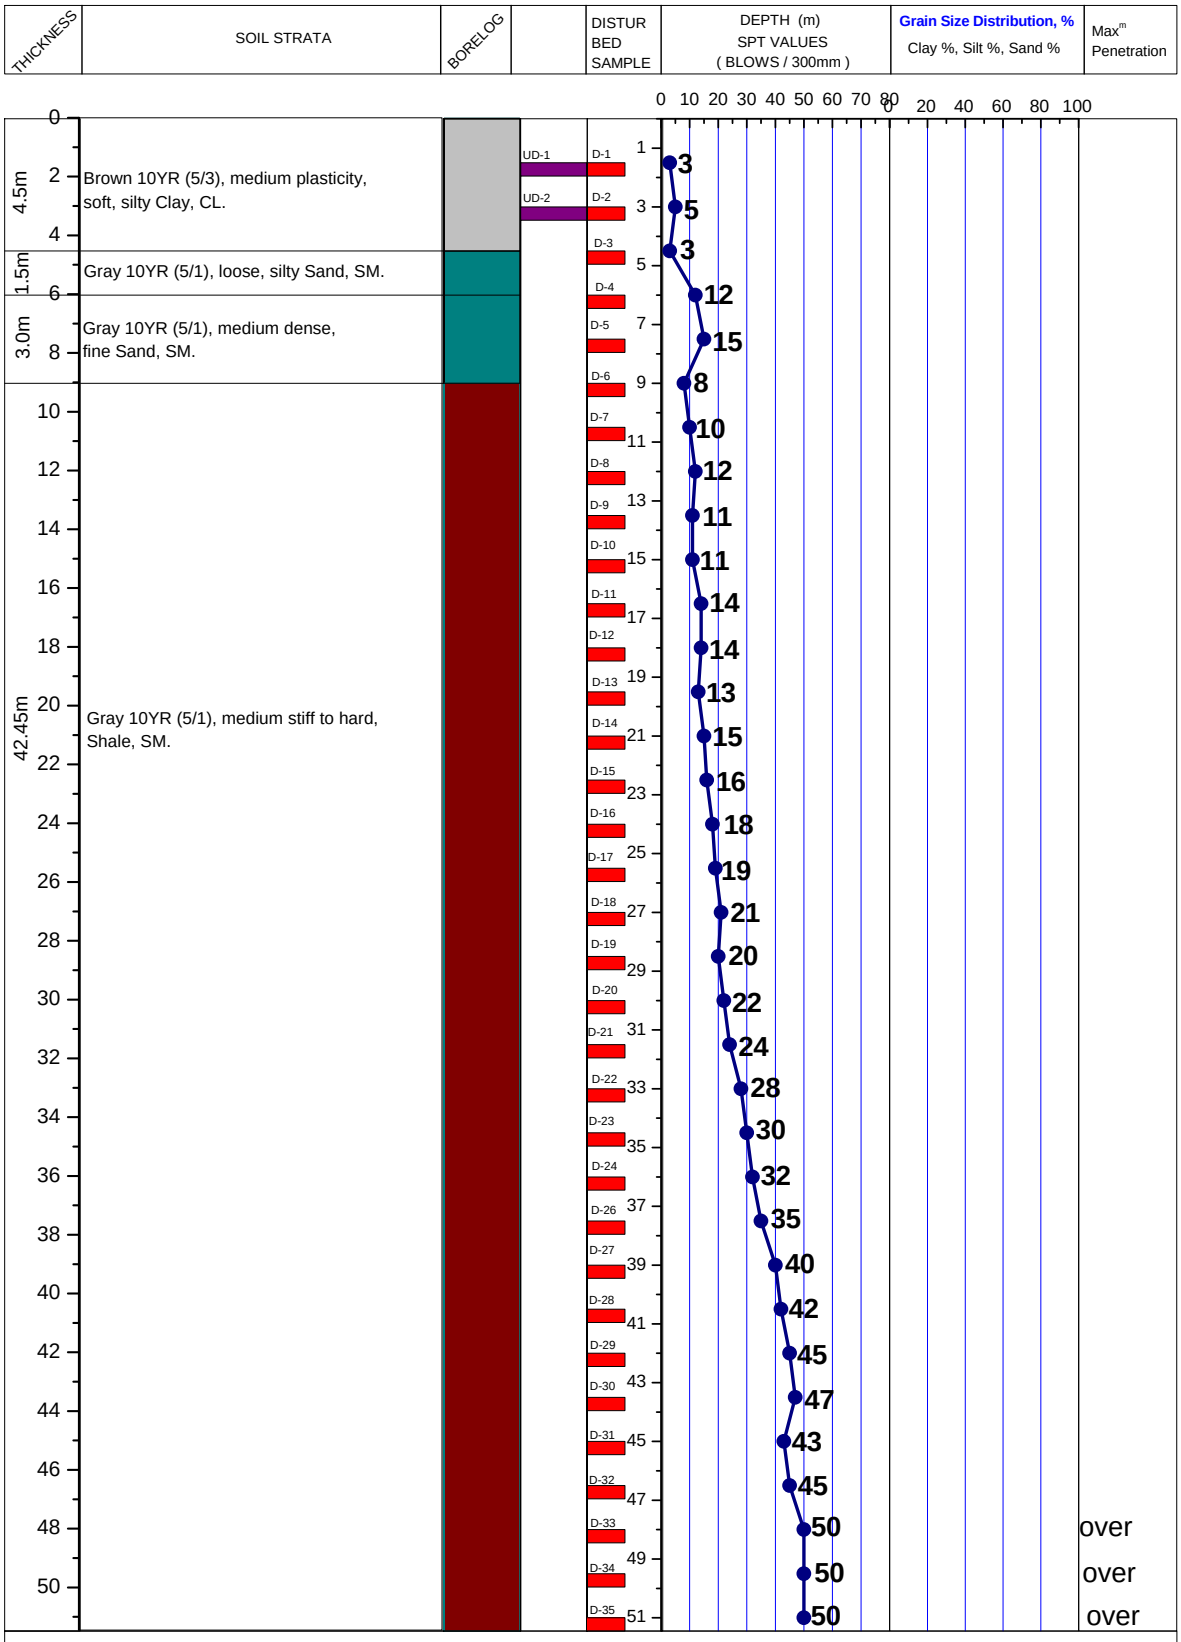

LEGEND FOR BORELOG AND GRAIN SIZE DISTRIBUTION (BASED ON 'ASTM CLASSIFICATION D-2487')

PLASTIC CLAY	SILT	PEAT/HIGHLY ORGANIC SOIL	UNDISTURBED SAMPLE
MICACEOUS FINE SAND/SILT	SAND	SHALE	DISTURBED SAMPLE

N- BLOWS DELIVERED PER FOOT BY A 140 LB HAMMER FALLING 30 INCHES

MAX^{m} PENETRATION= 50 BLOWS. AFTER 50 BLOWS PENETRATION DEPTH WERE MEASURED

A2 PROSOIL	BOREHOLE NO: BH-1	
	LOCATION : Bhujpur, Puran Ramgar, Bagan Bajar, Bhujpur, Fatikchari, Chittagong.	
PROJECT : Telecommunication Tower.	DEPTH OF BORING : 51.0m	R. L.: 0.90m below from Road Level.
CLIENT : AXIATA (Bangladesh) Ltd.	DATE OF BORING : 29-03-2012.	G. W. T : 0.90m below from E. G. L.

THICKNESS	SOIL STRATA	BORELOG	DISTURBED SAMPLE	DEPTH (m) SPT VALUES (BLOWS / 300mm)	Grain Size Distribution, % Clay %, Silt %, Sand %	Max^{m} Penetration
3.0m	Reddish Yellow 7.5YR (6/8), very loose, Silt, ML.		D-1 D-2 D-3	1 2 4		
3.0m	Light Brown 7.5YR (6/4), very loose to loose, Silt, ML.		D-4 D-5 D-6	4 5 2		
3.0m	Black 7.5YR (2.5/1), medium plasticity, soft, silty Clay, CL.		D-7 D-8 D-9	1 3 6		
3.0m	Gray 7.5YR (5/1), very loose, silty Sand, SM.		D-10 D-11 D-12	7 7 9		
39.45m	Light Gray 10YR (7/1), loose to very dense, silty Sand, SM.		D-13 D-14 D-15 D-16 D-17 D-18 D-19 D-20 D-21 D-22 D-23 D-24 D-26 D-27 D-28 D-29 D-30 D-31 D-32 D-33 D-34 D-35	11 13 14 14 15 17 17 16 19 21 26 27 28 28 30 33 35 35 37 38 36 40		


LEGEND FOR BORELOG AND GRAIN SIZE DISTRIBUTION (BASED ON 'ASTM CLASSIFICATION D-2487')

PLASTIC CLAY	SILT	PEAT/HIGHLY ORGANIC SOIL	UNDISTURBED SAMPLE
MICACEOUS FINE SAND/SILT	SAND	SHALE	DISTURBED SAMPLE

N- BLOWS DELIVERED PER FOOT BY A 140 LB HAMMER FALLING 30 INCHES

MAX^{m} PENETRATION= 50 BLOWS. AFTER 50 BLOWS PENETRATION DEPTH WERE MEASURED

A2	PROSOIL	BOREHOLE NO: BH-1	
		LOCATION : Dhaloy, Hathajari, Chittagong.	
PROJECT : Telecommunication Tower.		DEPTH OF BORING : 51.0m	R. L.: 0.91m below from Road Level.
CLIENT : TM International, Bangladesh Ltd.		DATE OF BORING : 08-06-2006	G. W. T : 0.10m above from E. G. L.

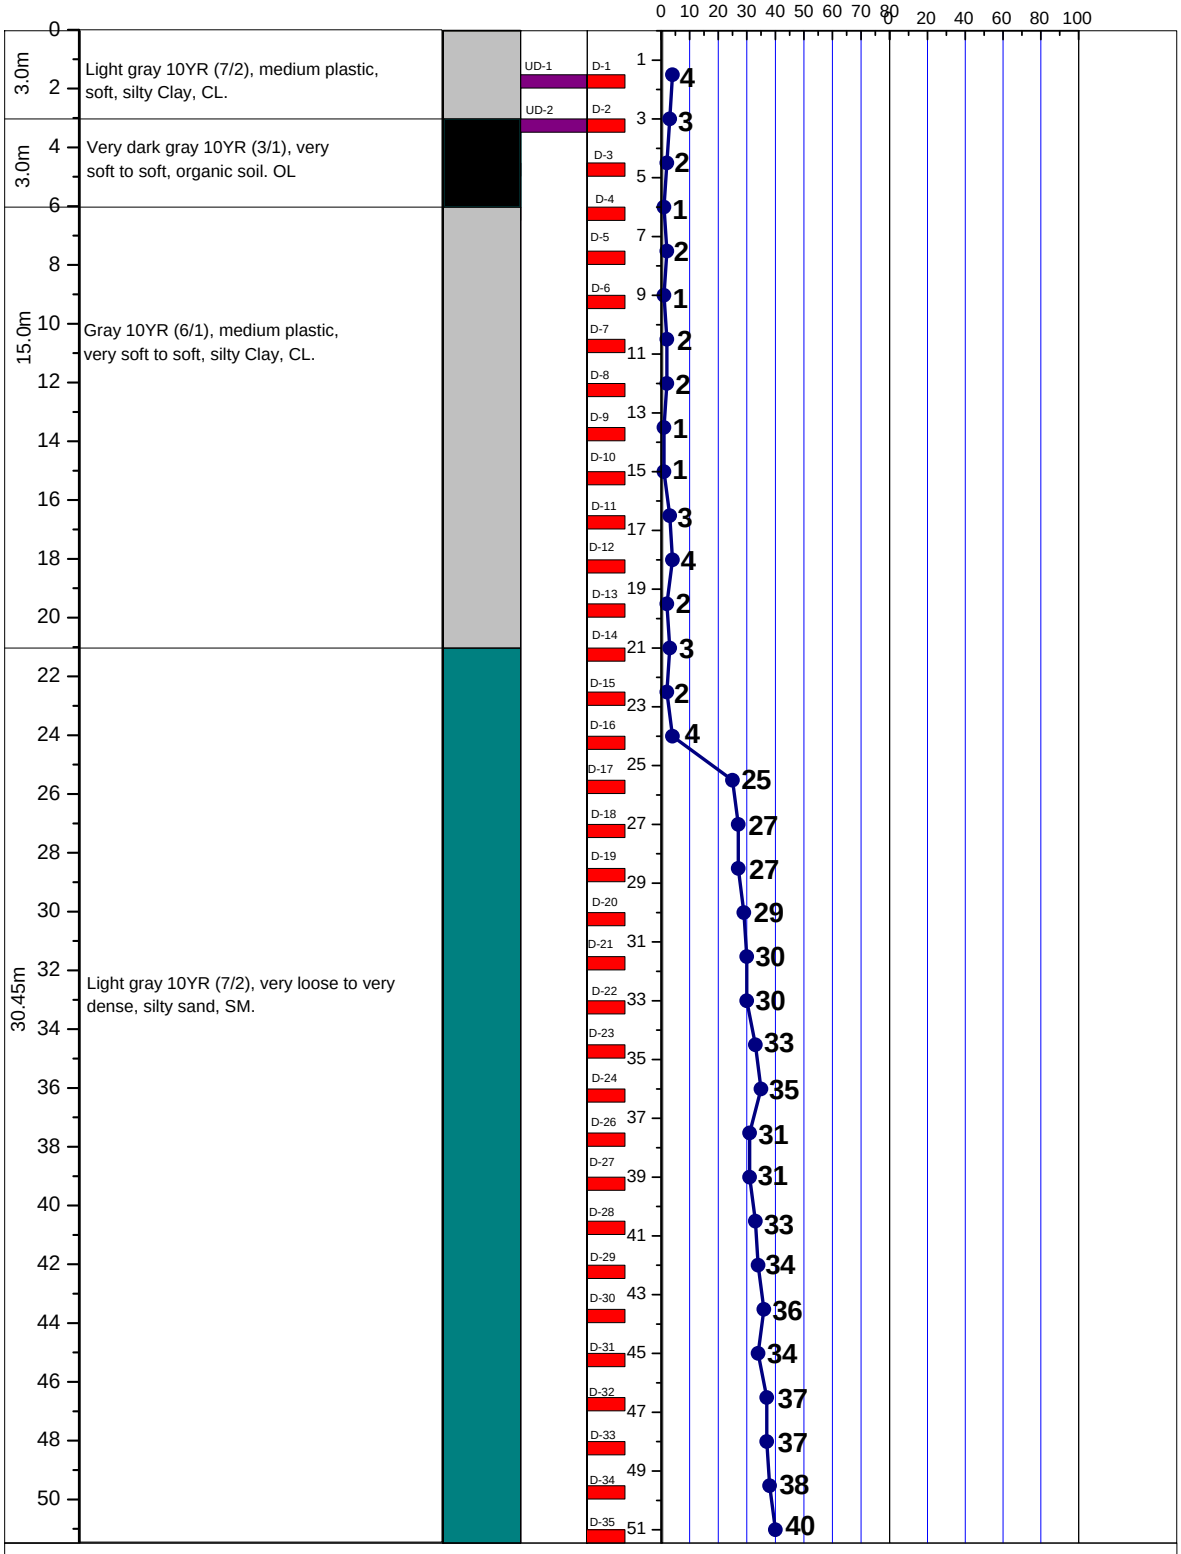


LEGEND FOR BORELOG AND GRAIN SIZE DISTRIBUTION (BASED ON 'ASTM CLASSIFICATION D-2487')

PLASTIC CLAY	SILT	PEAT/HIGHLY ORGANIC SOIL	UNDISTURBED SAMPLE
MICACEOUS FINE SAND/SILT	SAND	SHALE	DISTURBED SAMPLE

N- BLOWS DELIVERED PER FOOT BY A 140 LB HAMMER FALLING 30 INCHES

MAX^{m} PENETRATION= 50 BLOWS. AFTER 50 BLOWS PENETRATION DEPTH WERE MEASURED

A2 PROSOIL	BOREHOLE NO: BH-1	
	LOCATION : Akbar Hat, Sandwip, Chittagong.	
PROJECT : Telecommunication Tower.	DEPTH OF BORING : 51.0m	R. L.: 0.60m below from Road Level.
CLIENT : AXIATA (Bangladesh) Ltd.	DATE OF BORING : 11-10-2009.	G. W. T : 0.69m below from E. G. L.

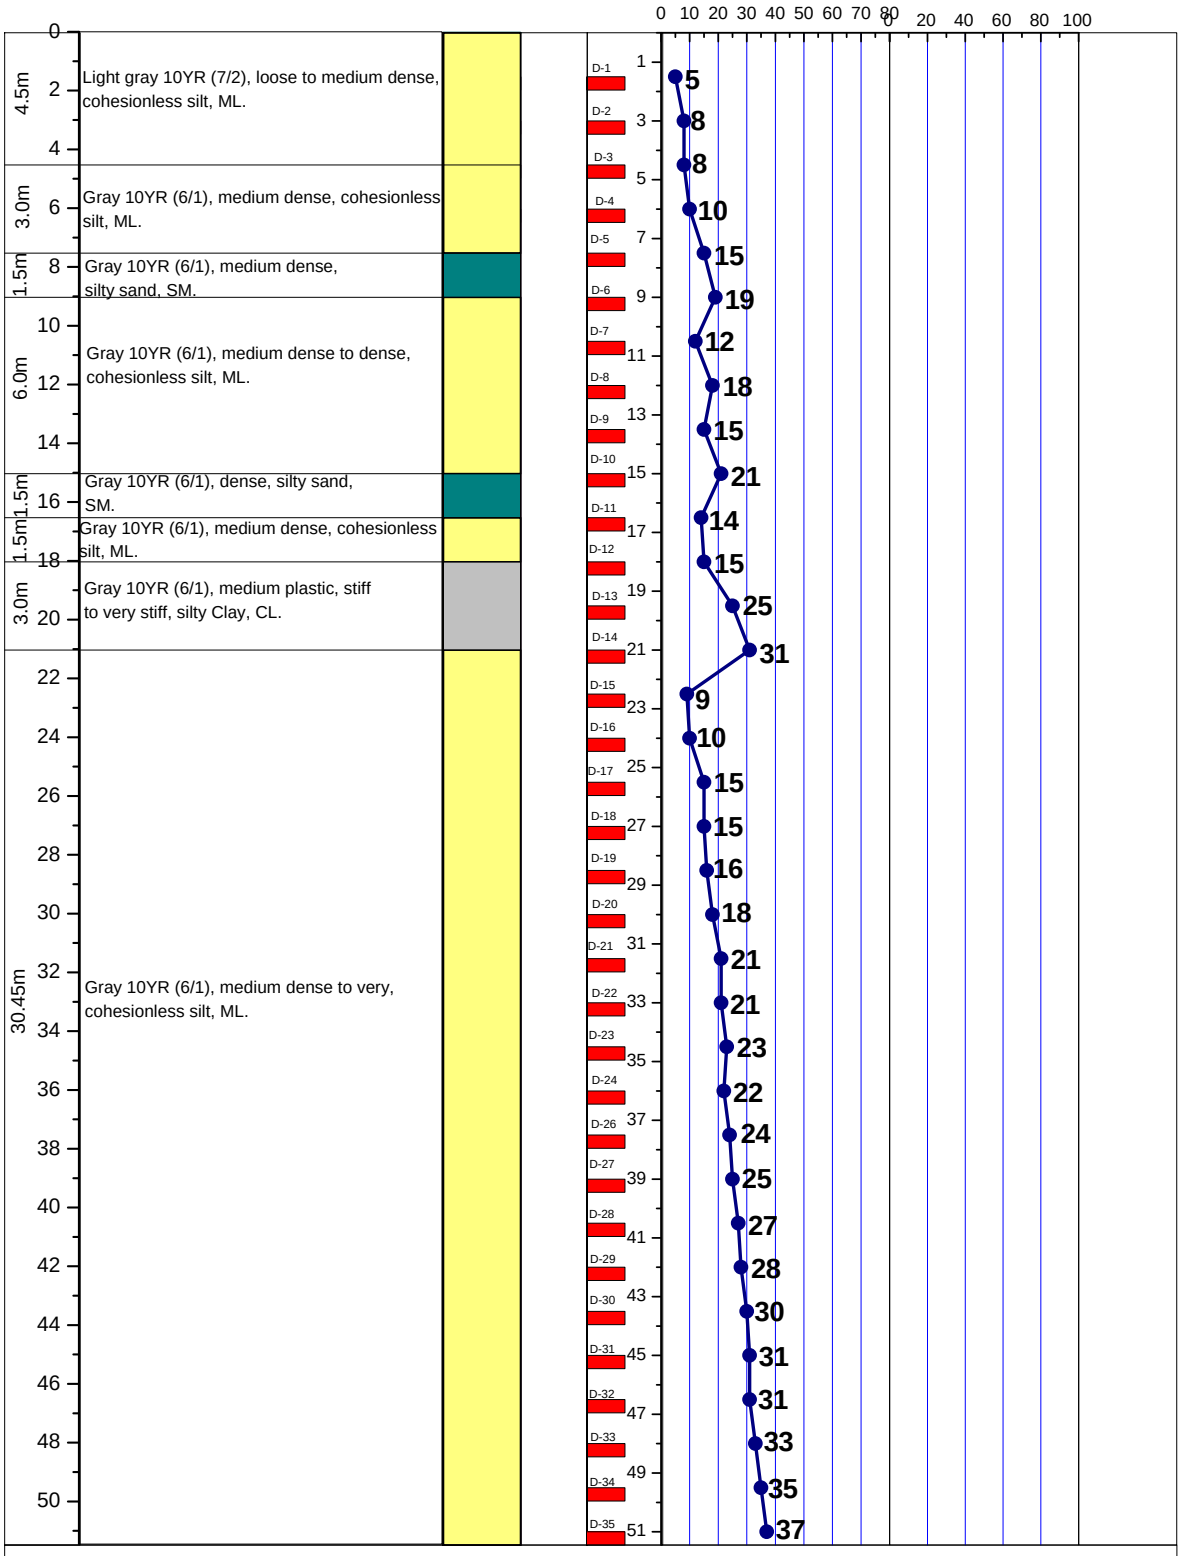


LEGEND FOR BORELOG AND GRAIN SIZE DISTRIBUTION (BASED ON 'ASTM CLASSIFICATION D-2487')

PLASTIC CLAY	SILT	PEAT/HIGHLY ORGANIC SOIL	UNDISTURBED SAMPLE
MICACEOUS FINE SAND/SILT	SAND	SHALE	DISTURBED SAMPLE

N- BLOWS DELIVERED PER FOOT BY A 140 LB HAMMER FALLING 30 INCHES

MAX^{m} PENETRATION= 50 BLOWS. AFTER 50 BLOWS PENETRATION DEPTH WERE MEASURED

A2	PROSOIL	BOREHOLE NO: BH-1	
		LOCATION : Alauddin Market, Mirersharai, Chittagong.	
PROJECT : Telecommunication Tower.		DEPTH OF BORING : 51.0m	R. L.: 1.52m below from Road Level.
CLIENT : AXIATA (Bangladesh) Ltd.		DATE OF BORING : 25-04-2010.	G. W. T : 0.15m below from E. G. L.

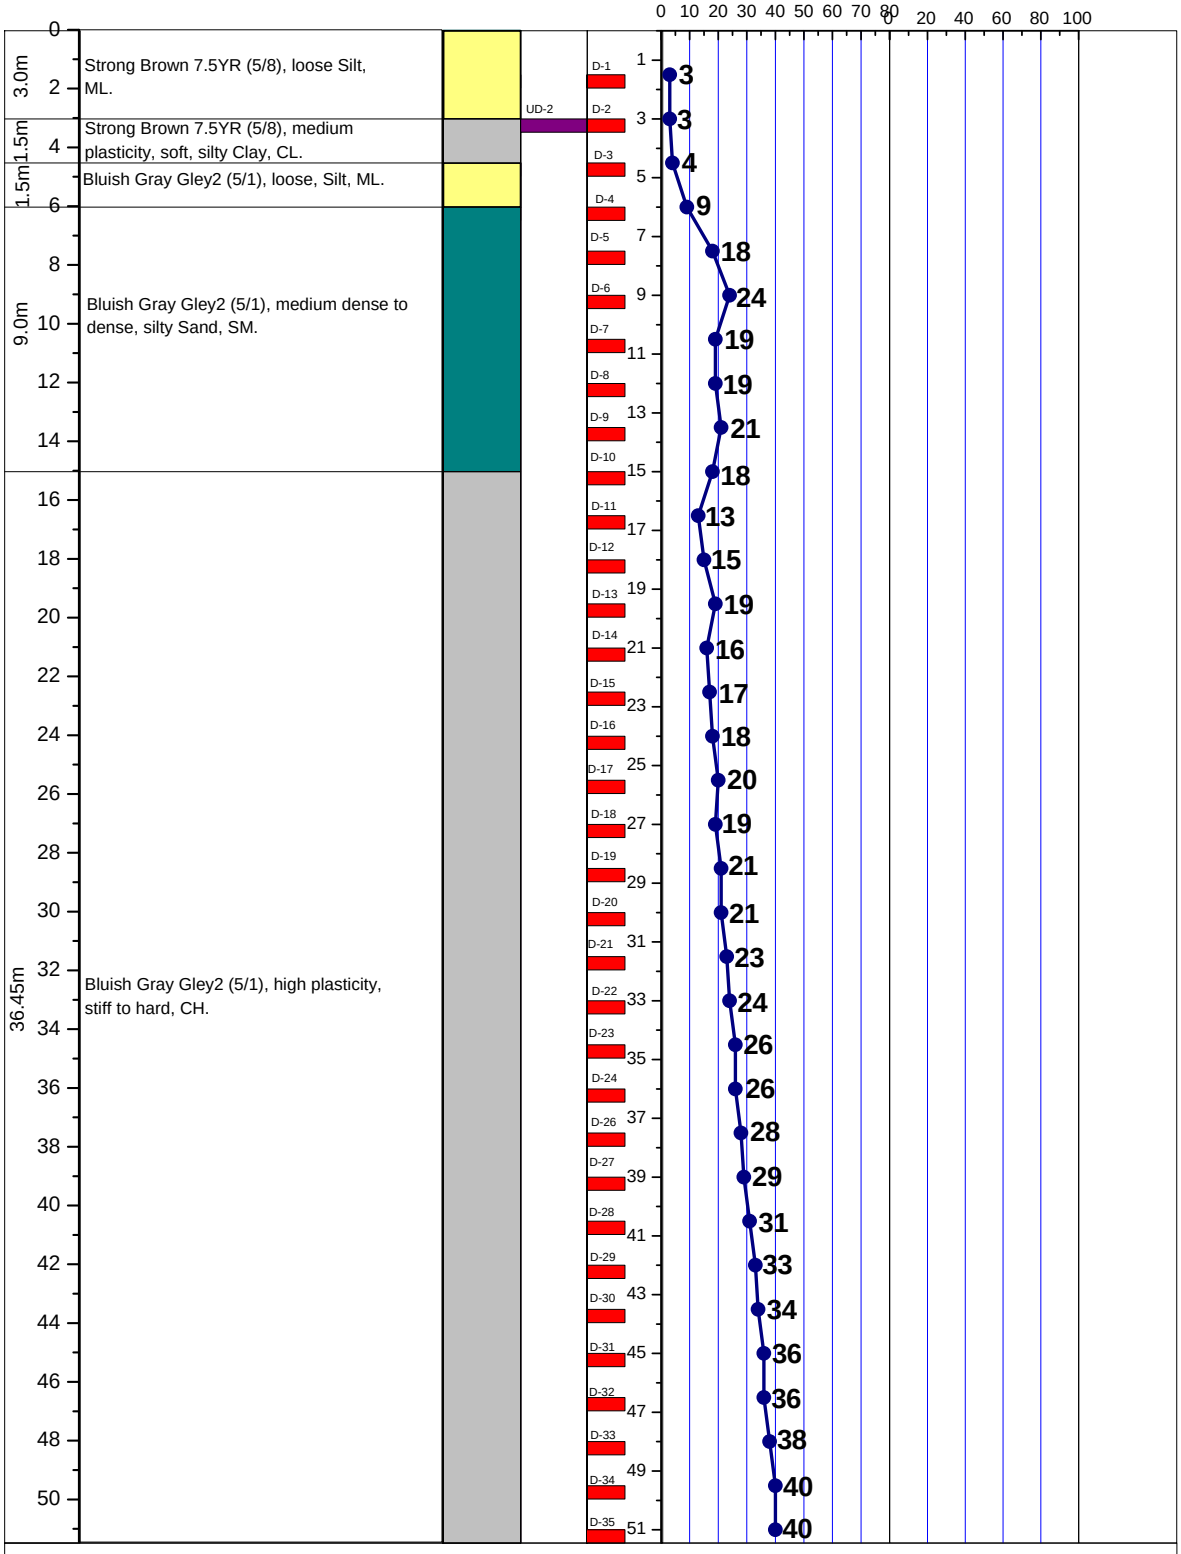


LEGEND FOR BORELOG AND GRAIN SIZE DISTRIBUTION (BASED ON 'ASTM CLASSIFICATION D-2487')

PLASTIC CLAY	SILT	PEAT/HIGHLY ORGANIC SOIL	UNDISTURBED SAMPLE
MICACEOUS FINE SAND/SILT	SAND	SHALE	DISTURBED SAMPLE

N- BLOWS DELIVERED PER FOOT BY A 140 LB HAMMER FALLING 30 INCHES

MAX^{m} PENETRATION= 50 BLOWS. AFTER 50 BLOWS PENETRATION DEPTH WERE MEASURED

A2 PROSOIL	BOREHOLE NO: BH-1	
	LOCATION : Baligaon, Bashkhali.	
PROJECT : Telecommunication Tower.	DEPTH OF BORING : 51.0m	R. L.: 1.83m below from Road Level.
CLIENT : AXIATA (Bangladesh) Ltd.	DATE OF BORING : 28-05-2010.	G. W. T : 0.15m above from E. G. L (Rain Water).

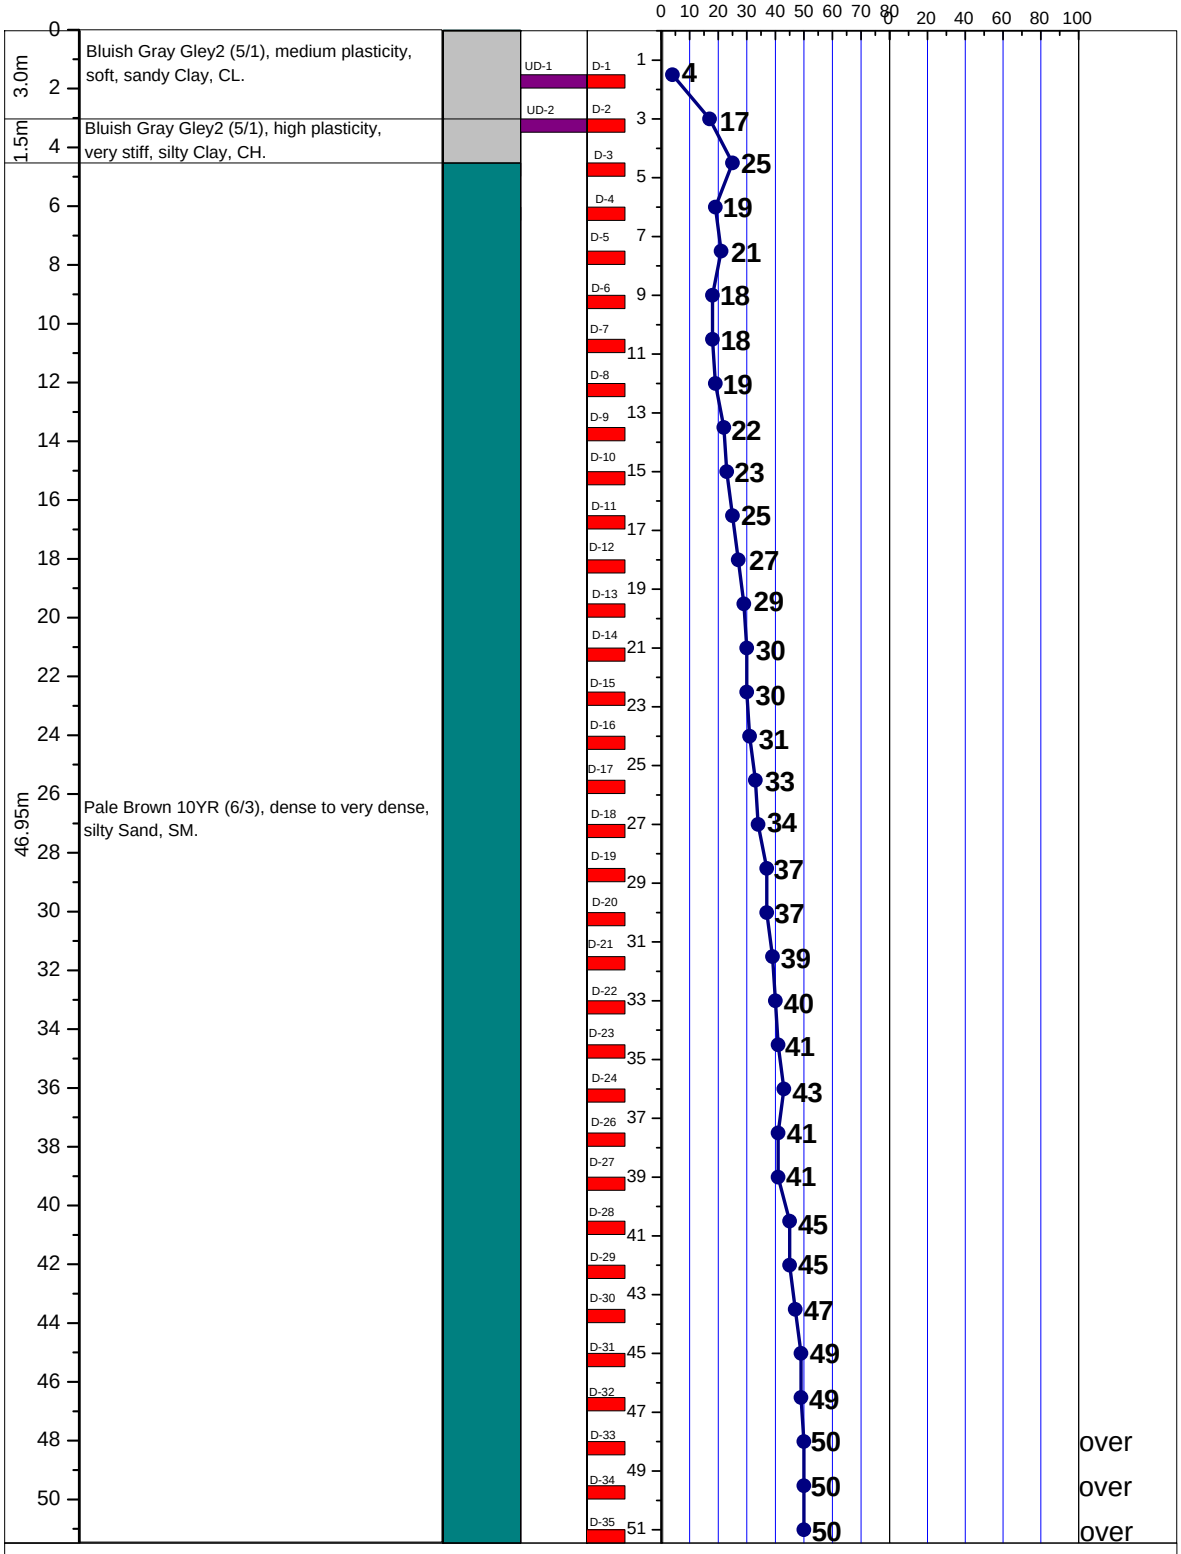


LEGEND FOR BORELOG AND GRAIN SIZE DISTRIBUTION (BASED ON 'ASTM CLASSIFICATION D-2487')

PLASTIC CLAY	SILT	PEAT/HIGHLY ORGANIC SOIL	UNDISTURBED SAMPLE
MICACEOUS FINE SAND/SILT	SAND	SHALE	DISTURBED SAMPLE

N- BLOWS DELIVERED PER FOOT BY A 140 LB HAMMER FALLING 30 INCHES

MAX^{m} PENETRATION= 50 BLOWS. AFTER 50 BLOWS PENETRATION DEPTH WERE MEASURED

A2 PROSOIL	BOREHOLE NO: BH-1	
	LOCATION : Bangabandhu Bazar, Land, Sandwip, Chittagong.	
PROJECT : Telecommunication Tower.	DEPTH OF BORING : 51.0m	R. L.: 0.76m below from Road Level.
CLIENT : AXIATA (Bangladesh) Ltd.	DATE OF BORING : 12-10-2009.	G. W. T : 0.15m above from E. G. L (Rain Water).

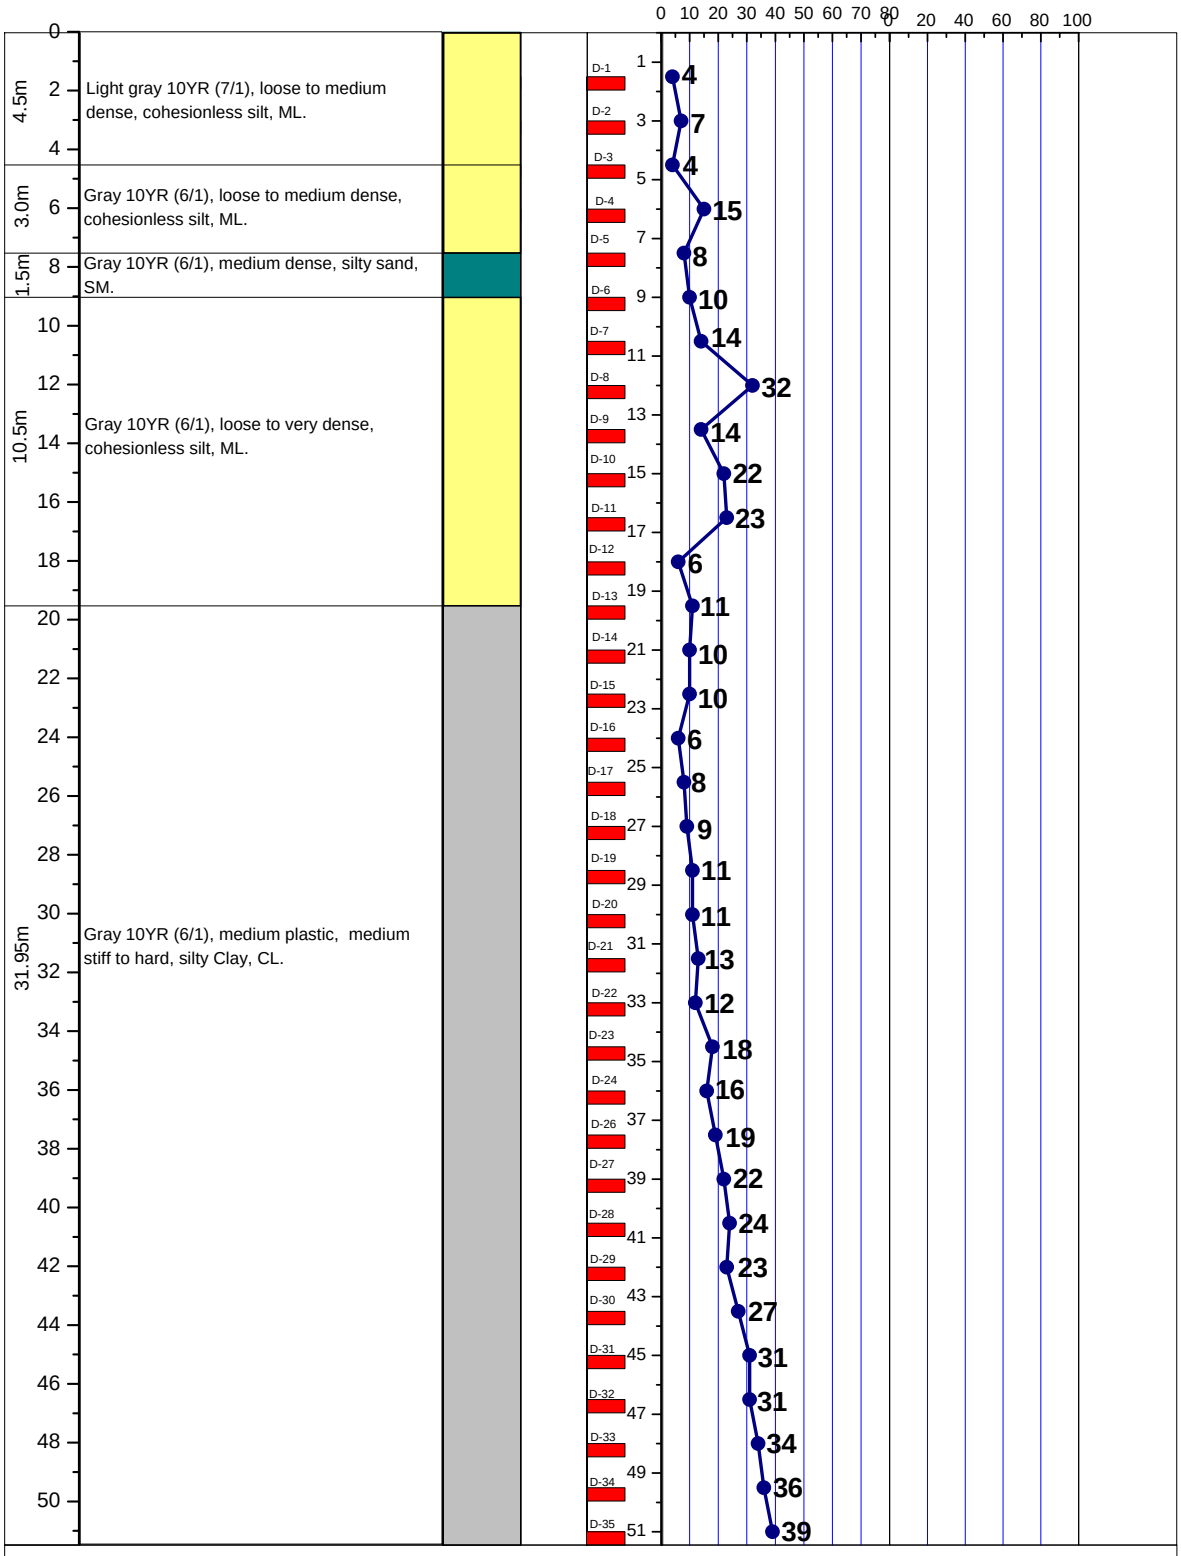


LEGEND FOR BORELOG AND GRAIN SIZE DISTRIBUTION (BASED ON 'ASTM CLASSIFICATION D-2487')

PLASTIC CLAY	SILT	PEAT/HIGHLY ORGANIC SOIL	UNDISTURBED SAMPLE
MICACEOUS FINE SAND/SILT	SAND	SHALE	DISTURBED SAMPLE

N- BLOWS DELIVERED PER FOOT BY A 140 LB HAMMER FALLING 30 INCHES

MAX^{m} PENETRATION= 50 BLOWS. AFTER 50 BLOWS PENETRATION DEPTH WERE MEASURED

A2 PROSOIL	BOREHOLE NO: BH-1	
	LOCATION : Boggon Shah Mazar, Chittagong.	
PROJECT : Telecommunication Tower.	DEPTH OF BORING : 51.0m	R. L.: 0.76m below from Road Level.
CLIENT : AXIATA (Bangladesh) Ltd.	DATE OF BORING : 08-05-2010.	G. W. T : water level was not measured due to paddy field.

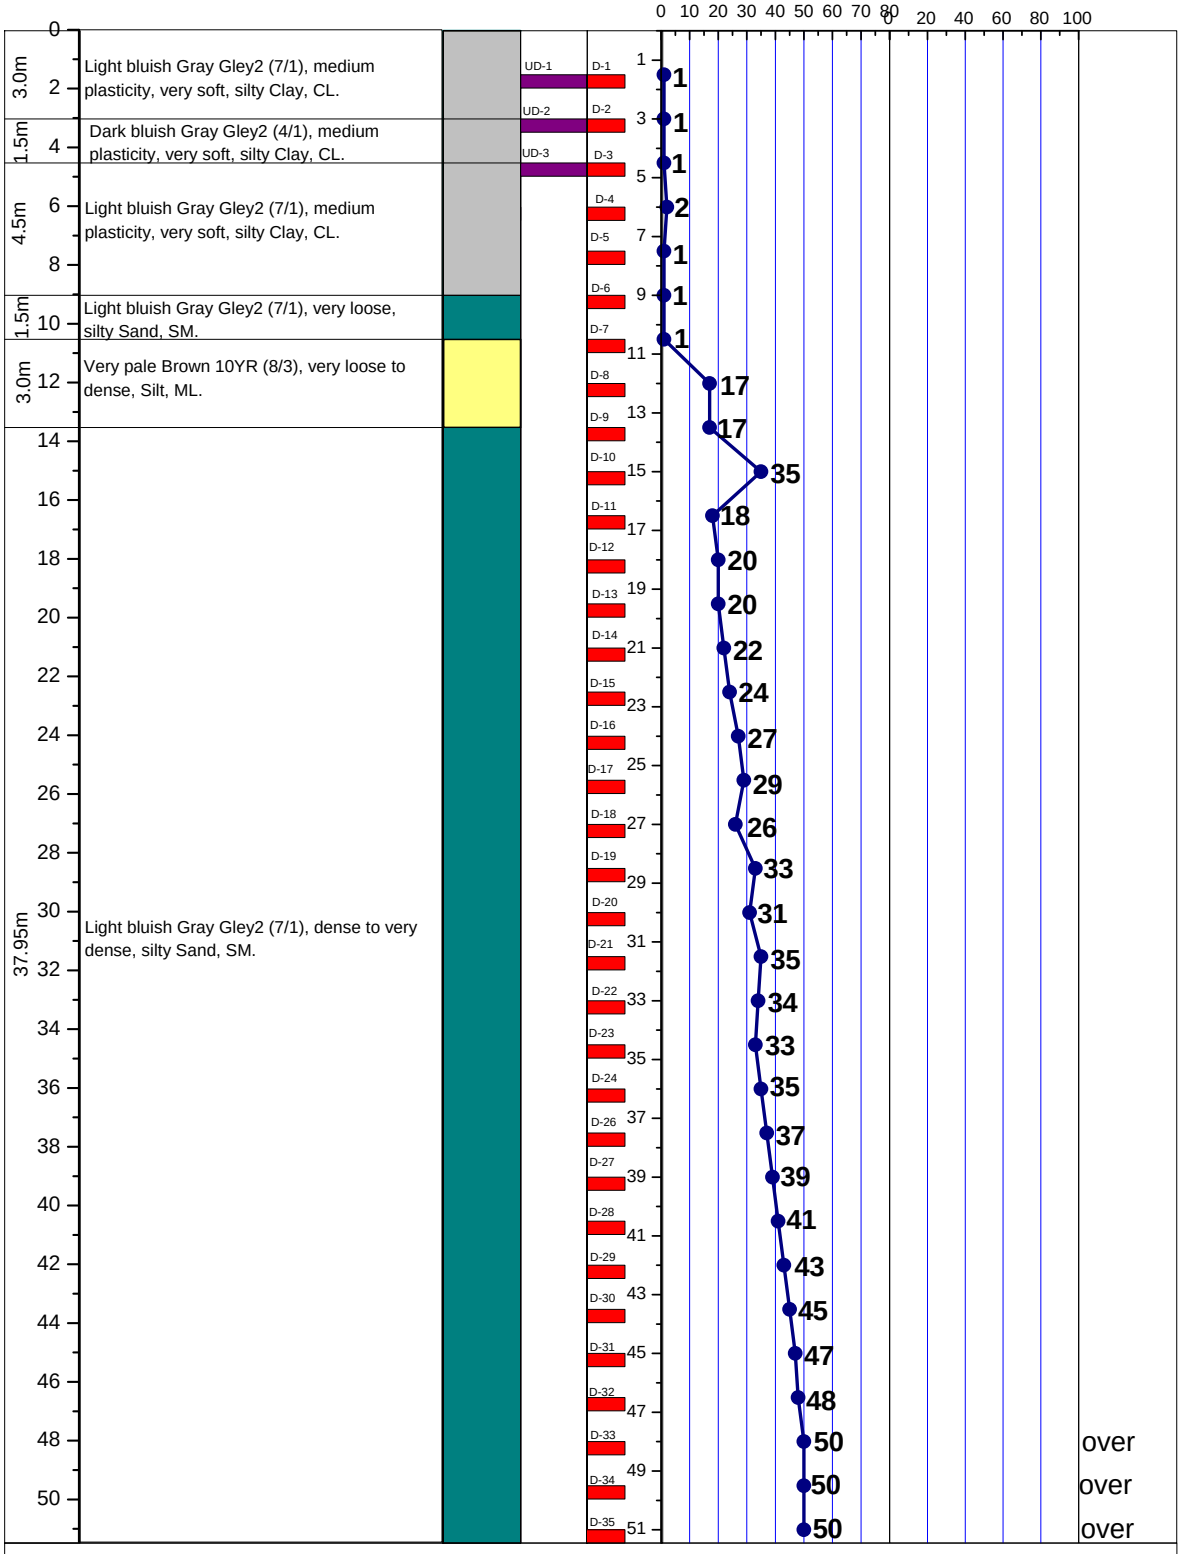


LEGEND FOR BORELOG AND GRAIN SIZE DISTRIBUTION (BASED ON 'ASTM CLASSIFICATION D-2487')

PLASTIC CLAY	SILT	PEAT/HIGHLY ORGANIC SOIL	UNDISTURBED SAMPLE
MICACEOUS FINE SAND/SILT	SAND	SHALE	DISTURBED SAMPLE

N- BLOWS DELIVERED PER FOOT BY A 140 LB HAMMER FALLING 30 INCHES

MAX^{m} PENETRATION= 50 BLOWS. AFTER 50 BLOWS PENETRATION DEPTH WERE MEASURED

A2 PROSOIL	BOREHOLE NO: BH-1	
	LOCATION : Boromashia, Chittagong.	
PROJECT : Telecommunication Tower.	DEPTH OF BORING : 51.0m	R. L.: 1.83m below from Road Level.
CLIENT : AXIATA (Bangladesh) Ltd.	DATE OF BORING : 07-04-2010.	G. W. T : 0.30m below from E. G. L.

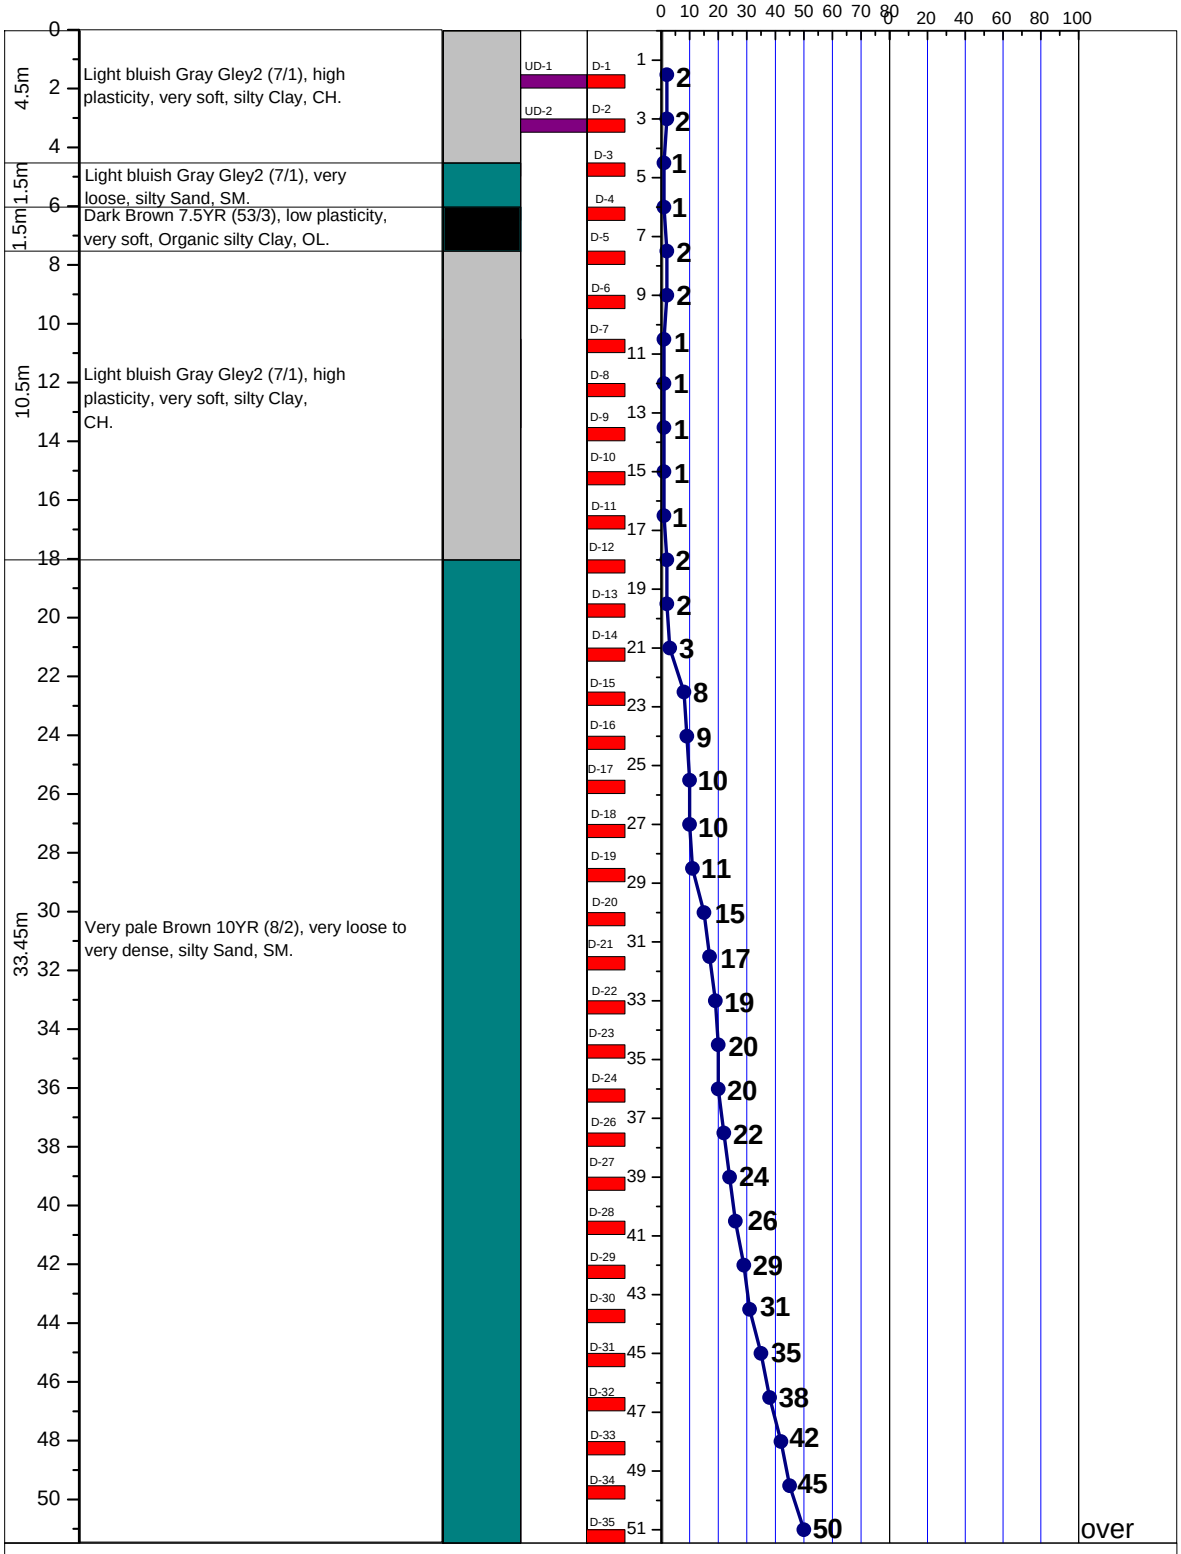


LEGEND FOR BORELOG AND GRAIN SIZE DISTRIBUTION (BASED ON 'ASTM CLASSIFICATION D-2487')

PLASTIC CLAY	SILT	PEAT/HIGHLY ORGANIC SOIL	UNDISTURBED SAMPLE
MICACEOUS FINE SAND/SILT	SAND	SHALE	DISTURBED SAMPLE

N- BLOWS DELIVERED PER FOOT BY A 140 LB HAMMER FALLING 30 INCHES

MAX^{m} PENETRATION= 50 BLOWS. AFTER 50 BLOWS PENETRATION DEPTH WERE MEASURED

A2 PROSOIL	BOREHOLE NO: BH-1	
	LOCATION : Buri Pukur Par, Chittagong.	
PROJECT : Telecommunication Tower.	DEPTH OF BORING : 51.0m	R. L.: 1.07m below from Road Level.
CLIENT : AXIATA (Bangladesh) Ltd.	DATE OF BORING : 16-05-2010.	G. W. T : 1.83m below from E. G. L.

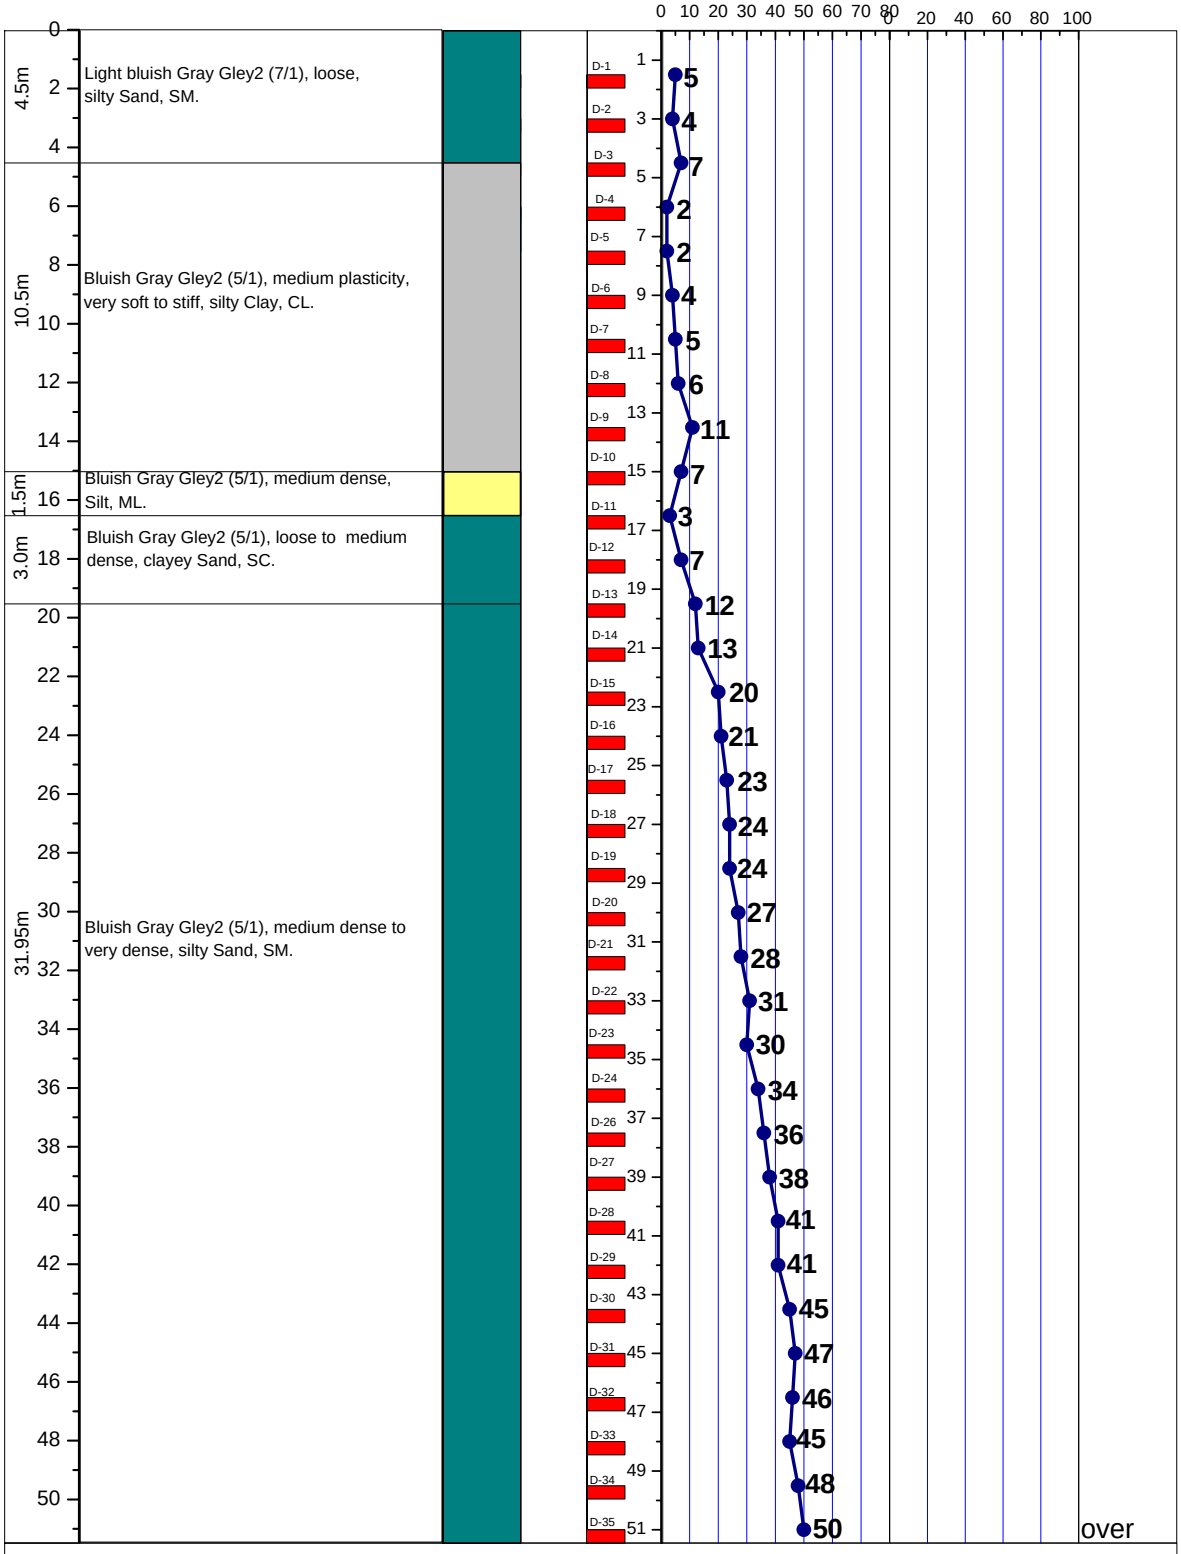


LEGEND FOR BORELOG AND GRAIN SIZE DISTRIBUTION (BASED ON 'ASTM CLASSIFICATION D-2487')

PLASTIC CLAY	SILT	PEAT/HIGHLY ORGANIC SOIL	UNDISTURBED SAMPLE
MICACEOUS FINE SAND/SILT	SAND	SHALE	DISTURBED SAMPLE

N- BLOWS DELIVERED PER FOOT BY A 140 LB HAMMER FALLING 30 INCHES

MAX^{m} PENETRATION= 50 BLOWS. AFTER 50 BLOWS PENETRATION DEPTH WERE MEASURED

A2 PROSOIL	BOREHOLE NO: BH-1	
	LOCATION : Fotikchori, Chittagong.	
PROJECT : Telecommunication Tower.	DEPTH OF BORING : 51.0m	R. L.: 0.91m below from Road Level.
CLIENT : Grameenphone Ltd.	DATE OF BORING : 19-04-2007.	G. W. T : 1.83m below from E. G. L.

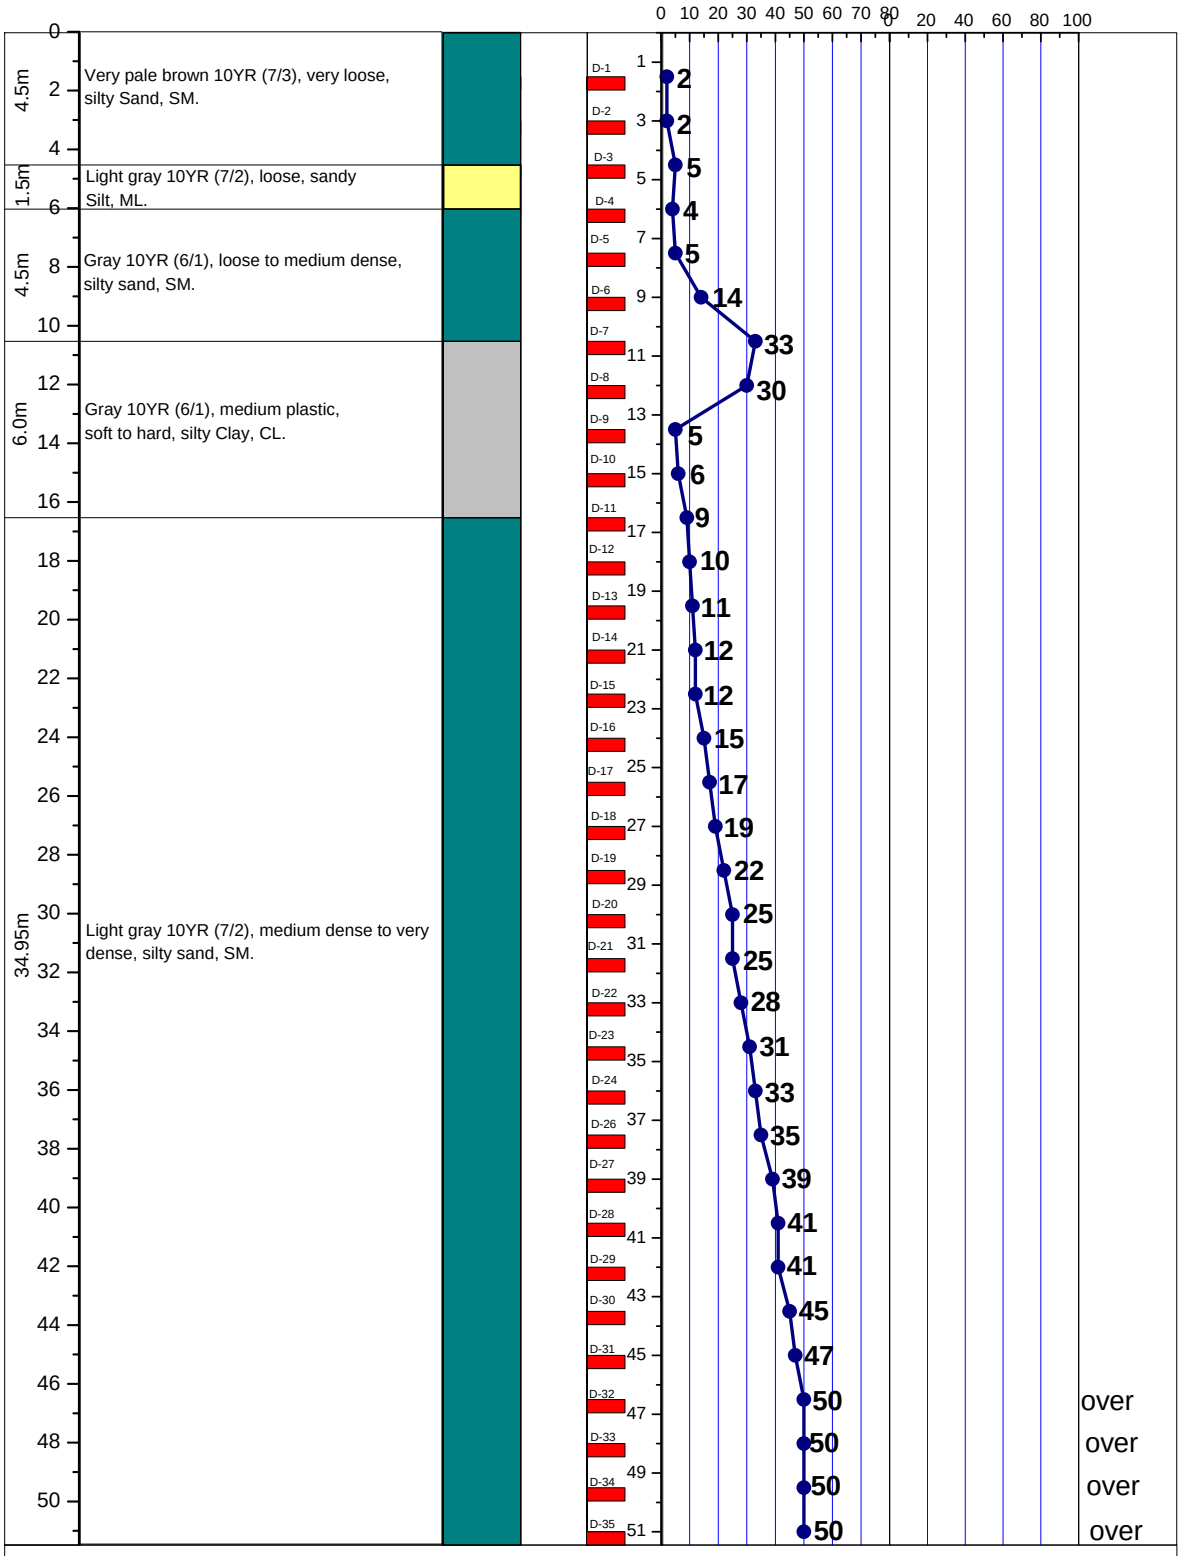


LEGEND FOR BORELOG AND GRAIN SIZE DISTRIBUTION (BASED ON 'ASTM CLASSIFICATION D-2487')

PLASTIC CLAY	SILT	PEAT/HIGHLY ORGANIC SOIL	UNDISTURBED SAMPLE
MICACEOUS FINE SAND/SILT	SAND	SHALE	DISTURBED SAMPLE

N- BLOWS DELIVERED PER FOOT BY A 140 LB HAMMER FALLING 30 INCHES

MAX^{m} PENETRATION= 50 BLOWS. AFTER 50 BLOWS PENETRATION DEPTH WERE MEASURED

A2 PROSOIL	BOREHOLE NO: BH-1	
	LOCATION : Mirshorai, Chittagong.	
PROJECT : Telecommunication Tower.	DEPTH OF BORING : 51.0m	R. L.: 0.76m below from Road Level.
CLIENT : Grameenphone Ltd.	DATE OF BORING : 16-04-2007.	G. W. T : Rain Water.

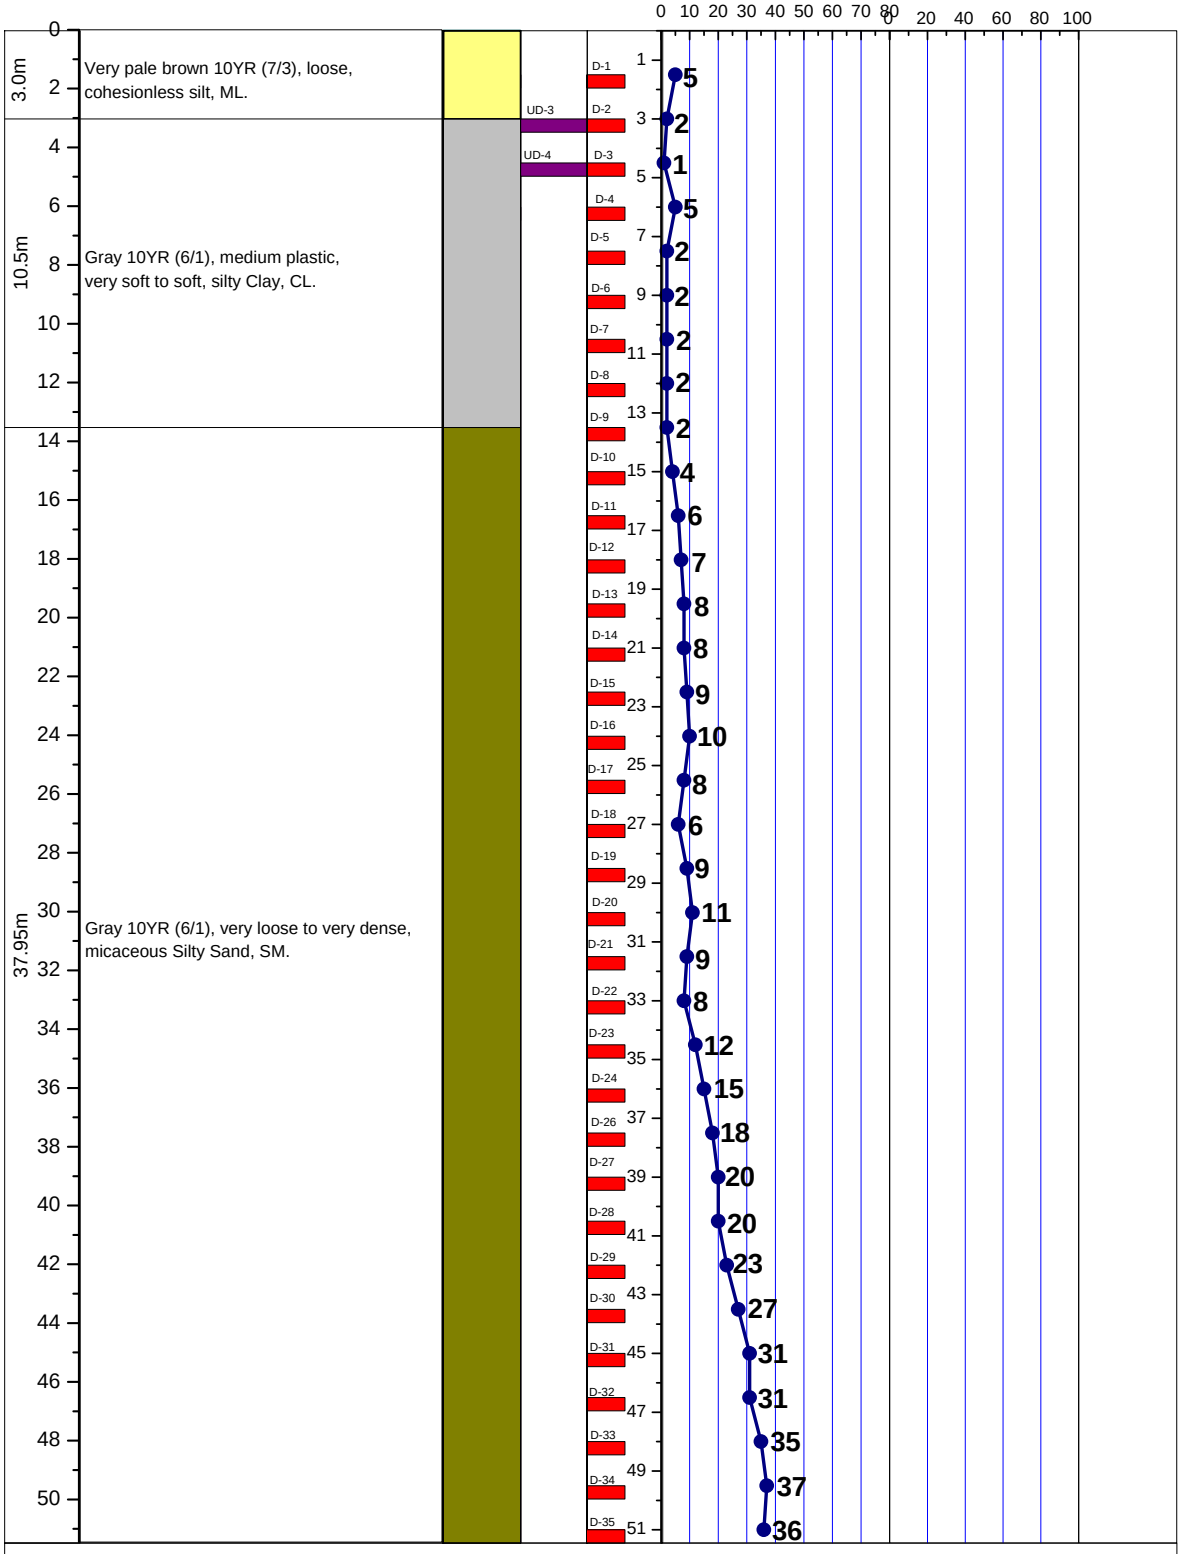


LEGEND FOR BORELOG AND GRAIN SIZE DISTRIBUTION (BASED ON 'ASTM CLASSIFICATION D-2487')

PLASTIC CLAY	SILT	PEAT/HIGHLY ORGANIC SOIL	UNDISTURBED SAMPLE
MICACEOUS FINE SAND/SILT	SAND	SHALE	DISTURBED SAMPLE

N- BLOWS DELIVERED PER FOOT BY A 140 LB HAMMER FALLING 30 INCHES

MAX^{m} PENETRATION= 50 BLOWS. AFTER 50 BLOWS PENETRATION DEPTH WERE MEASURED

A2	PROSOIL	BOREHOLE NO: BH-1	
		LOCATION : CGEPZ, Chittagong.	
PROJECT : Telecommunication Tower.		DEPTH OF BORING : 51.0m	R. L.: 0.10m below from Road Level.
CLIENT : Grameenphone Ltd.		DATE OF BORING : 10-10-2007.	G. W. T : 0.76m below from E. G. L.

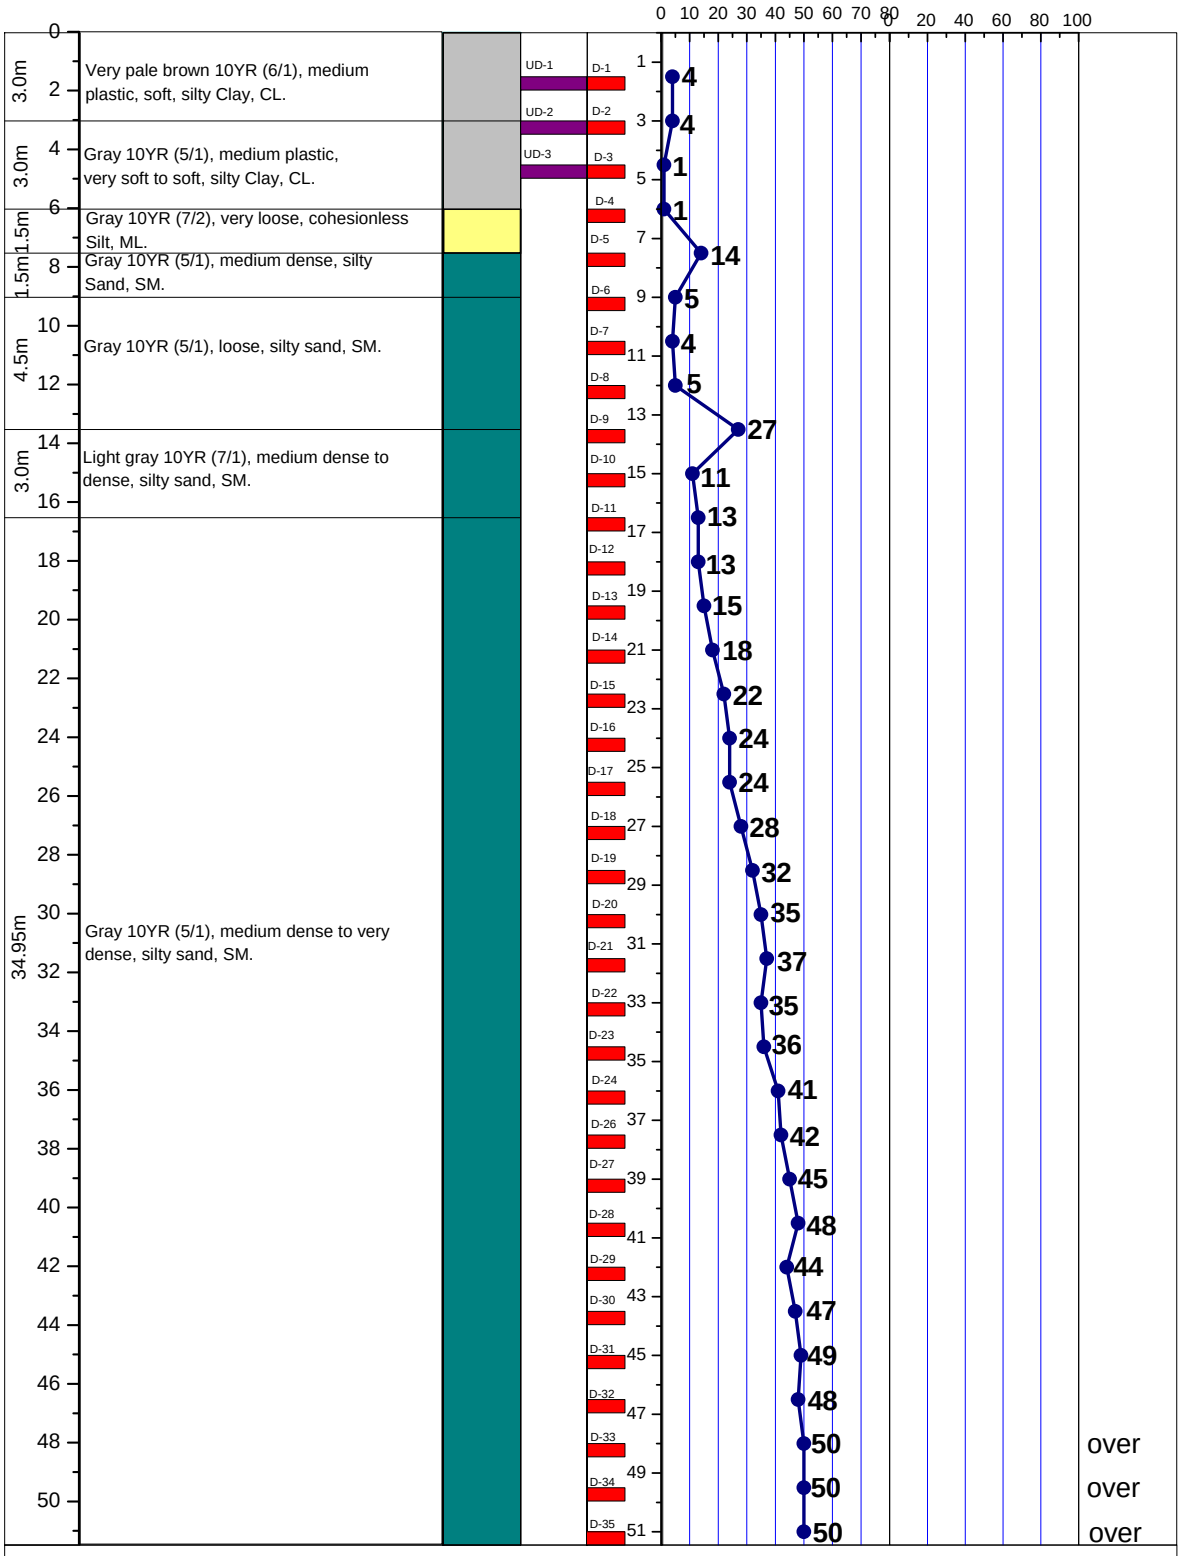


LEGEND FOR BORELOG AND GRAIN SIZE DISTRIBUTION (BASED ON 'ASTM CLASSIFICATION D-2487')

PLASTIC CLAY	SILT	PEAT/HIGHLY ORGANIC SOIL	UNDISTURBED SAMPLE
MICACEOUS FINE SAND/SILT	SAND	SHALE	DISTURBED SAMPLE

N- BLOWS DELIVERED PER FOOT BY A 140 LB HAMMER FALLING 30 INCHES

MAX^{m} PENETRATION= 50 BLOWS. AFTER 50 BLOWS PENETRATION DEPTH WERE MEASURED

A2 PROSOIL	BOREHOLE NO: BH-1	
	LOCATION : Chambol Bazar, Bashkhali, Chittagong.	
PROJECT : Telecommunication Tower.	DEPTH OF BORING : 51.0m	R. L.: 1.22m below from Road Level.
CLIENT : AXIATA (Bangladesh) Ltd.	DATE OF BORING : 02-11-2009.	G. W. T : 0.15m above from E. G. L.

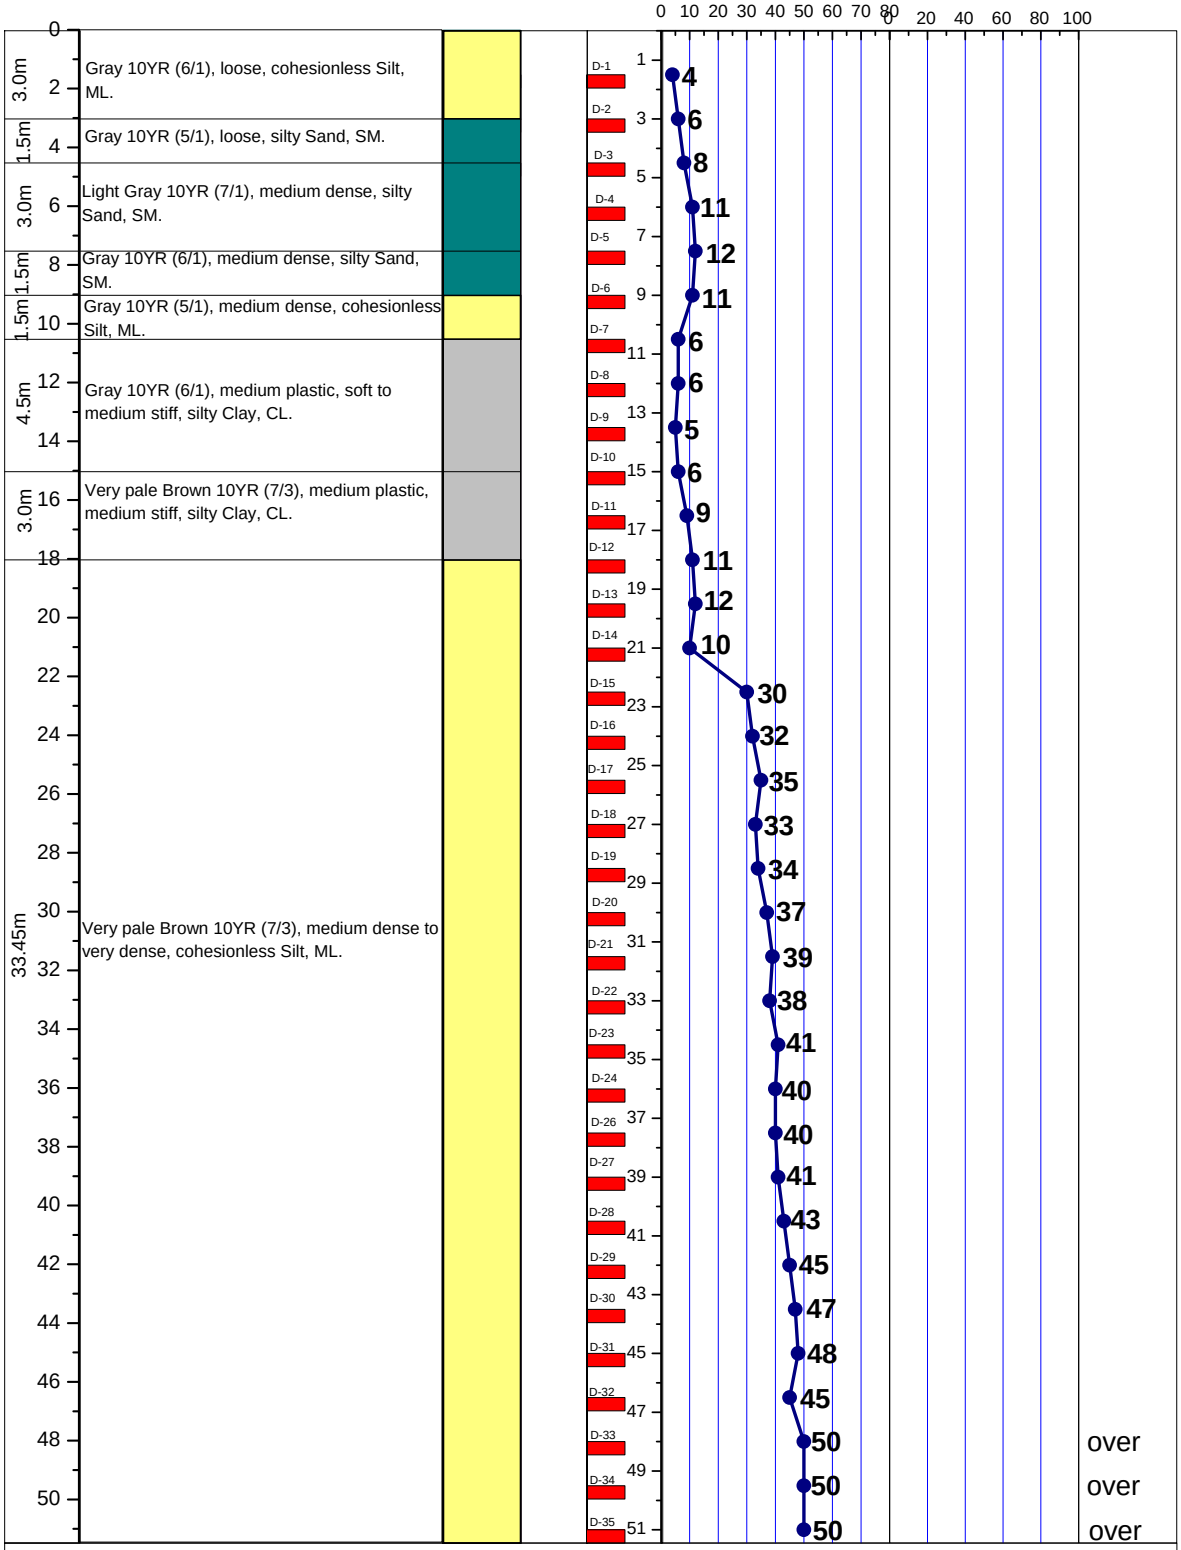


LEGEND FOR BORELOG AND GRAIN SIZE DISTRIBUTION (BASED ON 'ASTM CLASSIFICATION D-2487')

PLASTIC CLAY	SILT	PEAT/HIGHLY ORGANIC SOIL	UNDISTURBED SAMPLE
MICACEOUS FINE SAND/SILT	SAND	SHALE	DISTURBED SAMPLE

N- BLOWS DELIVERED PER FOOT BY A 140 LB HAMMER FALLING 30 INCHES

MAX^{m} PENETRATION= 50 BLOWS. AFTER 50 BLOWS PENETRATION DEPTH WERE MEASURED

A2	PROSOIL	BOREHOLE NO: BH-1	
		LOCATION : Chikon Chori, Bhujpur, Chittagong.	
PROJECT : Telecommunication Tower.		DEPTH OF BORING : 51.0m	R. L.: 3.96m below from Road Level.
CLIENT : TM International, Bangladesh Ltd.		DATE OF BORING : 10-01-2009	G. W. T : 0.10m above from E. G. L.

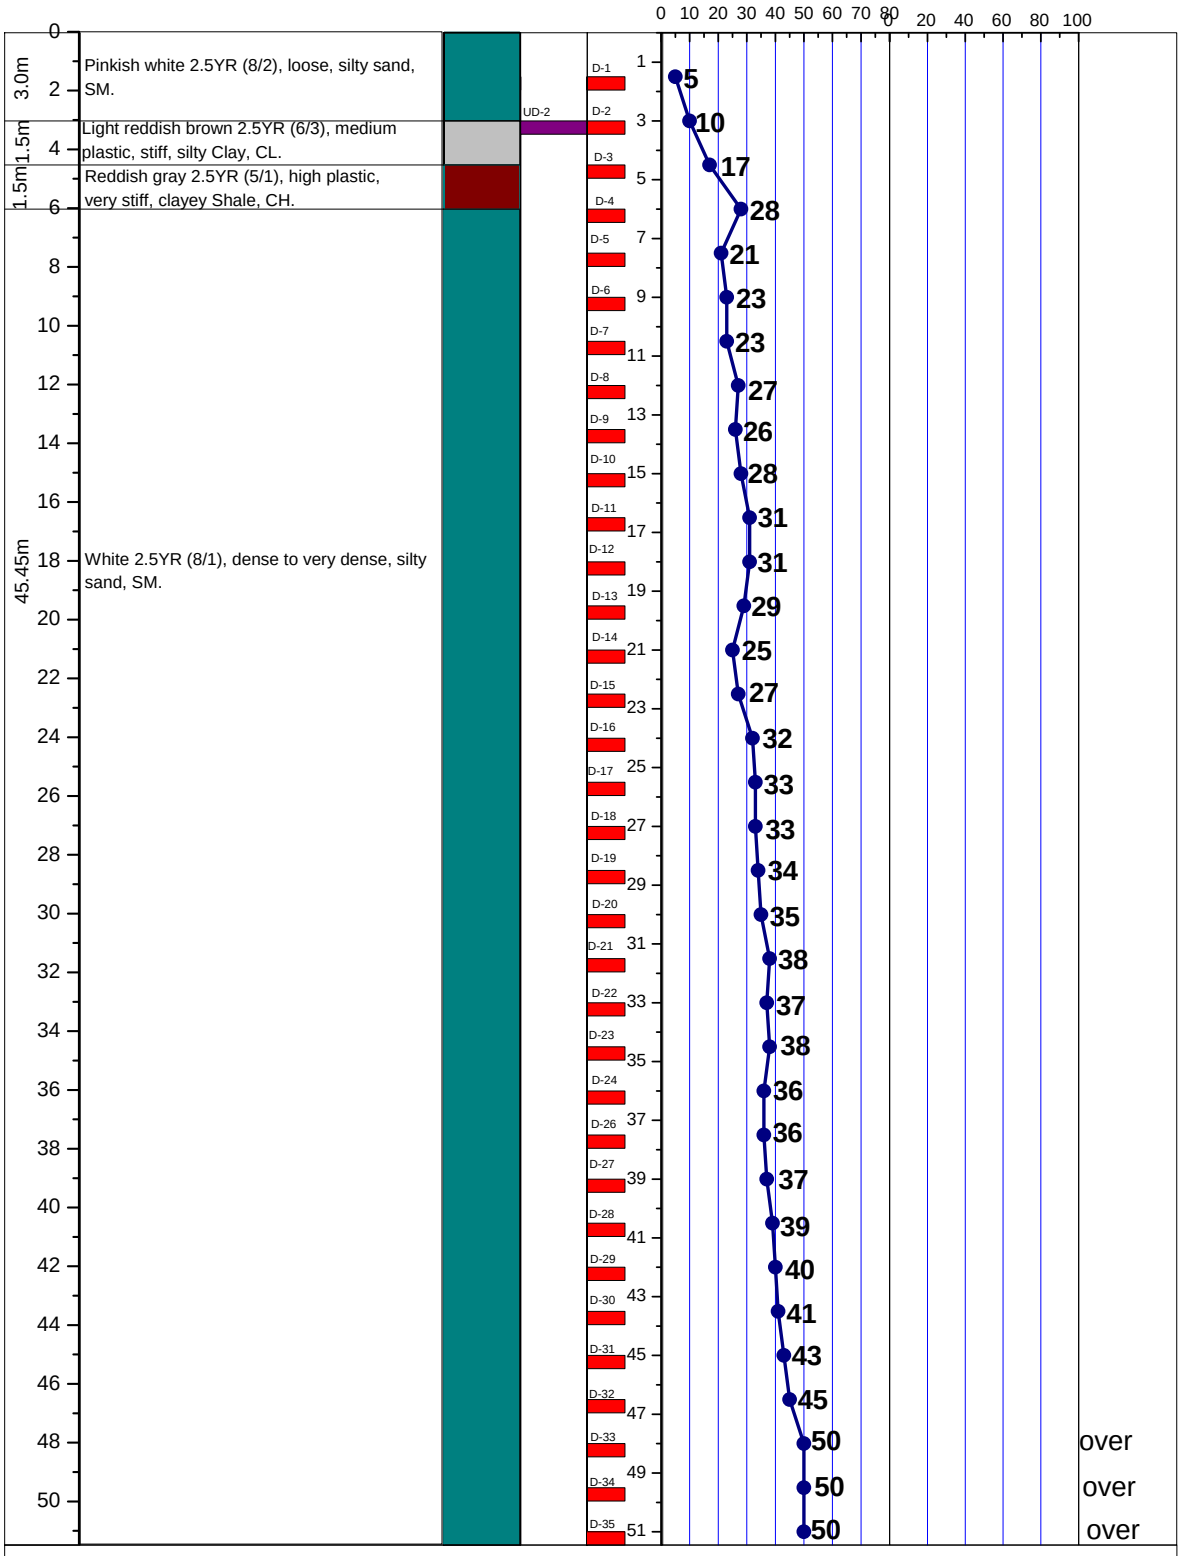


LEGEND FOR BORELOG AND GRAIN SIZE DISTRIBUTION (BASED ON 'ASTM CLASSIFICATION D-2487')

PLASTIC CLAY	SILT	PEAT/HIGHLY ORGANIC SOIL	UNDISTURBED SAMPLE
MICACEOUS FINE SAND/SILT	SAND	SHALE	DISTURBED SAMPLE

N- BLOWS DELIVERED PER FOOT BY A 140 LB HAMMER FALLING 30 INCHES

MAX^{m} PENETRATION= 50 BLOWS. AFTER 50 BLOWS PENETRATION DEPTH WERE MEASURED

A2 PROSOIL	BOREHOLE NO: BH-1	
	LOCATION : Doloinagar, Hathazari, Raujan, Chittagong.	
PROJECT : Telecommunication Tower.	DEPTH OF BORING : 51.0m	R. L.: 0.15m below from Road Level.
CLIENT : AXIATA (Bangladesh) Ltd.	DATE OF BORING : 02-06-2011.	G. W. T : 1.52m below from E. G. L.

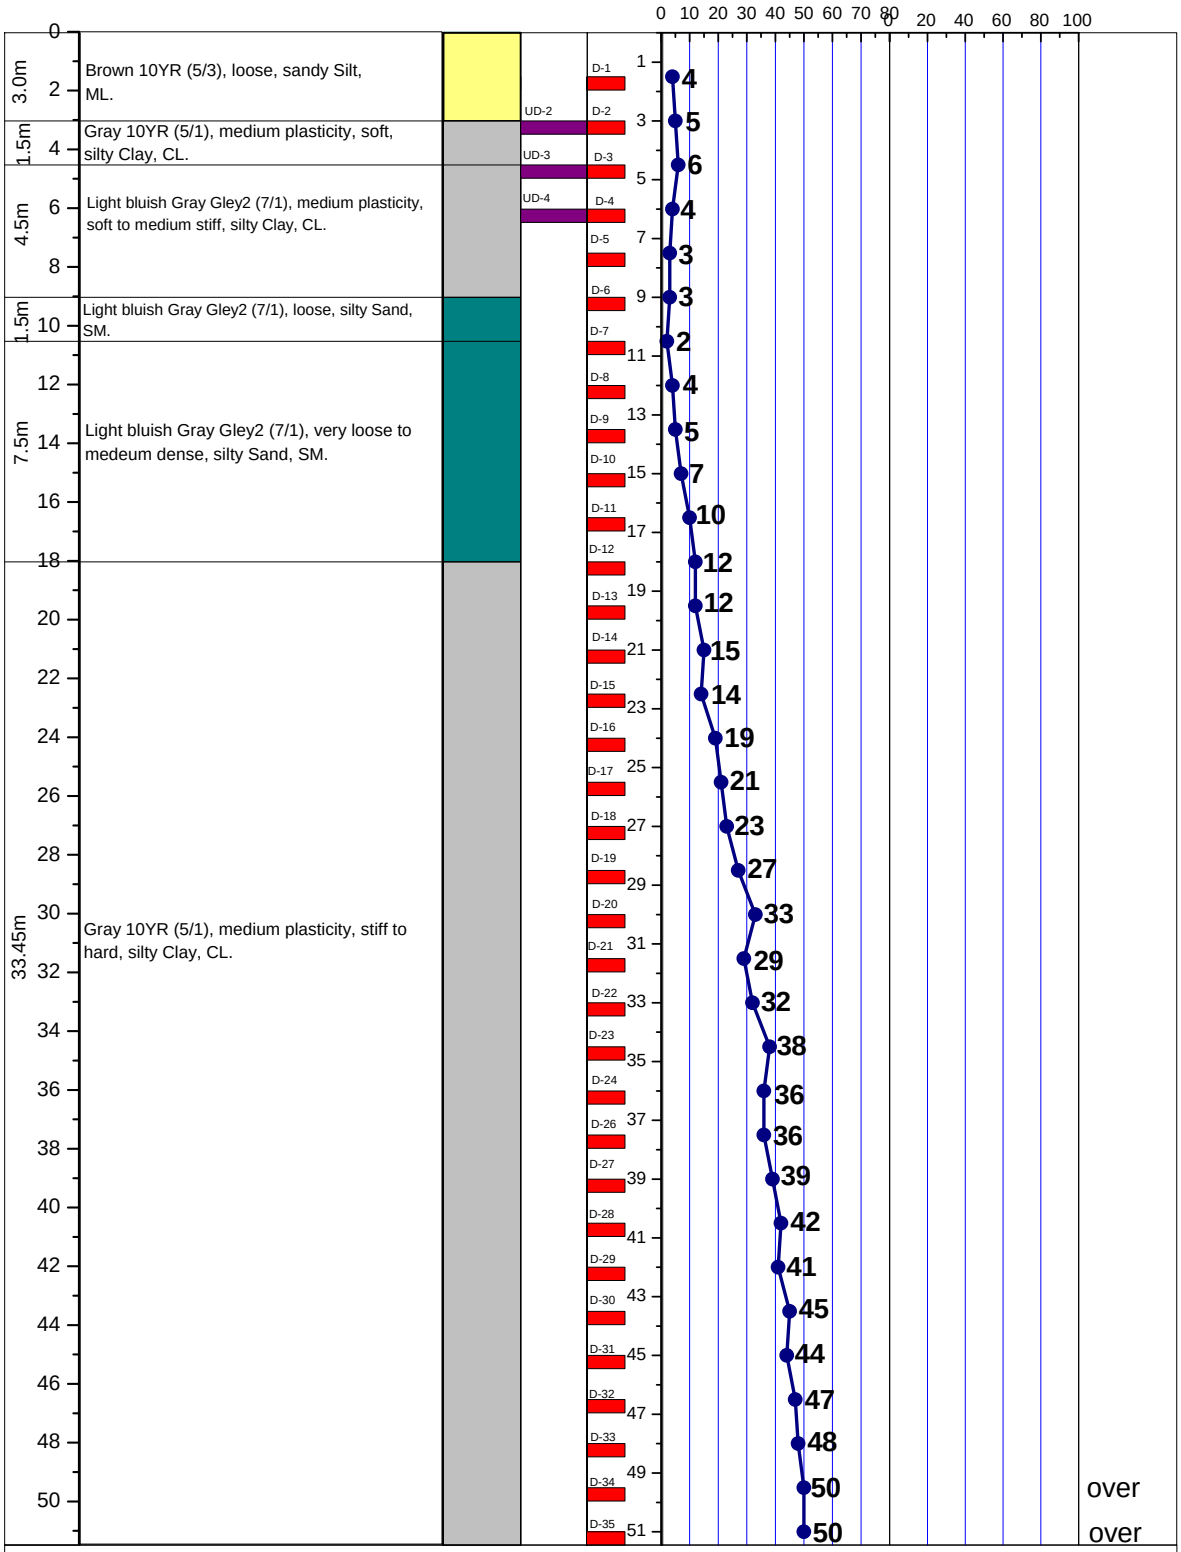


LEGEND FOR BORELOG AND GRAIN SIZE DISTRIBUTION (BASED ON 'ASTM CLASSIFICATION D-2487')

PLASTIC CLAY	SILT	PEAT/HIGHLY ORGANIC SOIL	UNDISTURBED SAMPLE
MICACEOUS FINE SAND/SILT	SAND	SHALE	DISTURBED SAMPLE

N- BLOWS DELIVERED PER FOOT BY A 140 LB HAMMER FALLING 30 INCHES

MAX^{m} PENETRATION= 50 BLOWS. AFTER 50 BLOWS PENETRATION DEPTH WERE MEASURED

A2 PROSOIL	BOREHOLE NO: BH-1	
	LOCATION : Dhurong, Fatikchori, Chittagong.	
PROJECT : Telecommunication Tower.	DEPTH OF BORING : 51.0m	R. L.: 1.21m below from Road Level.
CLIENT : TM International, Bangladesh Ltd.	DATE OF BORING : 19-02-2009.	G. W. T : 1.82m below from E. G. L.

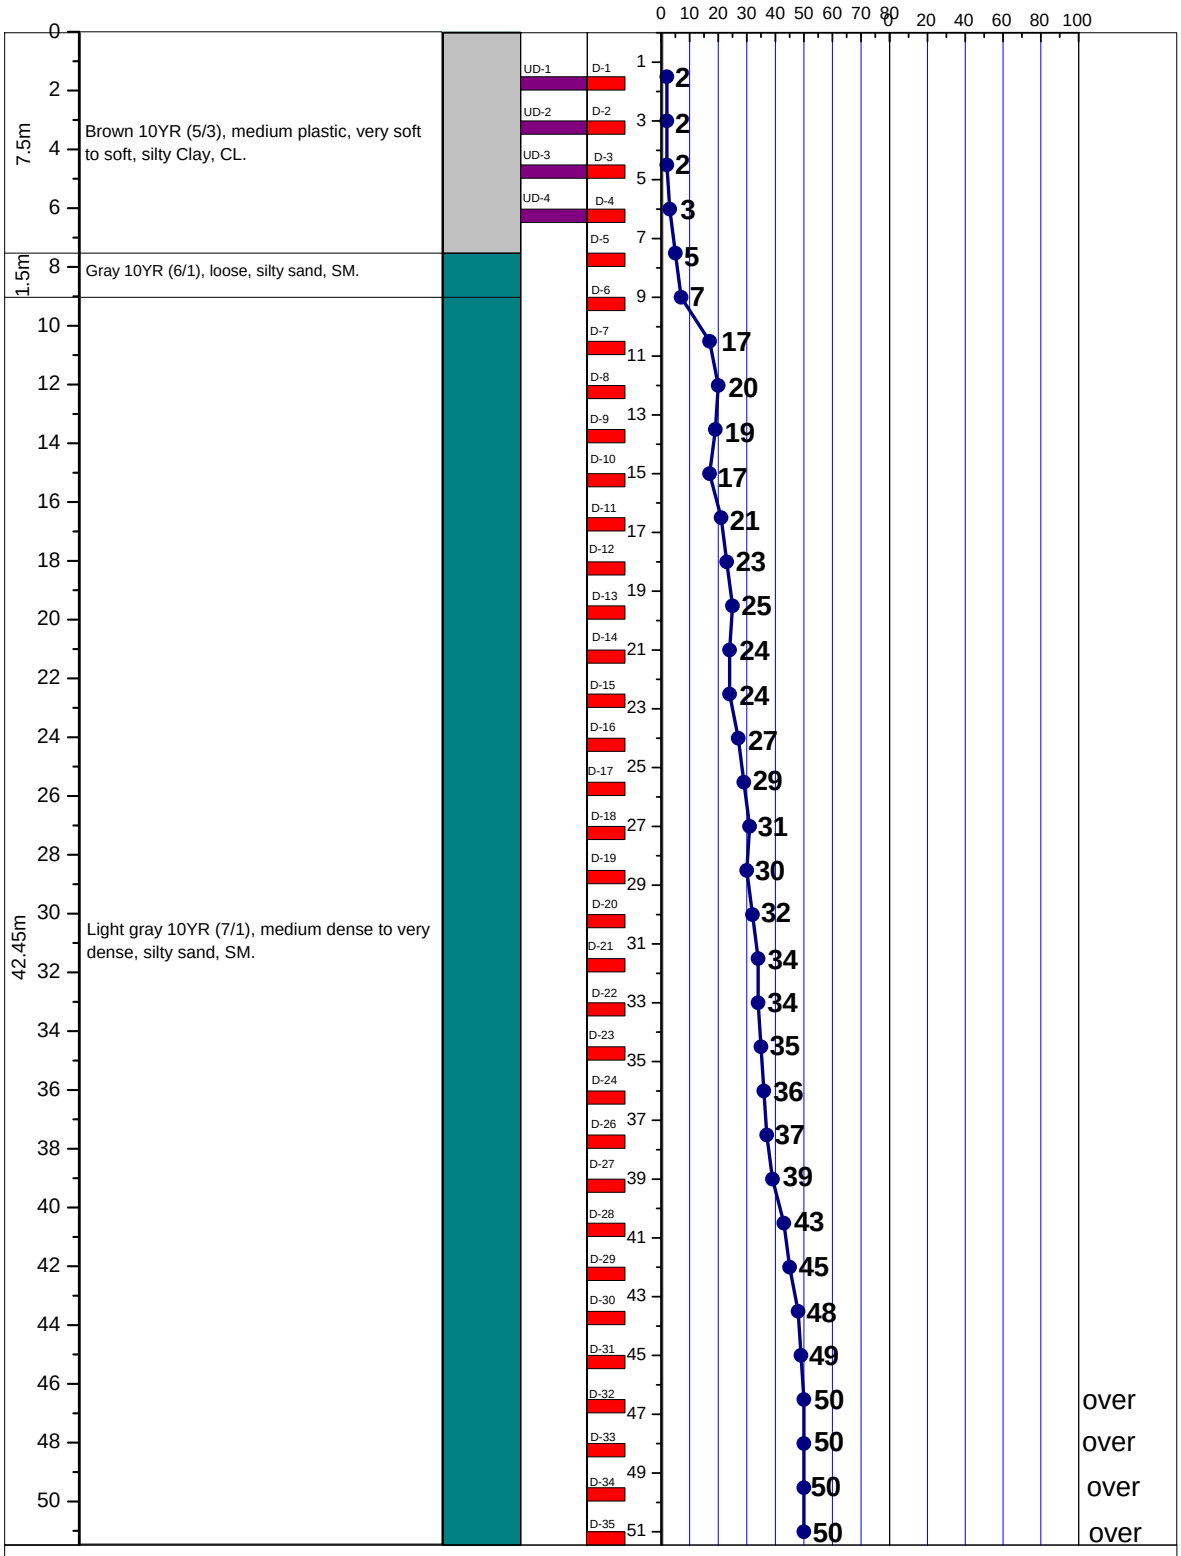


LEGEND FOR BORELOG AND GRAIN SIZE DISTRIBUTION (BASED ON 'ASTM CLASSIFICATION D-2487')

PLASTIC CLAY	SILT	PEAT/HIGHLY ORGANIC SOIL	UNDISTURBED SAMPLE
MICACEOUS FINE SAND/SILT	SAND	SHALE	DISTURBED SAMPLE

N- BLOWS DELIVERED PER FOOT BY A 140 LB HAMMER FALLING 30 INCHES

MAX^{m} PENETRATION= 50 BLOWS. AFTER 50 BLOWS PENETRATION DEPTH WERE MEASURED

A2	PROSOIL	BOREHOLE NO: BH-1	
		LOCATION : East Bhatirkhil, Sitakunda, Chittagong.	
PROJECT : Telecommunication Tower.		DEPTH OF BORING : 51.0m	R. L.: 1.06m below from Road Level.
CLIENT : AXIATA (Bangladesh) Ltd.		DATE OF BORING : 16-02-2010.	G. W. T : 2.43m below from E. G. L.

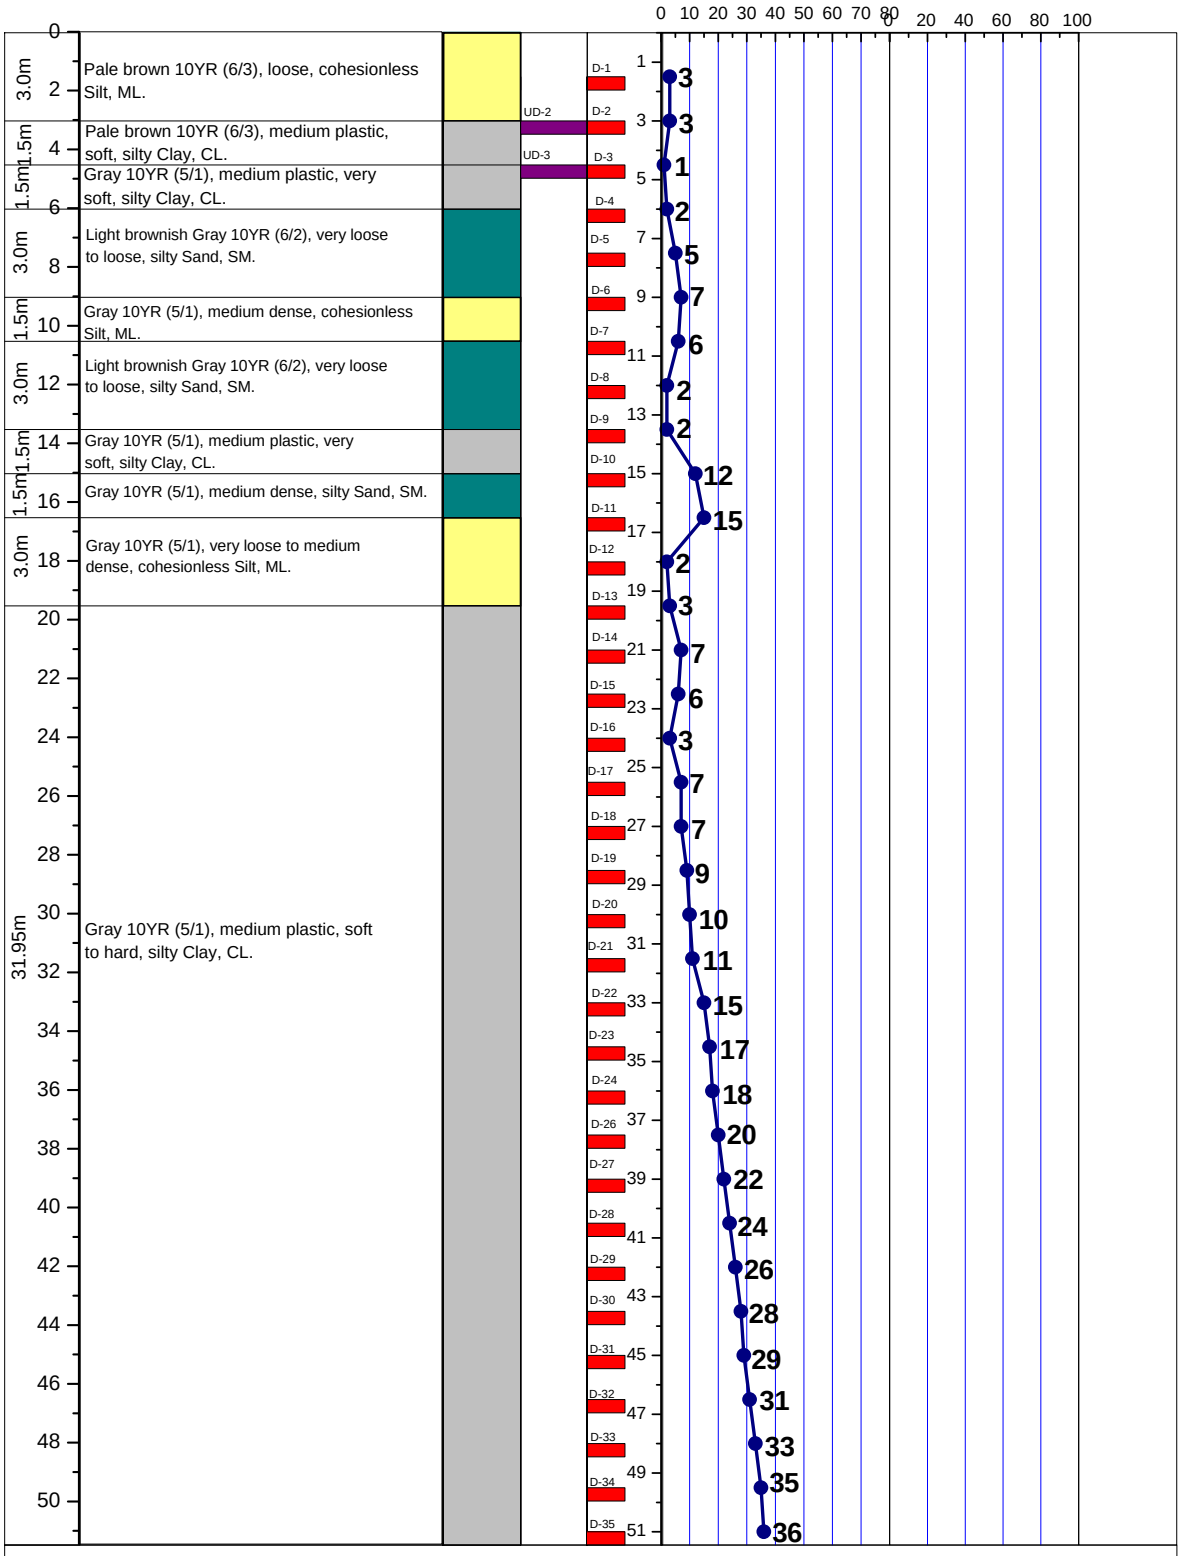


LEGEND FOR BORELOG AND GRAIN SIZE DISTRIBUTION (BASED ON 'ASTM CLASSIFICATION D-2487')

PLASTIC CLAY	SILT	PEAT/HIGHLY ORGANIC SOIL	UNDISTURBED SAMPLE
MICACEOUS FINE SAND/SILT	SAND	SHALE	DISTURBED SAMPLE

N- BLOWS DELIVERED PER FOOT BY A 140 LB HAMMER FALLING 30 INCHES

MAX^{m} PENETRATION= 50 BLOWS. AFTER 50 BLOWS PENETRATION DEPTH WERE MEASURED

A2	PROSOIL	BOREHOLE NO: BH-1	
		LOCATION : Uttar Madrasa, Hathazari, Chittagong.	
PROJECT : Telecommunication Tower.		DEPTH OF BORING : 51.0m	R. L.: 1.52m below from Road Level.
CLIENT : TM International, Bangladesh Ltd.		DATE OF BORING : 19-02-2009.	G. W. T : 1.21m below from E. G. L.

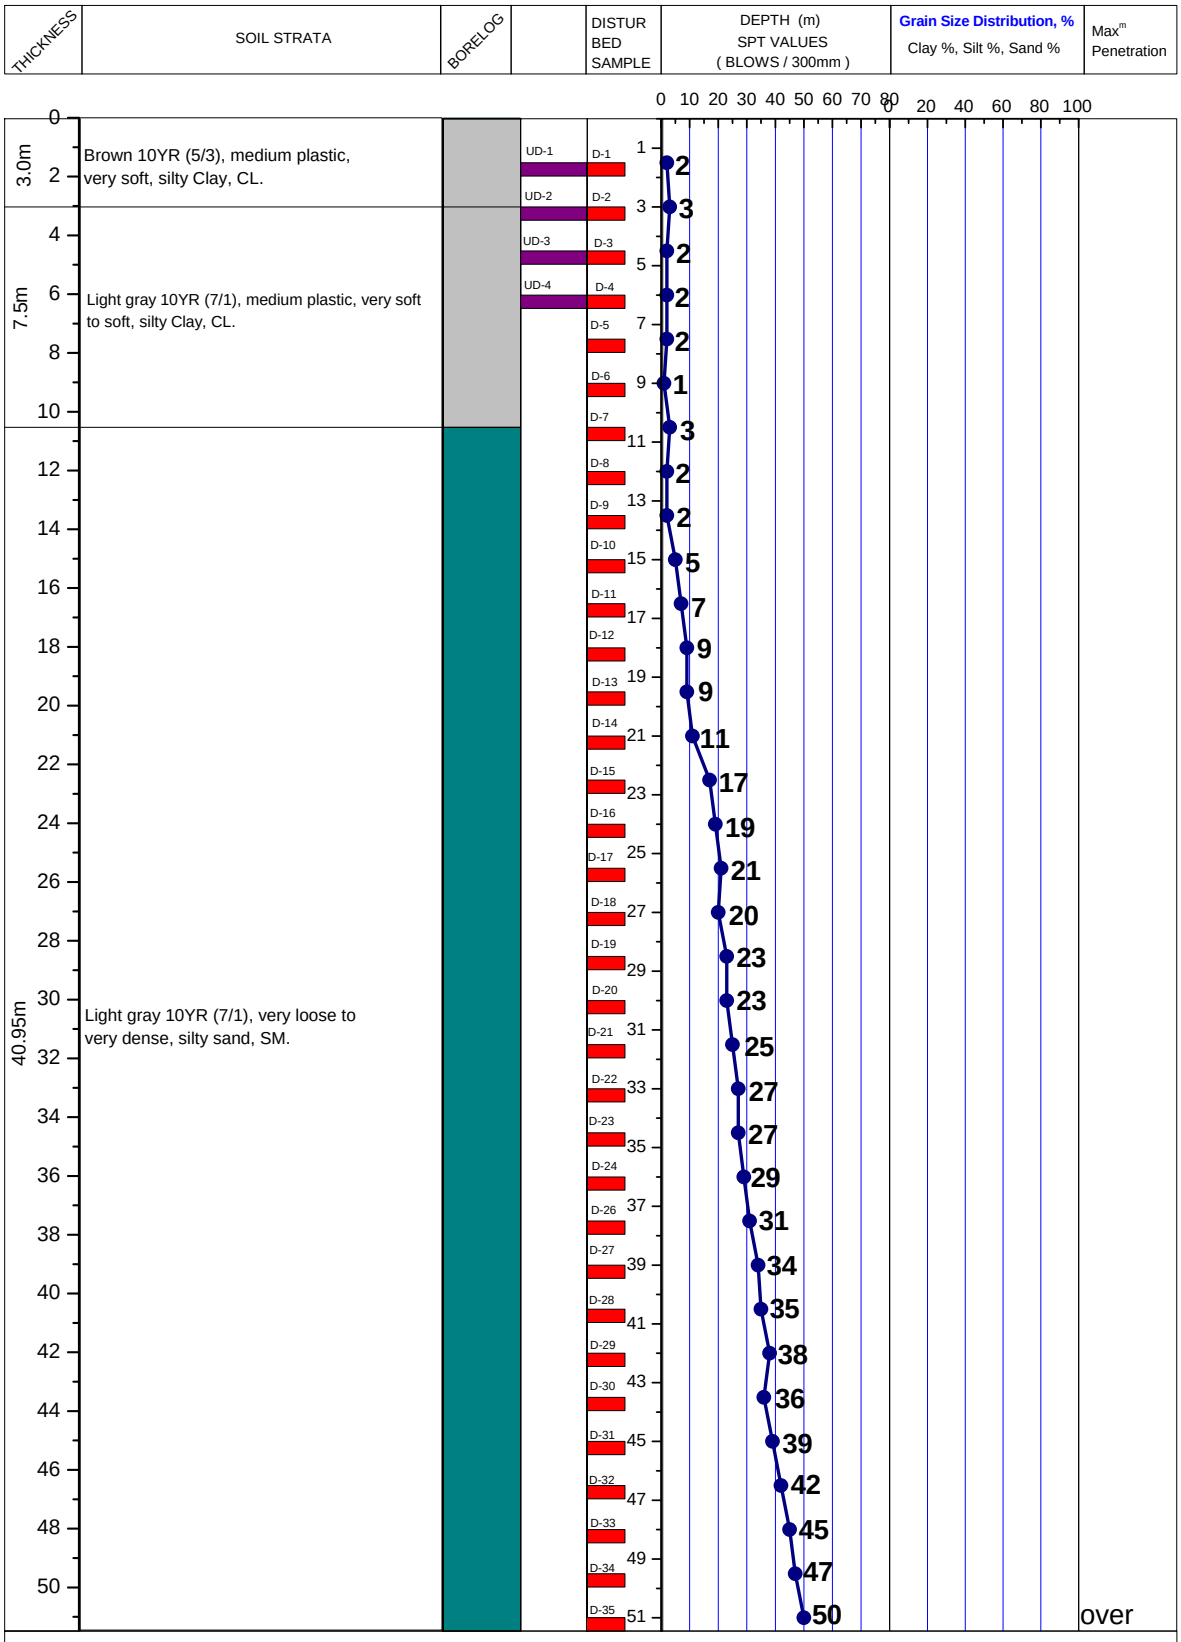


LEGEND FOR BORELOG AND GRAIN SIZE DISTRIBUTION (BASED ON 'ASTM CLASSIFICATION D-2487')

PLASTIC CLAY	SILT	PEAT/HIGHLY ORGANIC SOIL	UNDISTURBED SAMPLE
MICACEOUS FINE SAND/SILT	SAND	SHALE	DISTURBED SAMPLE

N- BLOWS DELIVERED PER FOOT BY A 140 LB HAMMER FALLING 30 INCHES

MAX^{m} PENETRATION= 50 BLOWS. AFTER 50 BLOWS PENETRATION DEPTH WERE MEASURED

A2	PROSOIL	BOREHOLE NO: BH-1	
		LOCATION : Hazipara, Fatikchari, Chittagong.	
PROJECT : Telecommunication Tower.		DEPTH OF BORING : 51.0m	R. L.: 0.91m above from Road Level.
CLIENT : TM International, Bangladesh Ltd.		DATE OF BORING : 01-01-2009	G. W. T : 6.09m below from E. G. L.

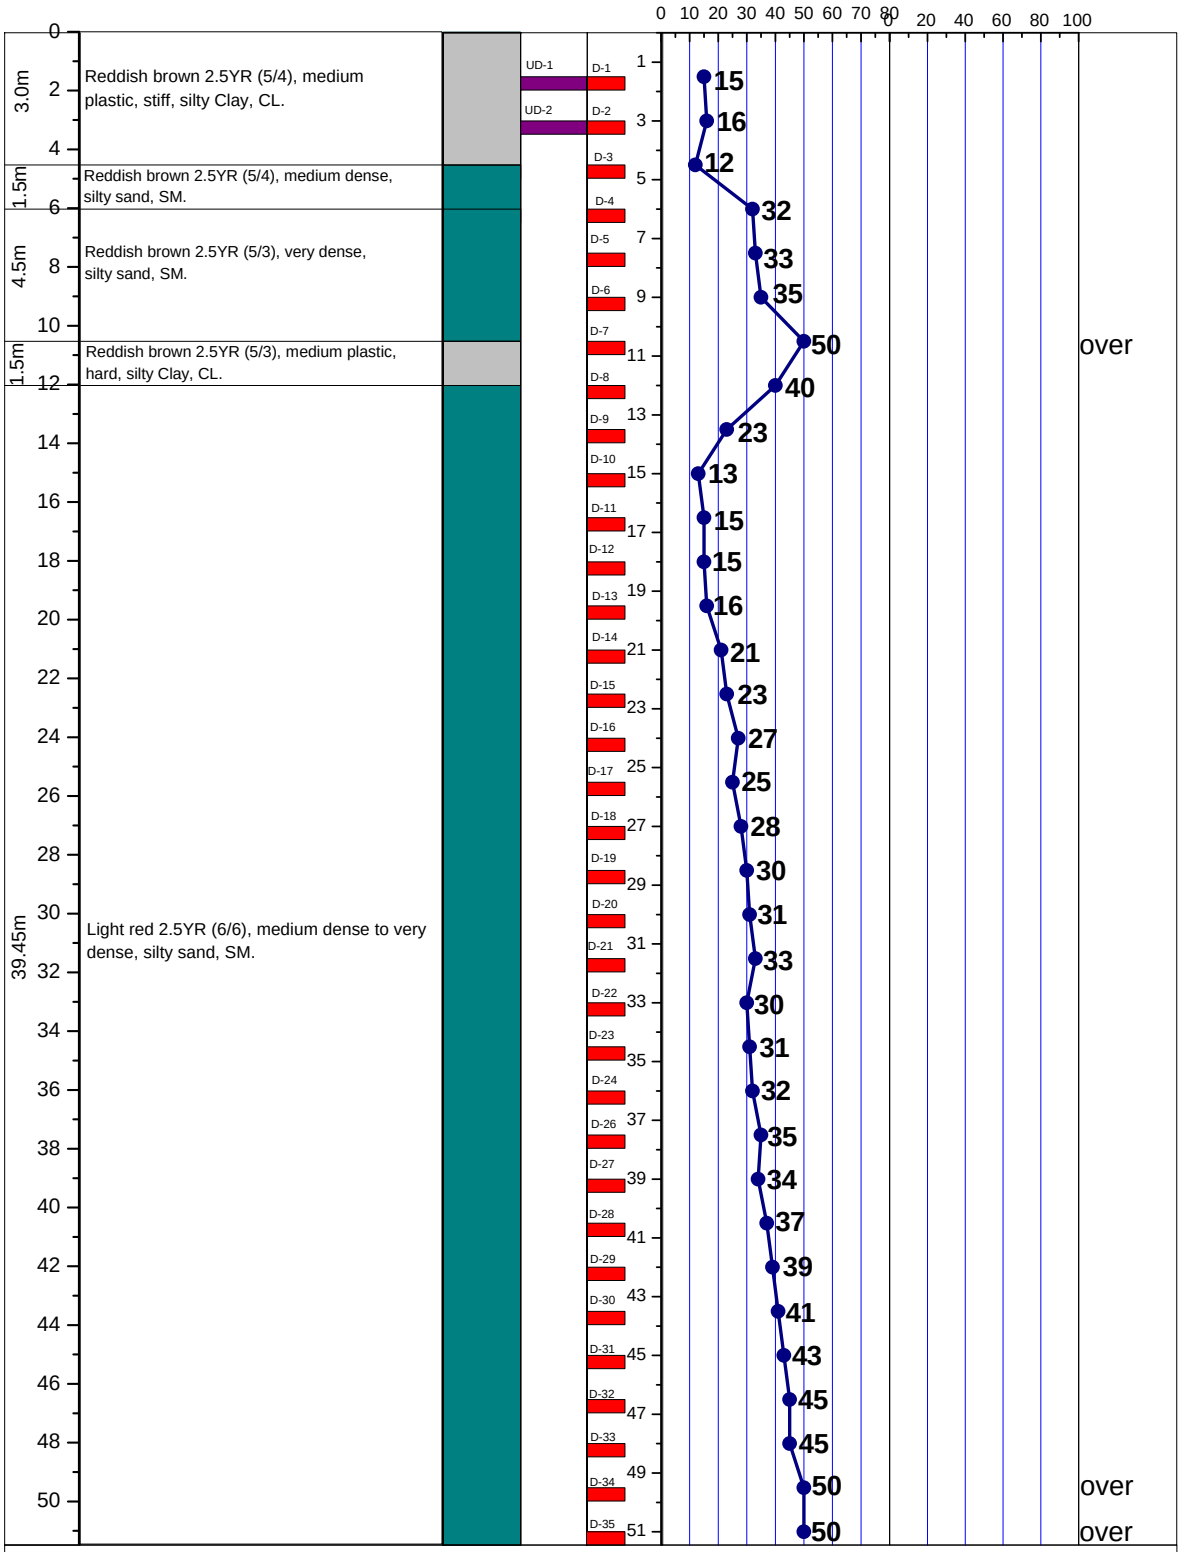


LEGEND FOR BORELOG AND GRAIN SIZE DISTRIBUTION (BASED ON 'ASTM CLASSIFICATION D-2487')

PLASTIC CLAY	SILT	PEAT/HIGHLY ORGANIC SOIL	UNDISTURBED SAMPLE
MICACEOUS FINE SAND/SILT	SAND	SHALE	DISTURBED SAMPLE

N- BLOWS DELIVERED PER FOOT BY A 140 LB HAMMER FALLING 30 INCHES

MAX^{m} PENETRATION= 50 BLOWS. AFTER 50 BLOWS PENETRATION DEPTH WERE MEASURED

A2 PROSOIL	BOREHOLE NO: BH-1	
	LOCATION : Heakow 3, Gojaria, Heakow, Bhujpur, Chittagong.	
PROJECT : Telecommunication Tower.	DEPTH OF BORING : 51.0m	R. L.: 1.52m below from Road Level.
CLIENT : AXIATA (Bangladesh) Ltd.	DATE OF BORING : 20-12-2012.	G. W. T : 0.91m below from E. G. L.

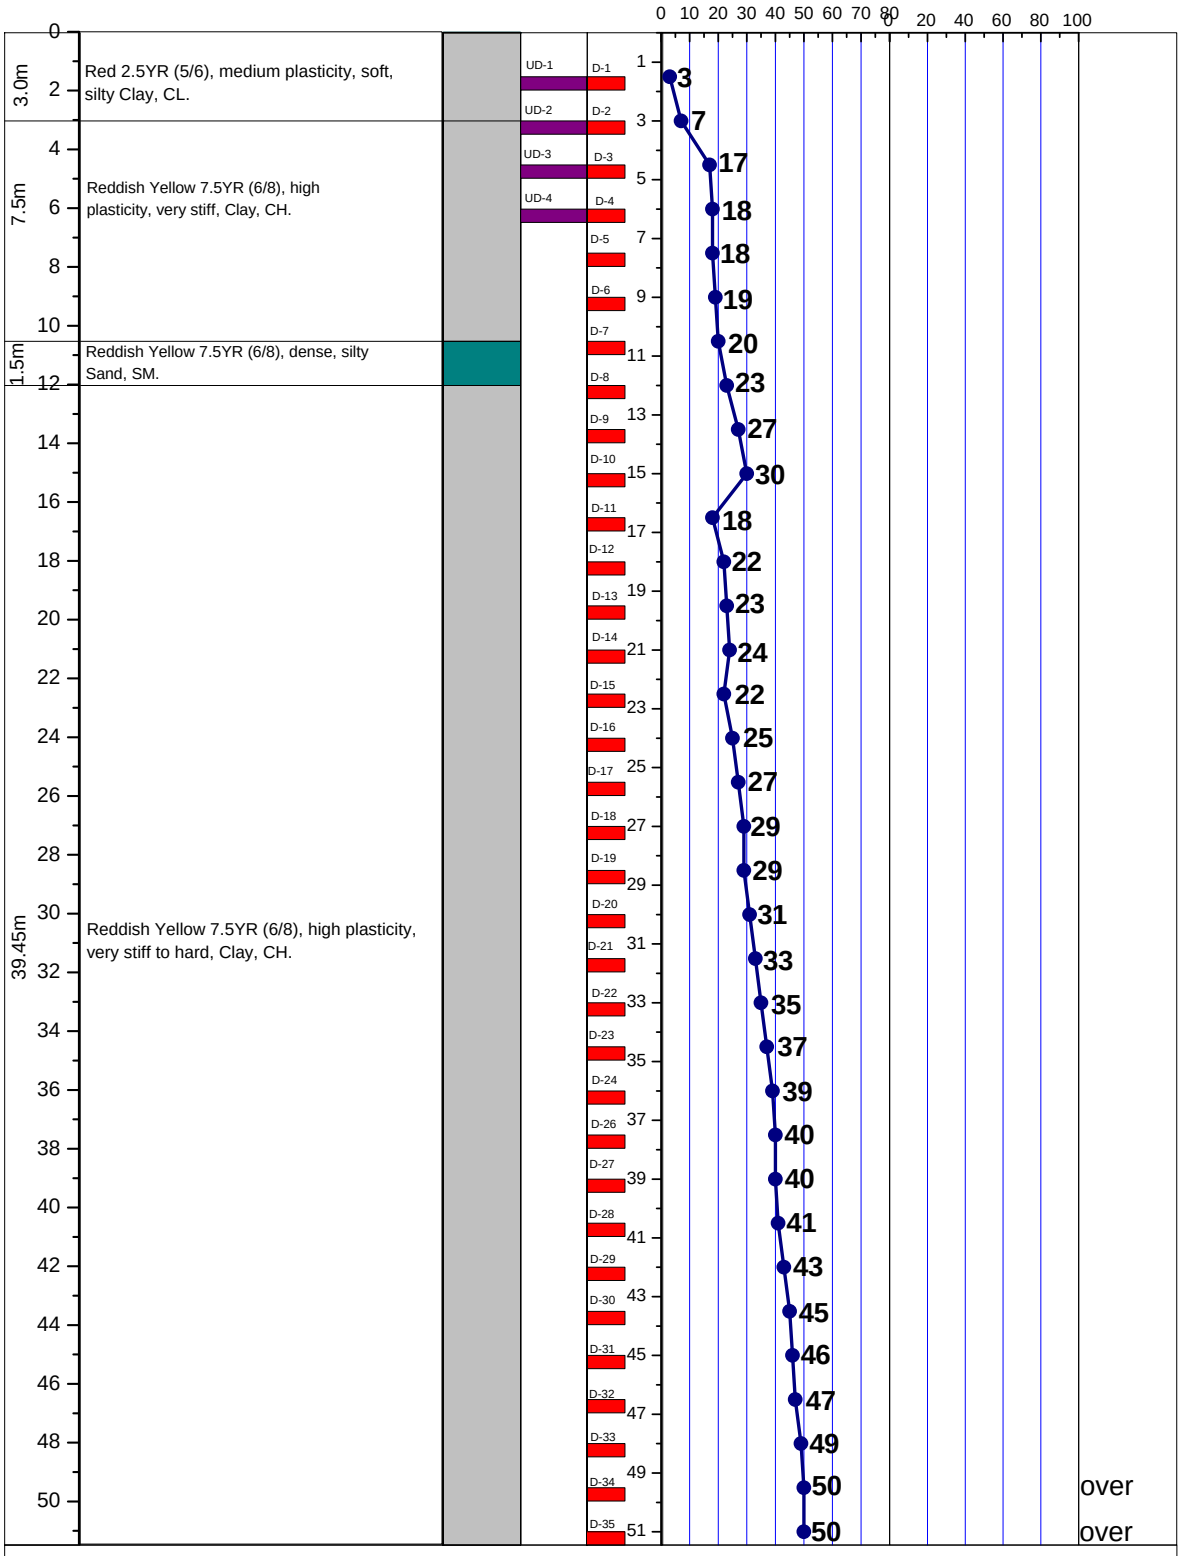


LEGEND FOR BORELOG AND GRAIN SIZE DISTRIBUTION (BASED ON 'ASTM CLASSIFICATION D-2487')

PLASTIC CLAY	SILT	PEAT/HIGHLY ORGANIC SOIL	UNDISTURBED SAMPLE
MICACEOUS FINE SAND/SILT	SAND	SHALE	DISTURBED SAMPLE

N- BLOWS DELIVERED PER FOOT BY A 140 LB HAMMER FALLING 30 INCHES

MAX^{m} PENETRATION= 50 BLOWS. AFTER 50 BLOWS PENETRATION DEPTH WERE MEASURED

A2	PROSOIL	BOREHOLE NO: BH-1	
		LOCATION : Jani pathar, Rouzan, Chittagong.	
PROJECT : Telecommunication Tower.		DEPTH OF BORING : 51.0m	R. L.: 0.76m below from Road Level.
CLIENT : AXIATA (Bangladesh) Ltd.		DATE OF BORING : 01-10-2009.	G. W. T : 0.15m above from E. G. L.

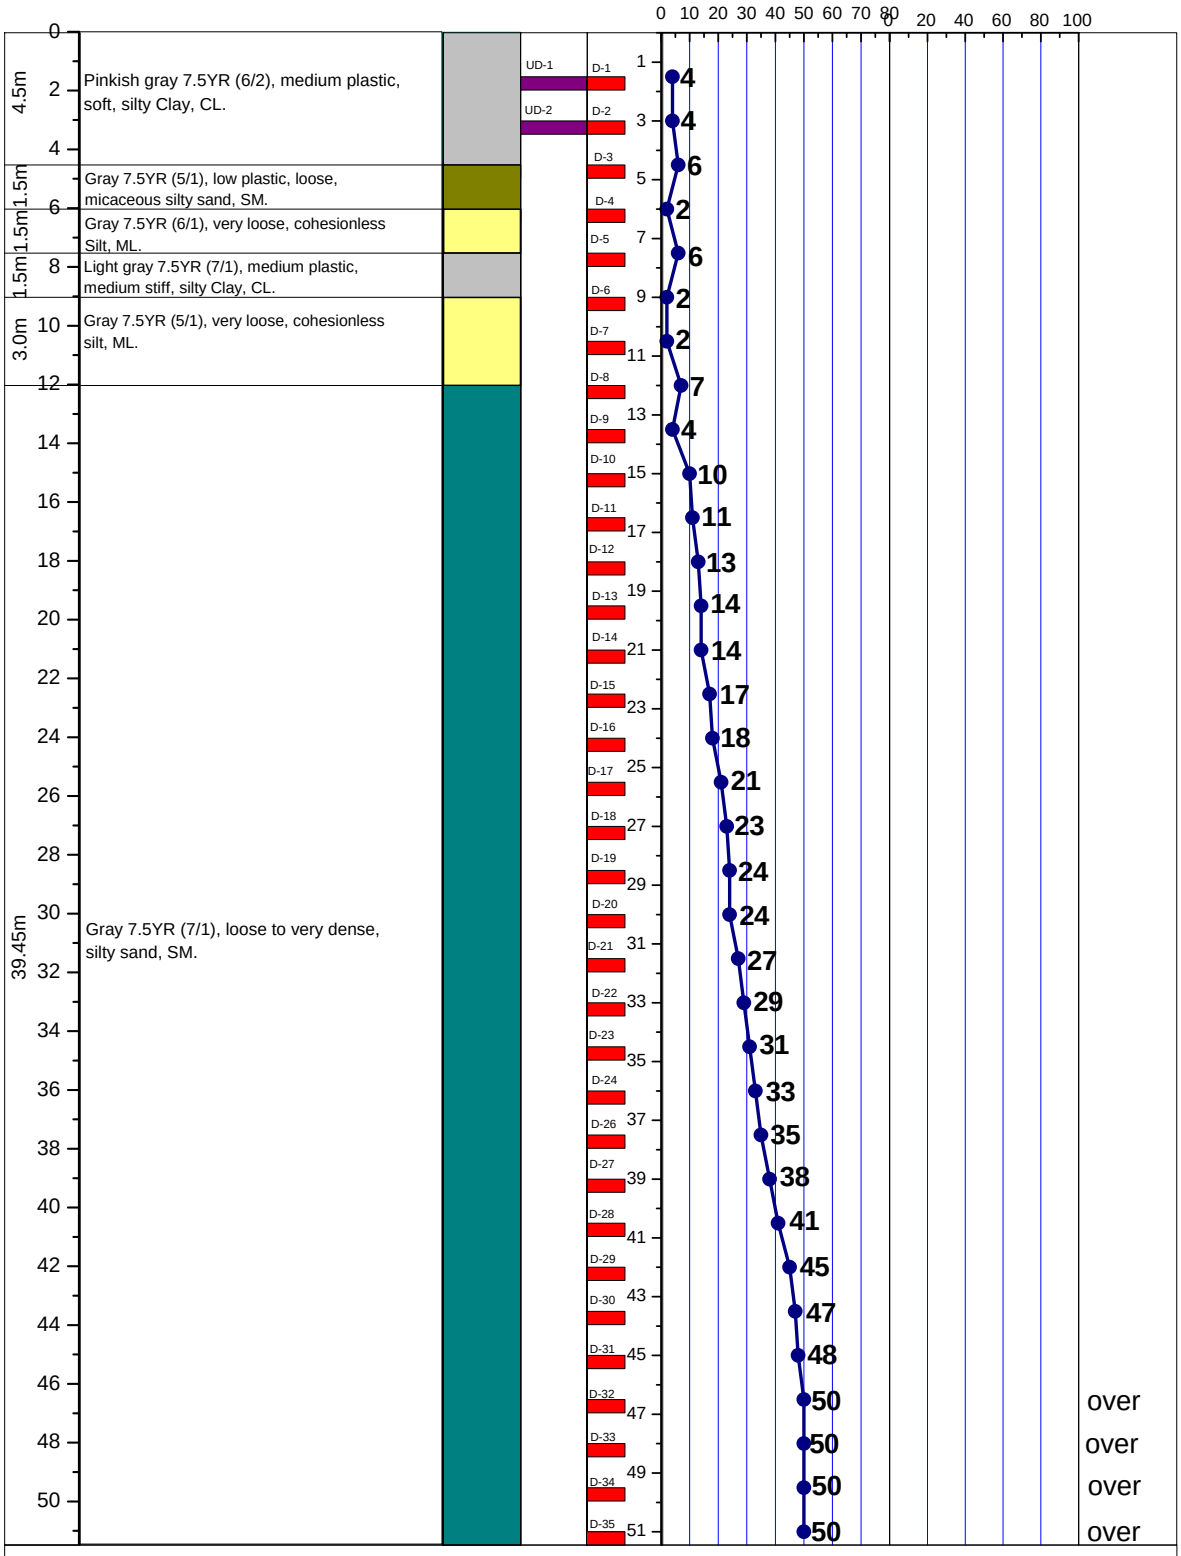


LEGEND FOR BORELOG AND GRAIN SIZE DISTRIBUTION (BASED ON 'ASTM CLASSIFICATION D-2487')

PLASTIC CLAY	SILT	PEAT/HIGHLY ORGANIC SOIL	UNDISTURBED SAMPLE
MICACEOUS FINE SAND/SILT	SAND	SHALE	DISTURBED SAMPLE

N- BLOWS DELIVERED PER FOOT BY A 140 LB HAMMER FALLING 30 INCHES

MAX^{m} PENETRATION= 50 BLOWS. AFTER 50 BLOWS PENETRATION DEPTH WERE MEASURED

A2	PROSOIL	BOREHOLE NO: BH-1	
		LOCATION : Jholon Pool, Mirershari, Chittagong.	
PROJECT : Telecommunication Tower.		DEPTH OF BORING : 51.0m	R. L.: Road Level.
CLIENT : AXIATA (Bangladesh) Ltd.		DATE OF BORING : 29-08-2009.	G. W. T : 1.22m below from E. G. L.

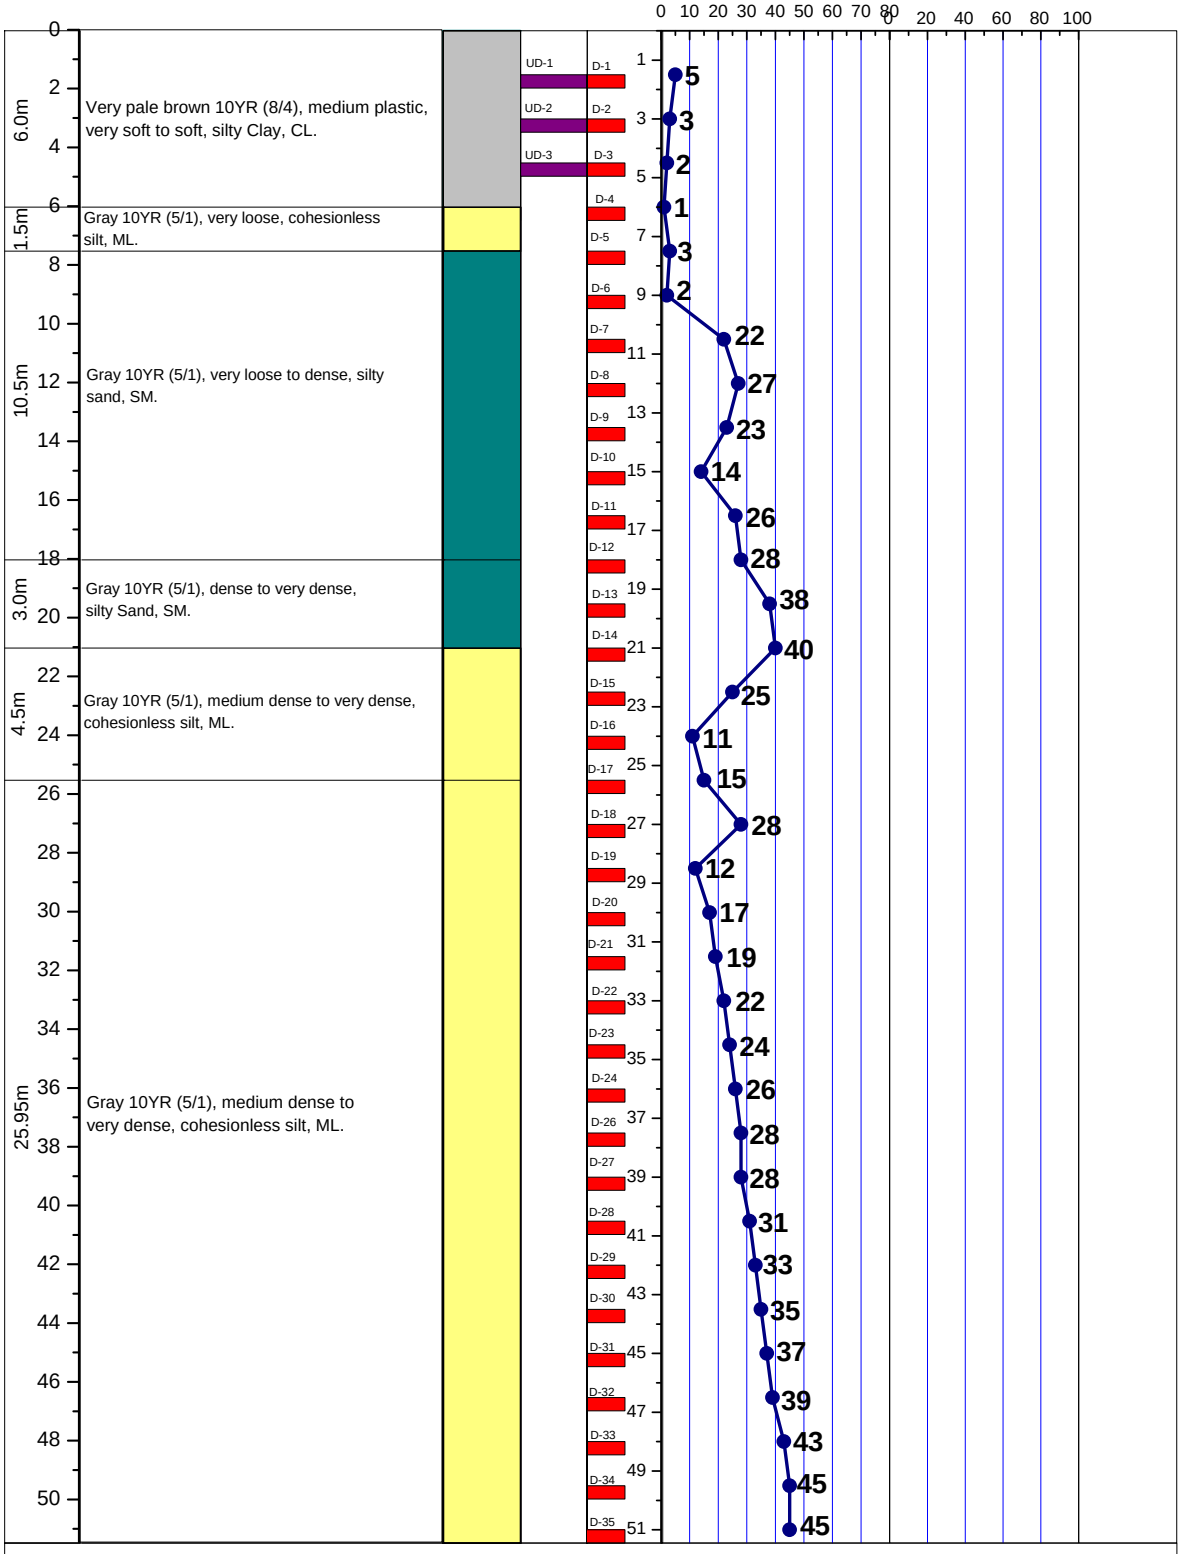


LEGEND FOR BORELOG AND GRAIN SIZE DISTRIBUTION (BASED ON 'ASTM CLASSIFICATION D-2487')

PLASTIC CLAY	SILT	PEAT/HIGHLY ORGANIC SOIL	UNDISTURBED SAMPLE
MICACEOUS FINE SAND/SILT	SAND	SHALE	DISTURBED SAMPLE

N- BLOWS DELIVERED PER FOOT BY A 140 LB HAMMER FALLING 30 INCHES

MAX^{m} PENETRATION= 50 BLOWS. AFTER 50 BLOWS PENETRATION DEPTH WERE MEASURED

A2	PROSOIL	BOREHOLE NO: BH-1	
		LOCATION : Middle Mayani, Mirsarai, Chittagong.	
PROJECT : Telecommunication Tower.		DEPTH OF BORING : 51.0m	R. L.: 0.81m below from Road Level.
CLIENT : AXIATA (Bangladesh) Ltd.		DATE OF BORING : 27-03-2010.	G. W. T : 2.44m below from E. G. L.

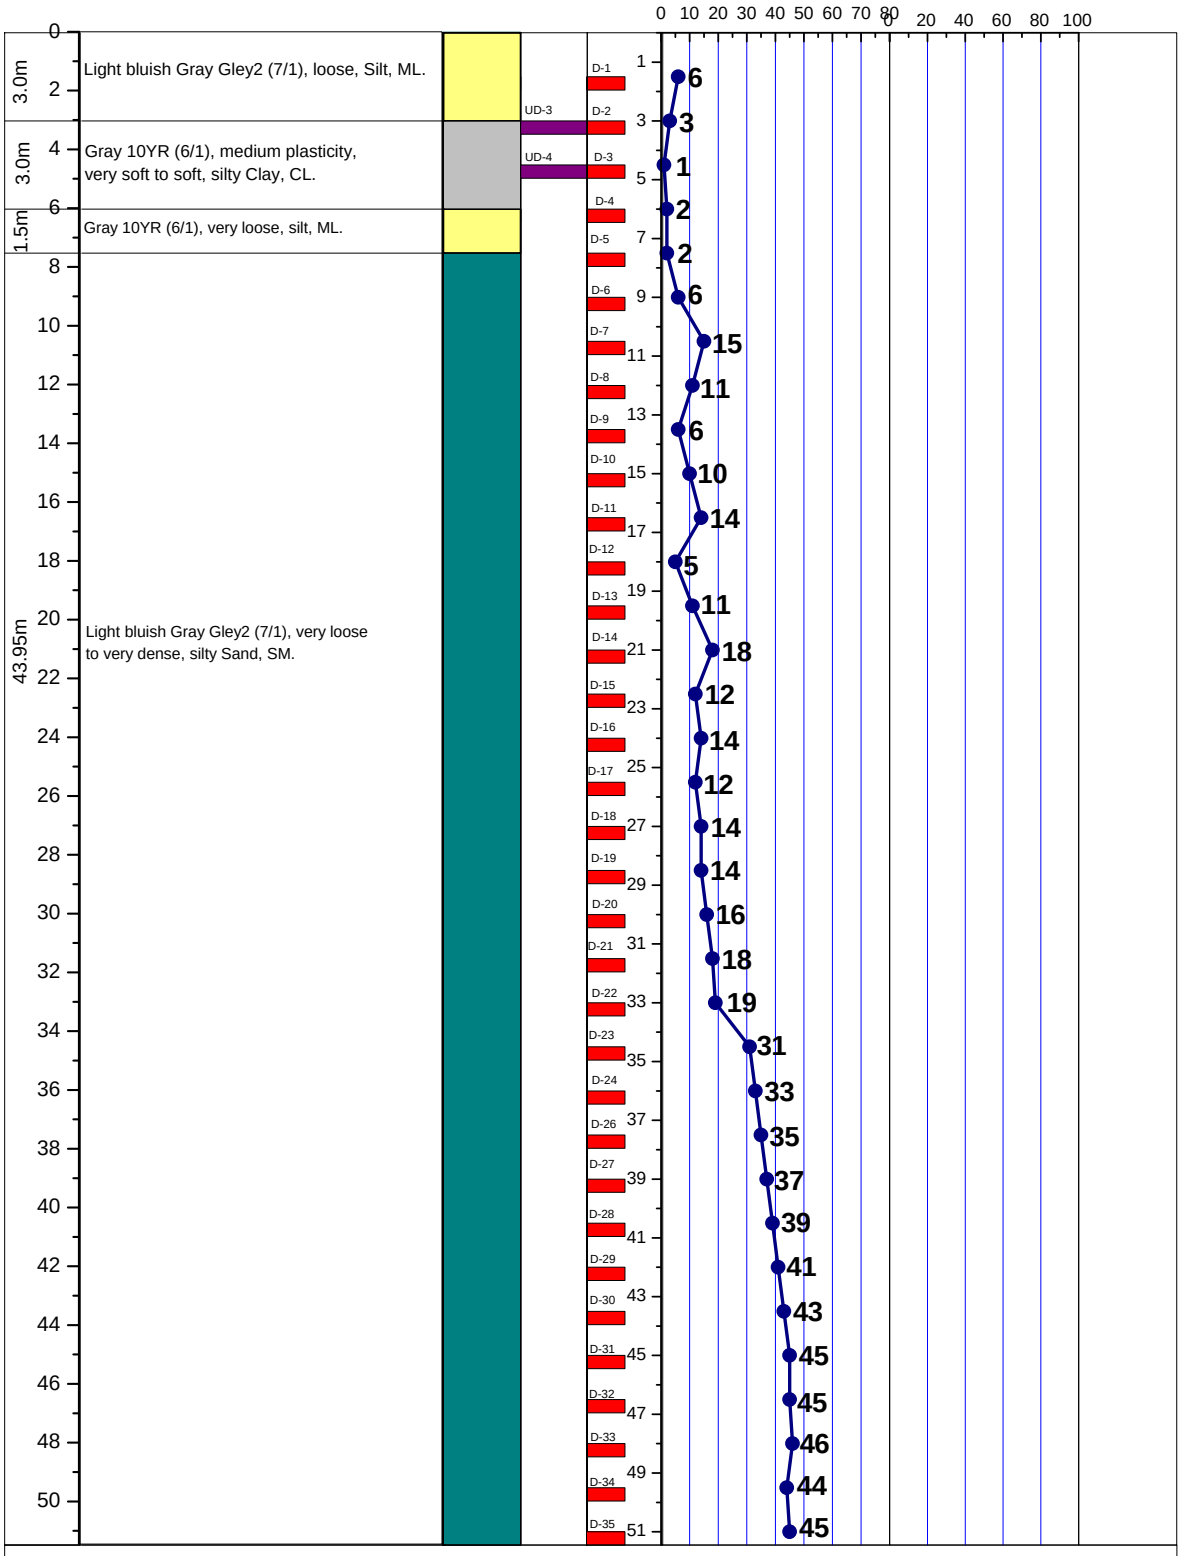


LEGEND FOR BORELOG AND GRAIN SIZE DISTRIBUTION (BASED ON 'ASTM CLASSIFICATION D-2487')

PLASTIC CLAY	SILT	PEAT/HIGHLY ORGANIC SOIL	UNDISTURBED SAMPLE
MICACEOUS FINE SAND/SILT	SAND	SHALE	DISTURBED SAMPLE

N- BLOWS DELIVERED PER FOOT BY A 140 LB HAMMER FALLING 30 INCHES

MAX^{m} PENETRATION= 50 BLOWS. AFTER 50 BLOWS PENETRATION DEPTH WERE MEASURED

A2 PROSOIL	BOREHOLE NO: BH-1	
	LOCATION : Mirzarhat 2, West Bhujpur, Bhujpur, Fatikchari, Chittagong.	
PROJECT : Telecommunication Tower.	DEPTH OF BORING : 51.0m	R. L.: 1.22m below from Road Level.
CLIENT : AXIATA (Bangladesh) Ltd.	DATE OF BORING : 20-12-2012.	G. W. T : 0.91m below from E. G. L.

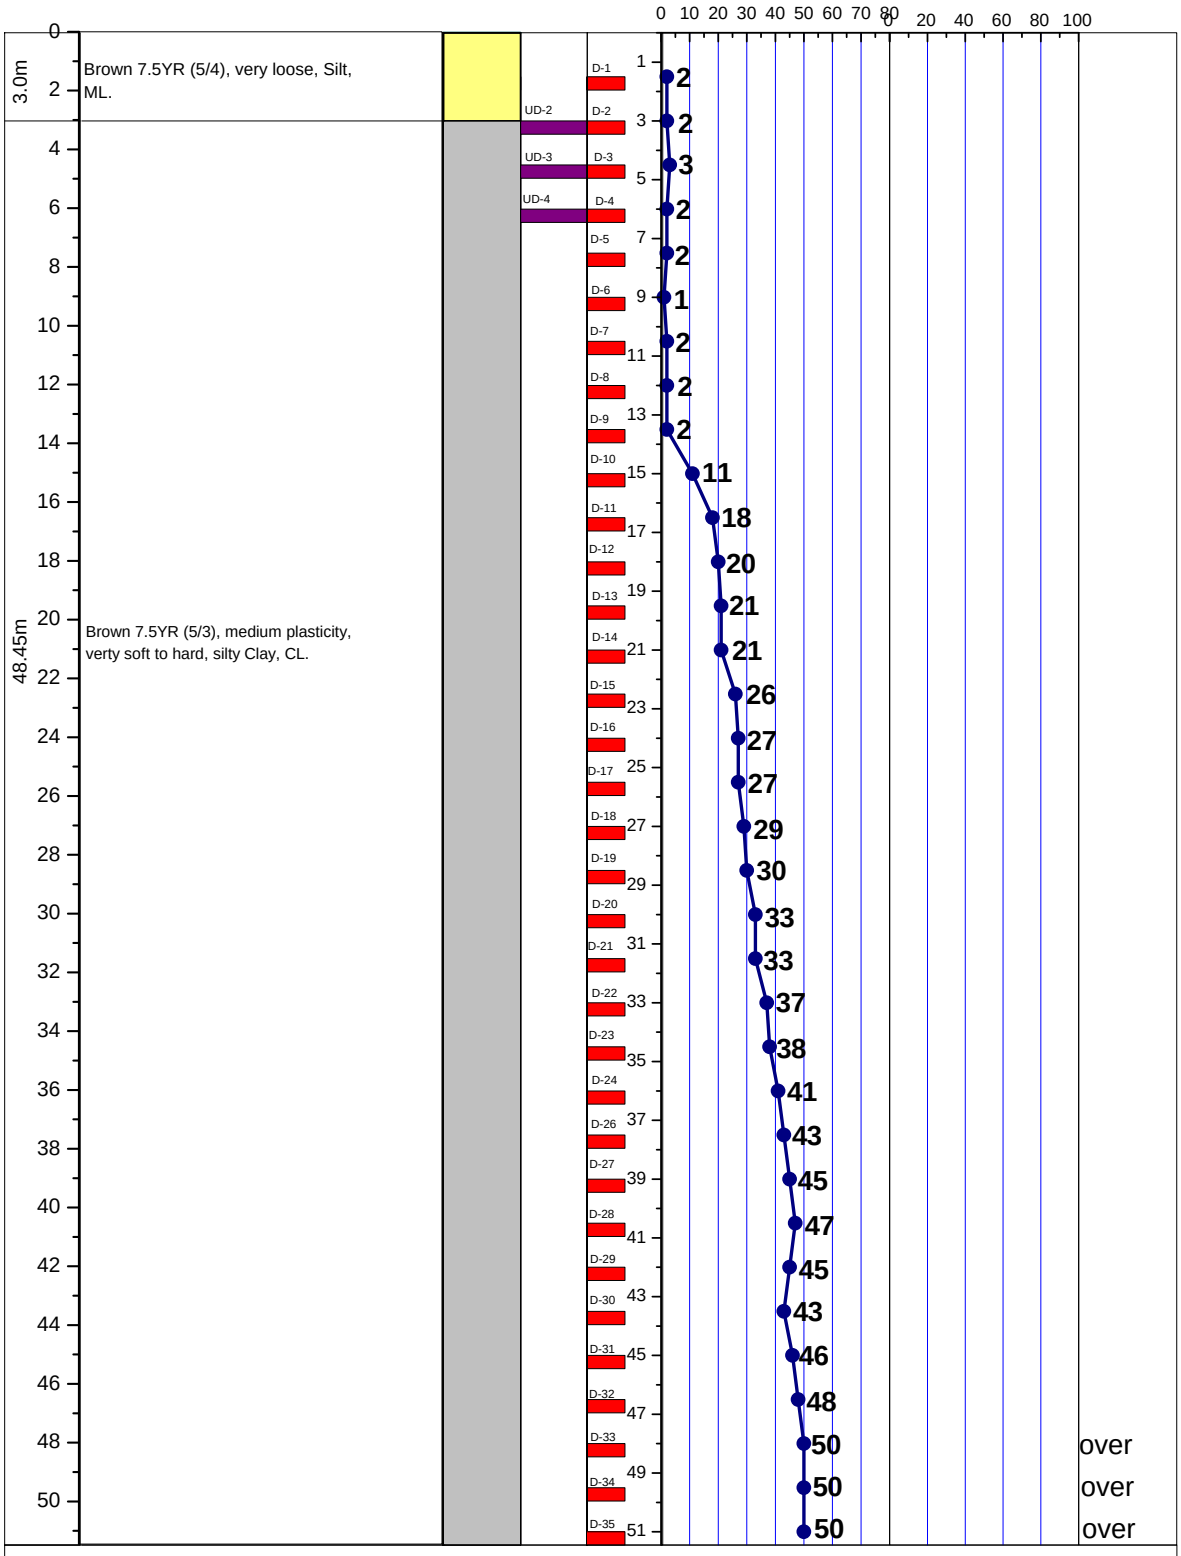


LEGEND FOR BORELOG AND GRAIN SIZE DISTRIBUTION (BASED ON 'ASTM CLASSIFICATION D-2487')

PLASTIC CLAY	SILT	PEAT/HIGHLY ORGANIC SOIL	UNDISTURBED SAMPLE
MICACEOUS FINE SAND/SILT	SAND	SHALE	DISTURBED SAMPLE

N- BLOWS DELIVERED PER FOOT BY A 140 LB HAMMER FALLING 30 INCHES

MAX^{m} PENETRATION= 50 BLOWS. AFTER 50 BLOWS PENETRATION DEPTH WERE MEASURED

A2 PROSOIL	BOREHOLE NO: BH-1	
	LOCATION : Mithanala, Mithanala High School, Mirersharai, Chittagong.	
PROJECT : Telecommunication Tower.	DEPTH OF BORING : 51.0m	R. L.: On Road Level.
CLIENT : AXIATA (Bangladesh) Ltd.	DATE OF BORING : 24-11-2011.	G. W. T : 3.05m below from E. G. L.

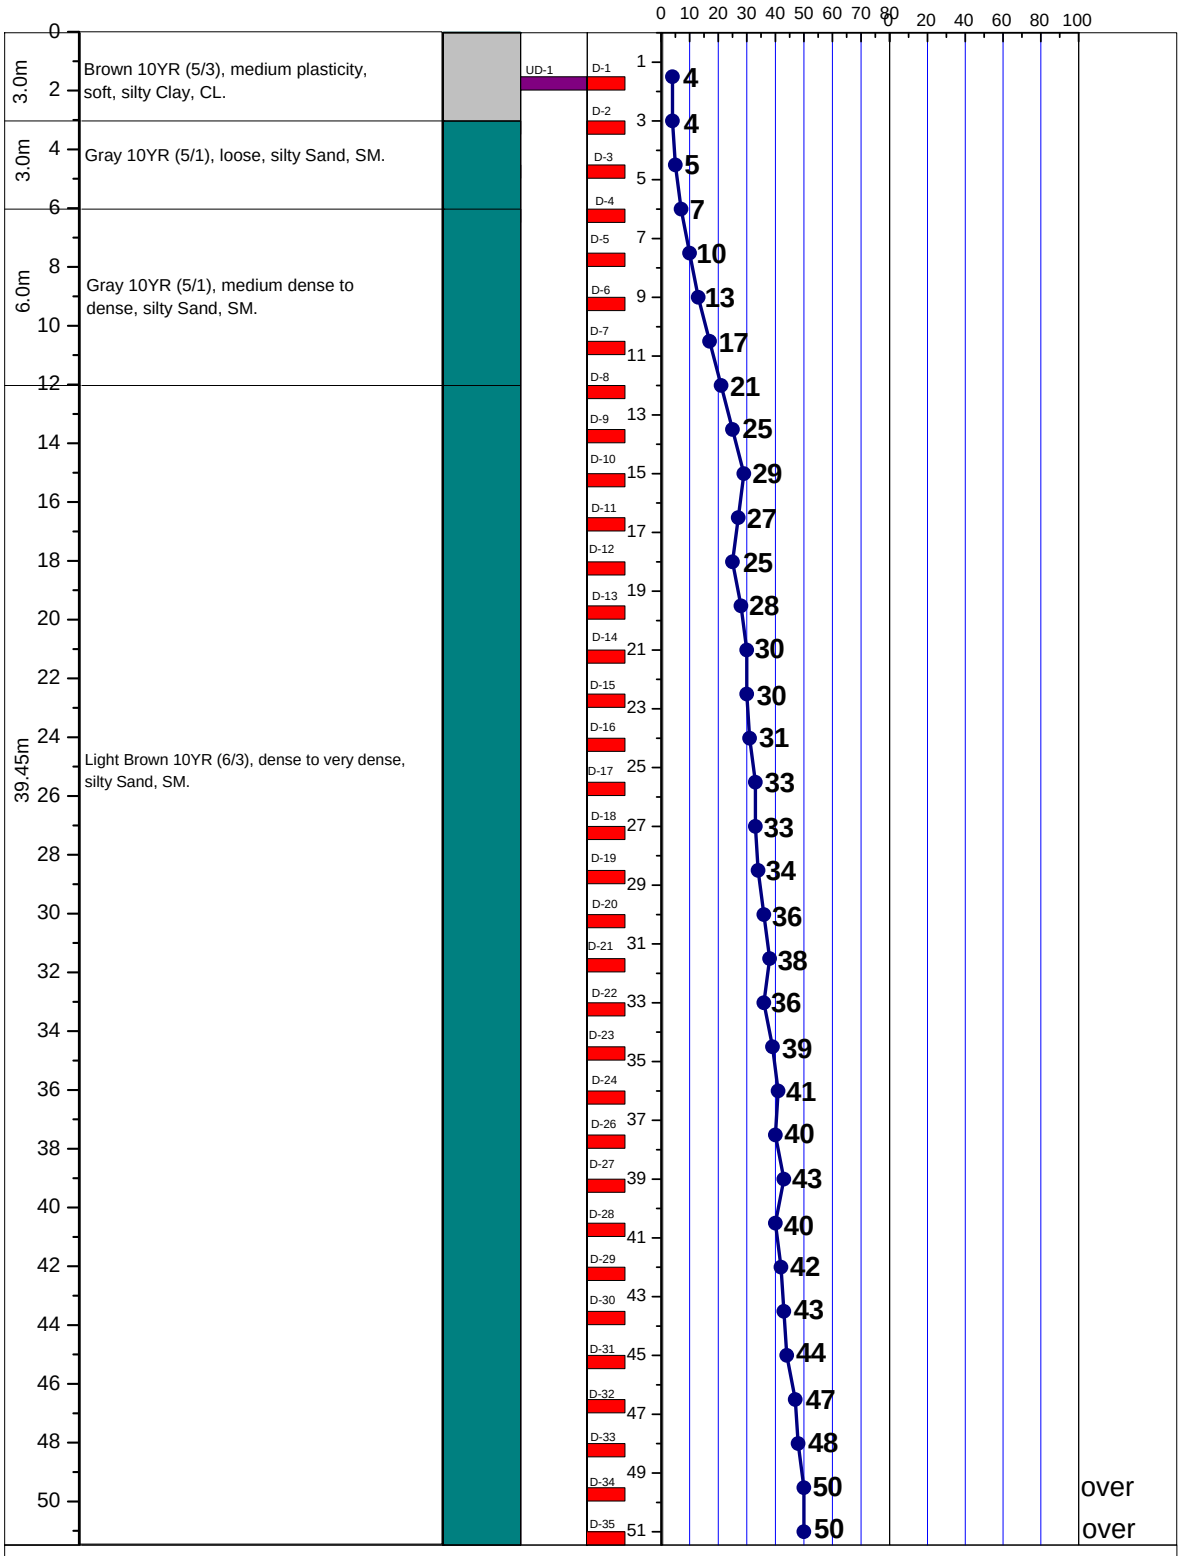


LEGEND FOR BORELOG AND GRAIN SIZE DISTRIBUTION (BASED ON 'ASTM CLASSIFICATION D-2487')

PLASTIC CLAY	SILT	PEAT/HIGHLY ORGANIC SOIL	UNDISTURBED SAMPLE
MICACEOUS FINE SAND/SILT	SAND	SHALE	DISTURBED SAMPLE

N- BLOWS DELIVERED PER FOOT BY A 140 LB HAMMER FALLING 30 INCHES

MAX^{m} PENETRATION= 50 BLOWS. AFTER 50 BLOWS PENETRATION DEPTH WERE MEASURED

A2 PROSOIL	BOREHOLE NO: BH-1	
	LOCATION : Moghai Chori, Rangunia, Chittagong.	
PROJECT : Telecommunication Tower.	DEPTH OF BORING : 51.0m	R. L.: 1.82m below from Road Level.
CLIENT : TM International, Bangladesh Ltd.	DATE OF BORING : 05-02-2009.	G. W. T : 1.52m below from E. G. L.

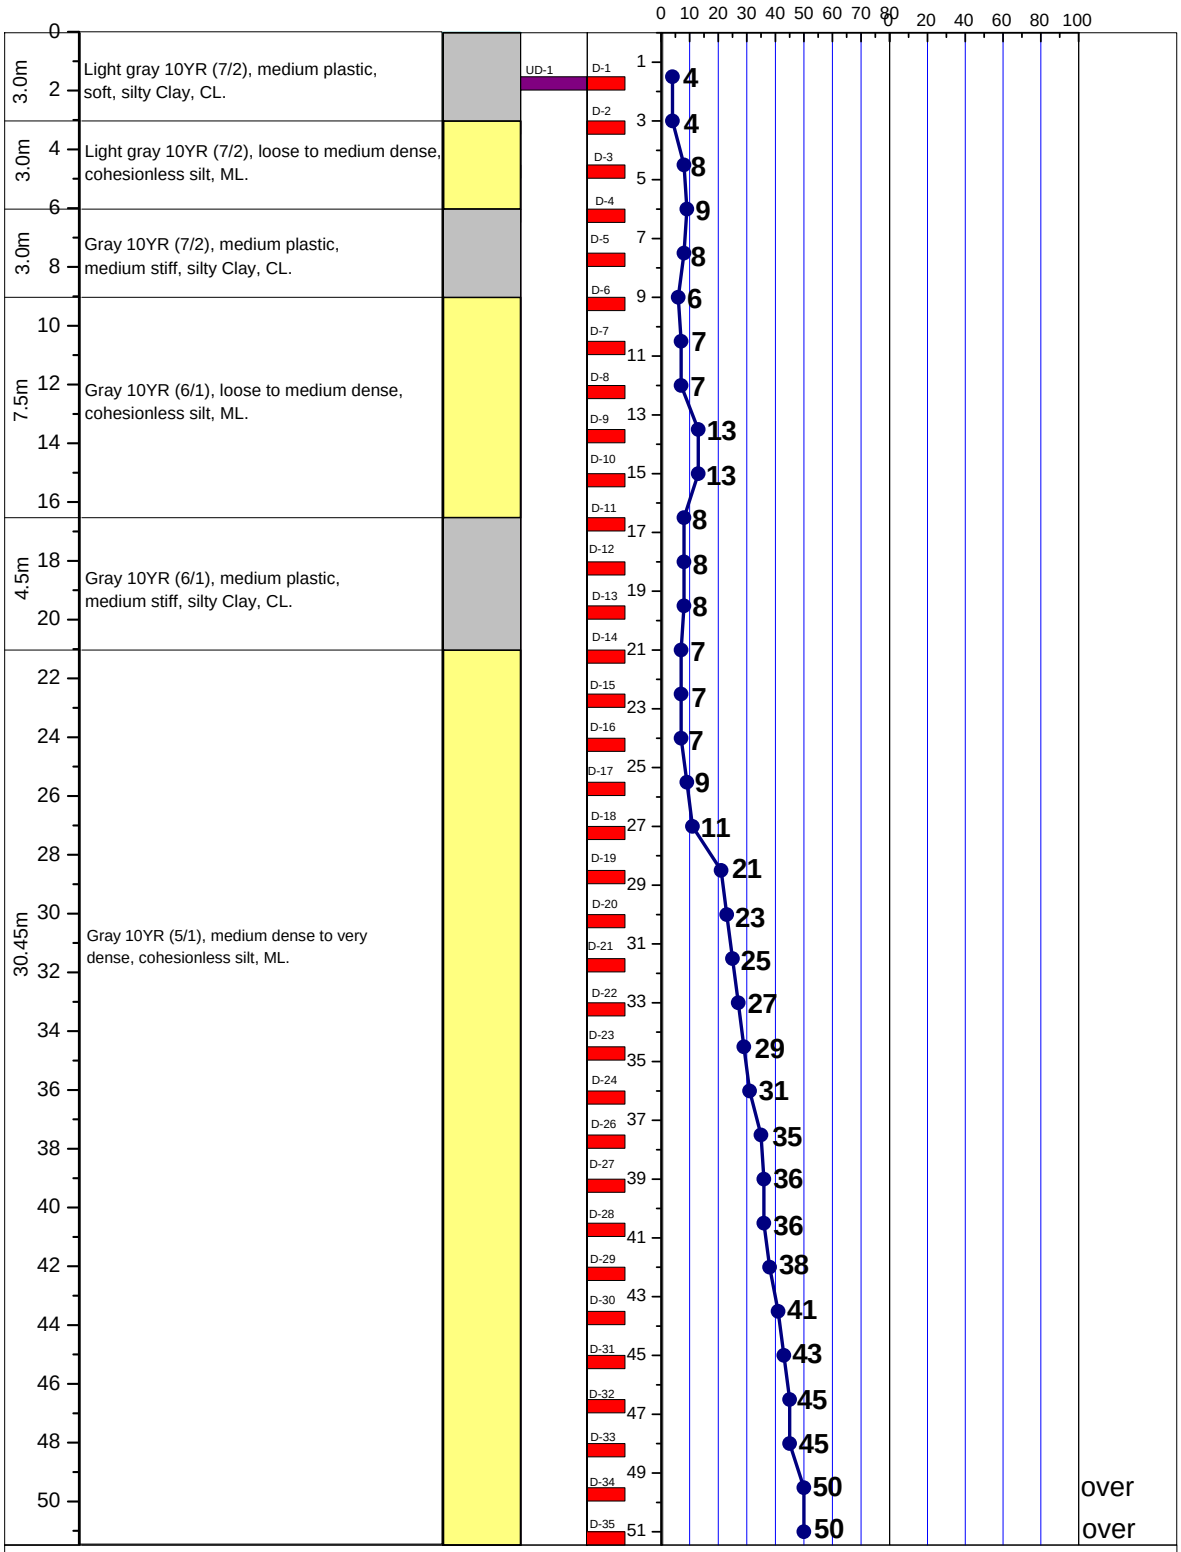


LEGEND FOR BORELOG AND GRAIN SIZE DISTRIBUTION (BASED ON 'ASTM CLASSIFICATION D-2487')

PLASTIC CLAY	SILT	PEAT/HIGHLY ORGANIC SOIL	UNDISTURBED SAMPLE
MICACEOUS FINE SAND/SILT	SAND	SHALE	DISTURBED SAMPLE

N- BLOWS DELIVERED PER FOOT BY A 140 LB HAMMER FALLING 30 INCHES

MAX^{m} PENETRATION= 50 BLOWS. AFTER 50 BLOWS PENETRATION DEPTH WERE MEASURED

A2 PROSOIL	BOREHOLE NO: BH-1	
	LOCATION : Moulanagram 2, South Sharaf Bhata, Mararkhil, Sharaf Bhata, Rangunia, Chittagong.	
PROJECT : Telecommunication Tower.	DEPTH OF BORING : 51.0m	R. L.: 0.91m below from Road Level.
CLIENT : AXIATA (Bangladesh) Ltd.	DATE OF BORING : 02-01-2013.	G. W. T : 2.44m below from E. G. L.

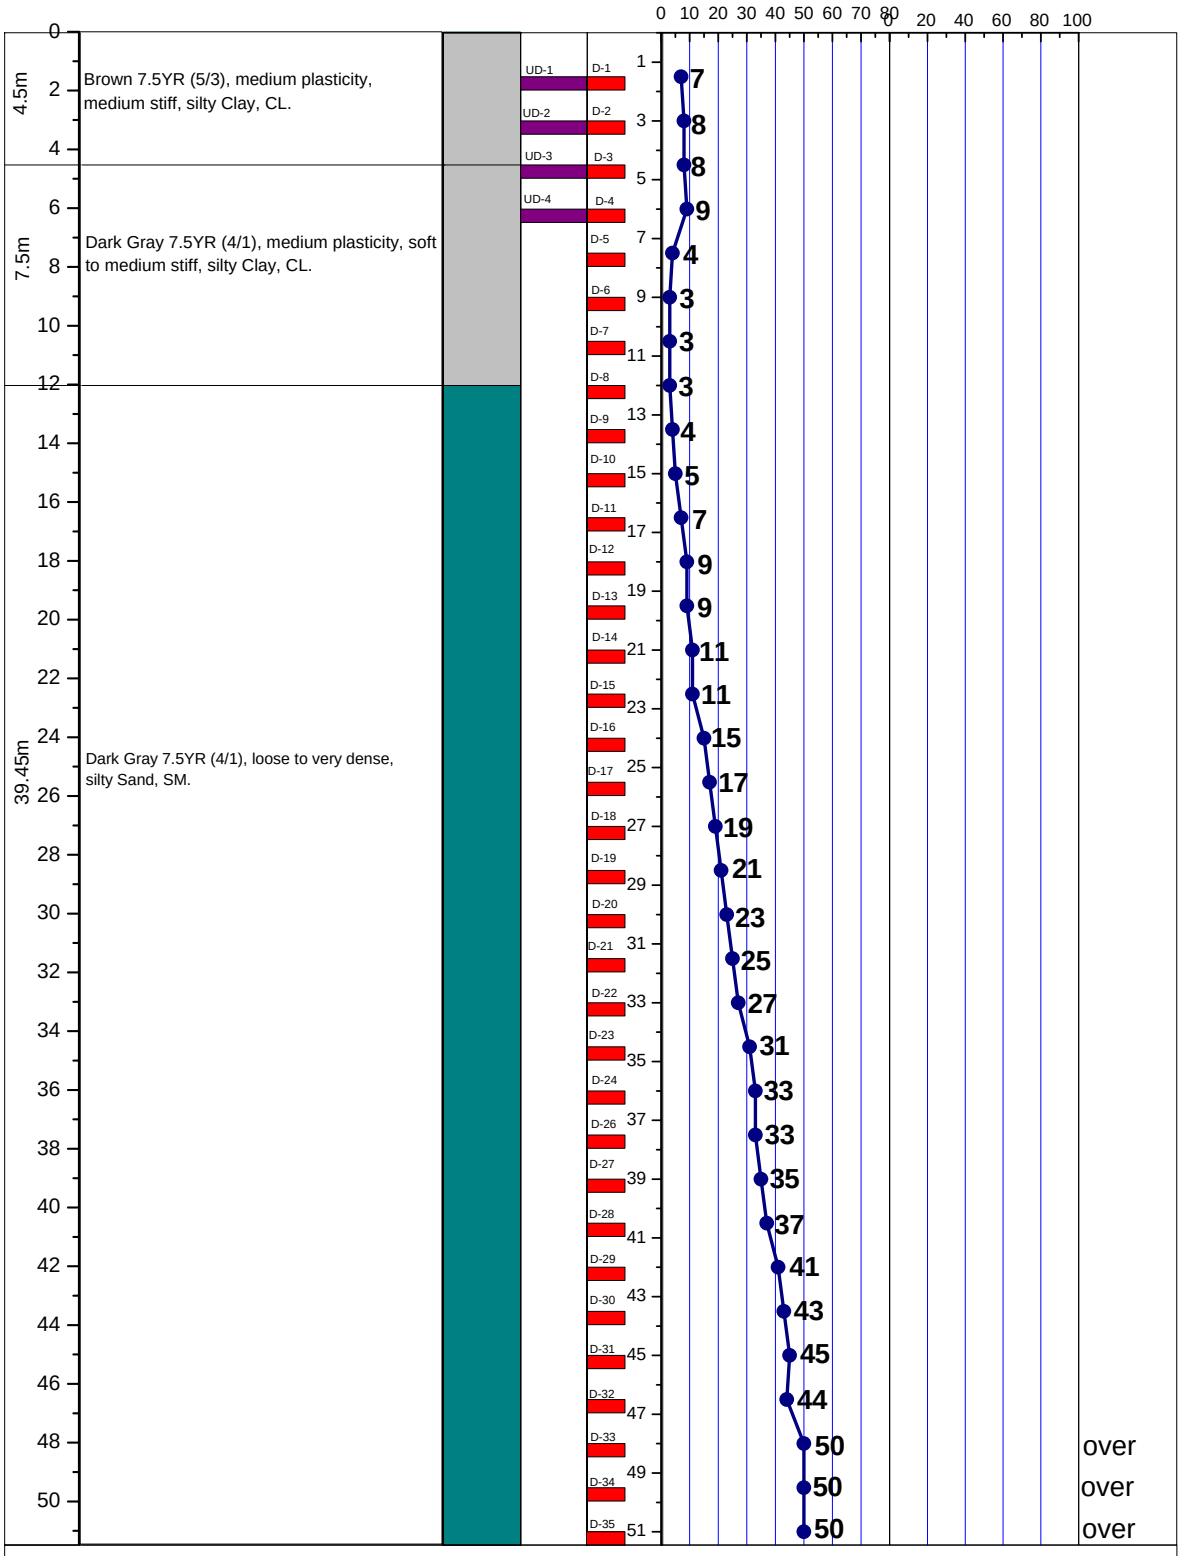


LEGEND FOR BORELOG AND GRAIN SIZE DISTRIBUTION (BASED ON 'ASTM CLASSIFICATION D-2487')

PLASTIC CLAY	SILT	PEAT/HIGHLY ORGANIC SOIL	UNDISTURBED SAMPLE
MICACEOUS FINE SAND/SILT	SAND	SHALE	DISTURBED SAMPLE

N- BLOWS DELIVERED PER FOOT BY A 140 LB HAMMER FALLING 30 INCHES

MAX^{m} PENETRATION= 50 BLOWS. AFTER 50 BLOWS PENETRATION DEPTH WERE MEASURED

A2 PROSOIL	BOREHOLE NO: BH-1	
	LOCATION : Mounsipara, Hathazari, Chittagong.	
PROJECT : Telecommunication Tower.	DEPTH OF BORING : 51.0m	R. L.: 0.40m below from Road Level.
CLIENT : AXIATA (Bangladesh) Ltd.	DATE OF BORING : 12-04-2011.	G. W. T : 1.22m below from E. G. L.

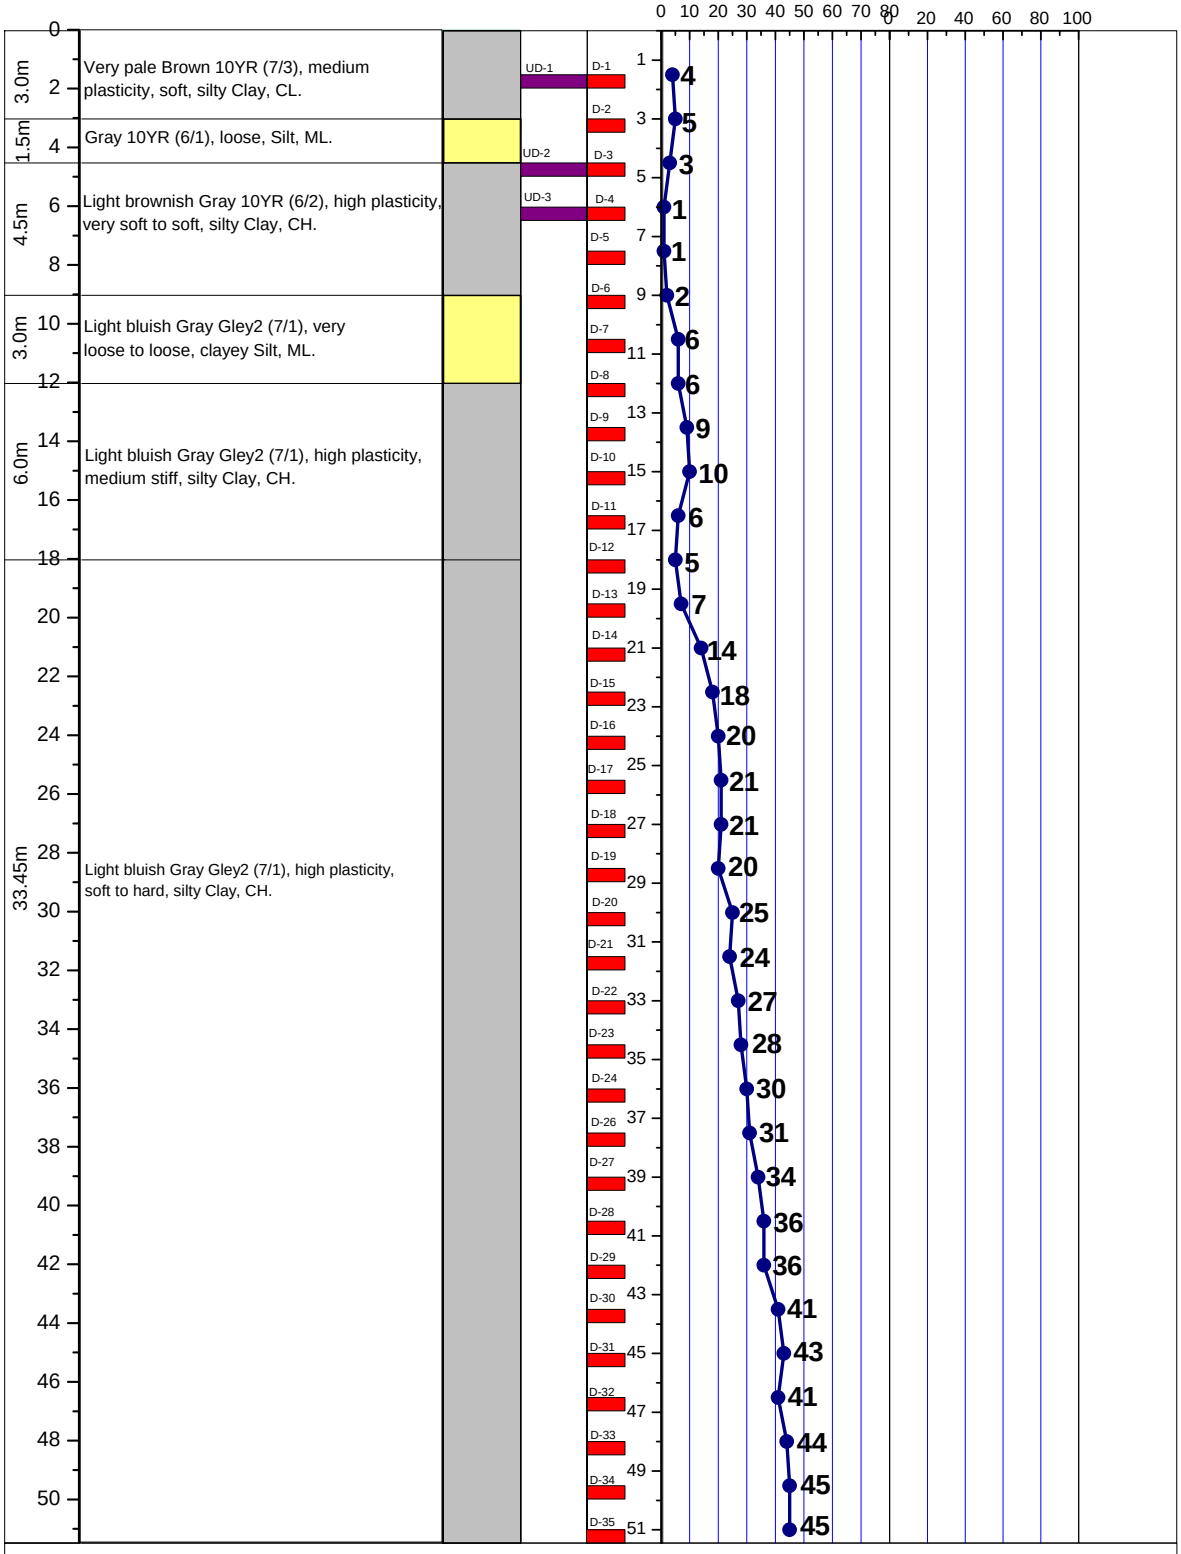


LEGEND FOR BORELOG AND GRAIN SIZE DISTRIBUTION (BASED ON 'ASTM CLASSIFICATION D-2487')

PLASTIC CLAY	SILT	PEAT/HIGHLY ORGANIC SOIL	UNDISTURBED SAMPLE
MICACEOUS FINE SAND/SILT	SAND	SHALE	DISTURBED SAMPLE

N- BLOWS DELIVERED PER FOOT BY A 140 LB HAMMER FALLING 30 INCHES

MAX^{m} PENETRATION= 50 BLOWS. AFTER 50 BLOWS PENETRATION DEPTH WERE MEASURED

A2 PROSOIL	BOREHOLE NO: BH-1	
	LOCATION : Nazirhat, Bawria, Sandip, Chittagong.	
PROJECT : Telecommunication Tower.	DEPTH OF BORING : 51.0m	R. L.: 0.76m below from Road Level.
CLIENT : AXIATA (Bangladesh) Ltd.	DATE OF BORING : 25-11-2011.	G. W. T : 2.16m below from E. G. L.

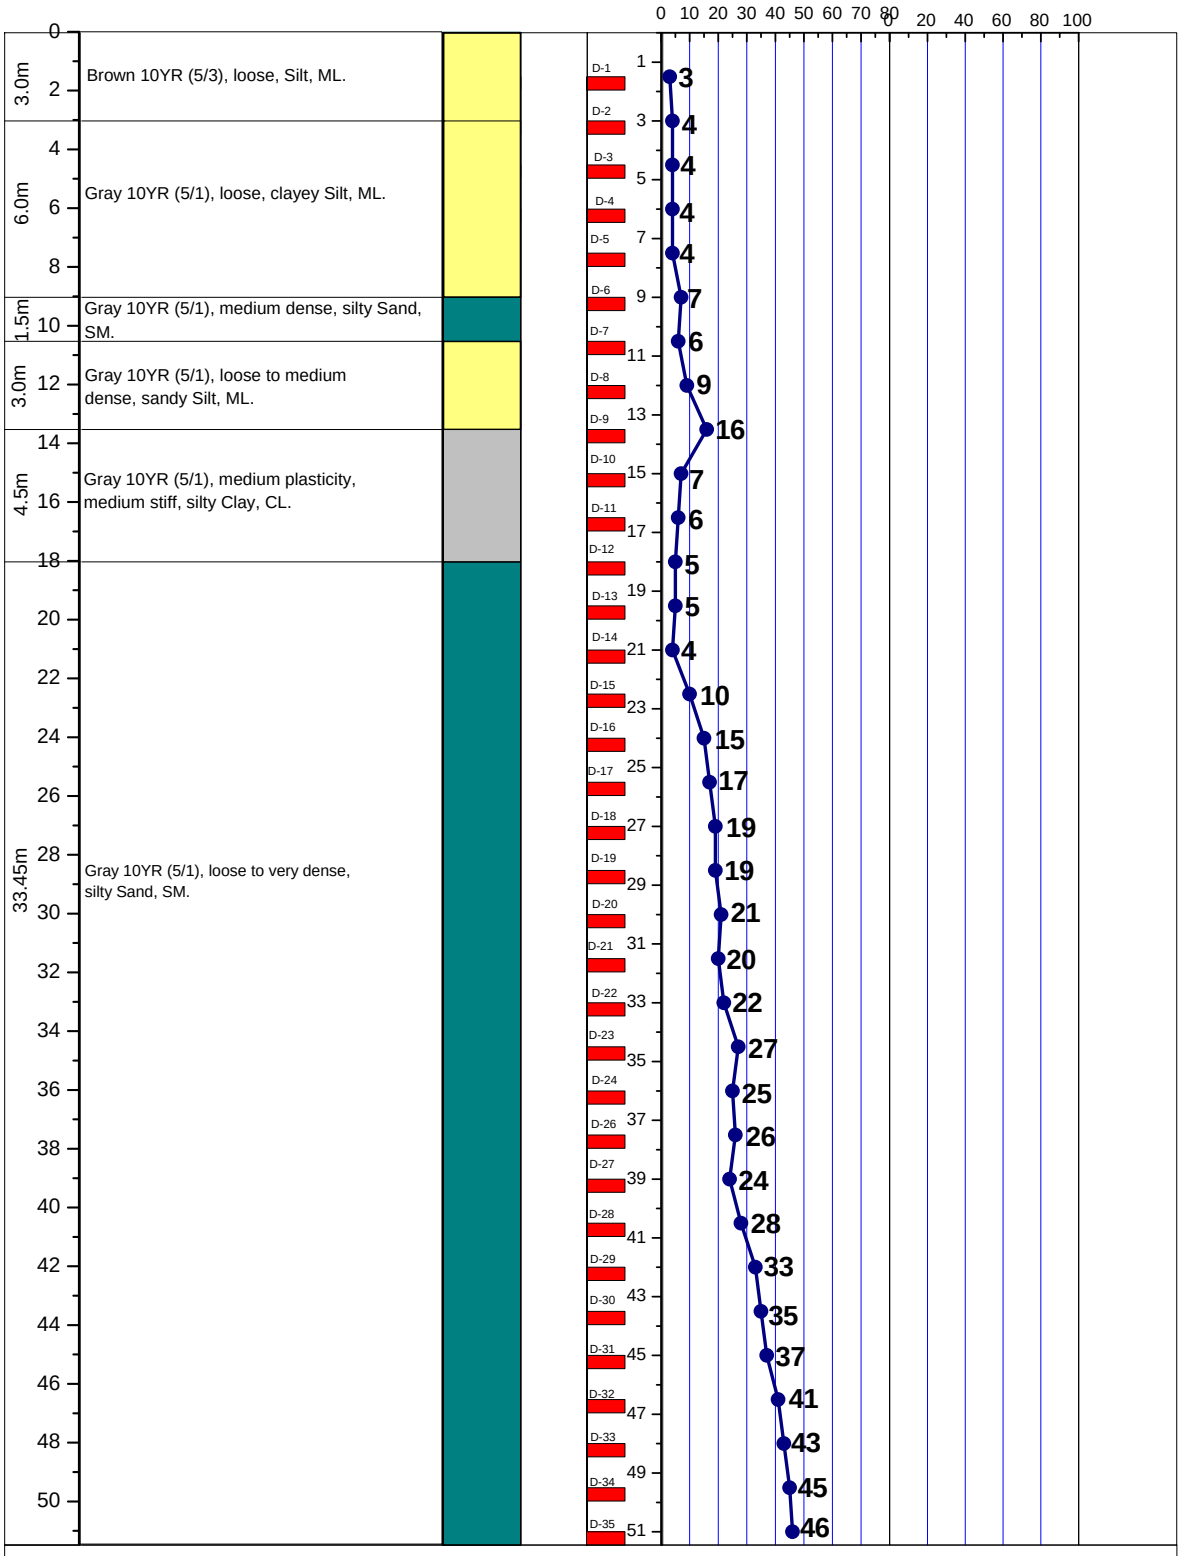


LEGEND FOR BORELOG AND GRAIN SIZE DISTRIBUTION (BASED ON 'ASTM CLASSIFICATION D-2487')

PLASTIC CLAY	SILT	PEAT/HIGHLY ORGANIC SOIL	UNDISTURBED SAMPLE
MICACEOUS FINE SAND/SILT	SAND	SHALE	DISTURBED SAMPLE

N- BLOWS DELIVERED PER FOOT BY A 140 LB HAMMER FALLING 30 INCHES

MAX^{m} PENETRATION= 50 BLOWS. AFTER 50 BLOWS PENETRATION DEPTH WERE MEASURED

A2 PROSOIL	BOREHOLE NO: BH-1	
	LOCATION : Palishar Bazar 25m land, Sandwip, Chittagong.	
PROJECT : Telecommunication Tower.	DEPTH OF BORING : 51.0m	R. L.: 0.50m above from Road Level.
CLIENT : AXIATA (Bangladesh) Ltd.	DATE OF BORING : 13-10-2009.	G. W. T : 0.60m below from E. G. L.

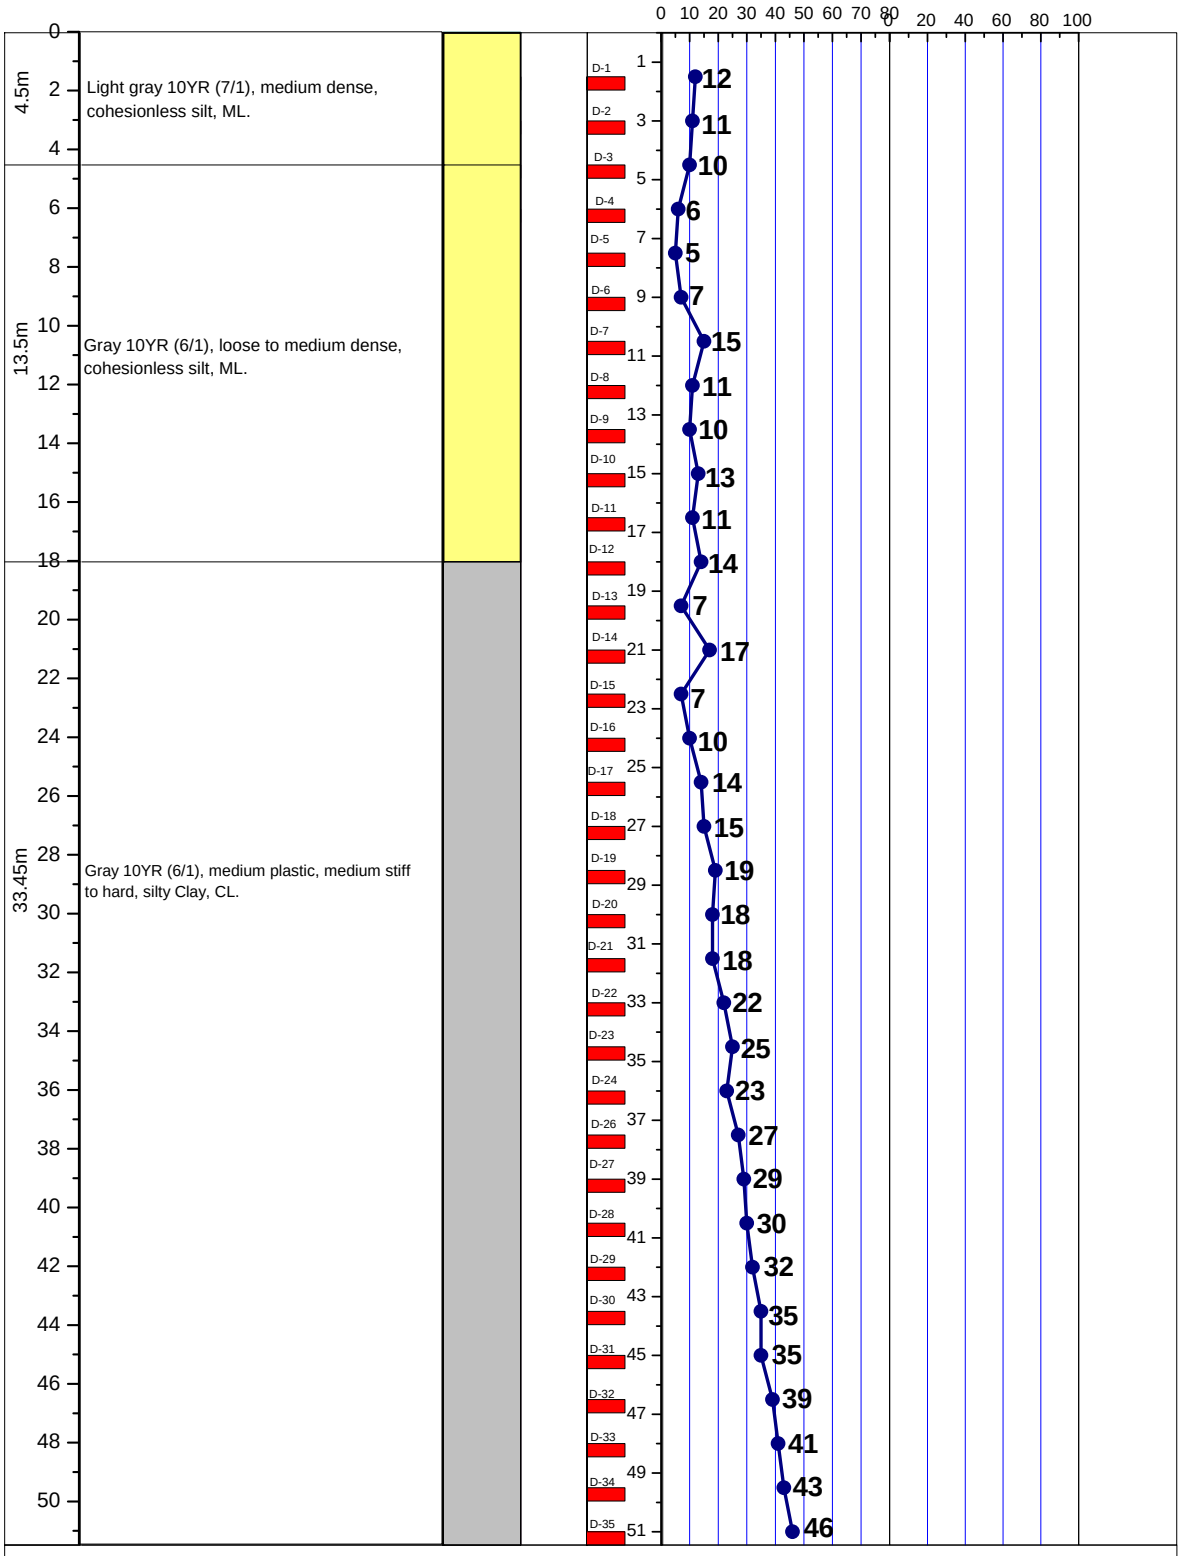


LEGEND FOR BORELOG AND GRAIN SIZE DISTRIBUTION (BASED ON 'ASTM CLASSIFICATION D-2487')

PLASTIC CLAY	SILT	PEAT/HIGHLY ORGANIC SOIL	UNDISTURBED SAMPLE
MICACEOUS FINE SAND/SILT	SAND	SHALE	DISTURBED SAMPLE

N- BLOWS DELIVERED PER FOOT BY A 140 LB HAMMER FALLING 30 INCHES

MAX^{m} PENETRATION= 50 BLOWS. AFTER 50 BLOWS PENETRATION DEPTH WERE MEASURED

A2	PROSOIL	BOREHOLE NO: BH-1	
		LOCATION : Raja Rastar Matha, Fatikchari, Chittagong.	
PROJECT : Telecommunication Tower.		DEPTH OF BORING : 51.0m	R. L.: 0.91m below from Road Level.
CLIENT : AXIATA (Bangladesh) Ltd.		DATE OF BORING : 27-09-2010.	G. W. T : Rain Water.

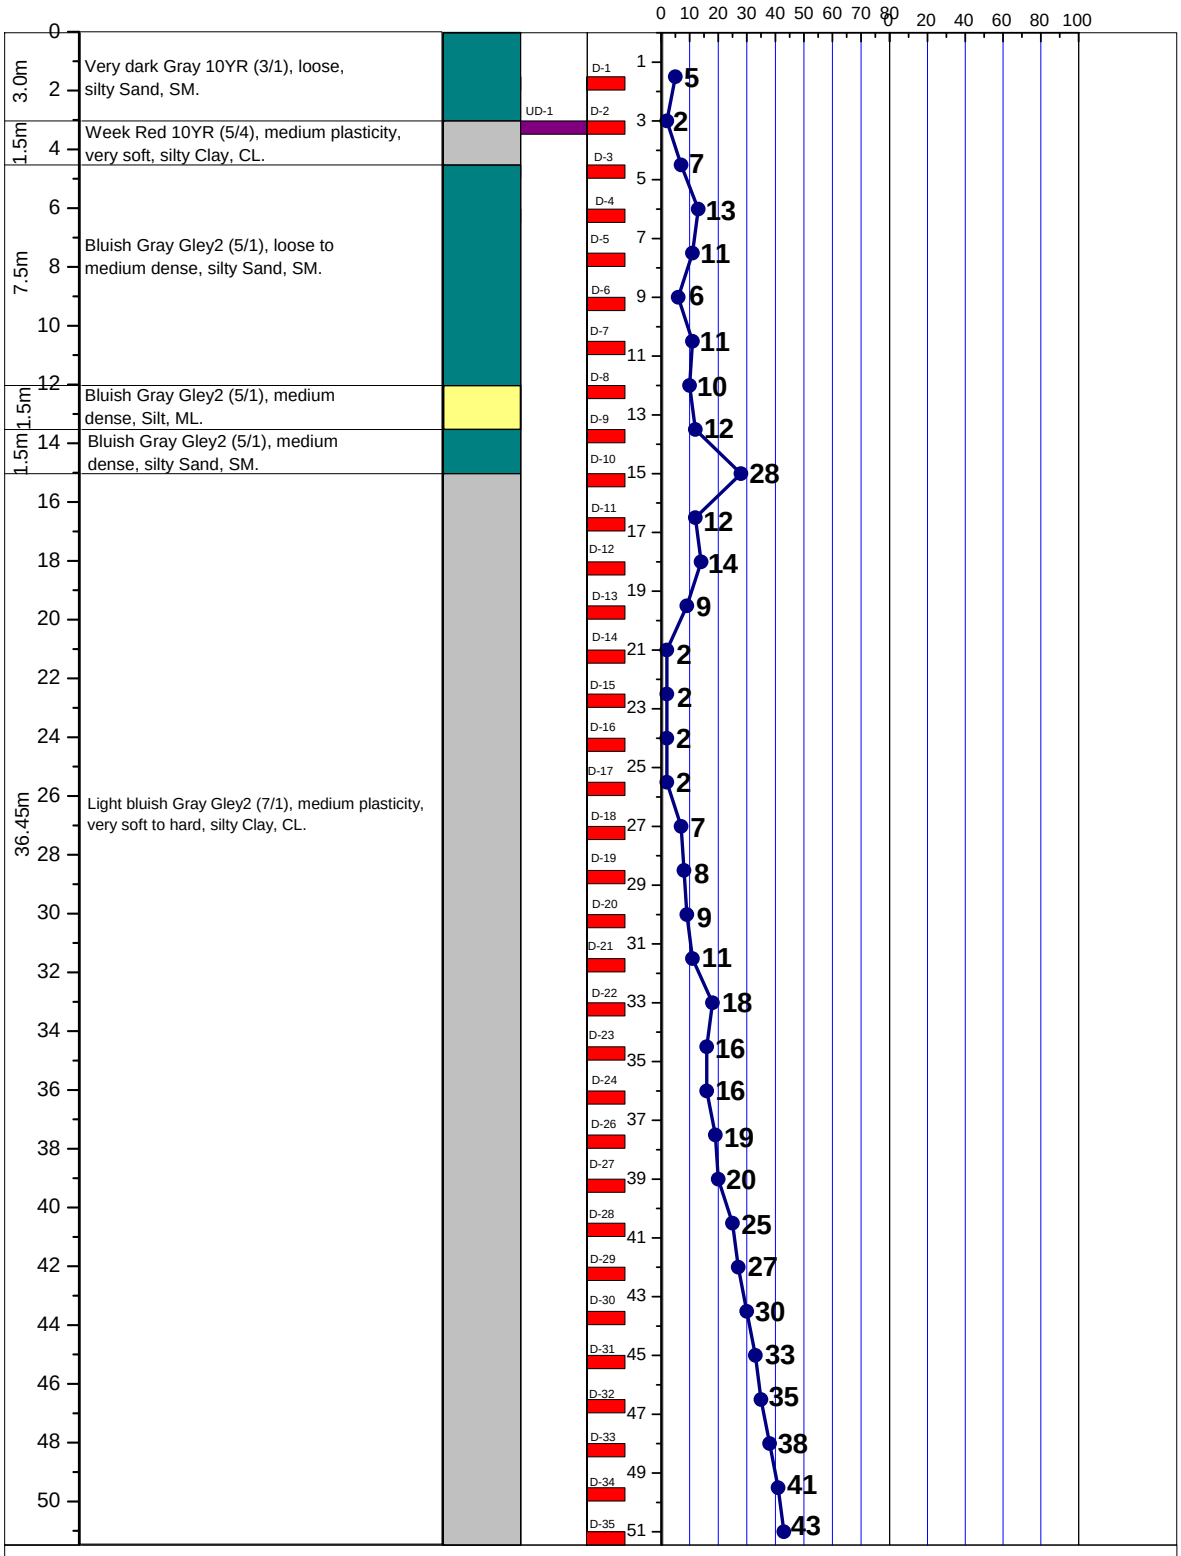


LEGEND FOR BORELOG AND GRAIN SIZE DISTRIBUTION (BASED ON 'ASTM CLASSIFICATION D-2487')

PLASTIC CLAY	SILT	PEAT/HIGHLY ORGANIC SOIL	UNDISTURBED SAMPLE
MICACEOUS FINE SAND/SILT	SAND	SHALE	DISTURBED SAMPLE

N- BLOWS DELIVERED PER FOOT BY A 140 LB HAMMER FALLING 30 INCHES

MAX^{m} PENETRATION= 50 BLOWS. AFTER 50 BLOWS PENETRATION DEPTH WERE MEASURED

A2	PROSOIL	BOREHOLE NO: BH-1	
		LOCATION : Rangamatia 3, Fatikchari, Chittagong.	
PROJECT : Telecommunication Tower.		DEPTH OF BORING : 51.0m	R. L.: 0.46m below from Road Level.
CLIENT : AXIATA (Bangladesh) Ltd.		DATE OF BORING : 13-04-2011.	G. W. T : 1.52m below from E. G. L.

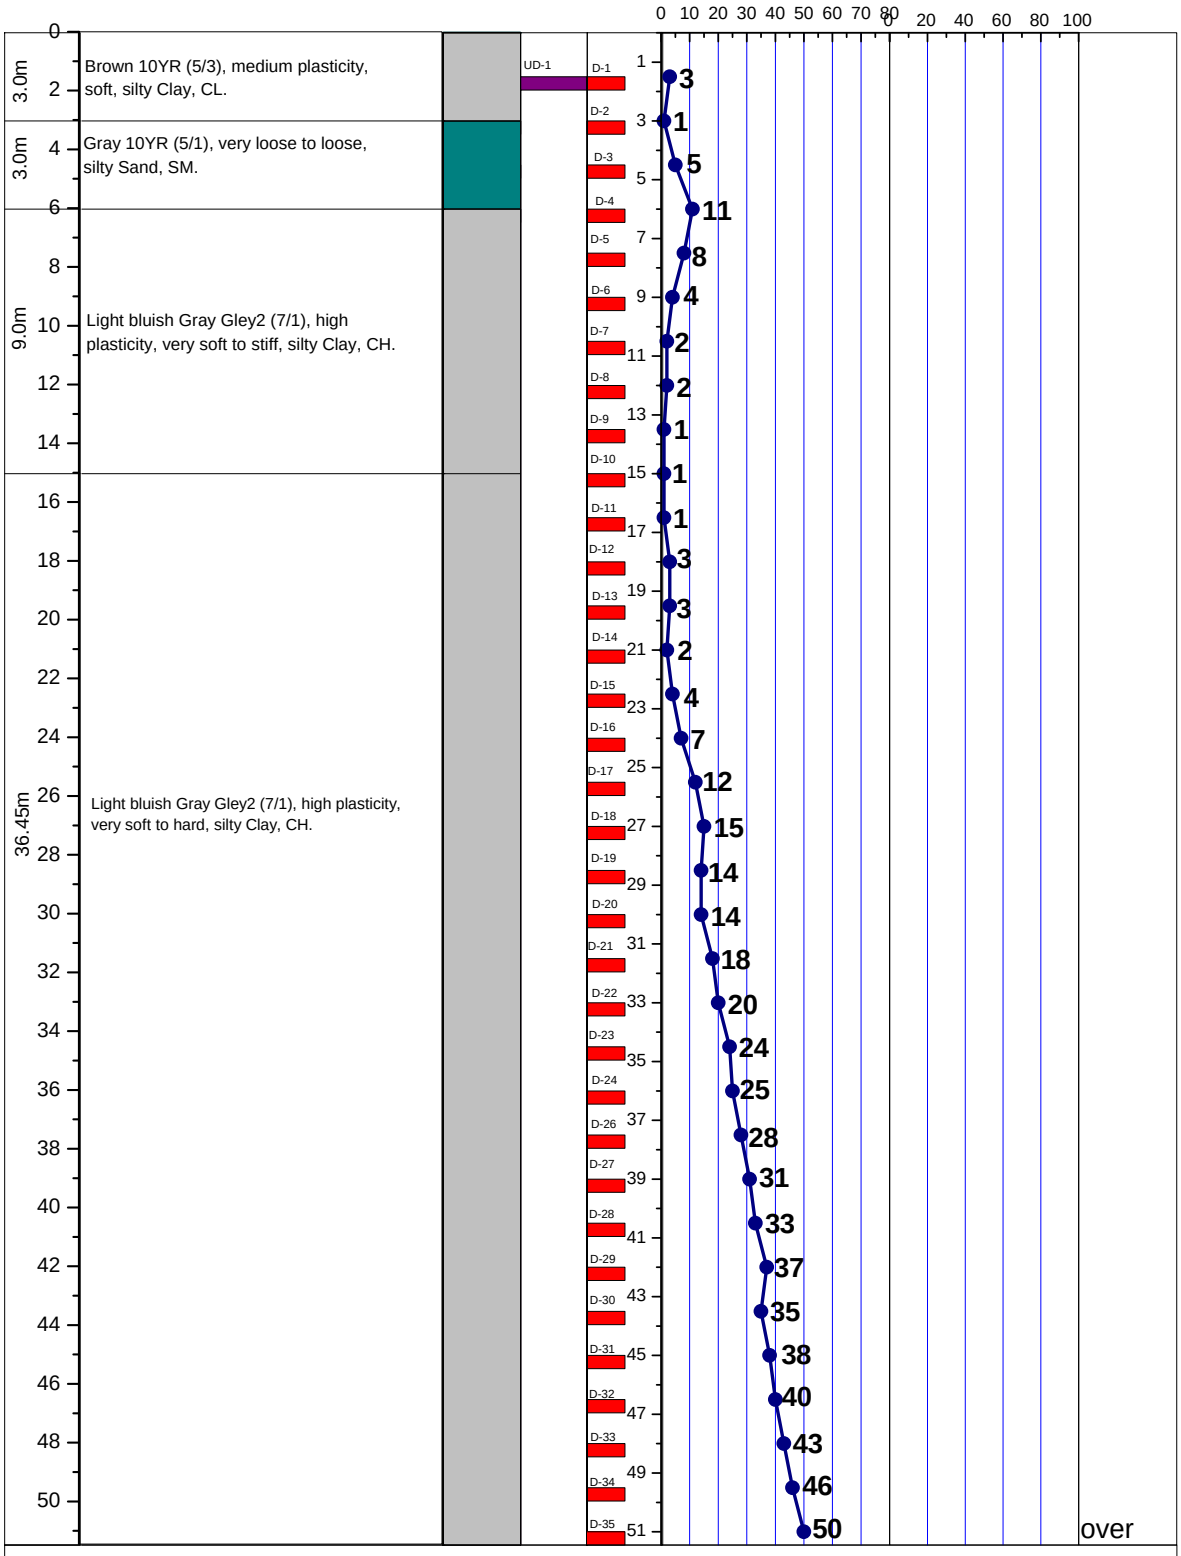

LEGEND FOR BORELOG AND GRAIN SIZE DISTRIBUTION (BASED ON 'ASTM CLASSIFICATION D-2487')

PLASTIC CLAY	SILT	PEAT/HIGHLY ORGANIC SOIL	UNDISTURBED SAMPLE
MICACEOUS FINE SAND/SILT	SAND	SHALE	DISTURBED SAMPLE

N- BLOWS DELIVERED PER FOOT BY A 140 LB HAMMER FALLING 30 INCHES

MAX^{m} PENETRATION= 50 BLOWS. AFTER 50 BLOWS PENETRATION DEPTH WERE MEASURED

A2 PROSOIL	BOREHOLE NO: BH-1	
	LOCATION : Ranirhat 2, Uttar Ghagra, Thanda Chorry, Rangunia, Chittagong.	
PROJECT : Telecommunication Tower.	DEPTH OF BORING : 51.0m	R. L.: 0.61m below from Road Level.
CLIENT : AXIATA (Bangladesh) Ltd.	DATE OF BORING : 17-12-2012.	G. W. T : 1.83m below from E. G. L.

THICKNESS	SOIL STRATA	BORELOG	DISTURBED SAMPLE	DEPTH (m) SPT VALUES (BLOWS / 300mm)	Grain Size Distribution, % Clay %, Silt %, Sand %	Max^{m} Penetration
6.0m	Brown 7.5YR (4/6), medium plasticity, very soft to medium stiff, silty Clay, CL.		UD-1, UD-2, UD-3, UD-4	2, 3, 6, 6		
3.0m	Dark Gray 7.5YR (4/1), medium plasticity, soft to medium stiff, silty Clay, CL.			5, 3, 4		
1.5m	Dark Gray 7.5YR (4/1), loose, silty Sand, SM.			13, 14		
7.5m	Dark Gray 7.5YR (4/1), medium plasticity, soft to stiff, silty Clay, CL.			7, 6, 6, 6, 8, 9, 9, 10		
33.45m	Light Gray 10YR (7/1), loose to very dense, silty Sand, SM.			15, 17, 19, 24, 26, 25, 25, 28, 31, 35, 37, 39, 41, 45, 45, 50, over 50		

LEGEND FOR BORELOG AND GRAIN SIZE DISTRIBUTION (BASED ON 'ASTM CLASSIFICATION D-2487')


PLASTIC CLAY | SILT | PEAT/HIGHLY ORGANIC SOIL | UNDISTURBED SAMPLE

MICACEOUS FINE SAND/SILT | SAND | SHALE | DISTURBED SAMPLE

N- BLOWS DELIVERED PER FOOT BY A 140 LB HAMMER FALLING 30 INCHES

MAX^{m} PENETRATION= 50 BLOWS. AFTER 50 BLOWS PENETRATION DEPTH WERE MEASURED

A2 PROSOIL	BOREHOLE NO: BH-1	
	LOCATION : Rawzan-6, Fakirtakia, West Rawzan, Chittagong.	
PROJECT : Telecommunication Tower.	DEPTH OF BORING : 51.0m	R. L.: 1.05m below from Road Level.
CLIENT : AXIATA (Bangladesh) Ltd.	DATE OF BORING : 02-06-2011.	G. W. T : 1.22m below from E. G. L.

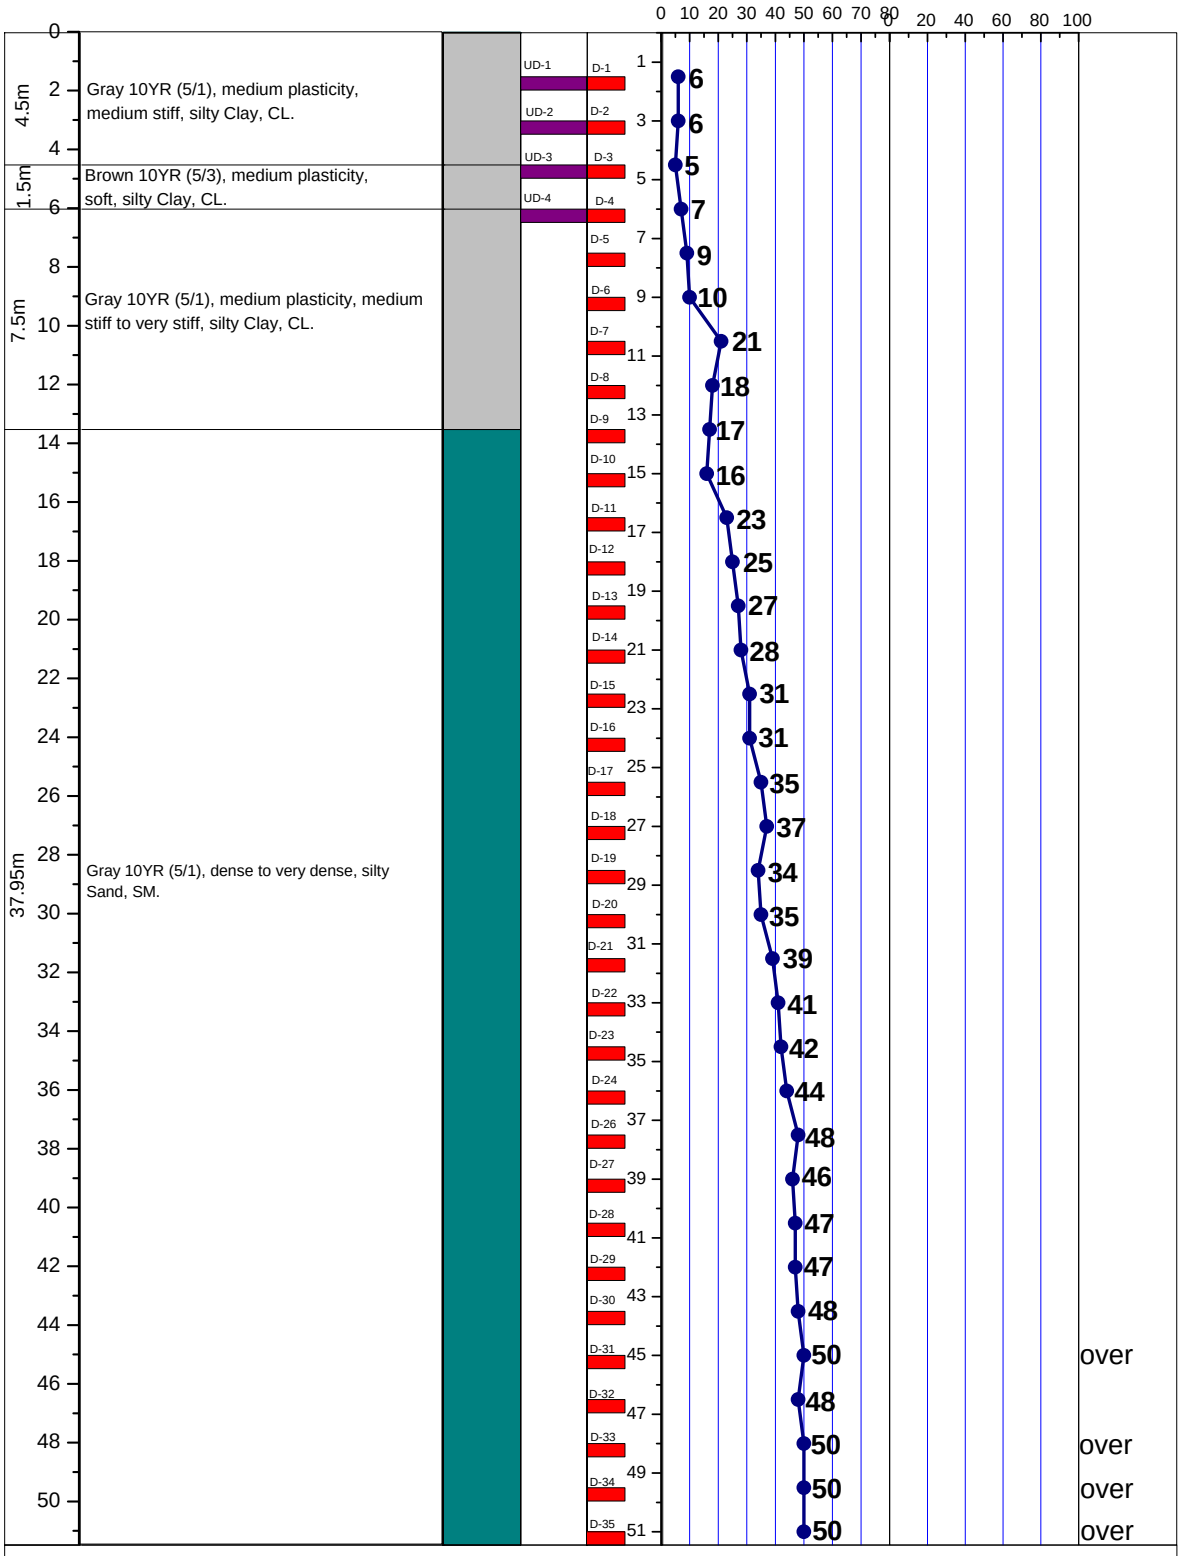


LEGEND FOR BORELOG AND GRAIN SIZE DISTRIBUTION (BASED ON 'ASTM CLASSIFICATION D-2487')

PLASTIC CLAY	SILT	PEAT/HIGHLY ORGANIC SOIL	UNDISTURBED SAMPLE
MICACEOUS FINE SAND/SILT	SAND	SHALE	DISTURBED SAMPLE

N- BLOWS DELIVERED PER FOOT BY A 140 LB HAMMER FALLING 30 INCHES

MAX^{m} PENETRATION= 50 BLOWS. AFTER 50 BLOWS PENETRATION DEPTH WERE MEASURED

A2	PROSOIL	BOREHOLE NO: BH-1	
		LOCATION : Sarkarhat2, Mirzapur, Hathazari, Chittagong, Bangladesh.	
PROJECT : Telecommunication Tower.		DEPTH OF BORING : 51.0m	R. L.: 0.91m below from Road Level.
CLIENT : AXIATA (Bangladesh) Ltd.		DATE OF BORING : 12-02-2012.	G. W. T : 6.1m below from E. G. L.

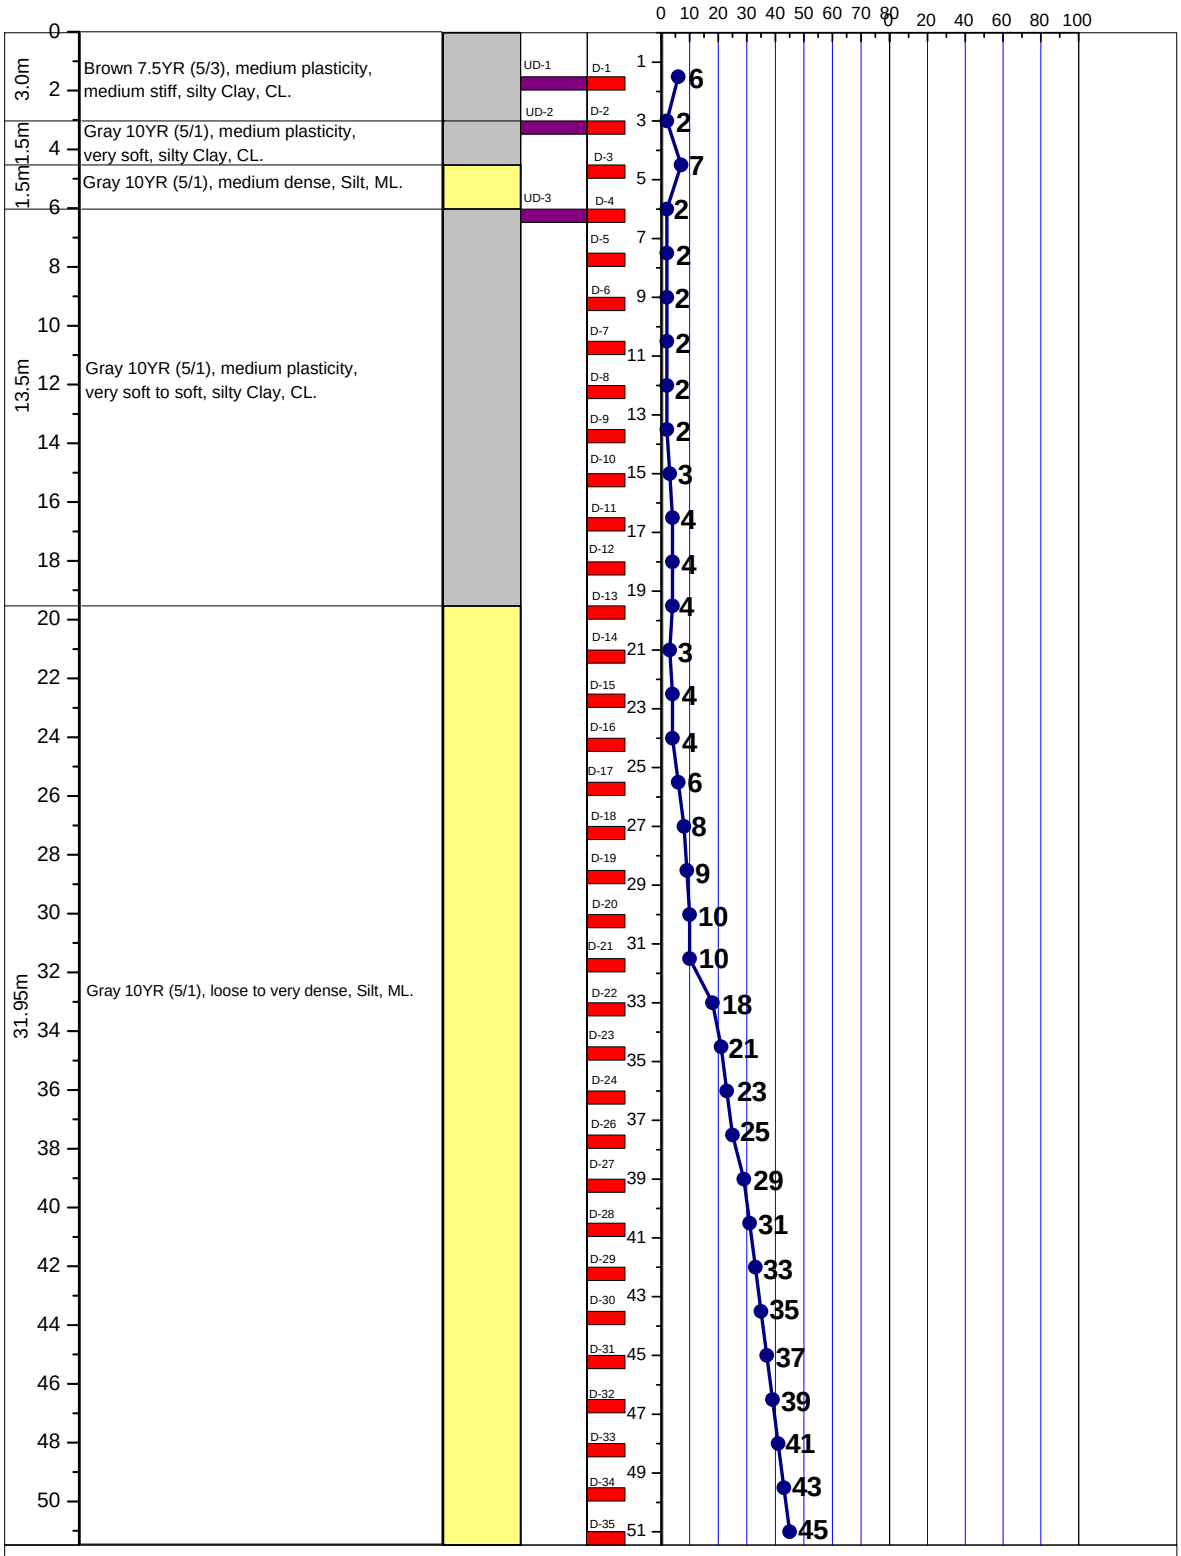


LEGEND FOR BORELOG AND GRAIN SIZE DISTRIBUTION (BASED ON 'ASTM CLASSIFICATION D-2487')

PLASTIC CLAY	SILT	PEAT/HIGHLY ORGANIC SOIL	UNDISTURBED SAMPLE
MICACEOUS FINE SAND/SILT	SAND	SHALE	DISTURBED SAMPLE

N- BLOWS DELIVERED PER FOOT BY A 140 LB HAMMER FALLING 30 INCHES

MAX^{m} PENETRATION= 50 BLOWS. AFTER 50 BLOWS PENETRATION DEPTH WERE MEASURED

A2 PROSOIL	BOREHOLE NO: BH-1	
	LOCATION : Shadurhat, Mirershari,Chittagong.	
PROJECT : Telecommunication Tower.	DEPTH OF BORING : 51.0m	R. L.: 1.07m below from Road Level.
CLIENT : AXIATA (Bangladesh) Ltd.	DATE OF BORING : 03-11-2009.	G. W. T : 1.22m below from E. G. L.

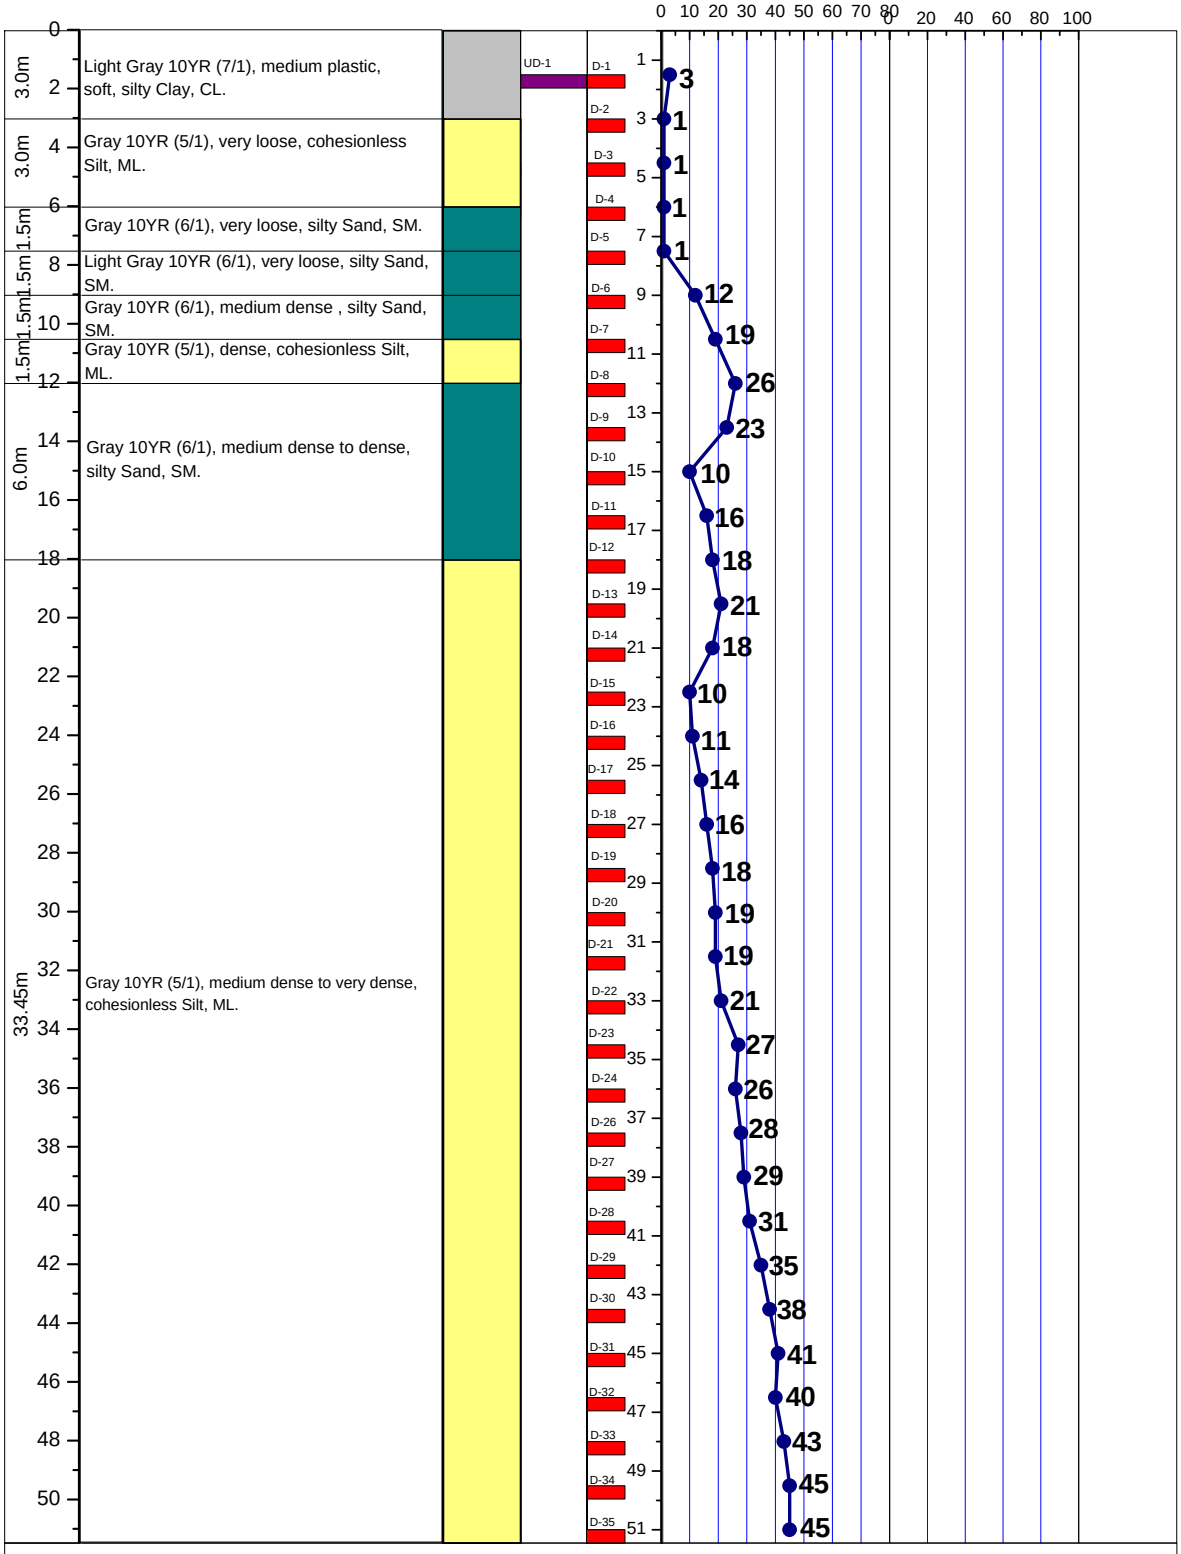


LEGEND FOR BORELOG AND GRAIN SIZE DISTRIBUTION (BASED ON 'ASTM CLASSIFICATION D-2487')

PLASTIC CLAY	SILT	PEAT/HIGHLY ORGANIC SOIL	UNDISTURBED SAMPLE
MICACEOUS FINE SAND/SILT	SAND	SHALE	DISTURBED SAMPLE

N- BLOWS DELIVERED PER FOOT BY A 140 LB HAMMER FALLING 30 INCHES

MAX^{m} PENETRATION= 50 BLOWS. AFTER 50 BLOWS PENETRATION DEPTH WERE MEASURED

A2	PROSOIL	BOREHOLE NO: BH-1	
		LOCATION : Shekher Taluk, Mirershari, Chittagong.	
PROJECT : Telecommunication Tower.		DEPTH OF BORING : 51.0m	R. L.: 0.76m below from Road Level.
CLIENT : AXIATA (Bangladesh) Ltd.		DATE OF BORING : 28-08-2009.	G. W. T : 0.10m above from E. G. L. (Rain water)

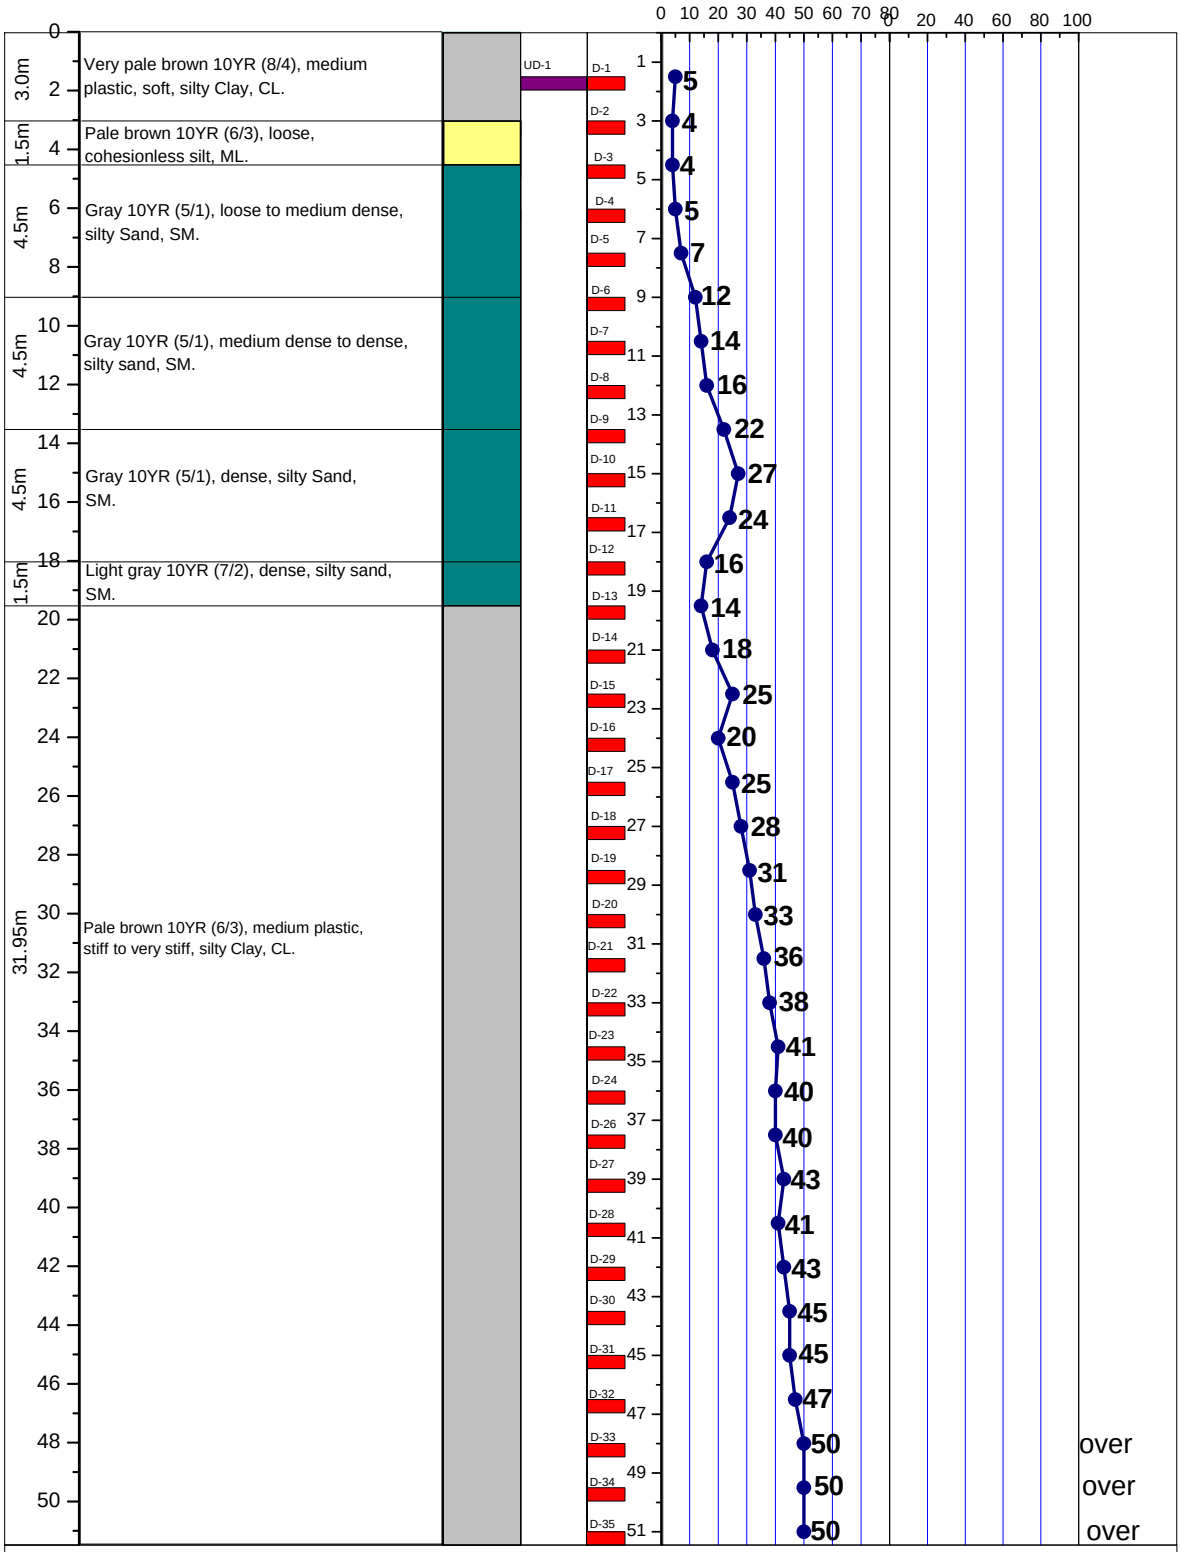


LEGEND FOR BORELOG AND GRAIN SIZE DISTRIBUTION (BASED ON 'ASTM CLASSIFICATION D-2487')

PLASTIC CLAY	SILT	PEAT/HIGHLY ORGANIC SOIL	UNDISTURBED SAMPLE
MICACEOUS FINE SAND/SILT	SAND	SHALE	DISTURBED SAMPLE

N- BLOWS DELIVERED PER FOOT BY A 140 LB HAMMER FALLING 30 INCHES

MAX^{m} PENETRATION= 50 BLOWS. AFTER 50 BLOWS PENETRATION DEPTH WERE MEASURED

A2	PROSOIL	BOREHOLE NO: BH-1	
		LOCATION : Shiber Hut 2 Land, Swandip, Chittagong.	
PROJECT : Telecommunication Tower.		DEPTH OF BORING : 51.0m	R. L.: 1.22m below from Road Level.
CLIENT : AXIATA (Bangladesh) Ltd.		DATE OF BORING : 27-04-2012.	G. W. T : 2.44m below from E. G. L.

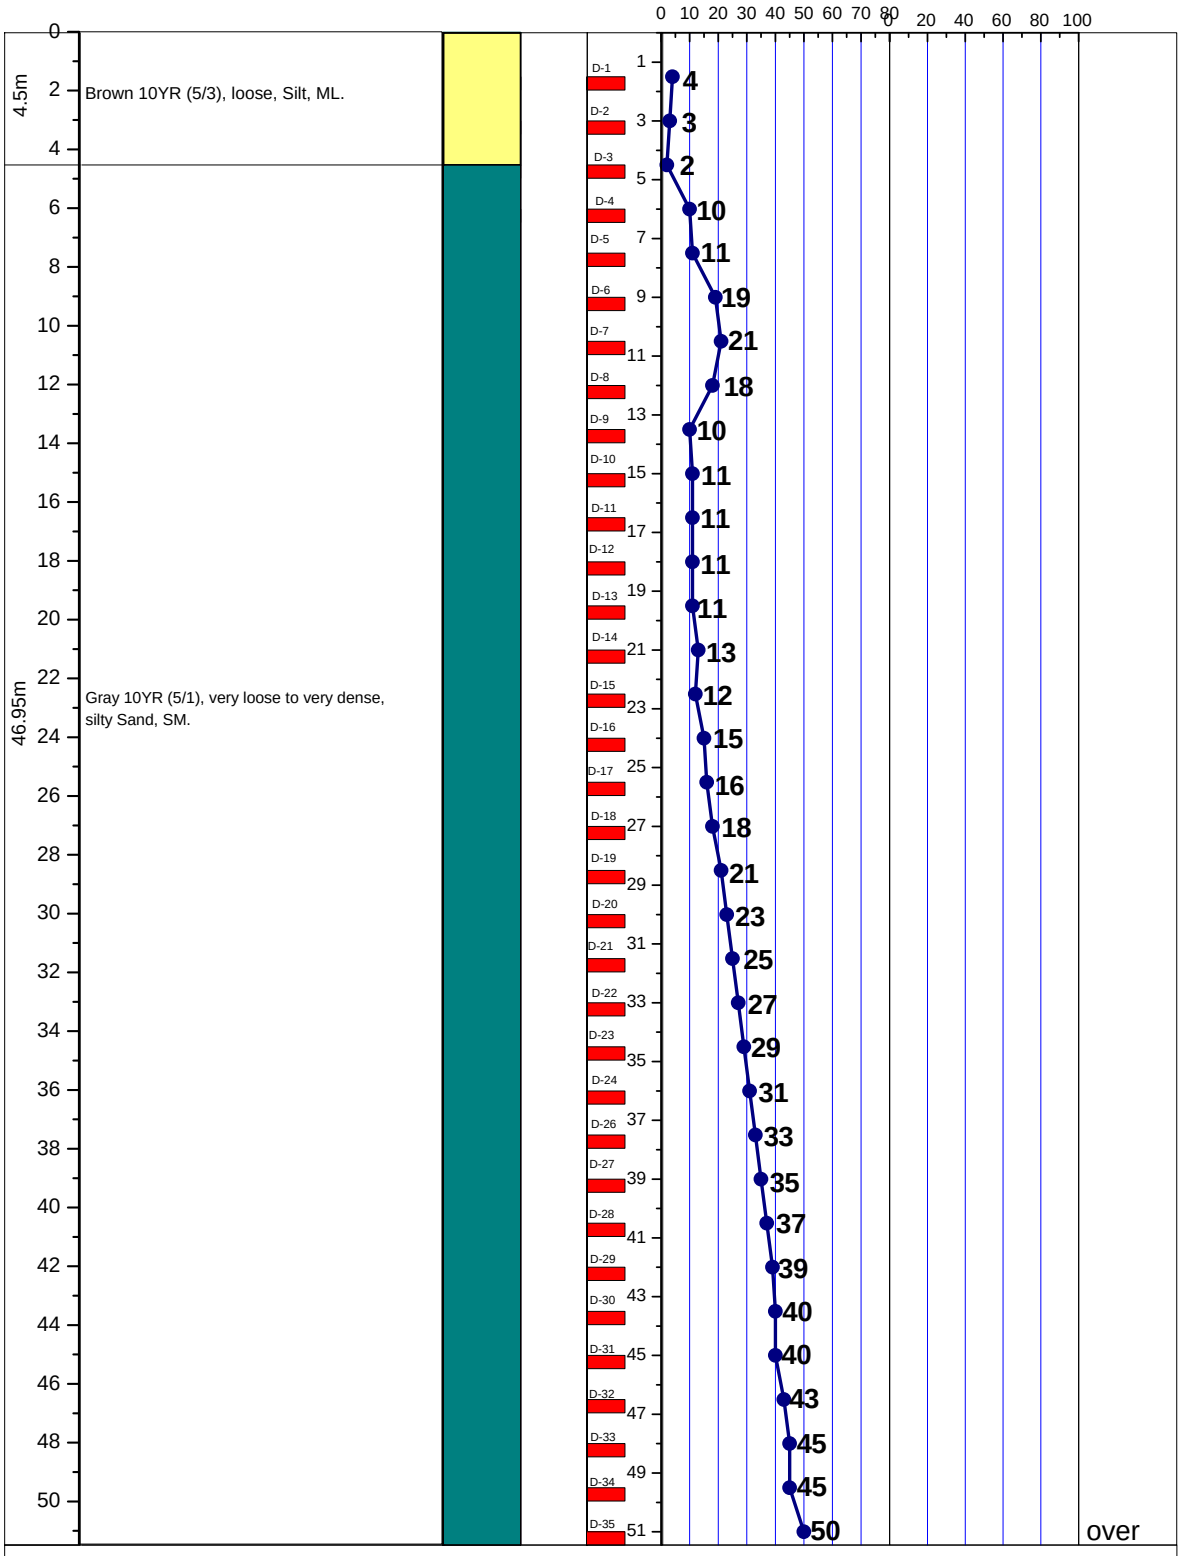


LEGEND FOR BORELOG AND GRAIN SIZE DISTRIBUTION (BASED ON 'ASTM CLASSIFICATION D-2487')

PLASTIC CLAY	SILT	PEAT/HIGHLY ORGANIC SOIL	UNDISTURBED SAMPLE
MICACEOUS FINE SAND/SILT	SAND	SHALE	DISTURBED SAMPLE

N- BLOWS DELIVERED PER FOOT BY A 140 LB HAMMER FALLING 30 INCHES

MAX^{m} PENETRATION= 50 BLOWS. AFTER 50 BLOWS PENETRATION DEPTH WERE MEASURED

A2 PROSOIL	BOREHOLE NO: BH-1	
	LOCATION : South Rangamatia, Fatikchari, Chittagong.	
PROJECT : Telecommunication Tower.	DEPTH OF BORING : 51.0m	R. L.: 1.22m below from Road Level.
CLIENT : TM International, Bangladesh Ltd.	DATE OF BORING : 28-03-2009.	G. W. T : 3.35m below from E. G. L.

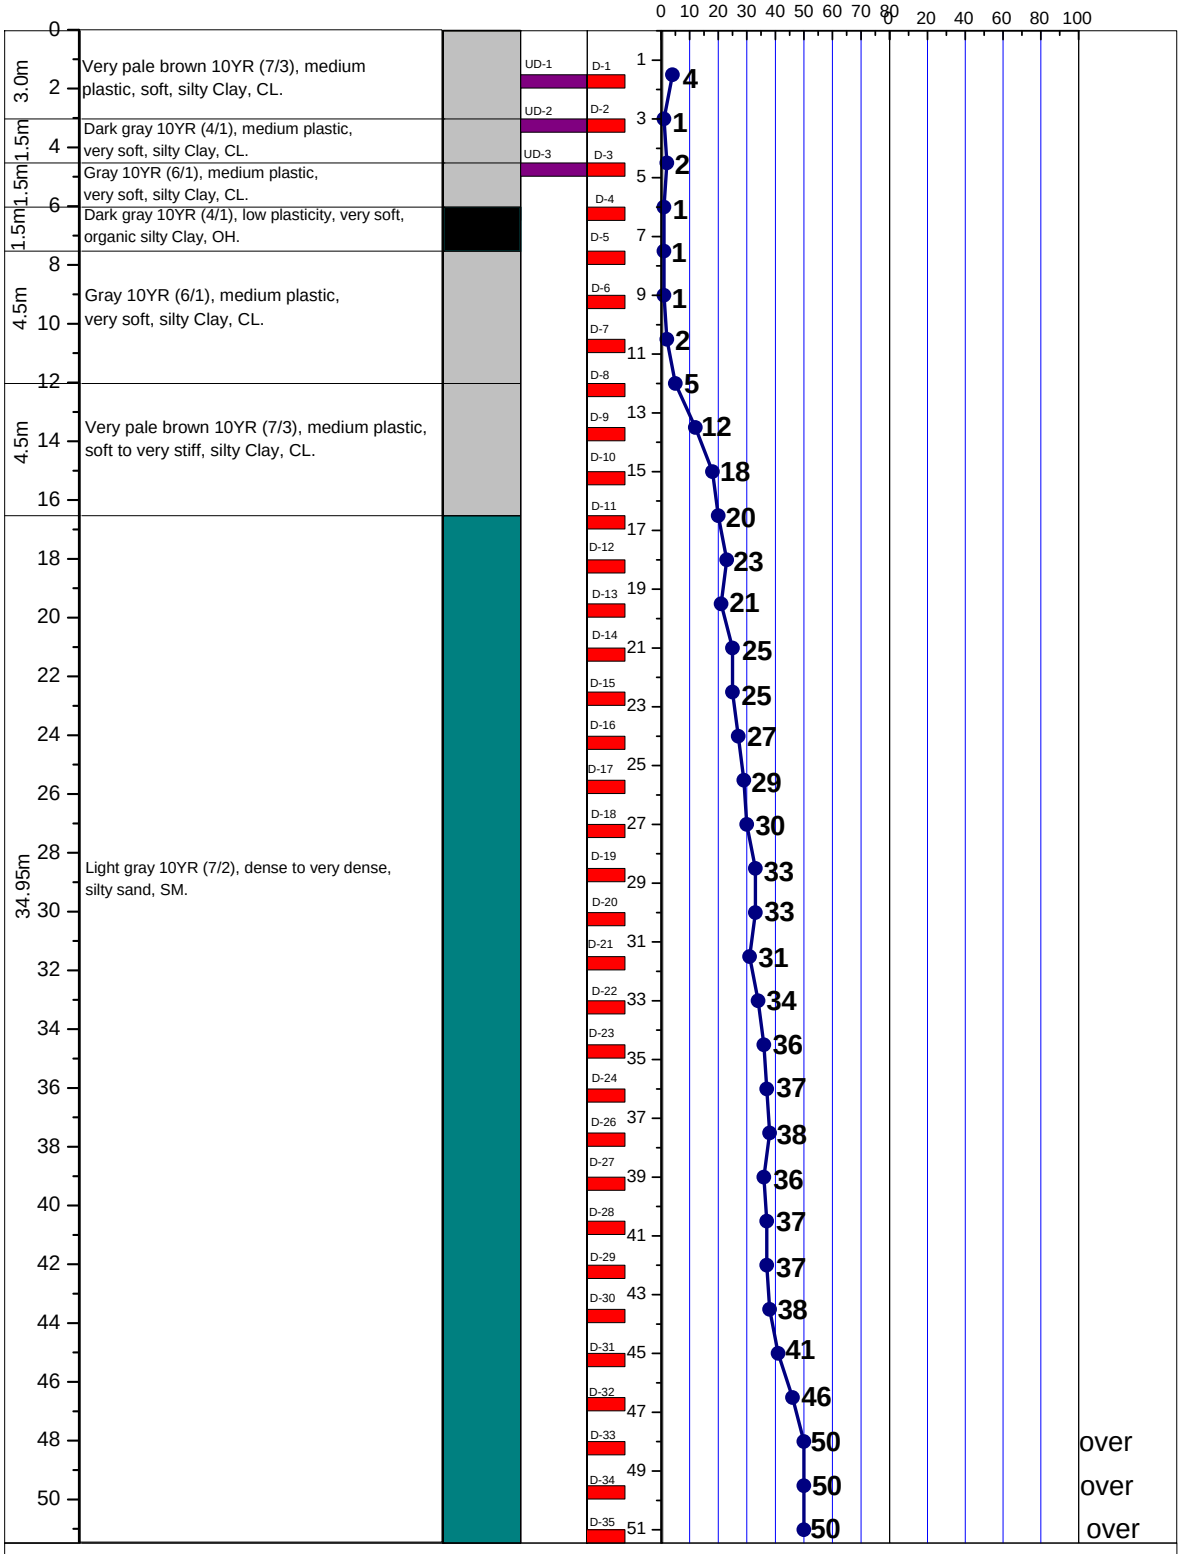


LEGEND FOR BORELOG AND GRAIN SIZE DISTRIBUTION (BASED ON 'ASTM CLASSIFICATION D-2487')

PLASTIC CLAY	SILT	PEAT/HIGHLY ORGANIC SOIL	UNDISTURBED SAMPLE
MICACEOUS FINE SAND/SILT	SAND	SHALE	DISTURBED SAMPLE

N- BLOWS DELIVERED PER FOOT BY A 140 LB HAMMER FALLING 30 INCHES

MAX^{m} PENETRATION= 50 BLOWS. AFTER 50 BLOWS PENETRATION DEPTH WERE MEASURED

A2	PROSOIL	BOREHOLE NO: BH-1	
		LOCATION : Sukhbilas, Rangunia, Chittagong.	
PROJECT : Telecommunication Tower.		DEPTH OF BORING : 51.0m	R. L.: 0.30m below from Road Level.
CLIENT : TM International, Bangladesh Ltd.		DATE OF BORING : 26-03-2009.	G. W. T : 1.52m below from E. G. L.

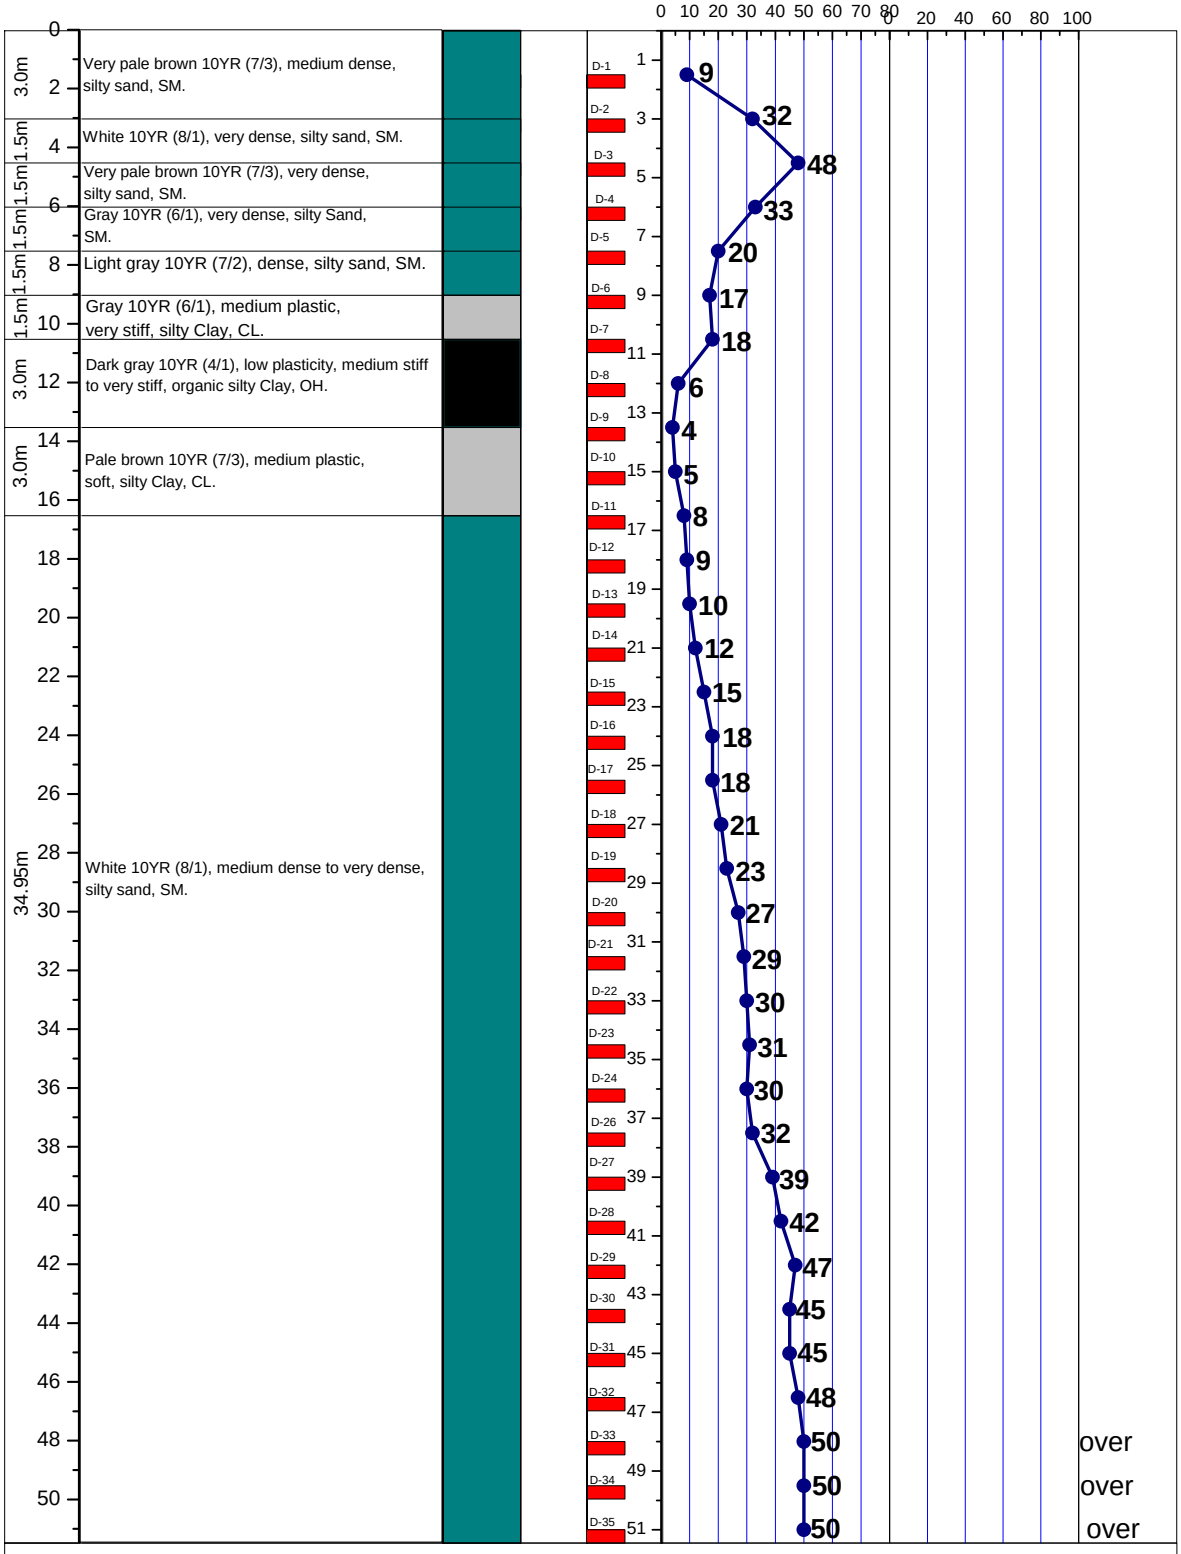


LEGEND FOR BORELOG AND GRAIN SIZE DISTRIBUTION (BASED ON 'ASTM CLASSIFICATION D-2487')

PLASTIC CLAY	SILT	PEAT/HIGHLY ORGANIC SOIL	UNDISTURBED SAMPLE
MICACEOUS FINE SAND/SILT	SAND	SHALE	DISTURBED SAMPLE

N- BLOWS DELIVERED PER FOOT BY A 140 LB HAMMER FALLING 30 INCHES

MAX^{m} PENETRATION= 50 BLOWS. AFTER 50 BLOWS PENETRATION DEPTH WERE MEASURED

A2 PROSOIL	BOREHOLE NO: BH-1	
	LOCATION : Gobindopur, Mirershari, Chittagong.	
PROJECT : Telecommunication Tower.	DEPTH OF BORING : 51.0m	R. L.: 1.52m below from Road Level.
CLIENT : AXIATA (Bangladesh) Ltd.	DATE OF BORING : 03-07-2010.	G. W. T : 0.40m below from E. G. L.

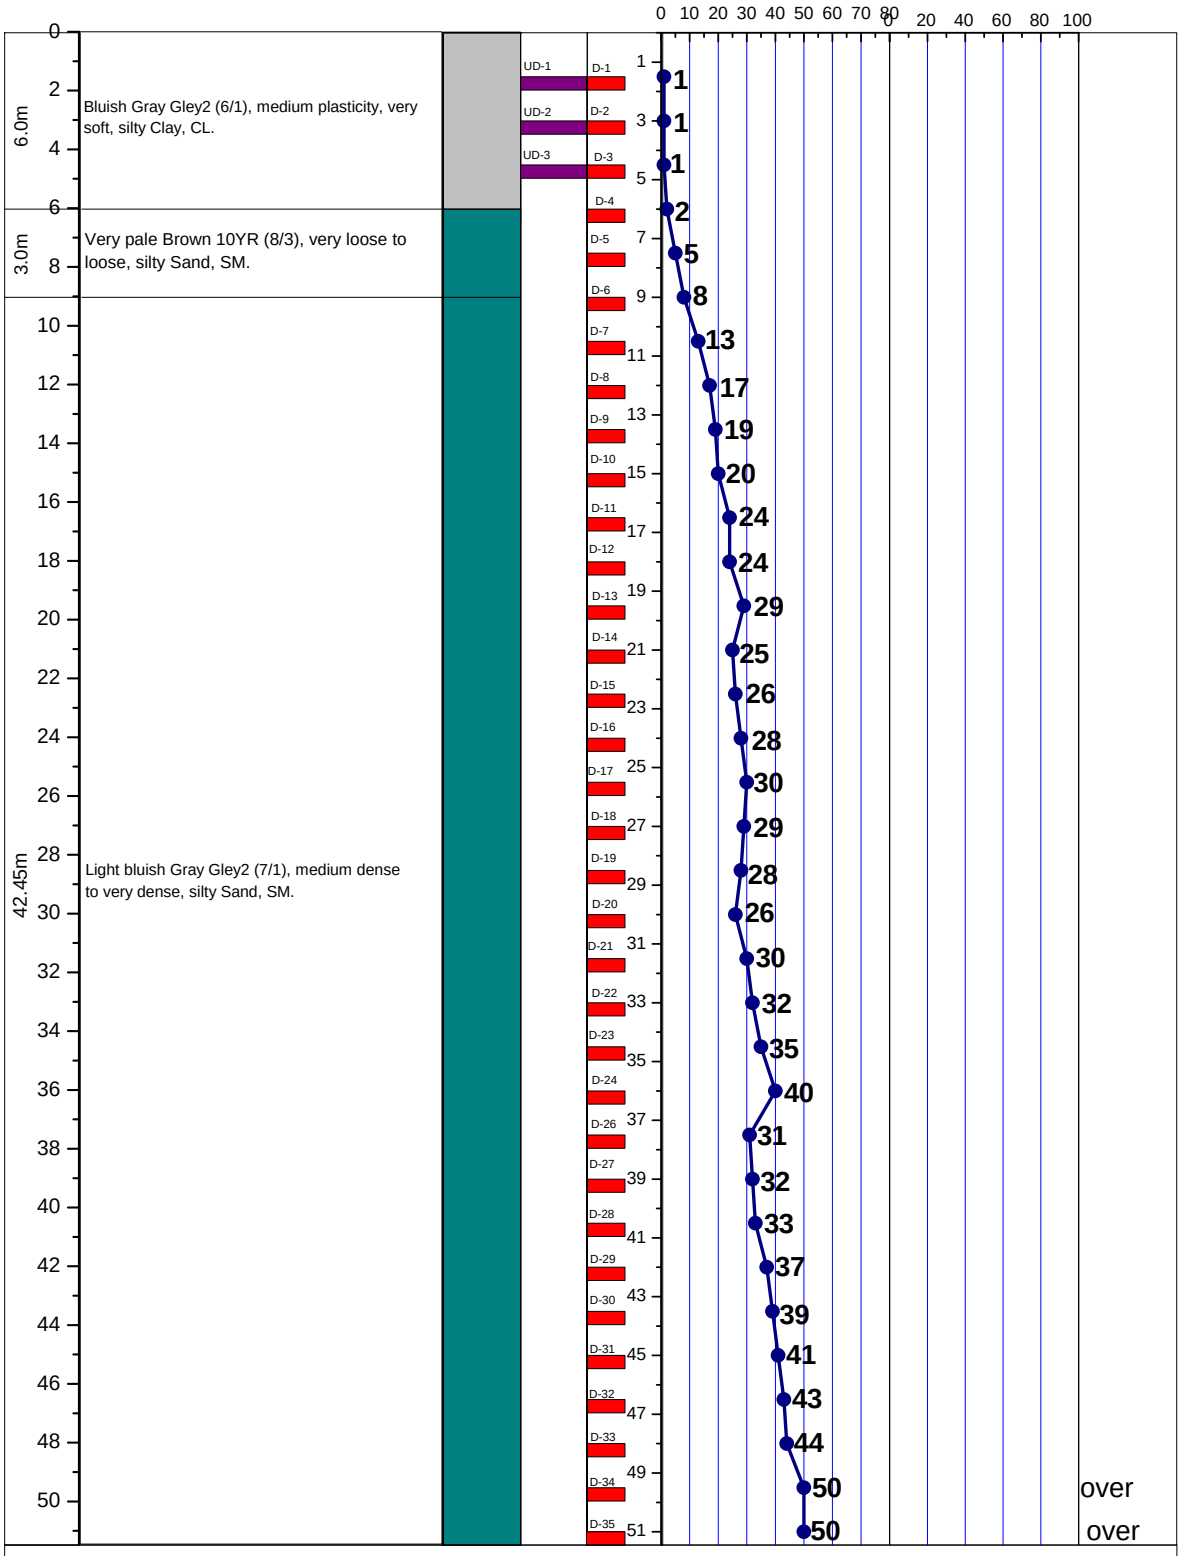


LEGEND FOR BORELOG AND GRAIN SIZE DISTRIBUTION (BASED ON 'ASTM CLASSIFICATION D-2487')

PLASTIC CLAY	SILT	PEAT/HIGHLY ORGANIC SOIL	UNDISTURBED SAMPLE
MICACEOUS FINE SAND/SILT	SAND	SHALE	DISTURBED SAMPLE

N- BLOWS DELIVERED PER FOOT BY A 140 LB HAMMER FALLING 30 INCHES

MAX^{m} PENETRATION= 50 BLOWS. AFTER 50 BLOWS PENETRATION DEPTH WERE MEASURED

A2 PROSOIL	BOREHOLE NO: BH-1	
	LOCATION : Mirersharai 2, Chittagong.	
PROJECT : Telecommunication Tower.	DEPTH OF BORING : 51.0m	R. L.: 0.23m below from Road Level.
CLIENT : AXIATA (Bangladesh) Ltd.	DATE OF BORING : 27-06-2010.	G. W. T : 0.31m below from E. G. L.

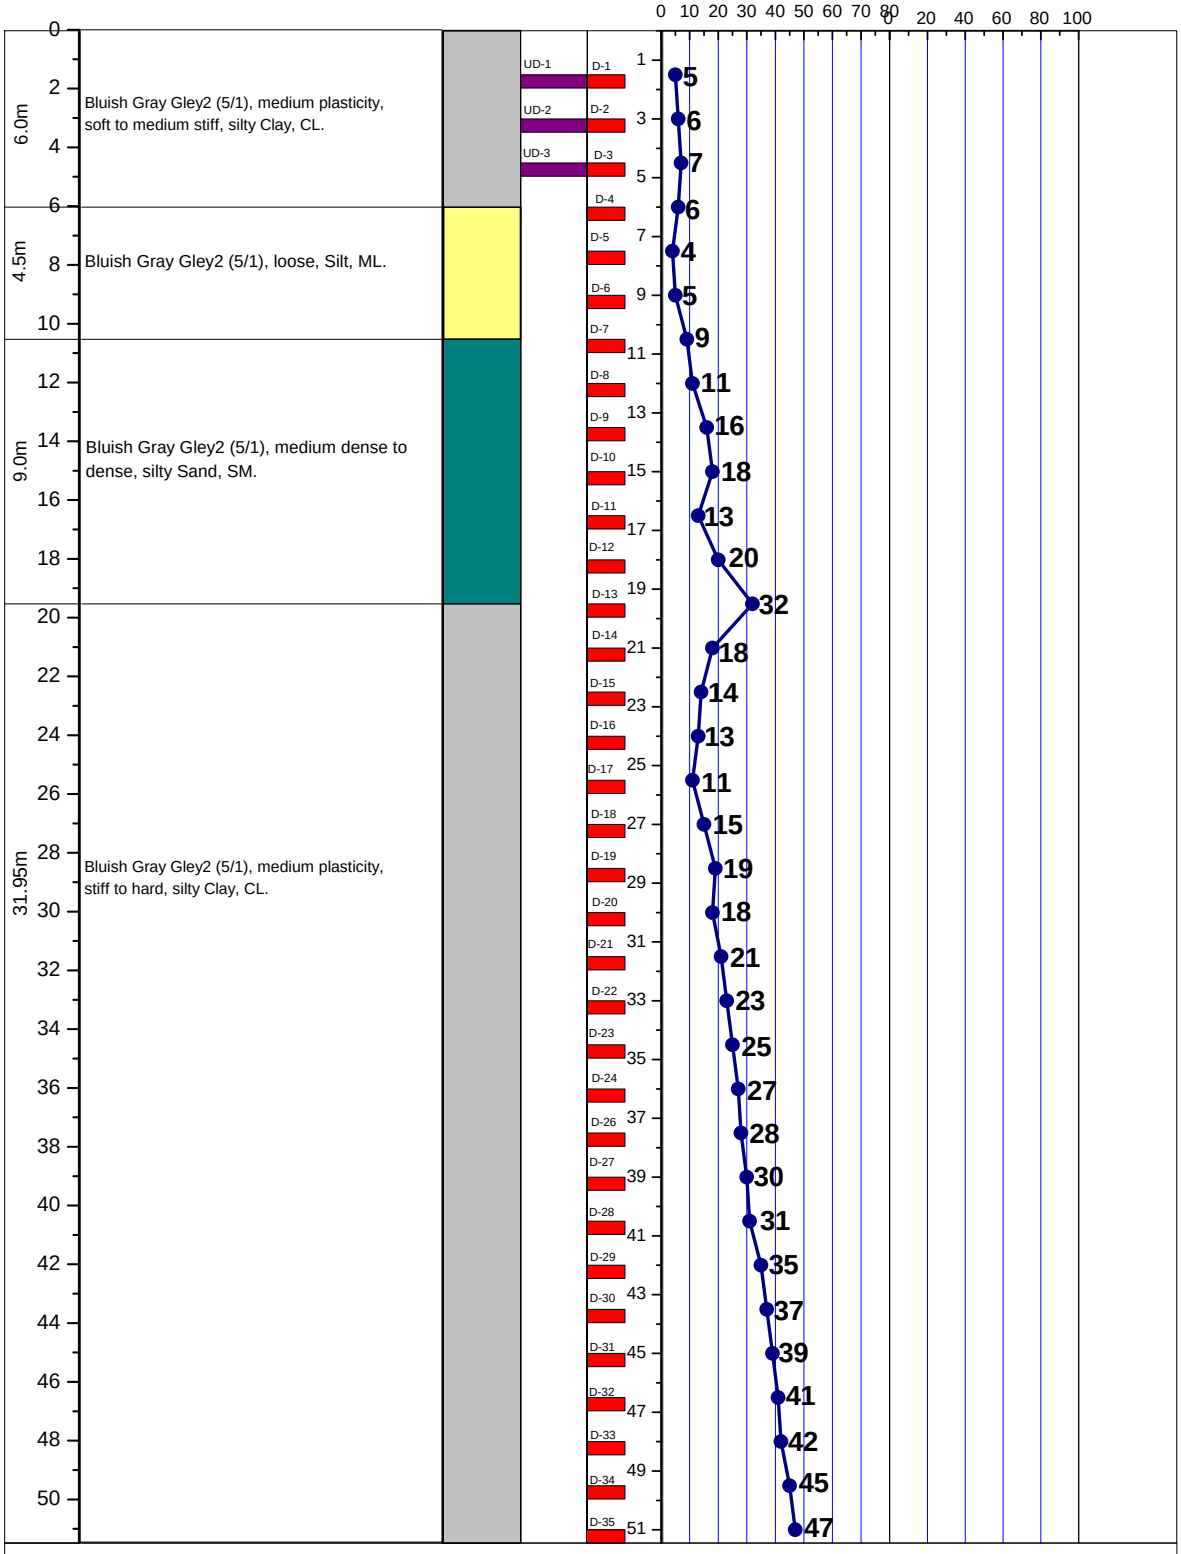


LEGEND FOR BORELOG AND GRAIN SIZE DISTRIBUTION (BASED ON 'ASTM CLASSIFICATION D-2487')

PLASTIC CLAY	SILT	PEAT/HIGHLY ORGANIC SOIL	UNDISTURBED SAMPLE
MICACEOUS FINE SAND/SILT	SAND	SHALE	DISTURBED SAMPLE

N- BLOWS DELIVERED PER FOOT BY A 140 LB HAMMER FALLING 30 INCHES

MAX^{m} PENETRATION= 50 BLOWS. AFTER 50 BLOWS PENETRATION DEPTH WERE MEASURED

A2 PROSOIL	BOREHOLE NO: BH-1	
	LOCATION : Mohadebpur, Miresarai, Chittagong.	
PROJECT : Telecommunication Tower.	DEPTH OF BORING : 51.0m	R. L.: 0.31m below from Road Level.
CLIENT : AXIATA (Bangladesh) Ltd.	DATE OF BORING : 30-07-2010.	G. W. T : 0.61m below from E. G. L.

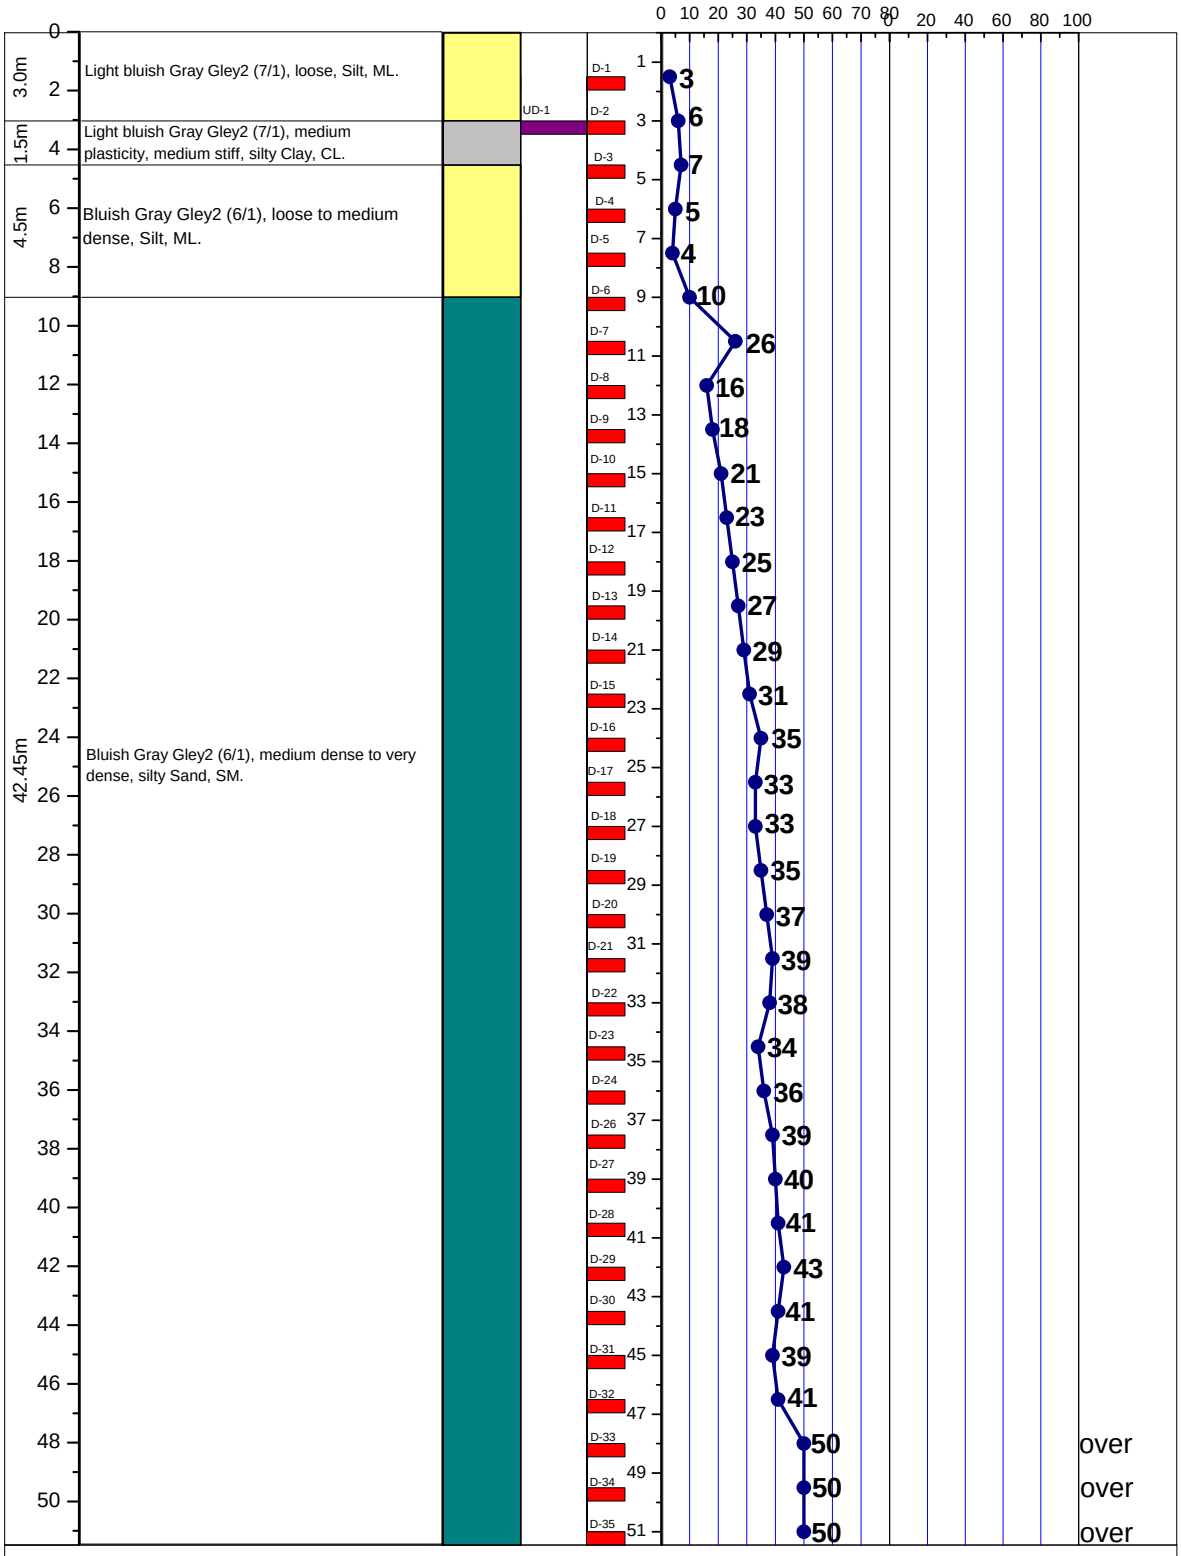


LEGEND FOR BORELOG AND GRAIN SIZE DISTRIBUTION (BASED ON 'ASTM CLASSIFICATION D-2487')

PLASTIC CLAY	SILT	PEAT/HIGHLY ORGANIC SOIL	UNDISTURBED SAMPLE
MICACEOUS FINE SAND/SILT	SAND	SHALE	DISTURBED SAMPLE

N- BLOWS DELIVERED PER FOOT BY A 140 LB HAMMER FALLING 30 INCHES

MAX^{m} PENETRATION= 50 BLOWS. AFTER 50 BLOWS PENETRATION DEPTH WERE MEASURED

A2 PROSOIL	BOREHOLE NO: BH-1	
	LOCATION : Muhuri Project 2 (Abdul Hat-2), Miresharai, Chittagong.	
PROJECT : Telecommunication Tower.	DEPTH OF BORING : 51.0m	R. L.: 0.31m below from Road Level.
CLIENT : AXIATA (Bangladesh) Ltd.	DATE OF BORING : 26-06-2010.	G. W. T : 0.31m above from E. G. L.

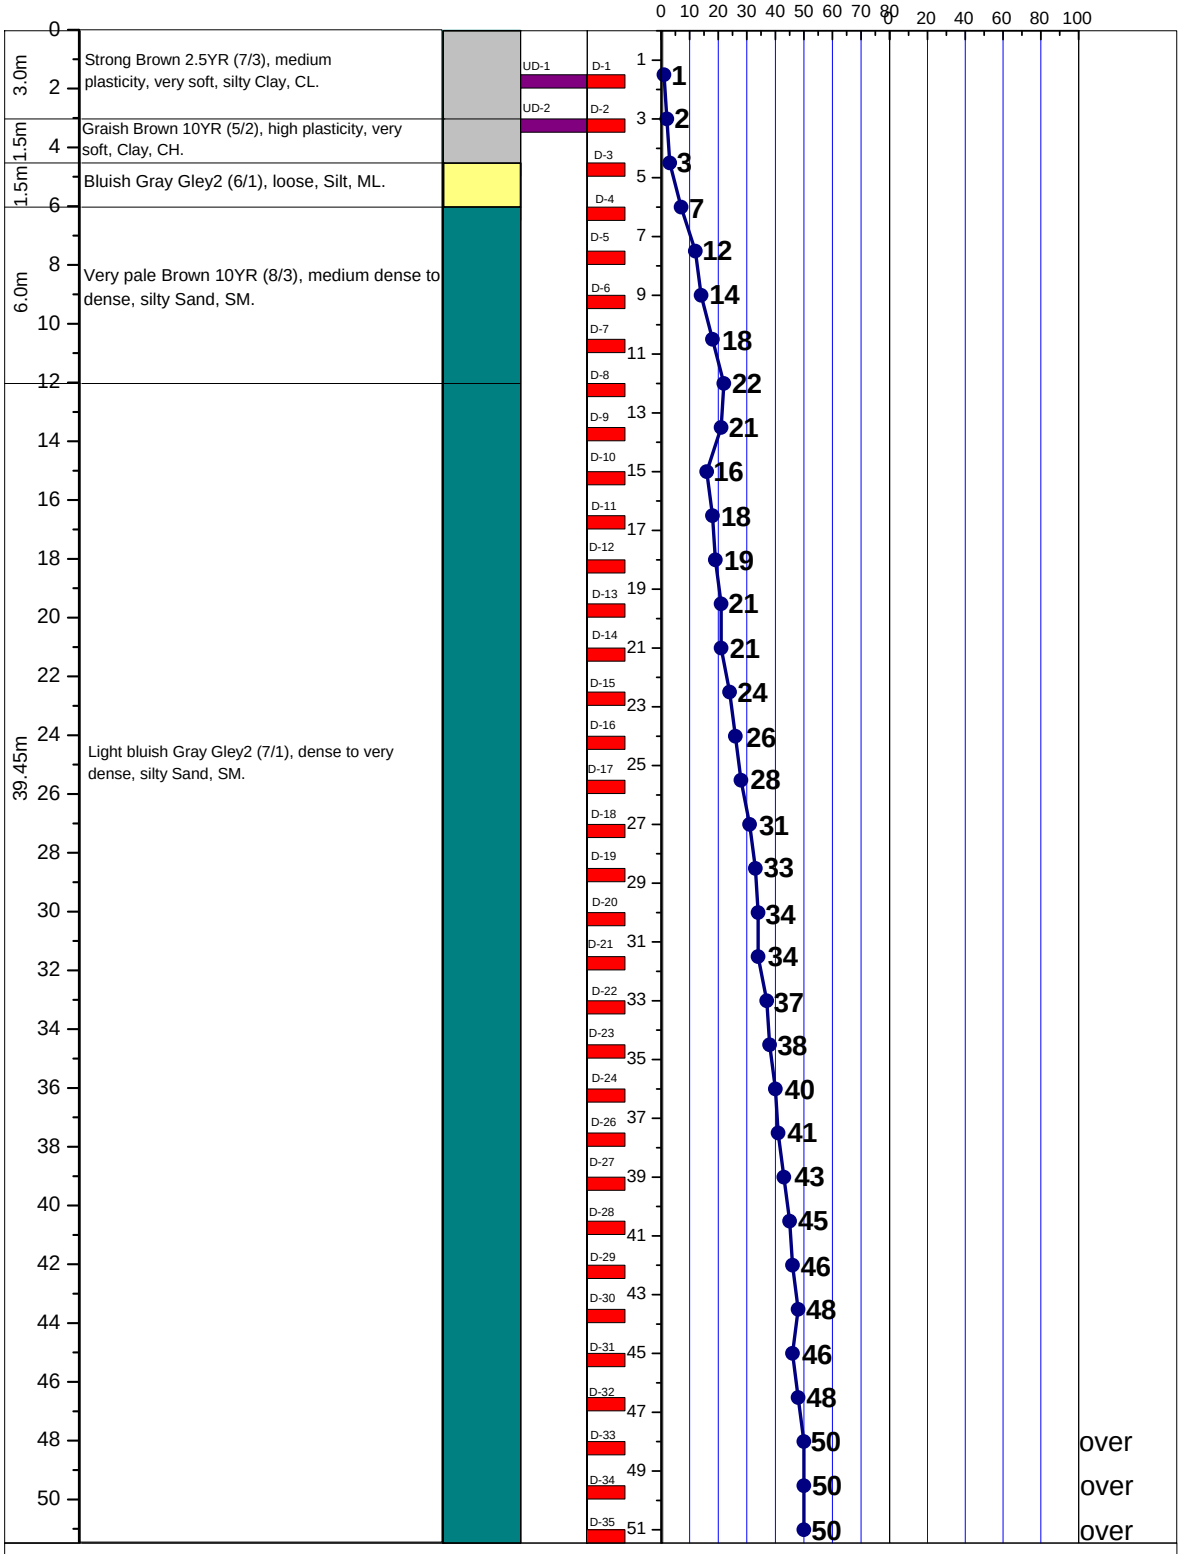


LEGEND FOR BORELOG AND GRAIN SIZE DISTRIBUTION (BASED ON 'ASTM CLASSIFICATION D-2487')

PLASTIC CLAY	SILT	PEAT/HIGHLY ORGANIC SOIL	UNDISTURBED SAMPLE
MICACEOUS FINE SAND/SILT	SAND	SHALE	DISTURBED SAMPLE

N- BLOWS DELIVERED PER FOOT BY A 140 LB HAMMER FALLING 30 INCHES

MAX^{m} PENETRATION= 50 BLOWS. AFTER 50 BLOWS PENETRATION DEPTH WERE MEASURED

A2	PROSOIL	BOREHOLE NO: BH-1	
		LOCATION : Shiberhat, Sandwip, Chittagong.	
PROJECT : Telecommunication Tower.		DEPTH OF BORING : 51.0m	R. L.: 1.21m below from Road Level.
CLIENT : AXIATA (Bangladesh) Ltd.		DATE OF BORING : 28-08-2010.	G. W. T : Rain Water.

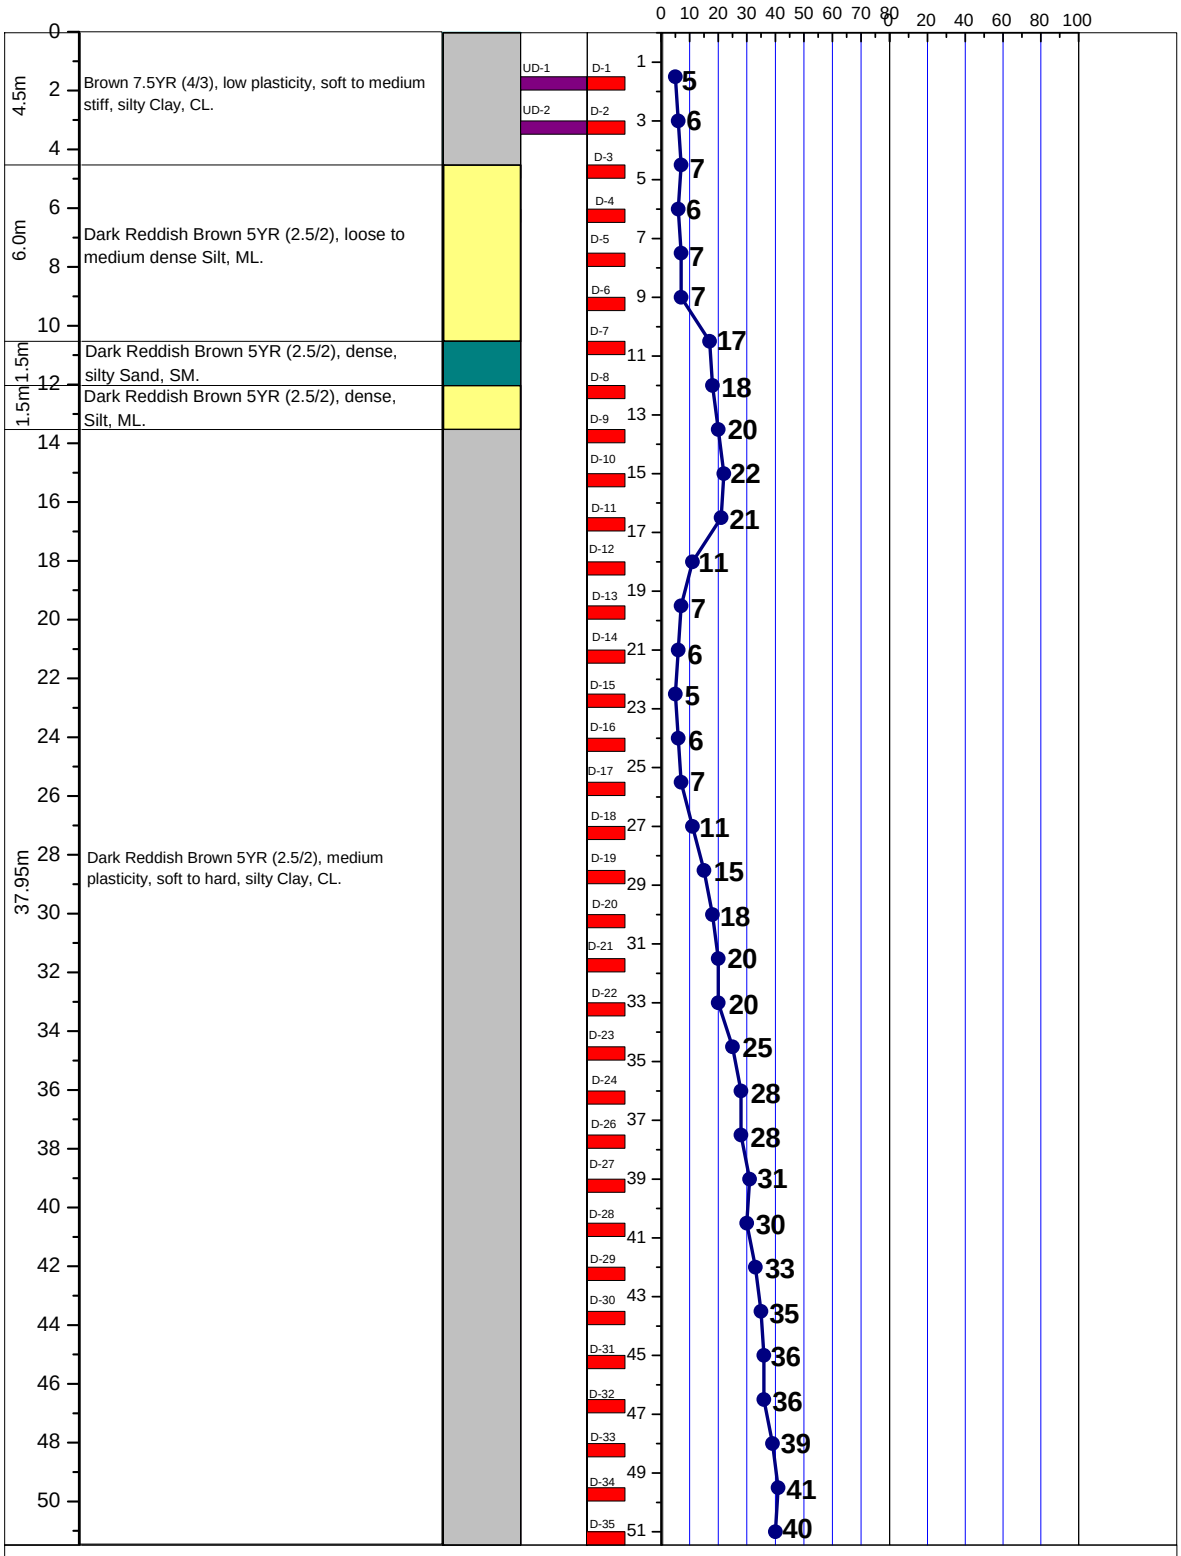


LEGEND FOR BORELOG AND GRAIN SIZE DISTRIBUTION (BASED ON 'ASTM CLASSIFICATION D-2487')

PLASTIC CLAY	SILT	PEAT/HIGHLY ORGANIC SOIL	UNDISTURBED SAMPLE
MICACEOUS FINE SAND/SILT	SAND	SHALE	DISTURBED SAMPLE

N- BLOWS DELIVERED PER FOOT BY A 140 LB HAMMER FALLING 30 INCHES

MAX^{m} PENETRATION= 50 BLOWS. AFTER 50 BLOWS PENETRATION DEPTH WERE MEASURED

A2 PROSOIL	BOREHOLE NO: BH-1	
	LOCATION : Shilerhat, Hathazari, Chittagong.	
PROJECT : Telecommunication Tower.	DEPTH OF BORING : 51.0m	R. L.: 1.52m below from Road Level.
CLIENT : AXIATA (Bangladesh) Ltd.	DATE OF BORING : 01-07-2010.	G. W. T : 0.08m below from E. G. L.

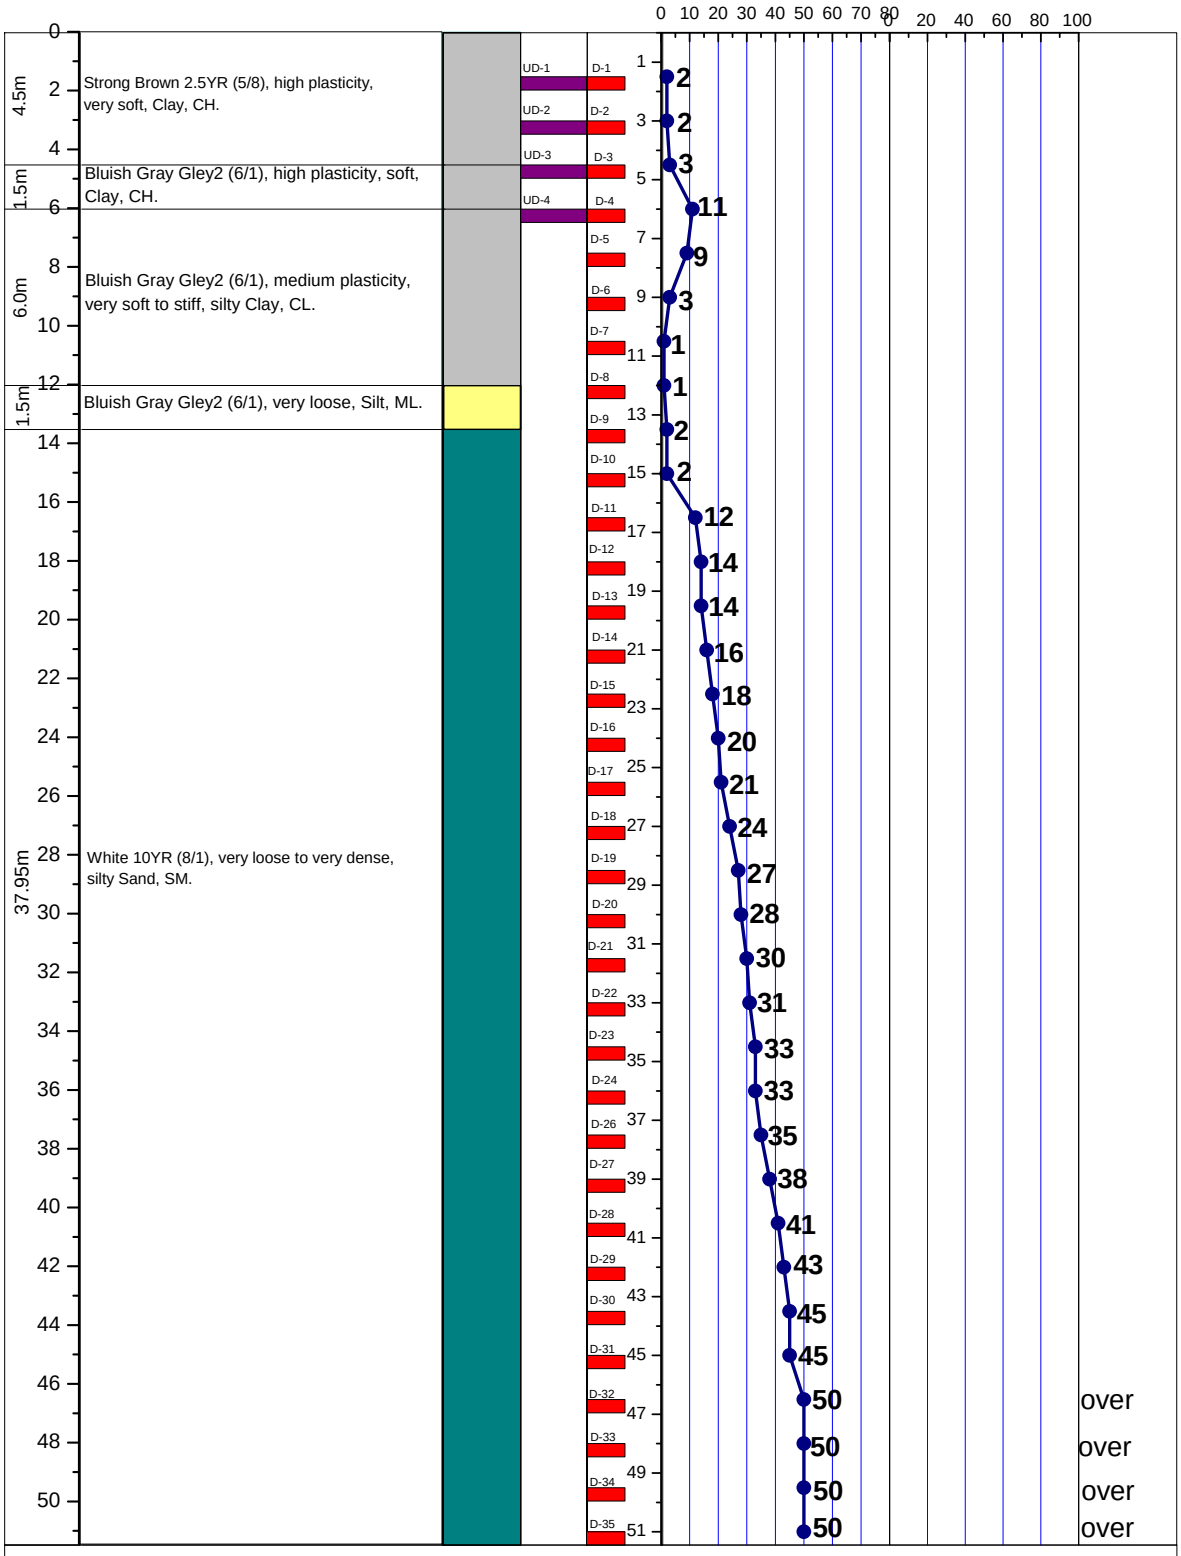


LEGEND FOR BORELOG AND GRAIN SIZE DISTRIBUTION (BASED ON 'ASTM CLASSIFICATION D-2487')

PLASTIC CLAY	SILT	PEAT/HIGHLY ORGANIC SOIL	UNDISTURBED SAMPLE
MICACEOUS FINE SAND/SILT	SAND	SHALE	DISTURBED SAMPLE

N- BLOWS DELIVERED PER FOOT BY A 140 LB HAMMER FALLING 30 INCHES

MAX^{m} PENETRATION= 50 BLOWS. AFTER 50 BLOWS PENETRATION DEPTH WERE MEASURED

A2 PROSOIL	BOREHOLE NO: BH-1	
	LOCATION : Sonagah, Rangonia, Chittagong.	
PROJECT : Telecommunication Tower.	DEPTH OF BORING : 51.0m	R. L.: 0.61m below from Road Level.
CLIENT : AXIATA (Bangladesh) Ltd.	DATE OF BORING : 29-11-2010.	G. W. T : 2.44m below from E. G. L.

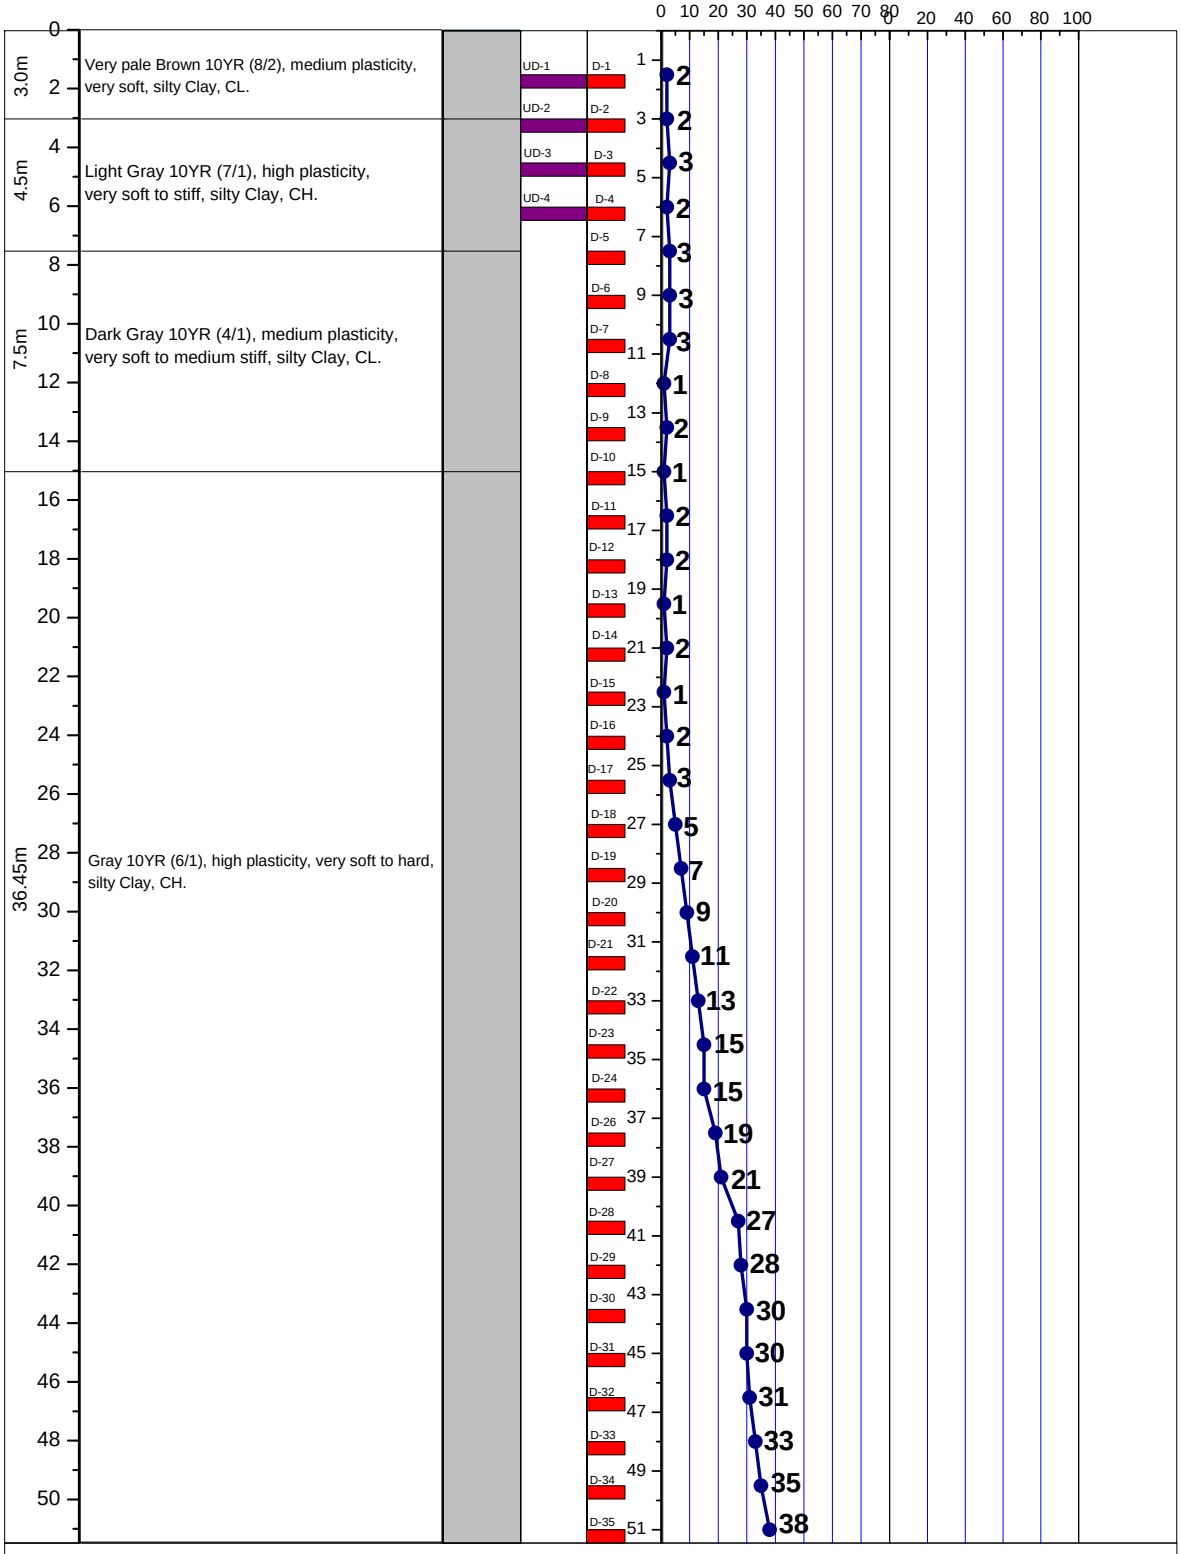


LEGEND FOR BORELOG AND GRAIN SIZE DISTRIBUTION (BASED ON 'ASTM CLASSIFICATION D-2487')

PLASTIC CLAY	SILT	PEAT/HIGHLY ORGANIC SOIL	UNDISTURBED SAMPLE
MICACEOUS FINE SAND/SILT	SAND	SHALE	DISTURBED SAMPLE

N- BLOWS DELIVERED PER FOOT BY A 140 LB HAMMER FALLING 30 INCHES

MAX^{m} PENETRATION= 50 BLOWS. AFTER 50 BLOWS PENETRATION DEPTH WERE MEASURED

A2	PROSOIL	BOREHOLE NO: BH-1	
		LOCATION : West Haid Chokia, Fotikchori, Chittagong.	
PROJECT : Telecommunication Tower.		DEPTH OF BORING : 51.0m	R. L.: 3.05m below from Road Level.
CLIENT : AXIATA (Bangladesh) Ltd.		DATE OF BORING : 29-06-2010.	G. W. T : On E. G. L.

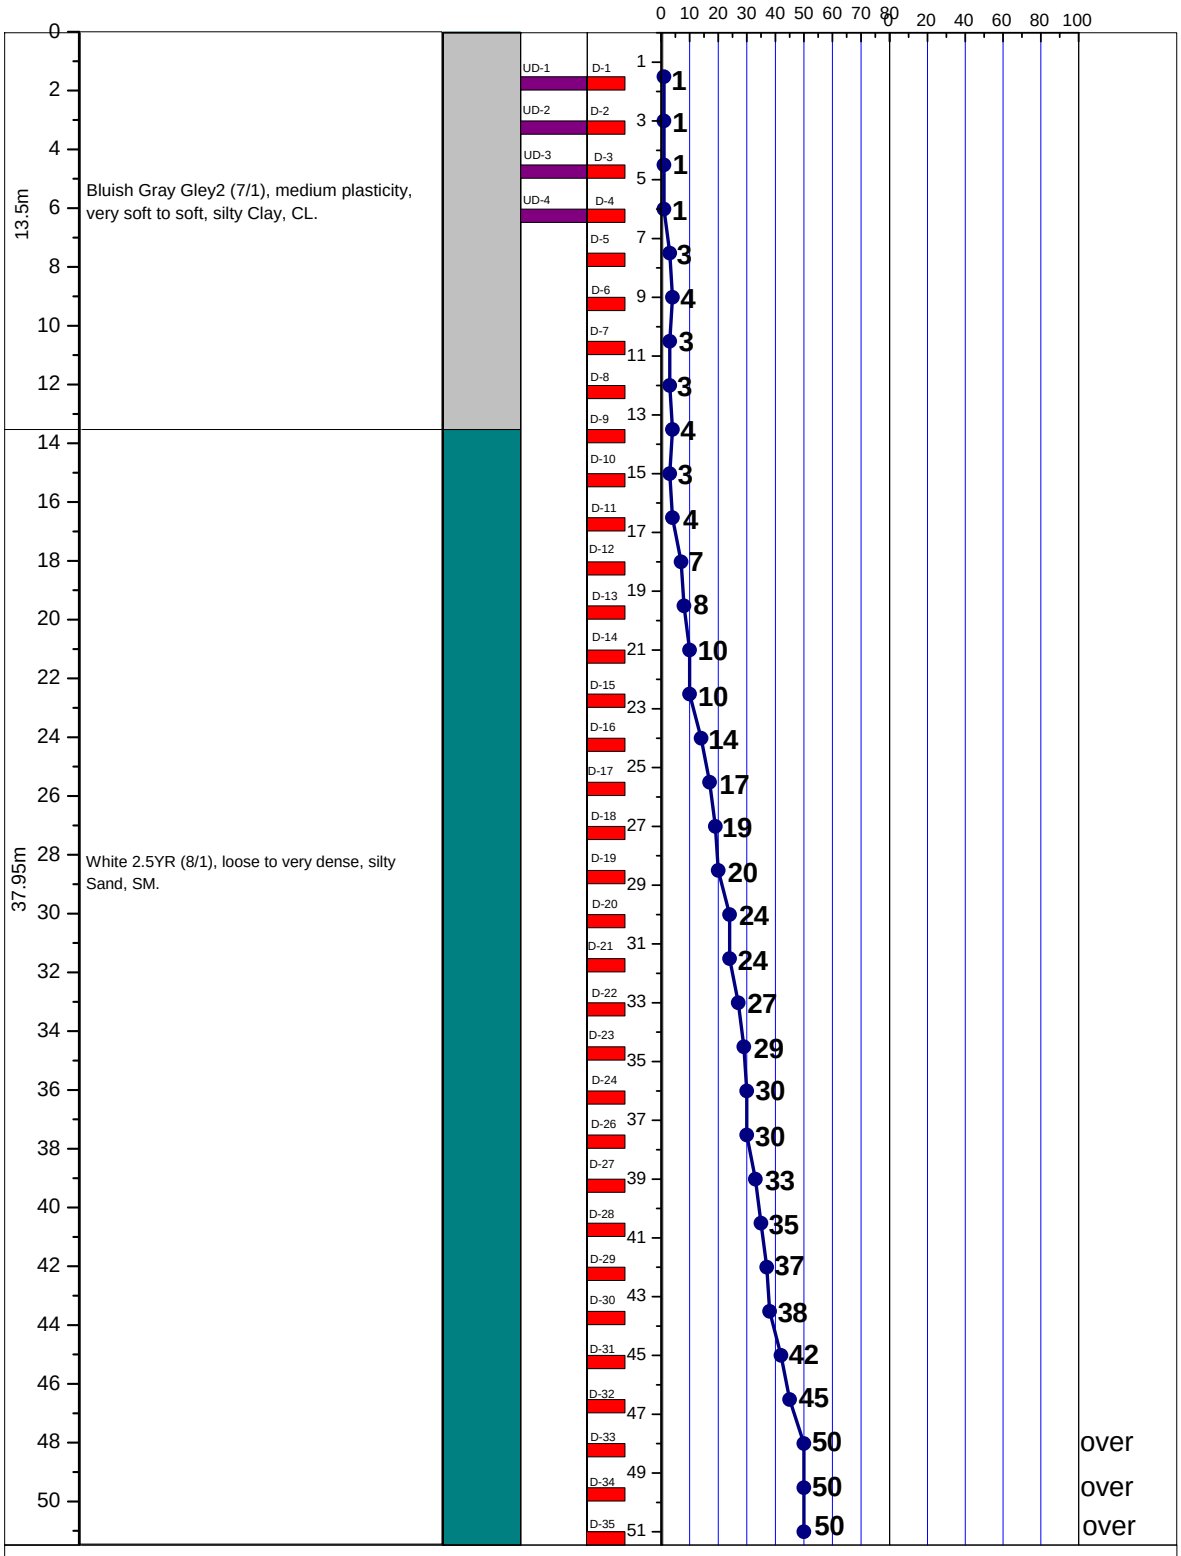


LEGEND FOR BORELOG AND GRAIN SIZE DISTRIBUTION (BASED ON 'ASTM CLASSIFICATION D-2487')

PLASTIC CLAY	SILT	PEAT/HIGHLY ORGANIC SOIL	UNDISTURBED SAMPLE
MICACEOUS FINE SAND/SILT	SAND	SHALE	DISTURBED SAMPLE

N- BLOWS DELIVERED PER FOOT BY A 140 LB HAMMER FALLING 30 INCHES

MAX^{m} PENETRATION= 50 BLOWS. AFTER 50 BLOWS PENETRATION DEPTH WERE MEASURED

A2 PROSOIL	BOREHOLE NO: BH-1	
	LOCATION : CEPZ-5, Chittagong.	
PROJECT : Telecommunication Tower.	DEPTH OF BORING : 51.0m	R. L.: 0.30m below from Road Level.
CLIENT : AXIATA (Bangladesh) Ltd.	DATE OF BORING : 21-04-2012.	G. W. T : 1.52m below from E. G. L.

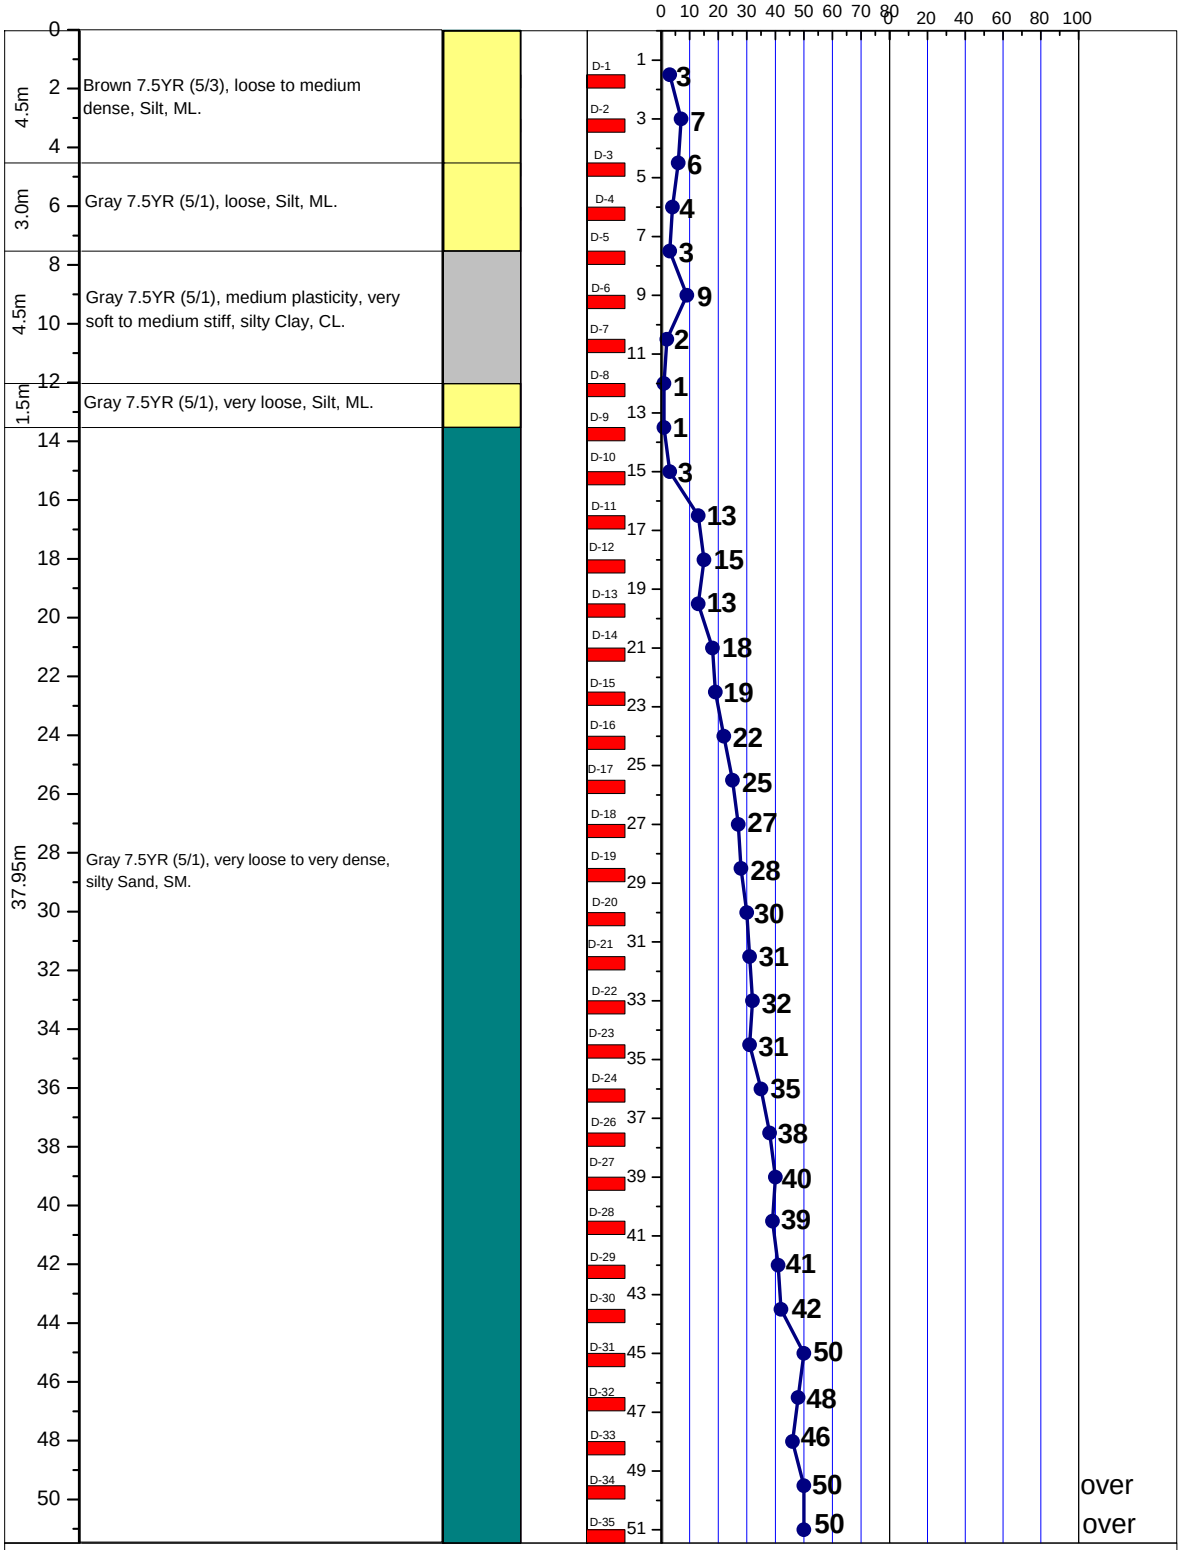


LEGEND FOR BORELOG AND GRAIN SIZE DISTRIBUTION (BASED ON 'ASTM CLASSIFICATION D-2487')

PLASTIC CLAY	SILT	PEAT/HIGHLY ORGANIC SOIL	UNDISTURBED SAMPLE
MICACEOUS FINE SAND/SILT	SAND	SHALE	DISTURBED SAMPLE

N- BLOWS DELIVERED PER FOOT BY A 140 LB HAMMER FALLING 30 INCHES

MAX^{m} PENETRATION= 50 BLOWS. AFTER 50 BLOWS PENETRATION DEPTH WERE MEASURED

A2 PROSOIL	BOREHOLE NO: BH-1	
	LOCATION : CEPZ-7, Chittagong.	
PROJECT : Telecommunication Tower.	DEPTH OF BORING : 51.0m	R. L.: On Road Level.
CLIENT : AXIATA (Bangladesh) Ltd.	DATE OF BORING : 18-07-2012.	G. W. T : 1.52m below from E. G. L.

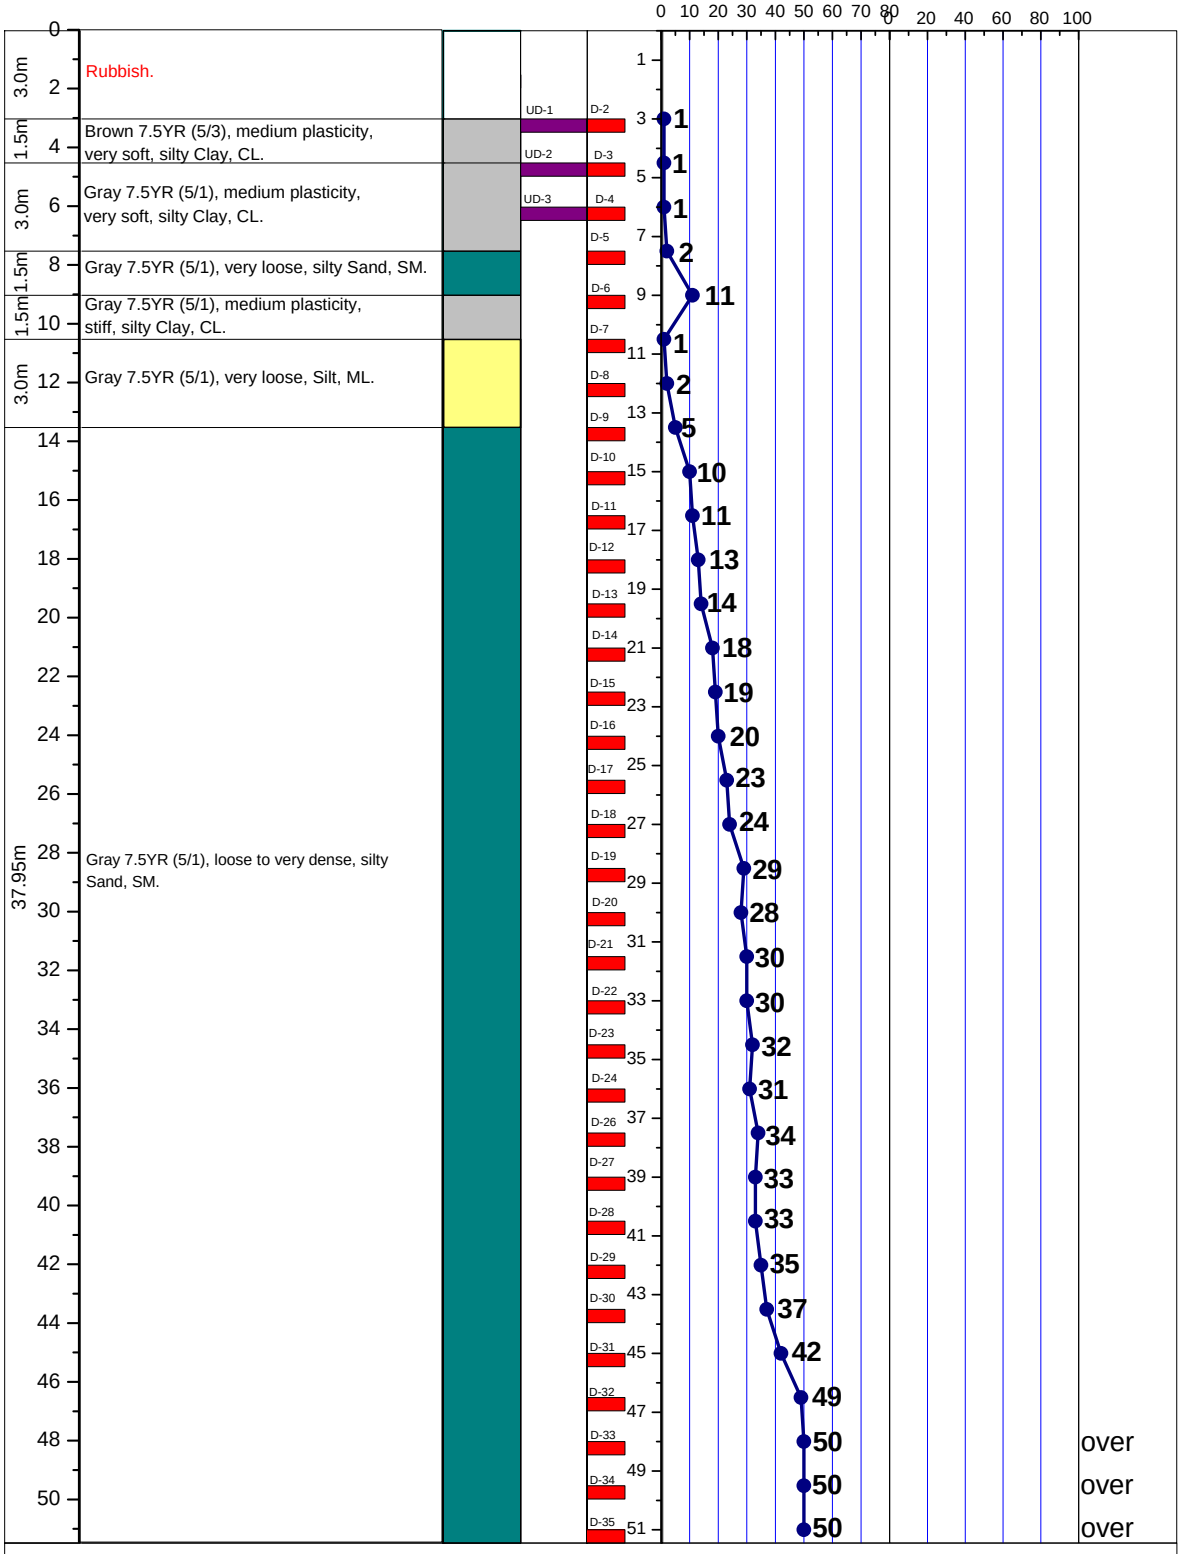


LEGEND FOR BORELOG AND GRAIN SIZE DISTRIBUTION (BASED ON 'ASTM CLASSIFICATION D-2487')

PLASTIC CLAY	SILT	PEAT/HIGHLY ORGANIC SOIL	UNDISTURBED SAMPLE
MICACEOUS FINE SAND/SILT	SAND	SHALE	DISTURBED SAMPLE

N- BLOWS DELIVERED PER FOOT BY A 140 LB HAMMER FALLING 30 INCHES

MAX^{m} PENETRATION= 50 BLOWS. AFTER 50 BLOWS PENETRATION DEPTH WERE MEASURED

A2 PROSOIL	BOREHOLE NO: BH-1	
	LOCATION : Rangunia, Chittagong.	
PROJECT : Telecommunication Tower.	DEPTH OF BORING : 51.0m	R. L.: 1.37m below from Road Level.
CLIENT : Grameenphone Ltd.	DATE OF BORING : 20-04-2007.	G. W. T : Rain Water.

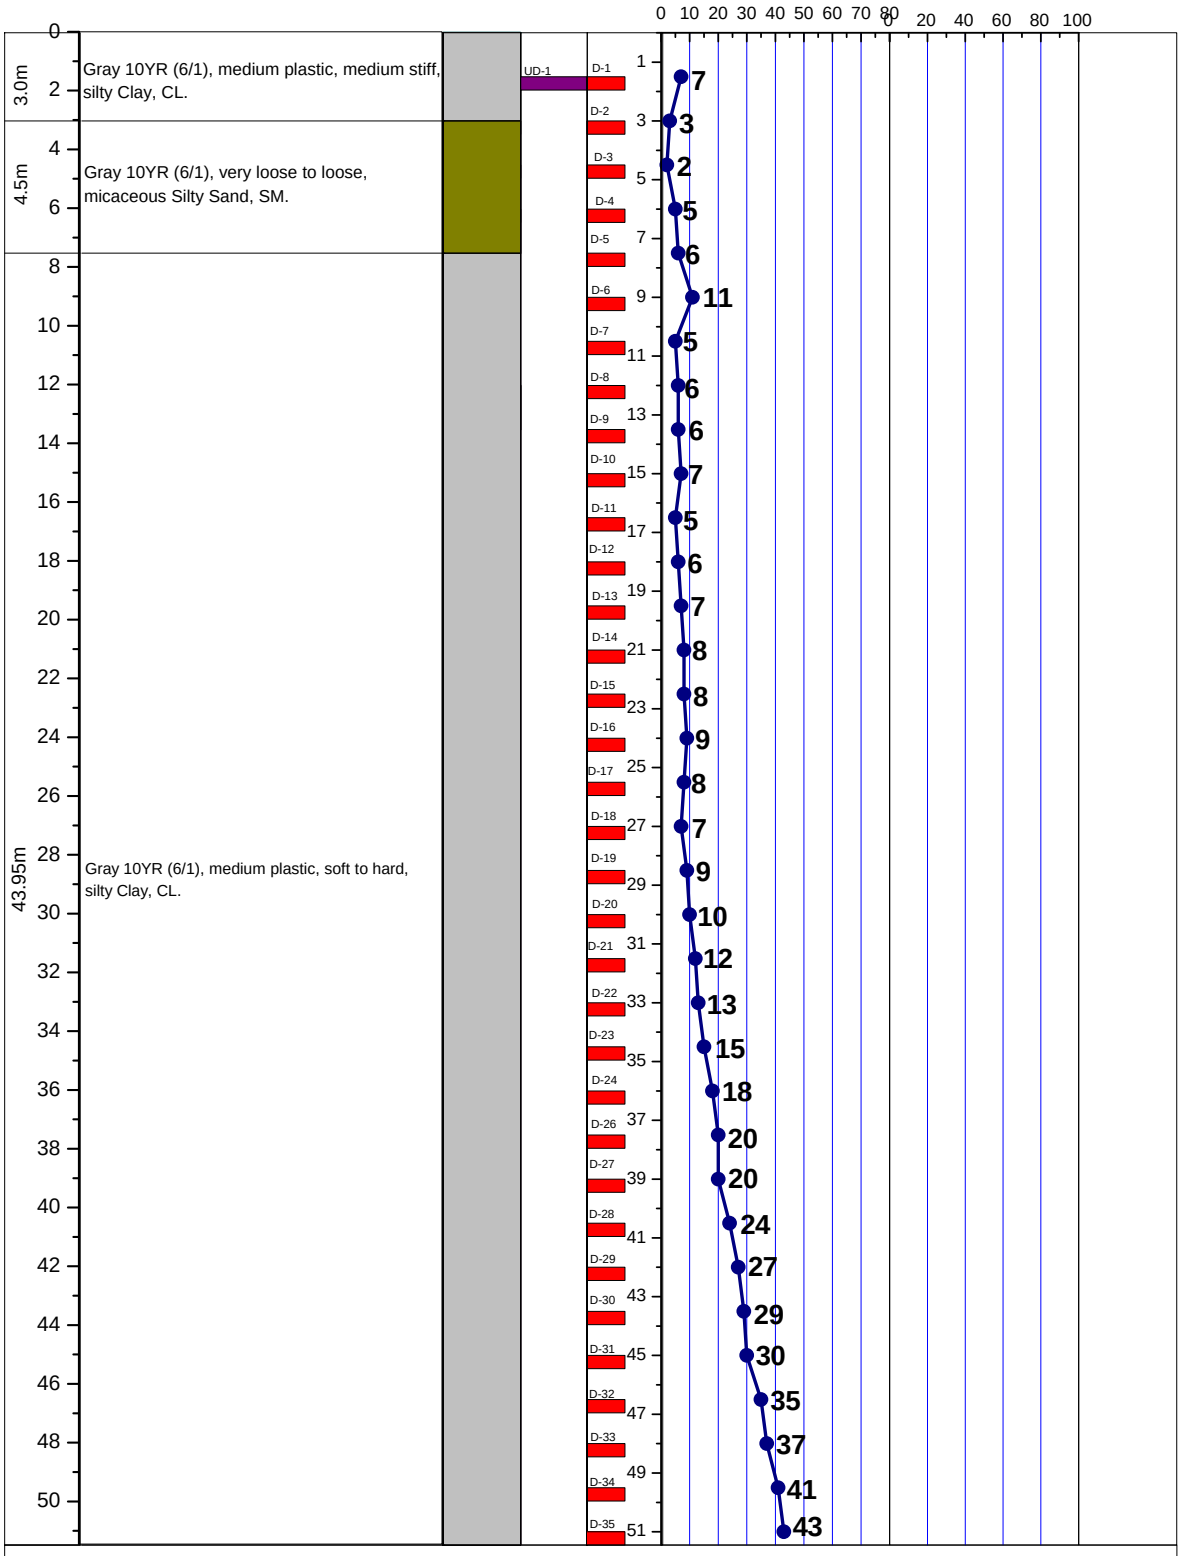


LEGEND FOR BORELOG AND GRAIN SIZE DISTRIBUTION (BASED ON 'ASTM CLASSIFICATION D-2487')

PLASTIC CLAY	SILT	PEAT/HIGHLY ORGANIC SOIL	UNDISTURBED SAMPLE
MICACEOUS FINE SAND/SILT	SAND	SHALE	DISTURBED SAMPLE

N- BLOWS DELIVERED PER FOOT BY A 140 LB HAMMER FALLING 30 INCHES

MAX^{m} PENETRATION= 50 BLOWS. AFTER 50 BLOWS PENETRATION DEPTH WERE MEASURED

A2 PROSOIL	BOREHOLE NO: BH-1	
	LOCATION : Barobkundo, Sitakundo, Chittagong.	
PROJECT : Telecommunication Tower.	DEPTH OF BORING : 51.0m	R. L.: 1.37m below from Road Level.
CLIENT : Grameenphone Ltd.	DATE OF BORING : 07-05-2007.	G. W. T : 0.15m above from E. G. L.

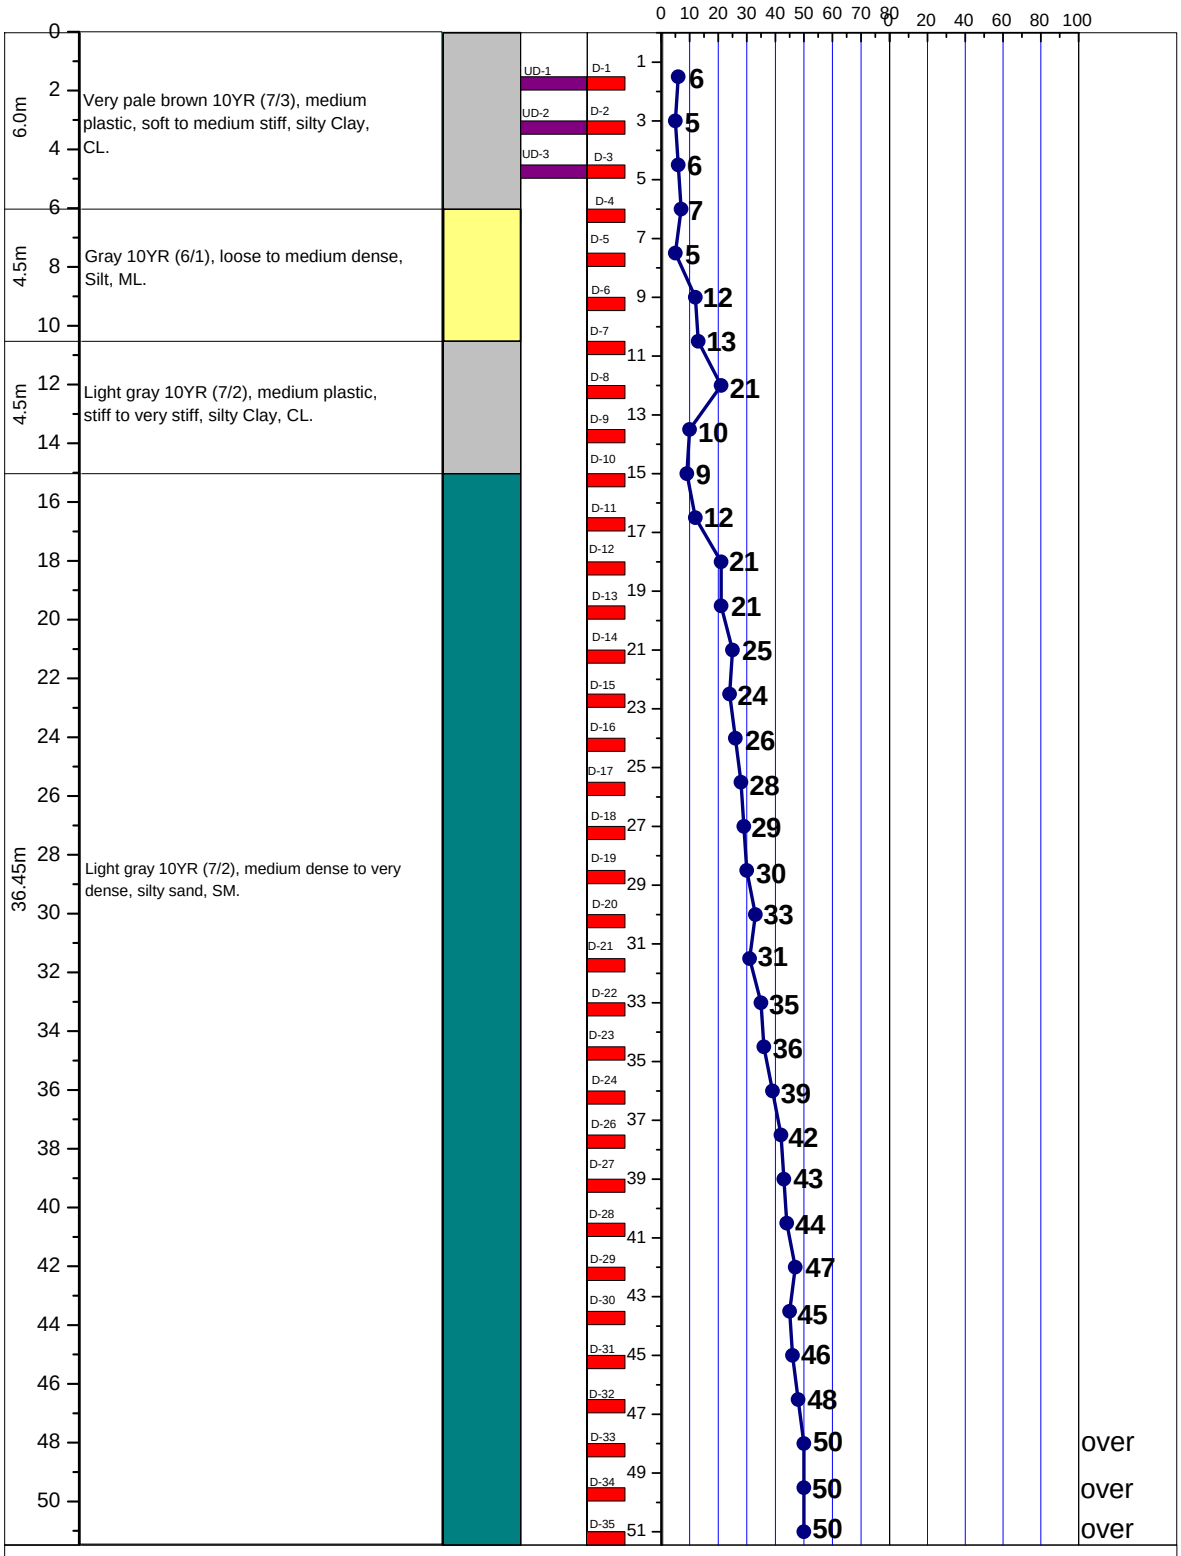

LEGEND FOR BORELOG AND GRAIN SIZE DISTRIBUTION (BASED ON 'ASTM CLASSIFICATION D-2487')

PLASTIC CLAY	SILT	PEAT/HIGHLY ORGANIC SOIL	UNDISTURBED SAMPLE
MICACEOUS FINE SAND/SILT	SAND	SHALE	DISTURBED SAMPLE

N- BLOWS DELIVERED PER FOOT BY A 140 LB HAMMER FALLING 30 INCHES

MAX^{m} PENETRATION= 50 BLOWS. AFTER 50 BLOWS PENETRATION DEPTH WERE MEASURED