A2	PROSOIL	BOREHOLE NO: BH-1	
		LOCATION : Shahnagar Islamia Bazar, Fatikchari, Chittagong.	
PROJECT : Telecommunication Tower.		DEPTH OF BORING : 18.0m	R. L.: 1.83m below from Road Level.
CLIENT : Warid Telecom International Ltd.		DATE OF BORING: 27-10-2011.	G. W. T : 0.15m above from E.G.L.

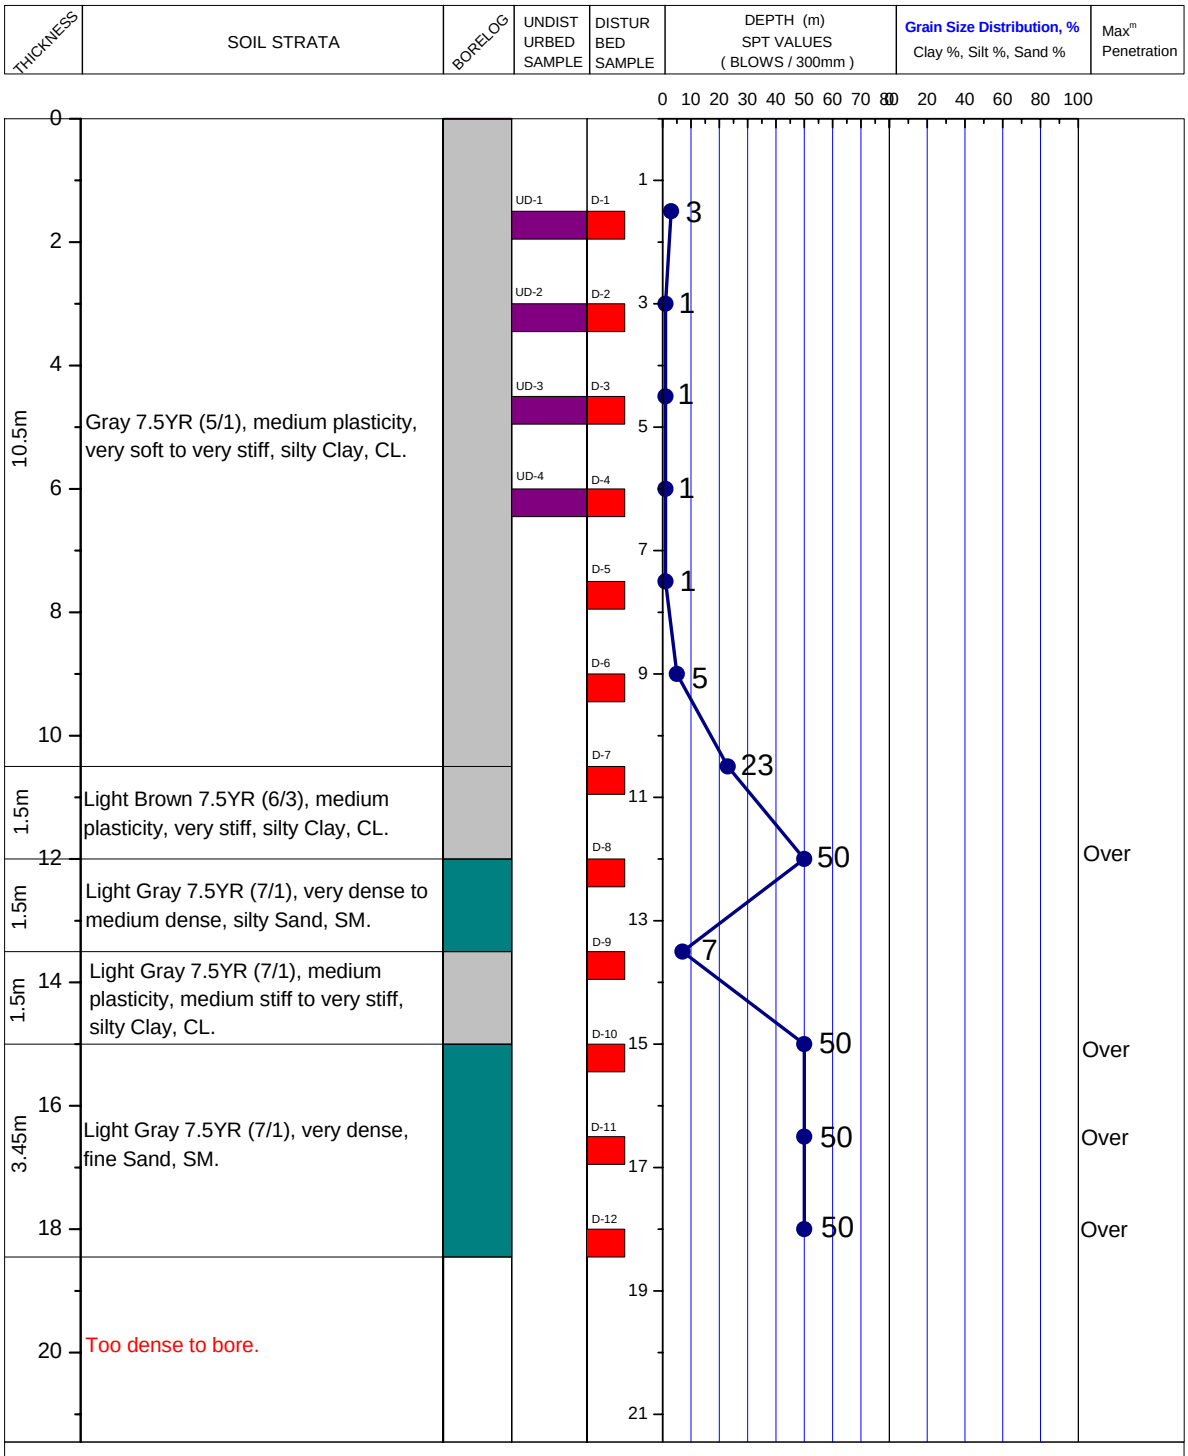

LEGEND FOR BORELOG AND GRAIN SIZE DISTRIBUTION (BASED ON 'ASTM CLASSIFICATION D-2487')

PLASTIC CLAY	SAND	SHALE	UNDISTURBED SAMPLE
MICACEOUS FINE SAND/SILT	SILT	PEAT/HIGHLY ORGANIC SOIL	DISTURBED SAMPLE

N- BLOWS DELIVERED PER FOOT BY A 140 LB HAMMER FALLING 30 INCHES

MAX^{m} PENETRATION= 50 BLOWS

AFTER 50 BLOWS PENETRATION DEPTH WERE MEASURED