A2	PROSOIL	BOREHOLE NO: BH-1	
		LOCATION : Town Border Station (TBS), Hakimpur Mouza, Jessore.	
PROJECT : DESIGN, BUILD AND TURNKEY SUPPLY, INSTALLATION, CONSTRUCTION, TESTING AND COMMISSIONING.		DEPTH OF BORING : 21.0m	R. L.: 0.61m below from Road Level.
CLIENT : GAS TRANSMISSION COMPANY LIMITED (GTCL).		DATE OF BORING: 04-07-2013.	G. W. T : 1.52m below from E.G.L.

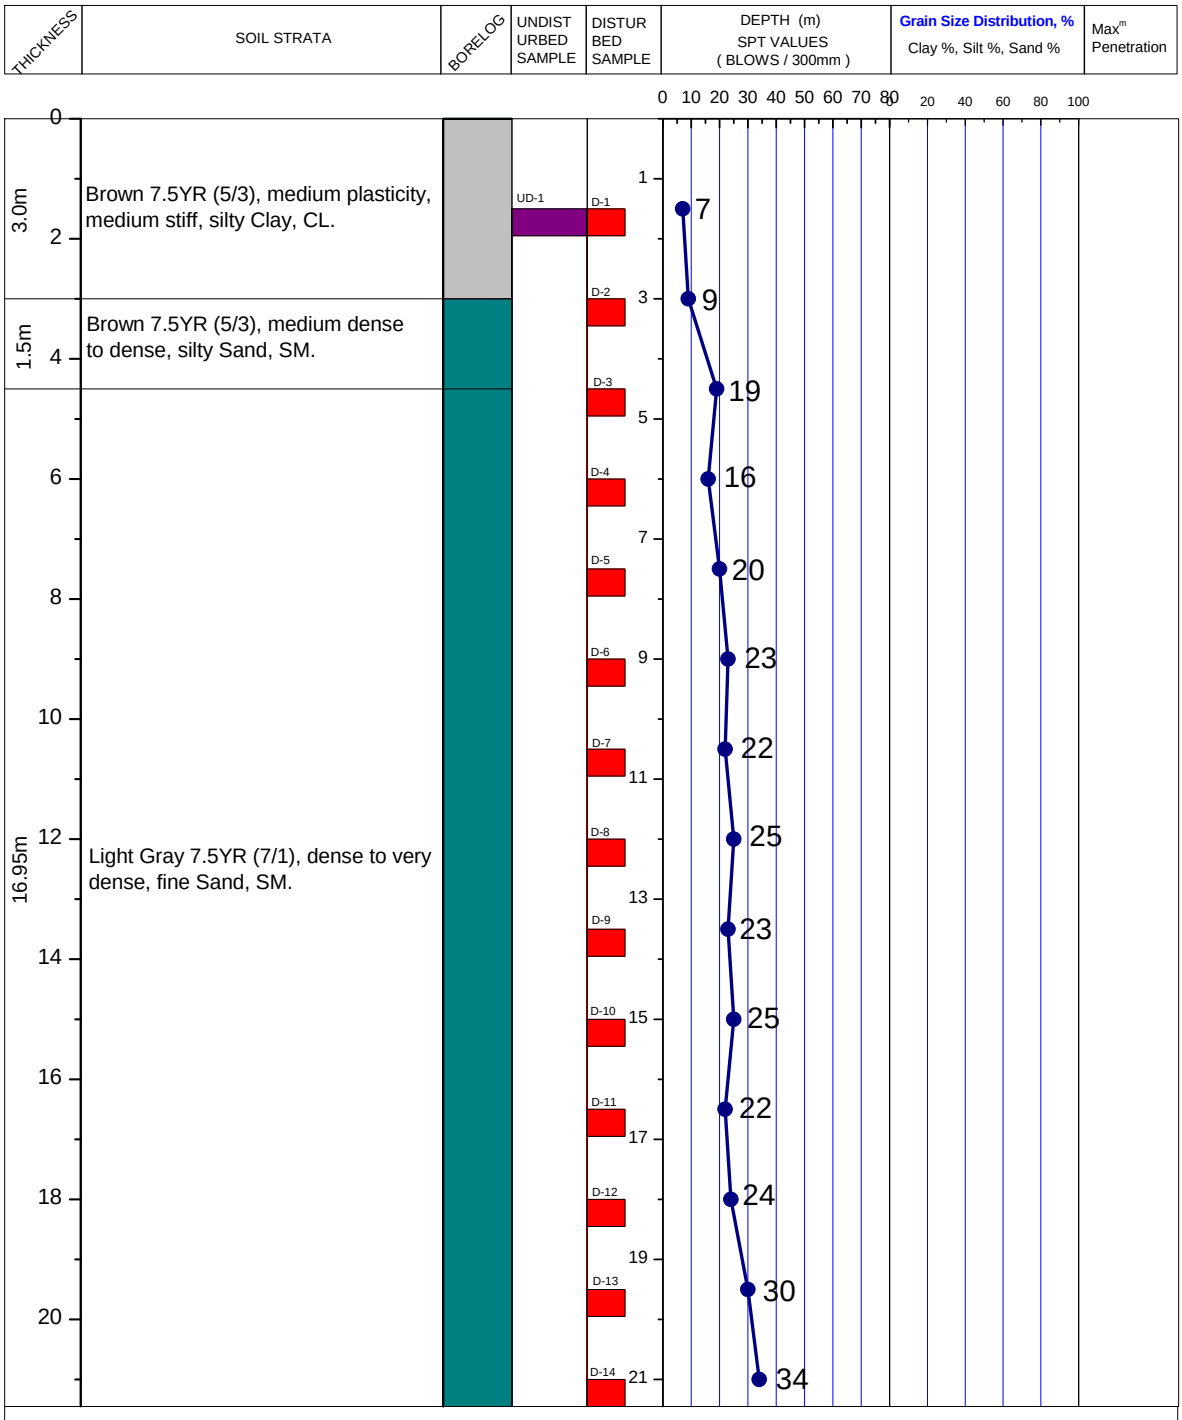

LEGEND FOR BORELOG AND GRAIN SIZE DISTRIBUTION (BASED ON 'ASTM CLASSIFICATION D-2487')

PLASTIC CLAY | SAND | SHALE | UNDISTURBED SAMPLE

MICACEOUS FINE SAND/SILT | SILT | PEAT/HIGHLY ORGANIC SOIL | DISTURBED SAMPLE

N- BLOWS DELIVERED PER FOOT BY A 140 LB HAMMER FALLING 30 INCHES
MAX^{m} PENETRATION= 50 BLOWS
AFTER 50 BLOWS PENETRATION DEPTH WERE MEASURED