A2 PROSOIL	BOREHOLE NO: BH-1	
	LOCATION : Mohonpur Bazar, Comilla.	
PROJECT : Telecommunication Tower.	DEPTH OF BORING : 21.0m	R. L.: 0.20m below from Road Level.
CLIENT : Sheba Telecom (PVT.) Ltd.	DATE OF BORING : 12-04-2008.	G. W. T : 1.52m below from E. G. L.

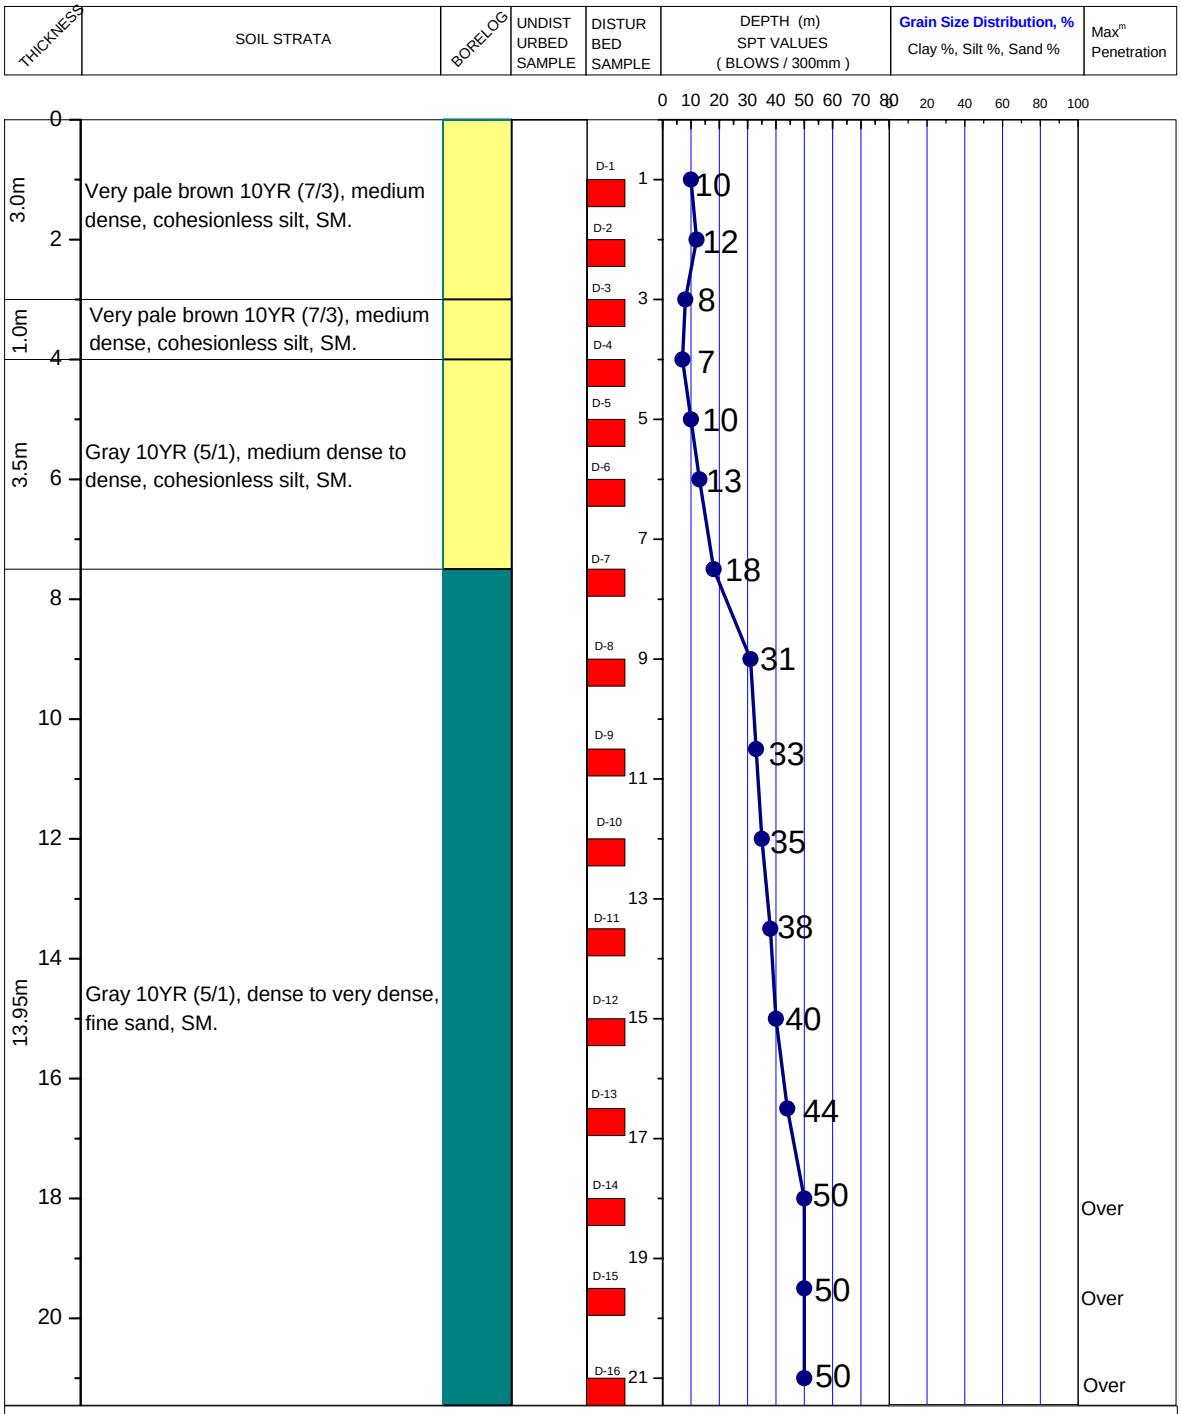

LEGEND FOR BORELOG AND GRAIN SIZE DISTRIBUTION

PLASTIC SILTY CLAY | LOW PLASTIC CLAYEY SILT | NON PLASTIC SILT | SAND

ORGANIC | UNDISTURBED SAMPLE / DISTURBED SAMPLE | SHALE

N- BLOWS DELIVERED PER FOOT BY A 140 LB HAMMER FALLING 30 INCHES

MAX^{m} PENETRATION= 50 BLOWS

AFTER 50 BLOWS PENETRATION DEPTH WERE MEASURED