A2	PROSOIL	BOREHOLE NO: BH-1	
		LOCATION : House no: E-40, 41, 42; Arambagh, Rupnagar, Mirpur, Dhaka.	
PROJECT : Proposed Rangs Sanchoita.		DEPTH OF BORING : 24.0m	R. L.: 0.15 below from Road Level.
CLIENT : Rangs Properties Ltd.		DATE OF BORING : 11-12-2009.	G. W. T : 0.90m below from E. G. L.

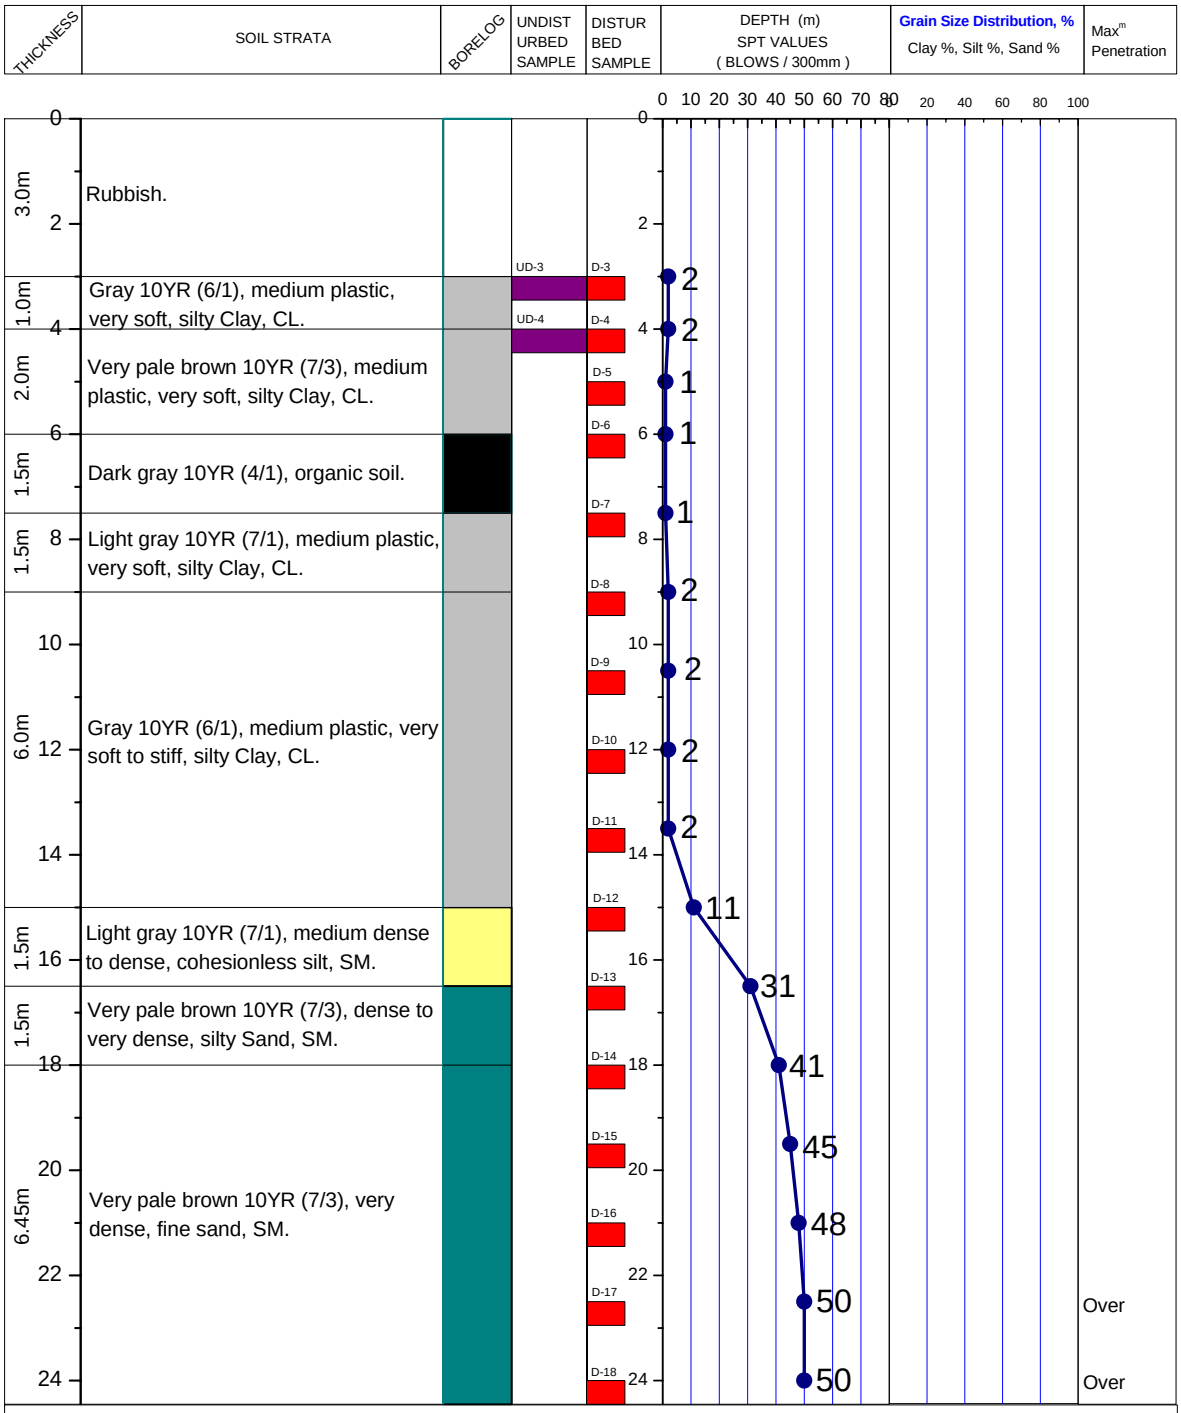

LEGEND FOR BORELOG AND GRAIN SIZE DISTRIBUTION

PLASTIC SILTY CLAY

LOW PLASTIC CLAYEY SILT

NON PLASTIC SILT

SAND

ORGANIC

UNDISTURBED SAMPLE

DISTURBED SAMPLE

SHALE

N- BLOWS DELIVERED PER FOOT BY A 140 LB HAMMER FALLING 30 INCHES

MAX^{m} PENETRATION= 50 BLOWS

AFTER 50 BLOWS PENETRATION DEPTH WERE MEASURED