A2	PROSOIL	BOREHOLE NO: BH-1	
		LOCATION : Chinage 21+290km Of Rikabibazar-Rampal-Digirpar -Banglabazar-Munshigonj Sadar Road, Munshigonj.	
PROJECT : Proposed Banglabazar Bridge.		DEPTH OF BORING : 36.0m	Chainage: 21+297 R. L. : 2.93
CLIENT : Road Division, Munshigonj.		DATE OF BORING : 01-12-2011 to 02-12-2011.	G. W. T : 2.44m below from E.G.L.

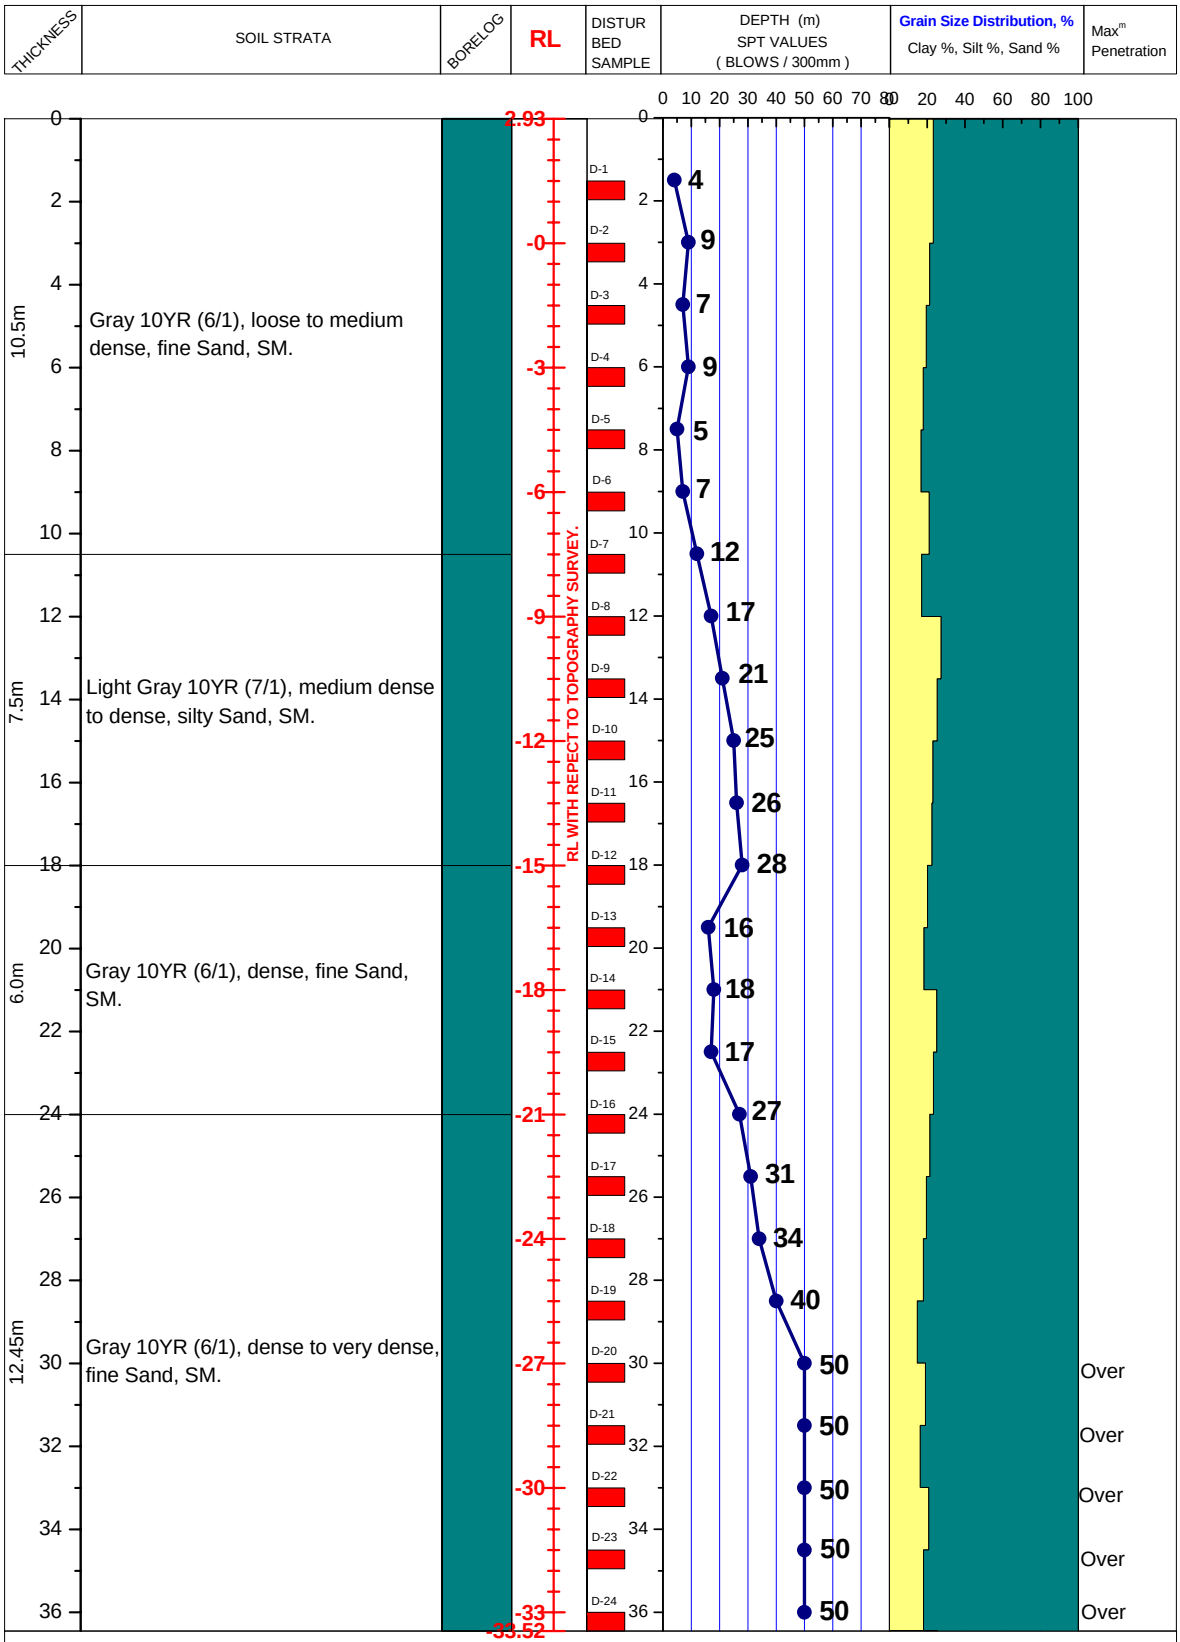

LEGEND FOR BORELOG AND GRAIN SIZE DISTRIBUTION (BASED ON 'ASTM CLASSIFICATION D-2487')

PLASTIC CLAY	SILT	PEAT/HIGHLY ORGANIC SOIL	UNDISTURBED SAMPLE
MICACEOUS FINE SAND/SILT	SAND	SHALE	DISTURBED SAMPLE

N- BLOWS DELIVERED PER FOOT BY A 140 LB HAMMER FALLING 30 INCHES

MAX^{m} PENETRATION= 50 BLOWS. AFTER 50 BLOWS PENETRATION DEPTH WERE MEASURED