A2 PROSOIL	BOREHOLE NO: BH-1	
	LOCATION : Borguna sadar, Borguna.	
PROJECT : Telecommunication Tower.	DEPTH OF BORING : 21.45m	R. L.: 0.61m below from Road Level.
CLIENT : BANGLADESH TELEGRAPH & TELEPHONE BOARD.	DATE OF BORING : 27-03-2008.	G. W. T : 0.91m below from E. G. L.

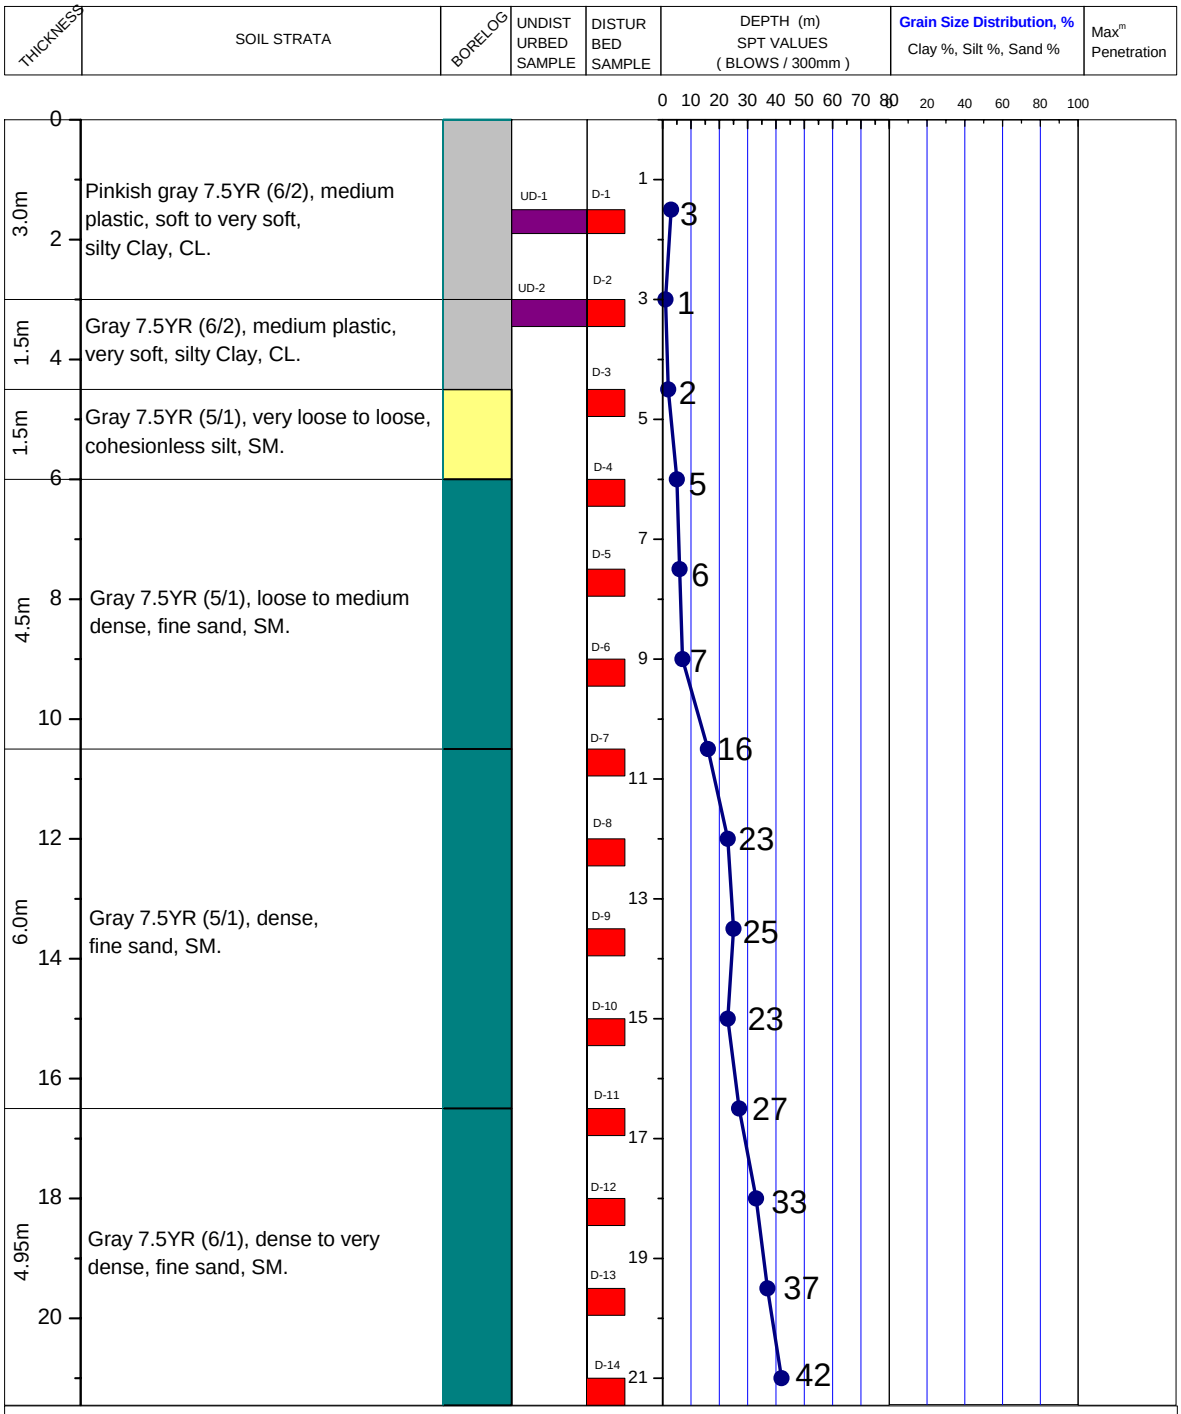

LEGEND FOR BORELOG AND GRAIN SIZE DISTRIBUTION

PLASTIC SILTY CLAY

LOW PLASTIC CLAYEY SILT

NON PLASTIC SILT

SAND

ORGANIC

UNDISTURBED SAMPLE

DISTURBED SAMPLE

SHALE

N- BLOWS DELIVERED PER FOOT BY A 140 LB HAMMER FALLING 30 INCHES

MAX^{m} PENETRATION= 50 BLOWS

AFTER 50 BLOWS PENETRATION DEPTH WERE MEASURED