
A2	PROSOIL	Borehole No: BH-01	
		Location: Alipur Noakhali Khal Chowmuhani.	
Name of Project: Chowmuhani Railway Overpass at Feni-Noakhali National Highway (N-104) under Noakhali Road Division.		Borehole Depth: 45.0m	R. L. : On Road Level
CLIENT: ROADS & HIGHWAYS DEPARTMENT.		Date of Boring: 03-08-2021 to 05-08-2021	B. W. T : 3.9m below from E. G. L.

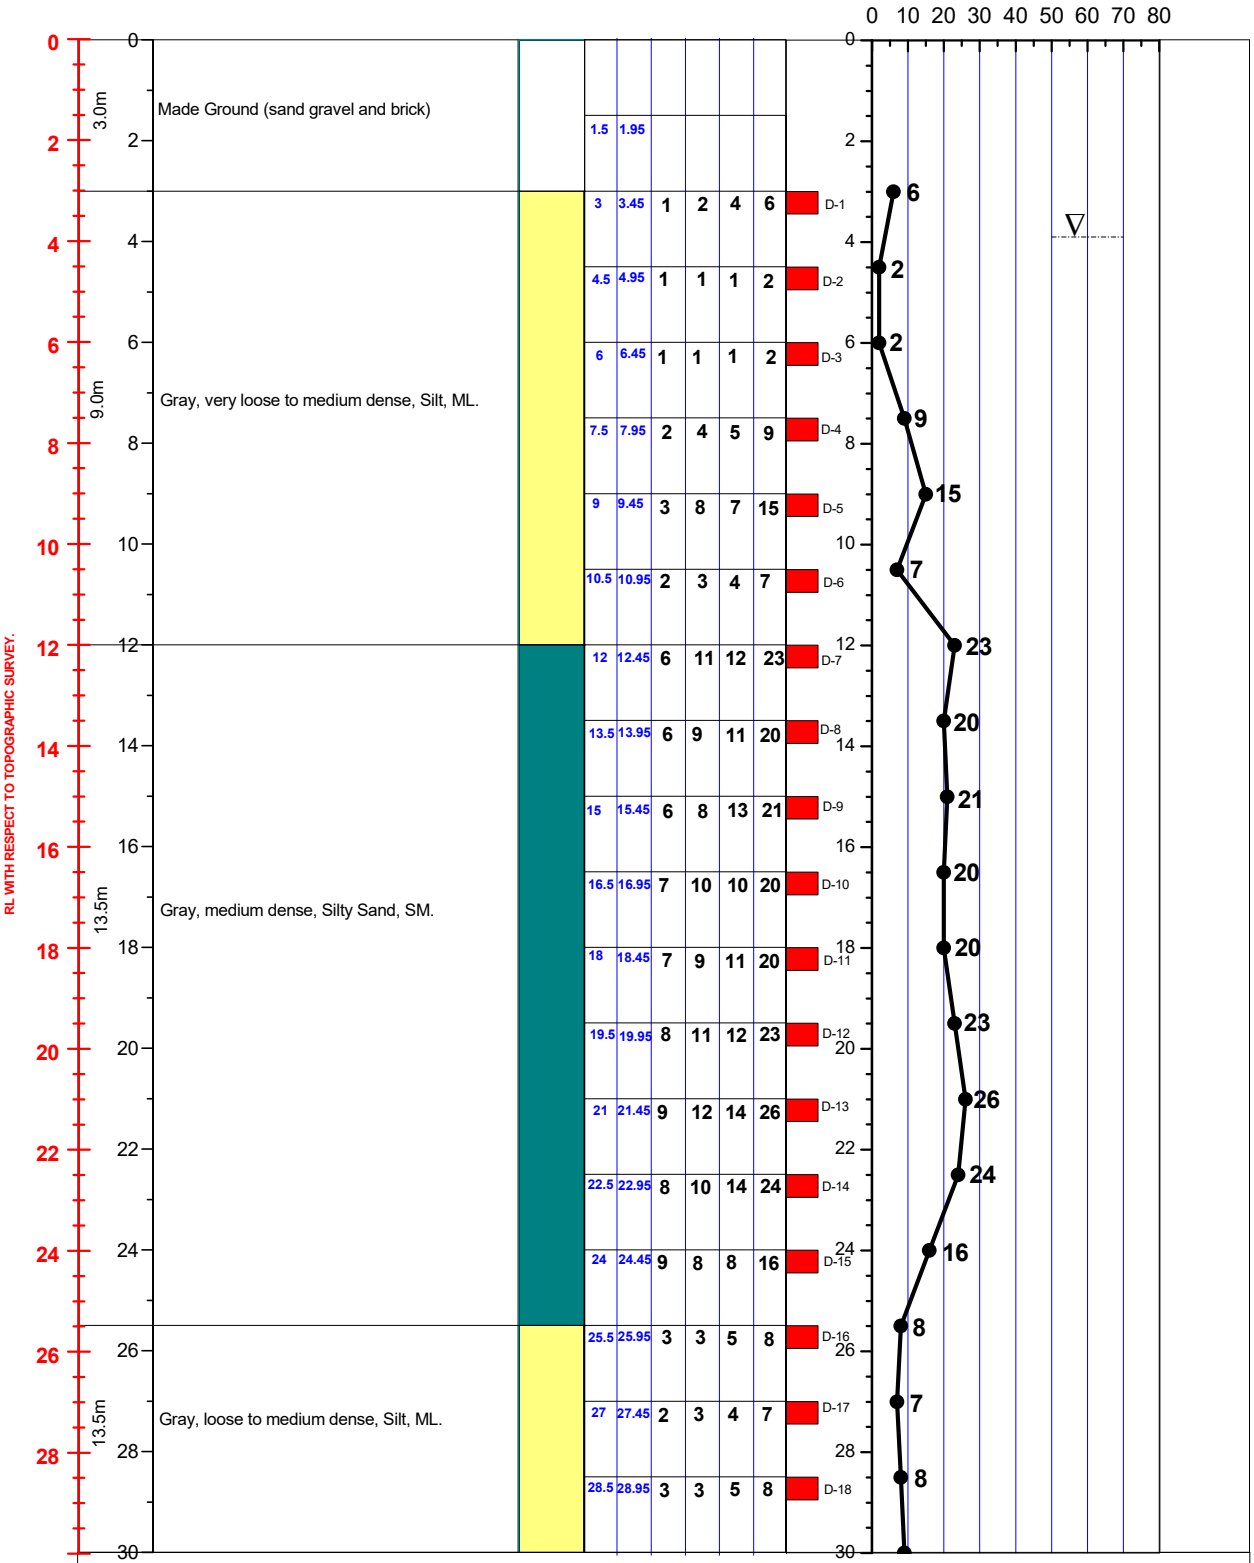


LEGEND FOR BORELOG AND GRAIN SIZE DISTRIBUTION (BASED ON 'ASTM CLASSIFICATION D-2487')

PLASTIC CLAY	SILT	PEAT/HIGHLY ORGANIC SOIL	UNDISTURBED SAMPLE
MICACEOUS FINE SAND/SILT	SAND	SHALE	DISTURBED SAMPLE

N- BLOWS DELIVERED PER FOOT BY A 140 LB HAMMER FALLING 30 INCHES

MAX^{m} PENETRATION= 50 BLOWS. AFTER 50 BLOWS PENETRATION DEPTH WERE MEASURED

A2	PROSOIL	Borehole No: BH-01	
		Location: Alipur Noakhali Khal Chowmuhani.	
Name of Project: Chowmuhani Railway Overpass at Feni-Noakhali National Highway (N-104) under Noakhali Road Division.		Borehole Depth: 45.0m	R. L. : On Road Level
CLIENT : ROADS & HIGHWAYS DEPARTMENT.		Date of Boring: 03-08-2021 to 05-08-2021	B. W. T : 3.9m below from E. G. L.

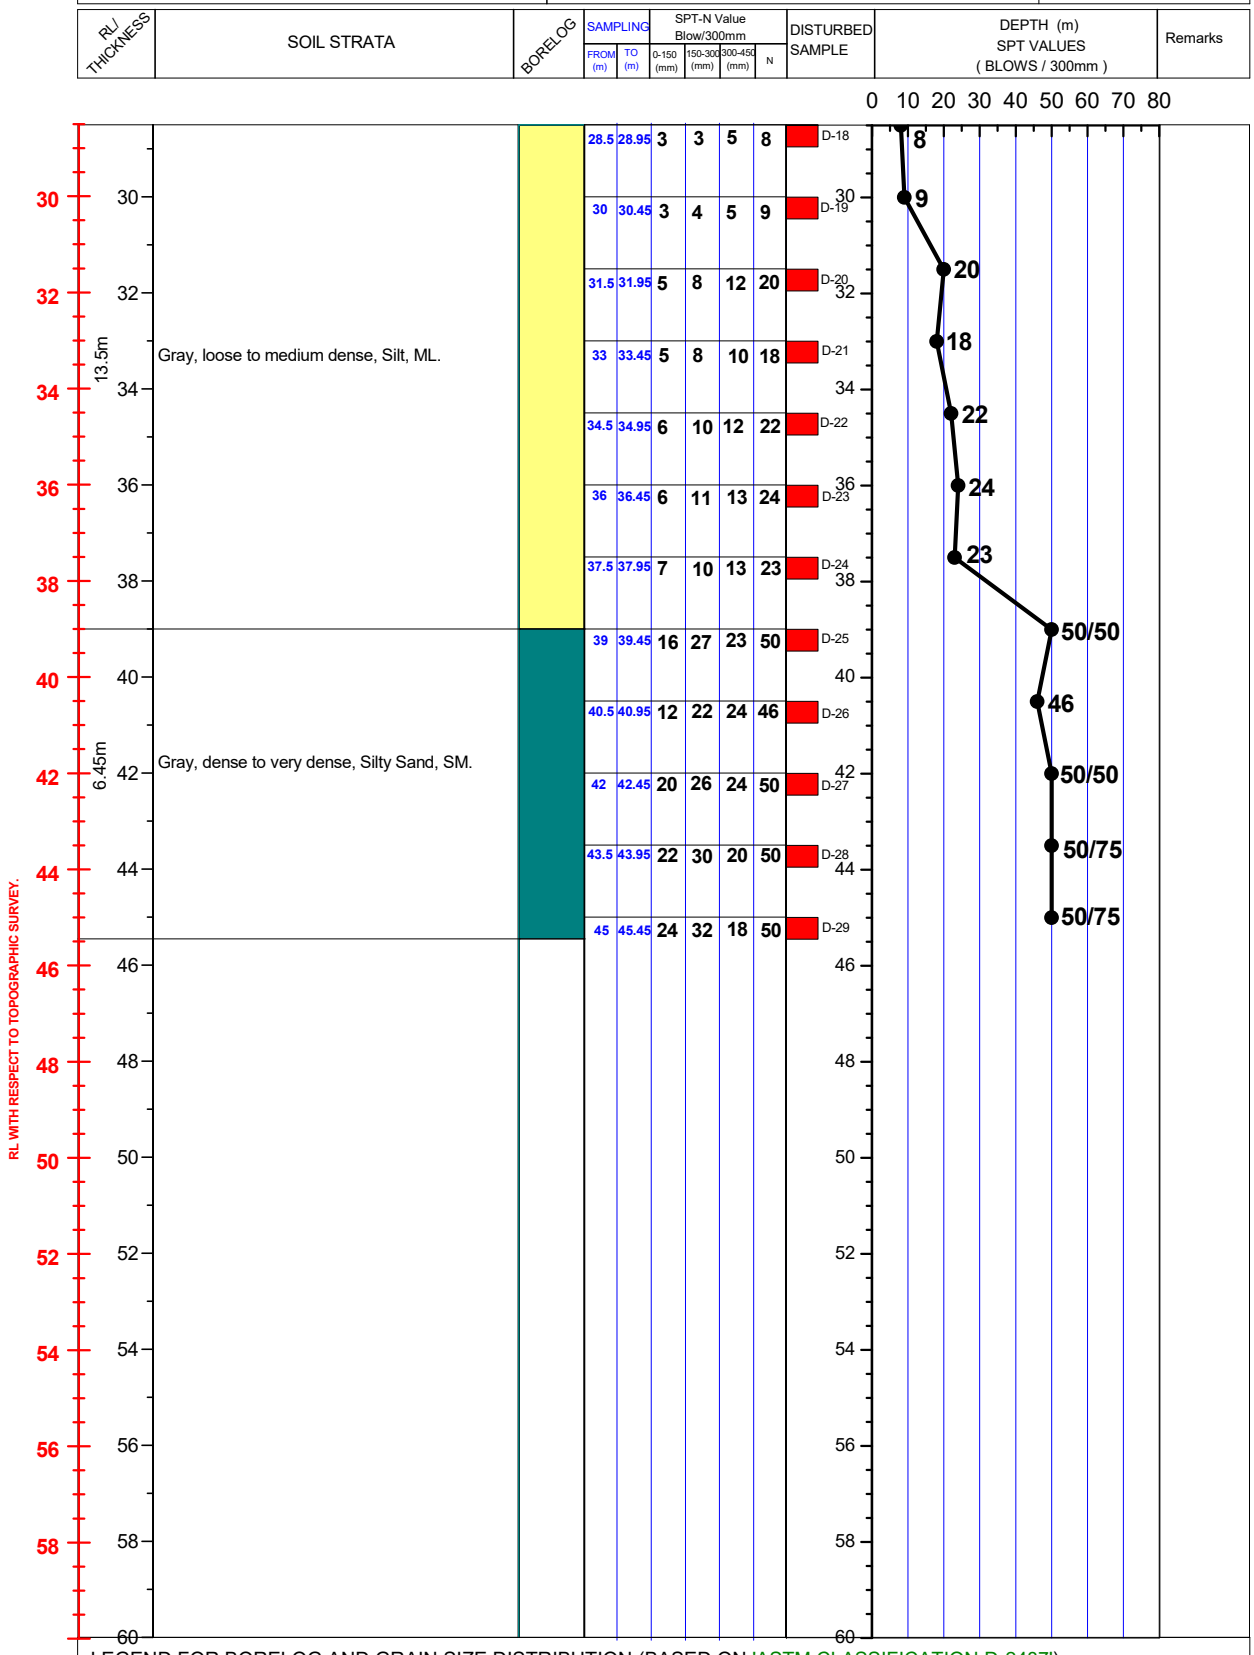

LEGEND FOR BORELOG AND GRAIN SIZE DISTRIBUTION (BASED ON 'ASTM CLASSIFICATION D-2487')

PLASTIC CLAY	SILT	PEAT/HIGHLY ORGANIC SOIL	UNDISTURBED SAMPLE
MICACEOUS FINE SAND/SILT	SAND	SHALE	DISTURBED SAMPLE

N- BLOWS DELIVERED PER FOOT BY A 140 LB HAMMER FALLING 30 INCHES

MAX^{m} PENETRATION= 50 BLOWS. AFTER 50 BLOWS PENETRATION DEPTH WERE MEASURED